
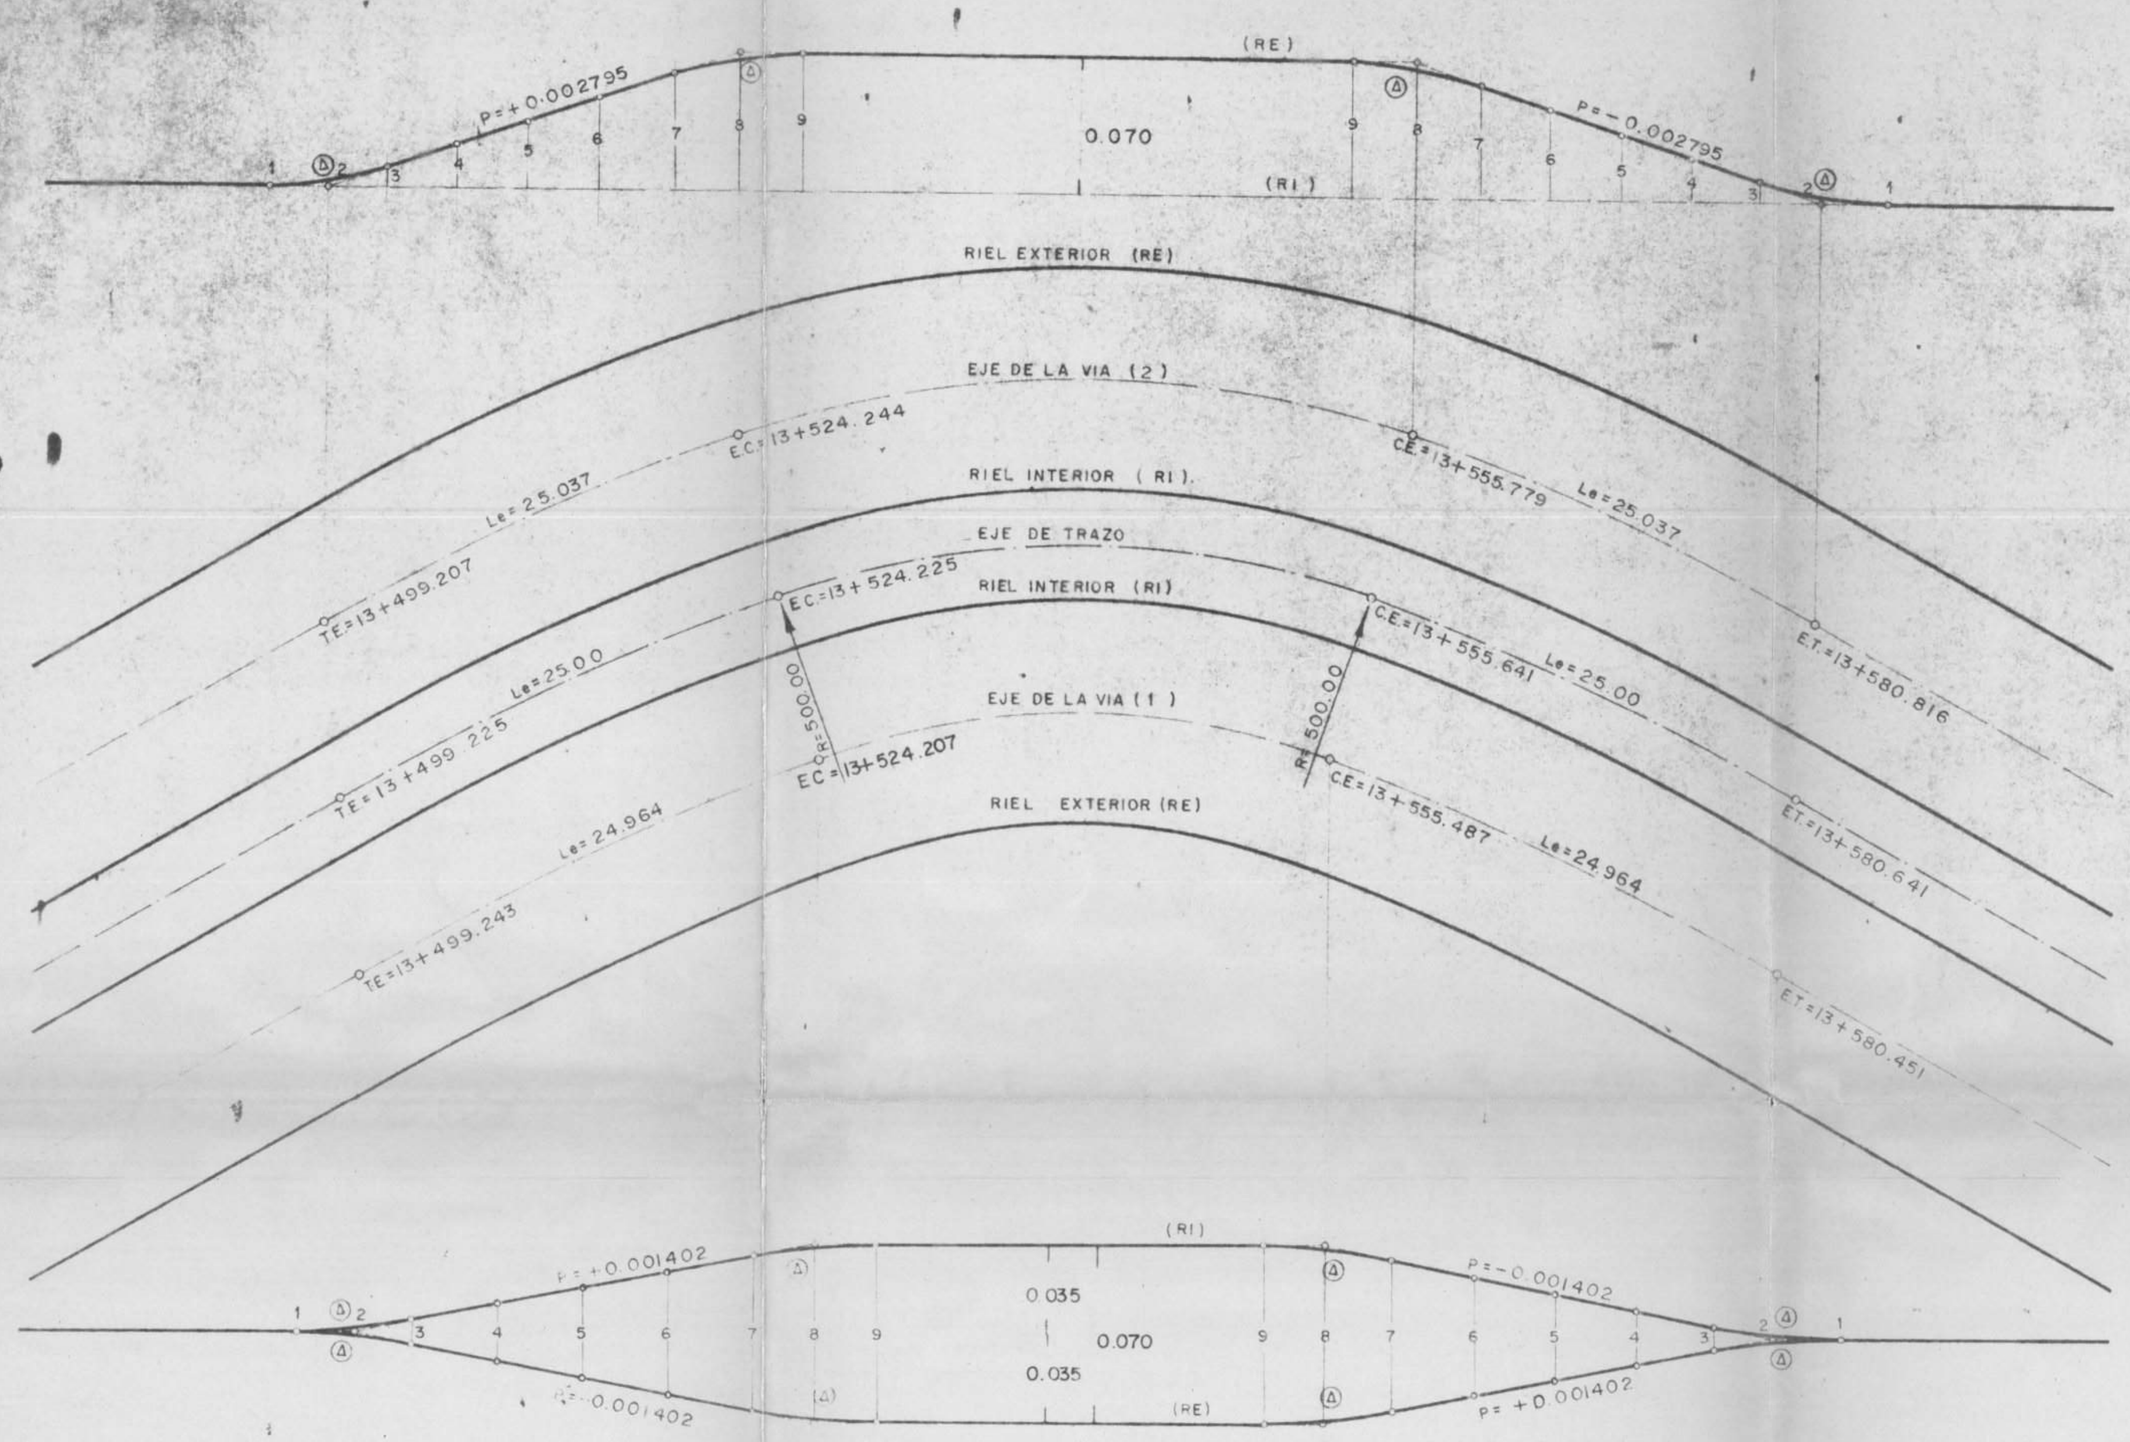


(A) TRANSICION VERTICAL

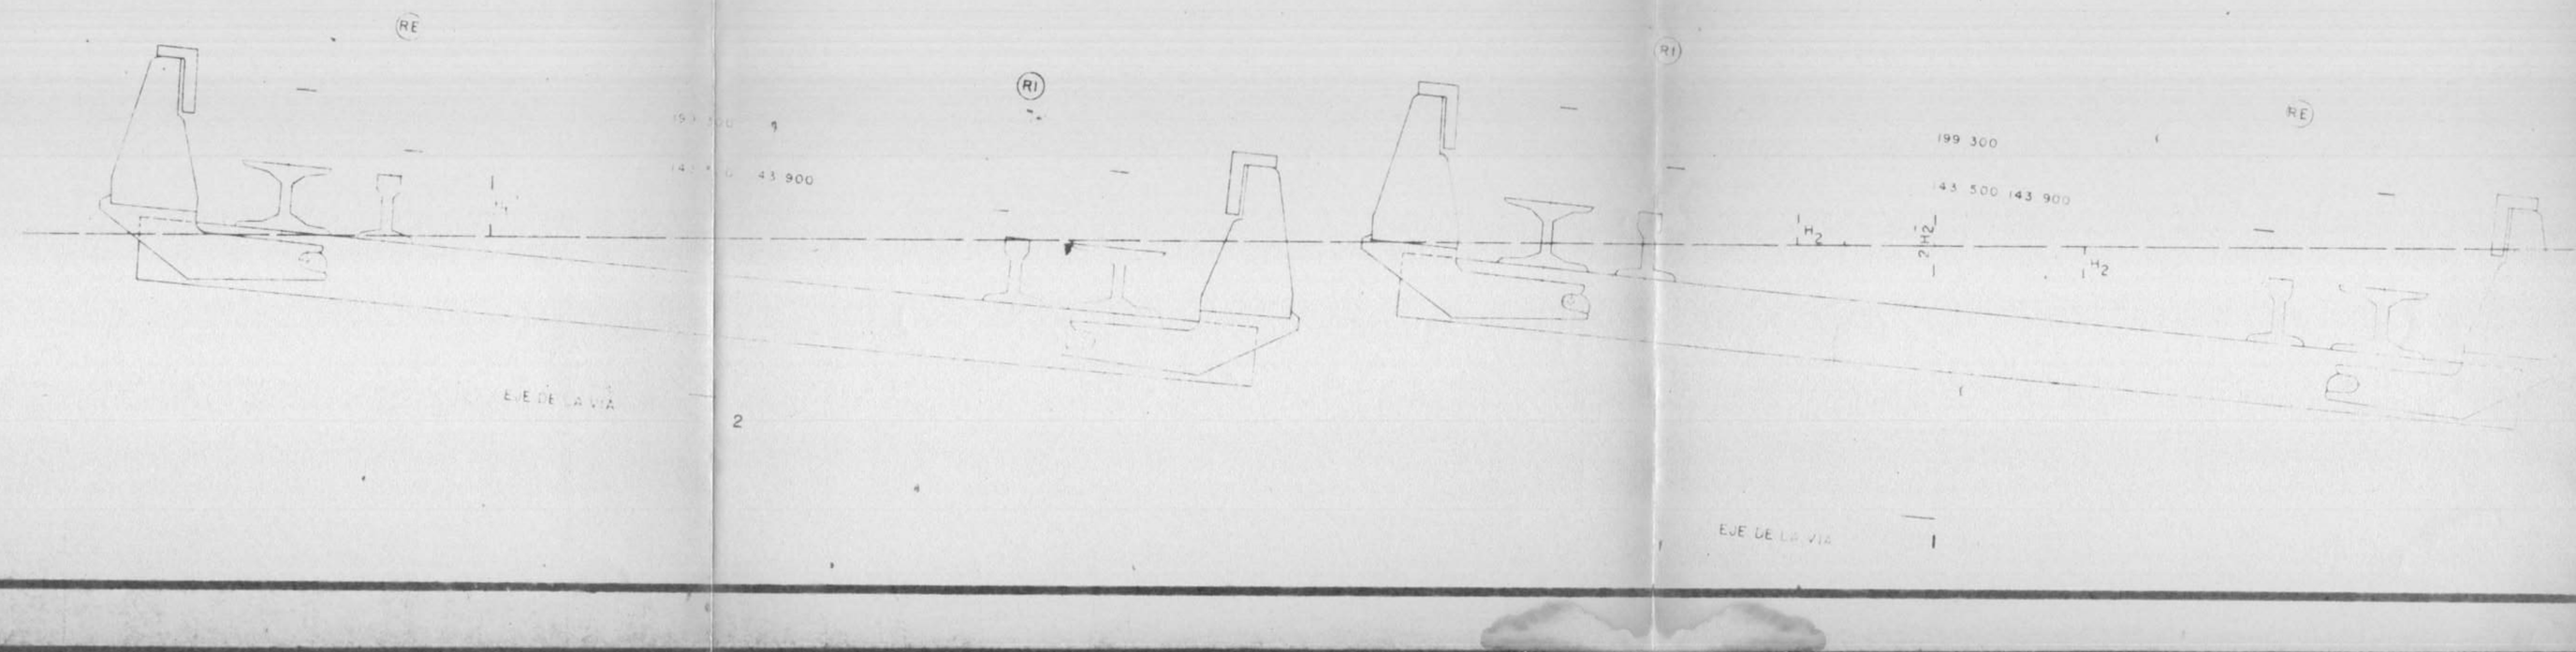

NUM. DE SECCION	DISTANCIA	SOBRE-ELEVACION TOTAL	R E VIA (2)	R I VIA (2)	CADENAMIENTOS		ENTRE-VIA
1		0.000	0.000	0.000	13+495.713	13+584.310	
	3.494						
2 TE ET		0.002	0.002	0.000	13+499.207	13+580.816	
	3.494						
3		0.010	0.010	0.000	13+502.701	13+577.321	
	4.512						
4		0.022	0.022	0.000	13+507.213	13+572.809	
	4.512						
5		0.035	0.035	0.000	13+511.725	13+568.297	2.900
	4.512						
6		0.048	0.048	0.000	13+516.237	13+567.785	
	4.512						
7		0.060	0.060	0.000	13+520.749	13+559.273	
	3.494						
8		0.068	0.068	0.000	13+524.244	13+555.779	
	3.494						
9 EC CE		0.070	0.070	0.000	13+527.738	13+552.285	

NUM. DE SECCION	DISTANCIA	SOBRE-ELEVACION TOTAL	R E VIA (1)	R I VIA (1)	CADENAMIENTOS		ENTRE-VIA
1		0.000	0.000	0.000	13+495.749	13+583.945	
	3.494						
2 TE ET		0.002	0.001	0.001	13+499.243	13+580.451	
	3.494						
3		0.010	0.005	0.005	13+502.737	13+576.957	
	4.494						
4		0.022	0.011	0.011	13+507.231	13+572.463	
	4.494						
5		0.036	0.018	0.018	13+511.725	13+567.969	2.900
	4.494						
6		0.048	0.024	0.024	13+516.219	13+563.475	
	4.494						
7		0.060	0.030	0.030	13+520.713	13+558.981	
	3.494						
EC CE		0.068	0.034	0.034	13+524.207	13+555.487	
	3.494						
9		0.070	0.035	0.035	13+527.701	13+551.993	

NOTA

Ver plano 69-VI-116-III-34

LOS CADENAMIENTOS NO SON OFICIALES

FECHA	MODIFICACION	APROBO

STC
SISTEMA DE TRANSPORTE COLECTIVO
METRO
DEPARTAMENTO DEL DISTRITO FEDERAL
SOFRETU

LINEA Nº1
PROLONGACION
TRAMO: JUANACATLAN - TACUBAYA
curvas 69 y 70
SOBRE-ELEVACIONES
CURVA Nº 8

ESCALA	FECHA	DIBUJO	PLANO NO.
ACOT. EN MM	21/SEP./69	I. S. T. M. E.	106

V°B° PROYECTO | APROBADO

Plano No. 69-VI-116-III-06