24

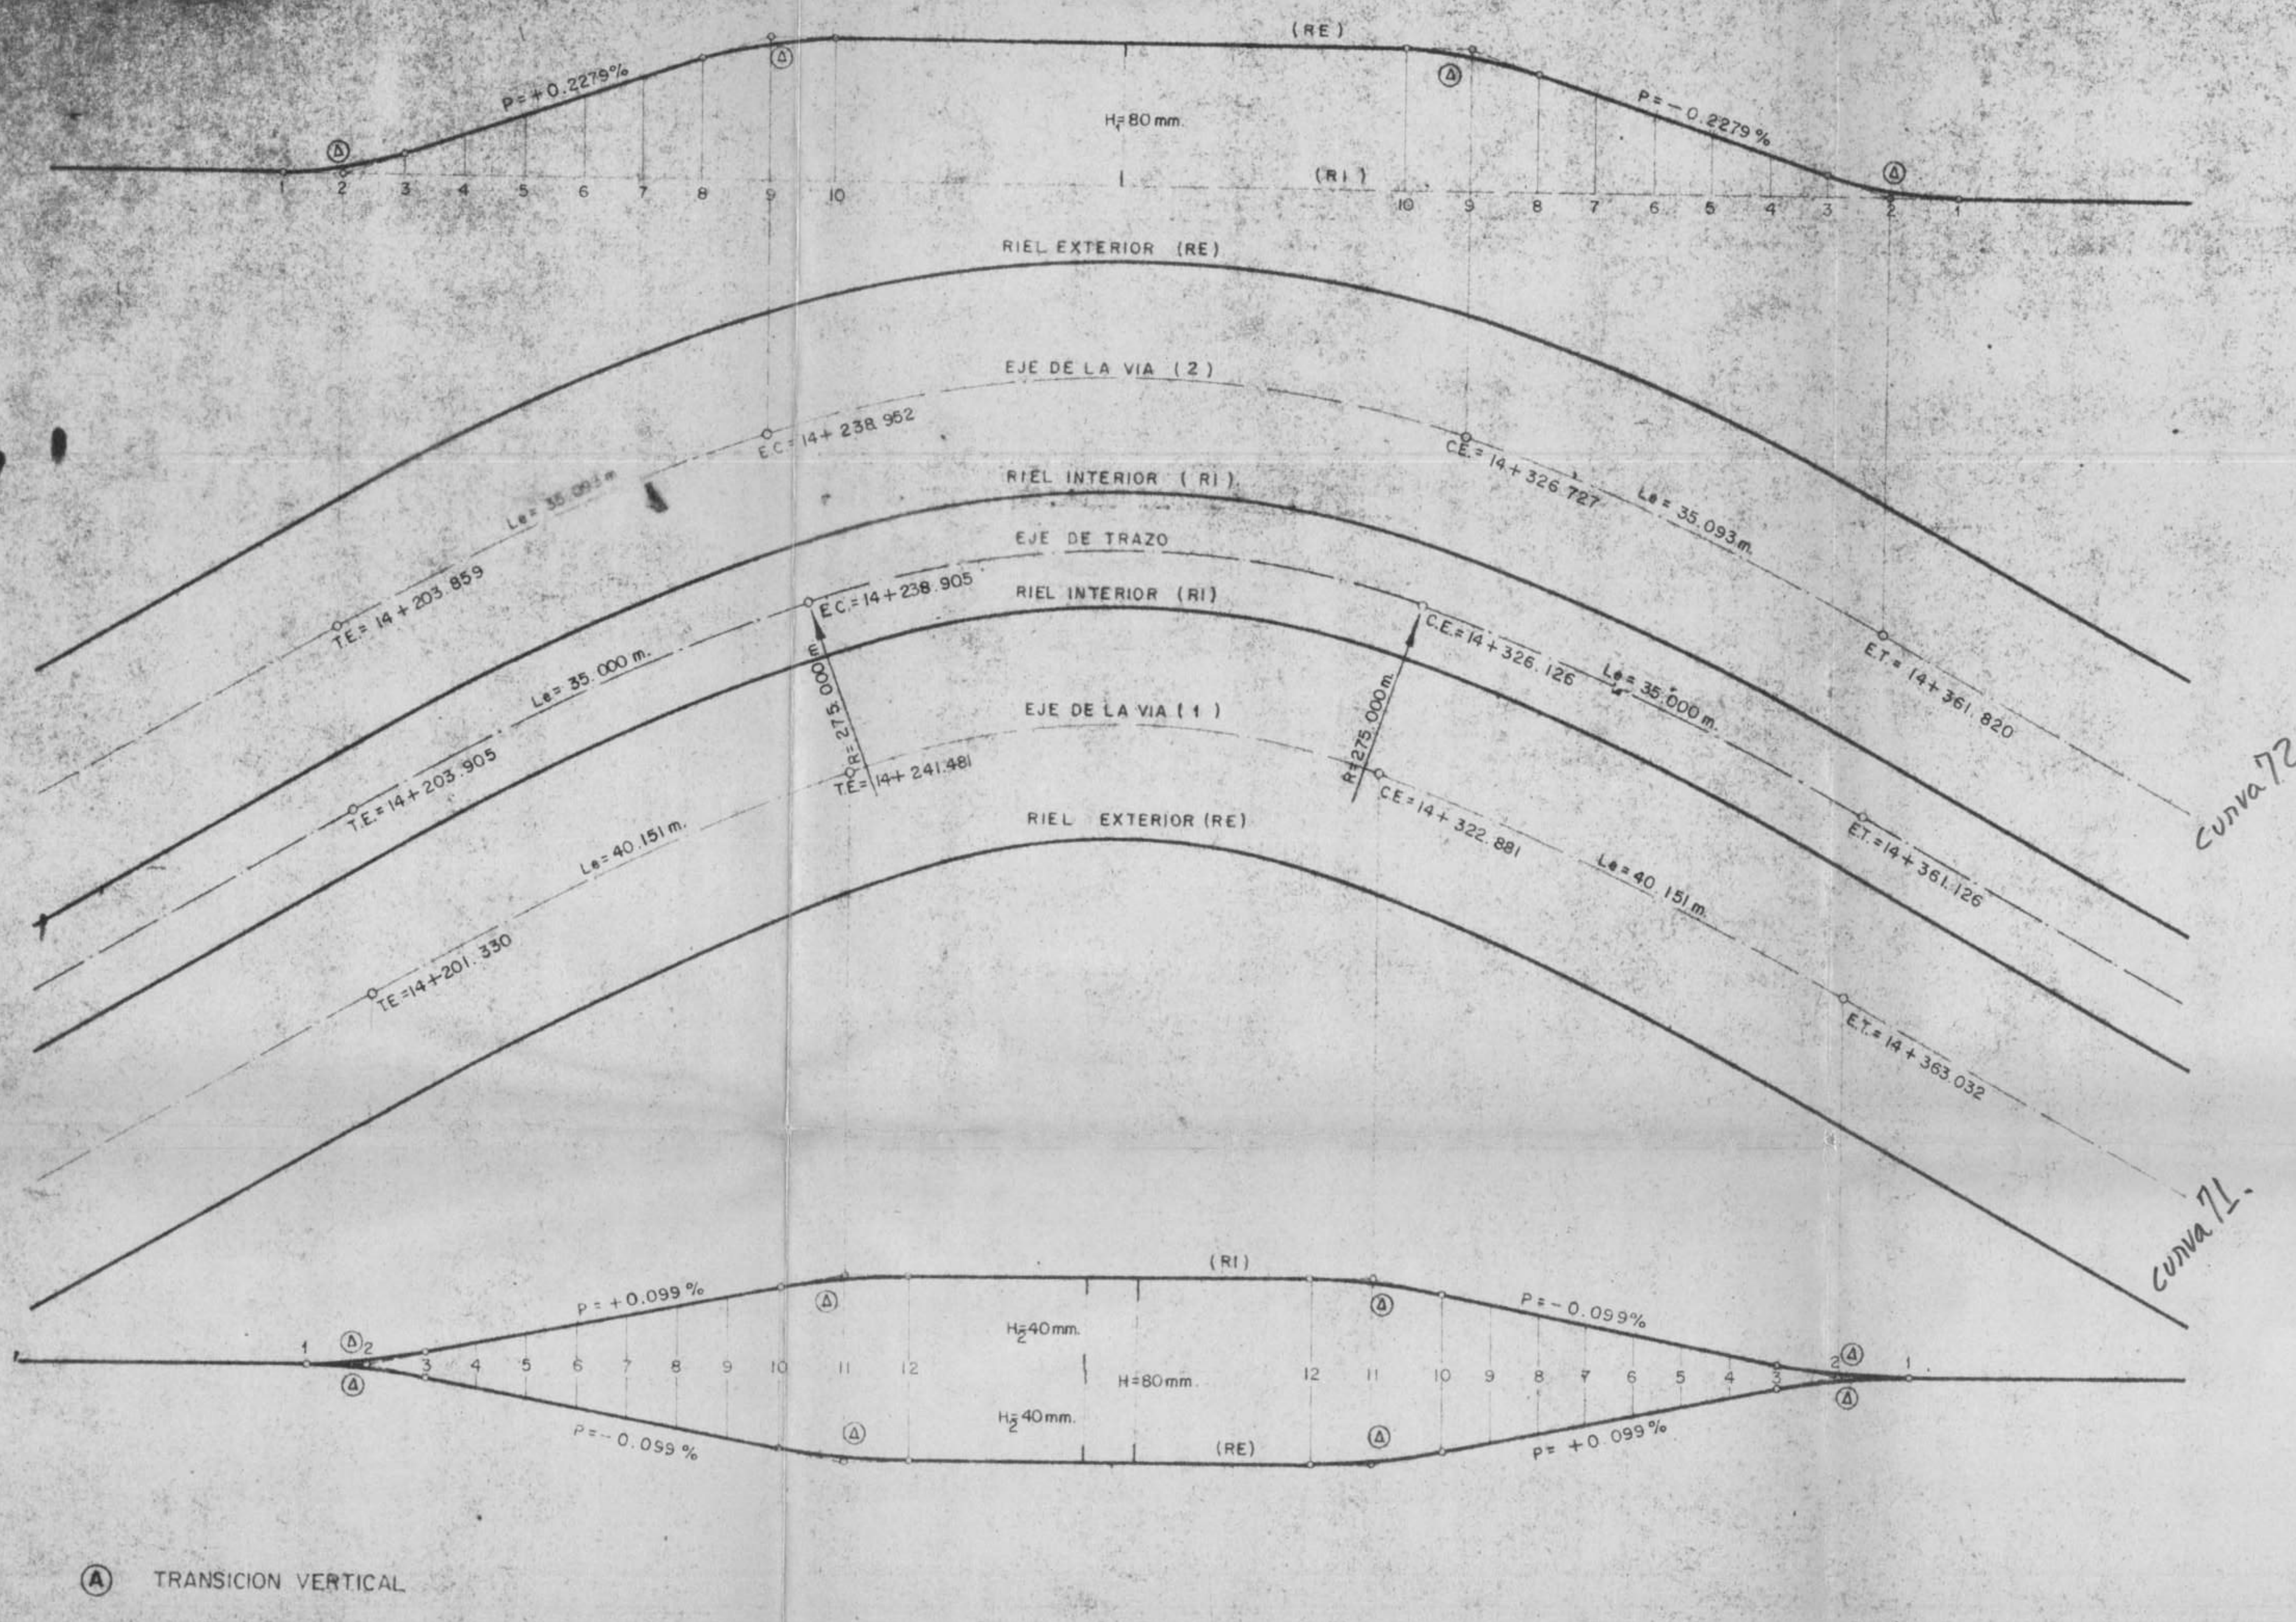

Ⓐ TRANSICION VERTICAL

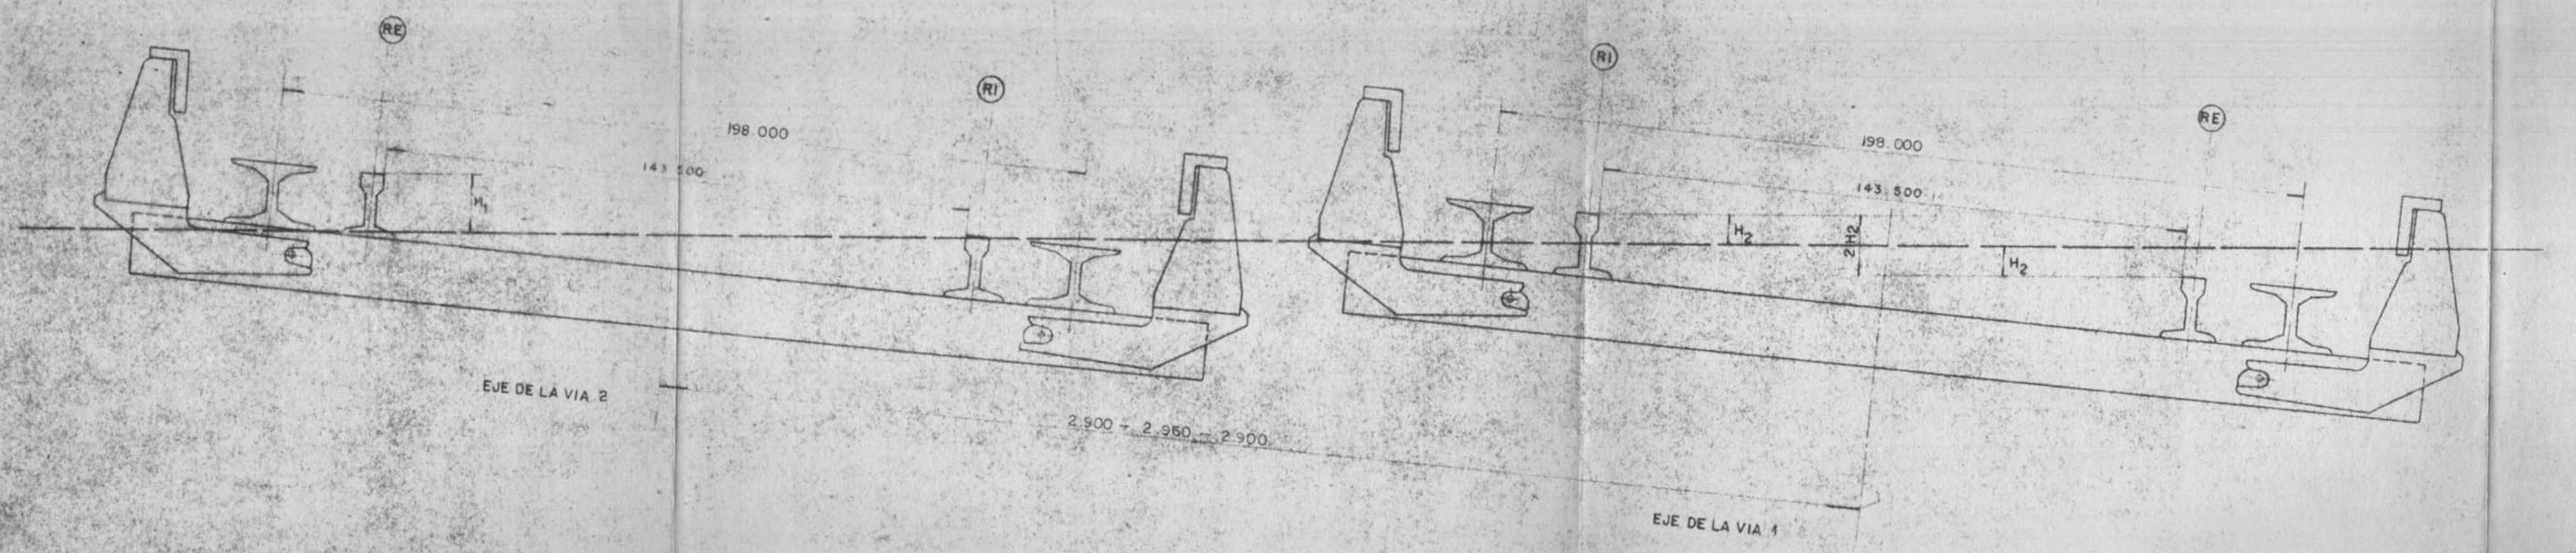

NUM. DE SECCION	DISTANCIA	SOBRE-ELEVACION TOTAL	R E VIA (2)	R I VIA (2)	CADENAMIENTOS		ENTRE-VIA
1		0.000	0.000	0.000	14+201.010	14+364.669	2.900 - 2.960 - 2.900
	2.849						
T.E. 2 E.T.		0.002	+0.002	0.000	14+203.859	14+361.820	
	2.849						
3		0.006	+0.006	0.000	14+206.708	14+358.971	
	5.879						
4		0.019	+0.019	0.000	14+212.587	14+353.092	
	5.879						
5		0.033	+0.033	0.000	14+218.466	14+347.213	
	5.879						
6		0.045	+0.045	0.000	14+224.345	14+341.334	
	5.879						
7		0.060	+0.060	0.000	14+230.224	14+335.455	
	5.879						
8		0.074	+0.074	0.000	14+236.103	14+329.576	
	2.849						
E.C. 9 C.E.		0.078	+0.078	0.000	14+238.952	14+326.727	
	2.849						
10		0.080	+0.080	0.000	14+241.801	14+323.878	

NUM. DE SECCION	DISTANCIA	SOBRE-ELEVACION TOTAL	R E VIA (1)	R I VIA (1)	CADENAMIENTOS		ENTRE-VIA
1		0.000	0.000	0.000	14+200.085	14+364.277	2.900 - 2.960 - 2.900
	1.245						
T.E. 2 E.T.		0.000	-0.000	+0.000	14+201.330	14+363.032	
	1.245						
3		0.002	-0.001	+0.001	14+202.575	14+361.787	
	5.380						
4		0.012	-0.006	+0.006	14+207.955	14+356.406	
	5.380						
5		0.024	-0.012	+0.012	14+213.335	14+351.026	
	5.380						
6		0.034	-0.017	+0.017	14+218.715	14+345.646	
	5.380						
7		0.044	-0.022	+0.022	14+224.095	14+340.266	
	5.380						
8		0.056	-0.028	+0.028	14+229.475	14+334.886	
	5.380						
9		0.066	-0.033	+0.033	14+234.855	14+329.506	
	5.380						
10		0.078	-0.039	+0.039	14+240.235	14+324.126	
	1.245						
E.C. 11 C.E.		0.080	-0.040	+0.040	14+241.481	14+322.881	
	1.245						
12		0.080	-0.040	+0.040	14+242.726	14+321.636	

NOTA.
LOS CADENAMIENTOS SON OFICIALES

FECHA	MODIFICACION	APROBO

STC
SISTEMA DE TRANSPORTE COLECTIVO
M E T R O
Aprobado
DEPARTAMENTO DEL DISTRITO FEDERAL
S.O.F.R.E.T.U.

LINEA Nº1

TRAMO: CHAPULTEPEC- PERIFERICO.
SUB-TRAMO: B FRANKLIN - TACUBAYA

SOBRE - ELEVACIONES

CURVA Nº 71 y 72.

ESCALA	FECHA	DIBUJO	PLANO No.:
S I N	27- JULIO-70	L S I M E	70-VI-118 III - 35

Vo. Bo. PROYECTO
APROBADO

010.021.118-32
01.021.118-35