
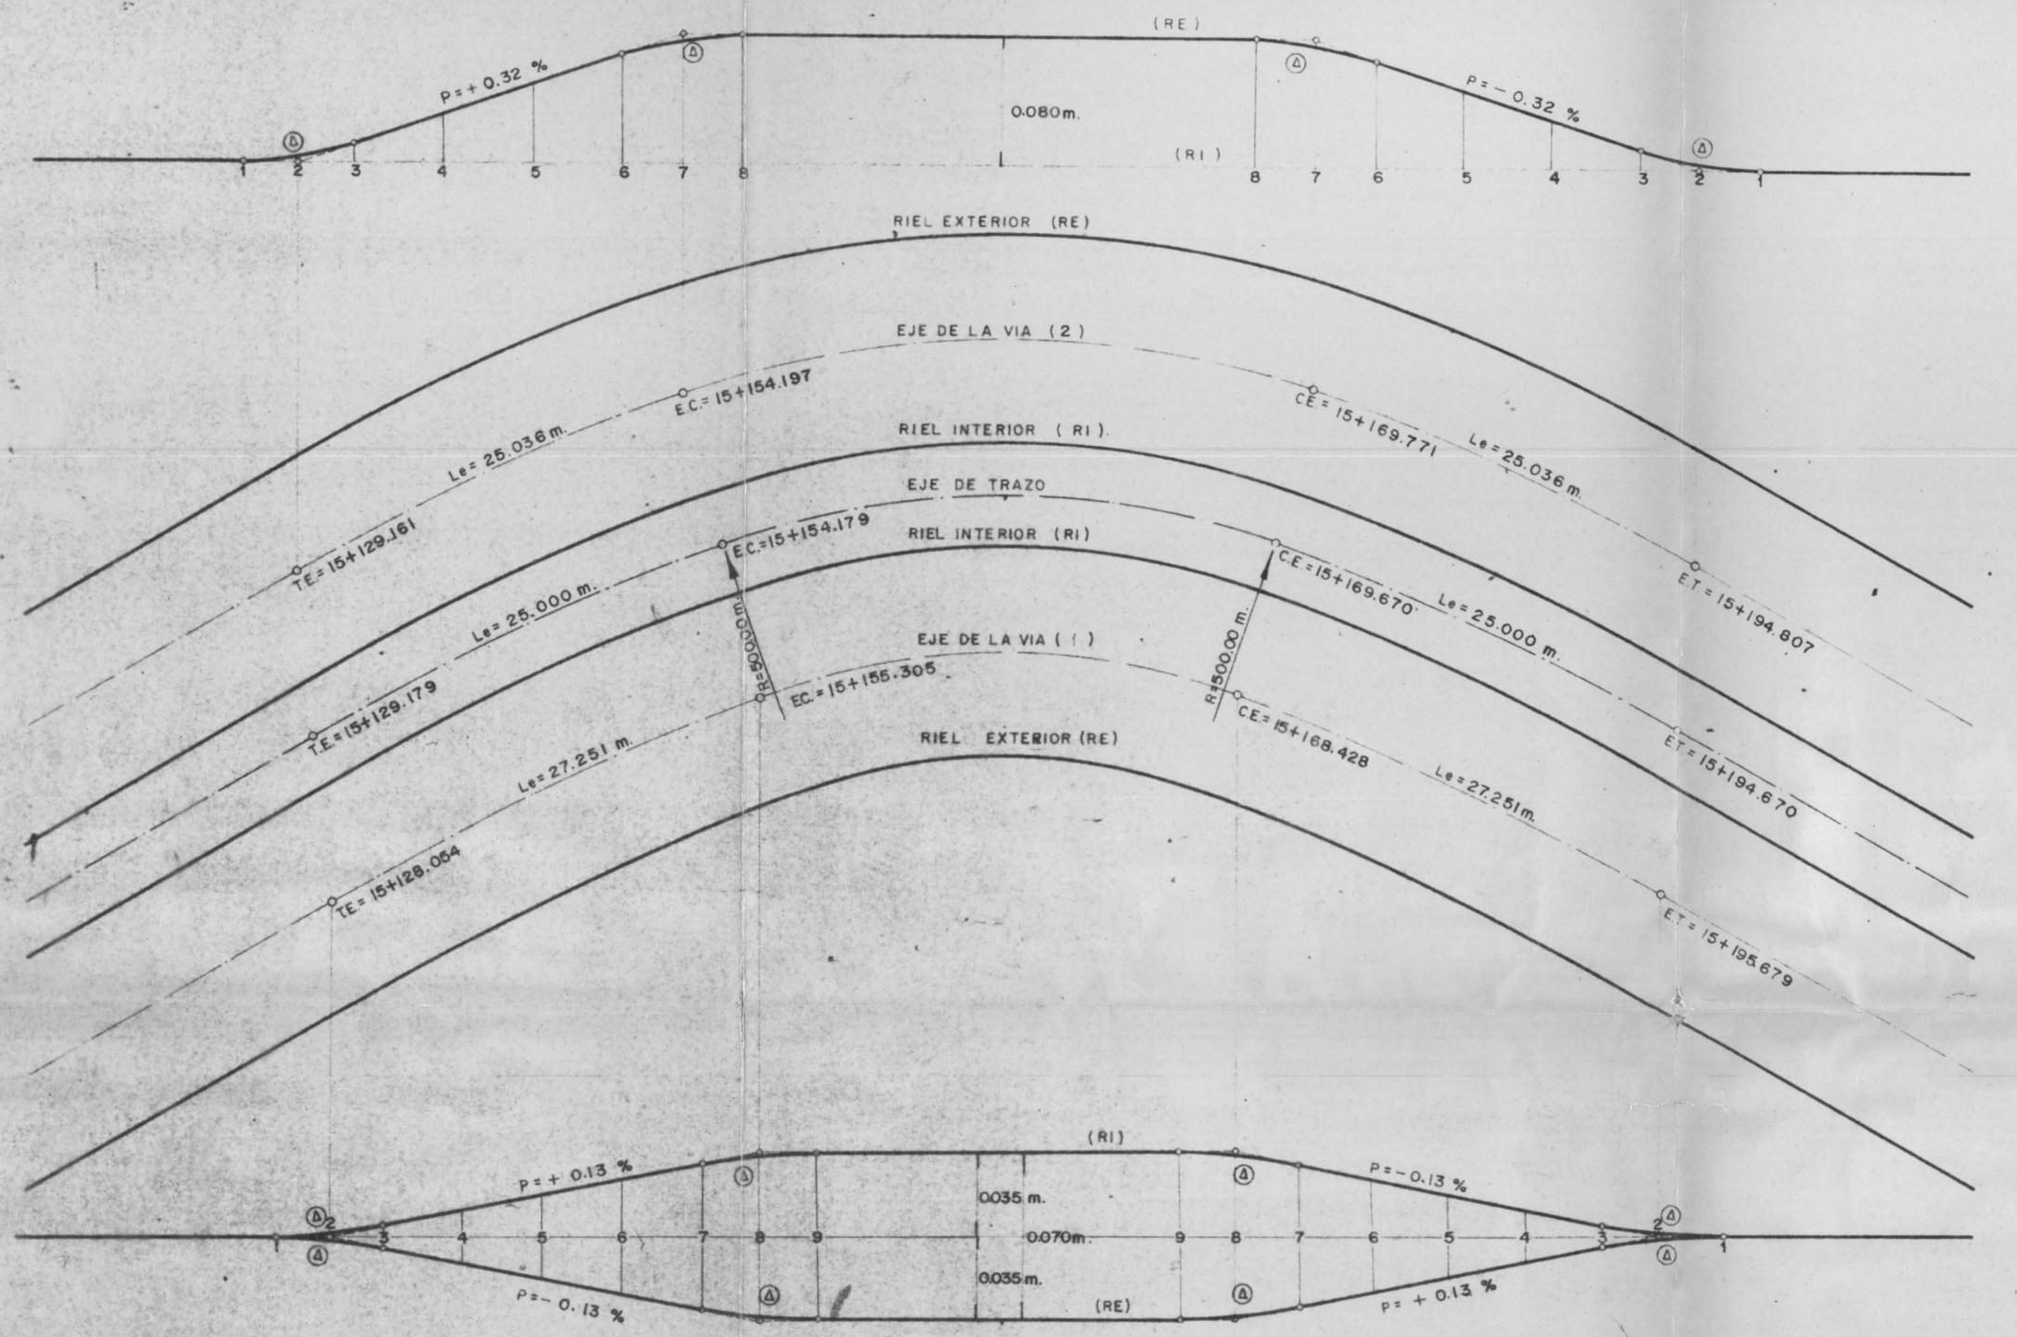


NUM. DE SECCION	DISTANCIA	SOBRE-ELEVACION TOTAL.	R E VIA (2).	R I VIA (2)	CADENAMIENTOS		ENTRE-VIA
1		0.000	0.000	0.000	15+125.168	15+198.800	
	3.993						
2 TE. ET.		0.003	+0.003	0.000	15+129.161	15+194.807	
	3.993						
3		0.013	+0.013	0.000	15+133.154	15+190.814	
	5.683						
4		0.031	+0.031	0.000	15+138.837	15+185.130	
	5.683						
5		0.049	+0.049	0.000	15+144.520	15+179.447	
	5.683						
6		0.067	+0.067	0.000	15+150.204	15+173.764	2.90 - 2.91 - 2.90
	3.993						
7 EC. CE.		0.077	+0.077	0.000	15+154.197	15+169.771	
	3.993						
8		0.080	+0.080	0.000	15+158.190	15+165.778	

NUM. DE SECCION	DISTANCIA	SOBRE-ELEVACION TOTAL.	R E VIA(1).	R I VIA(1)	CADENAMIENTOS.		ENTRE-VIA
1		0.000	0.000	0.000	15+126.449	15+197.284	
	1.605						
2 TE. ET.		0.002	-0.001	+0.001	15+128.054	15+195.679	
	1.605						
3		0.004	-0.002	+0.002	15+129.659	15+194.074	2.90
	6.010						
4		0.020	-0.010	+0.010	15+135.669	15+188.063	
	6.010						
5		0.036	-0.018	+0.018	15+141.679	15+182.053	2.90 - 2.91 - 2.90
	6.010						
6		0.052	-0.026	+0.026	15+147.689	15+176.043	
	6.010						
7		0.066	-0.033	+0.033	15+153.700	15+170.033	
	1.605						
8 EC. CE.		0.068	-0.034	+0.034	15+155.305	15+168.428	
	1.605						
9		0.070	-0.035	+0.035	15+156.910	15+166.823	

(A) TRANSICION VERTICAL

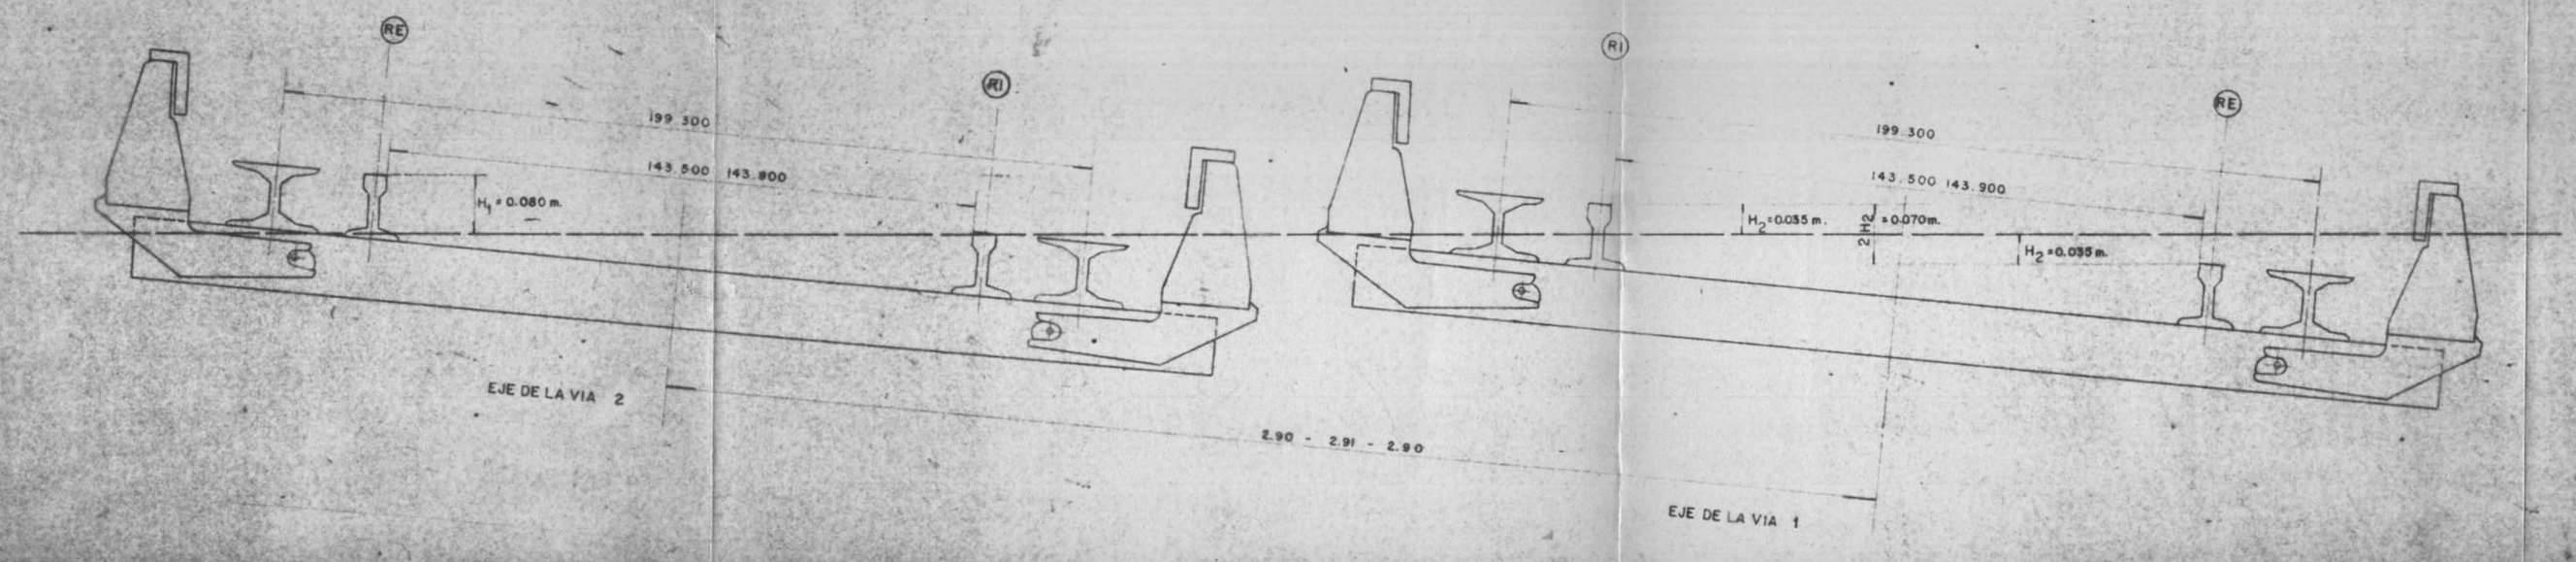

FECHA	MODIFICACION	APROBO	
STC SISTEMA DE TRANSPORTE COLECTIVO METRO	LINEA Nº1		
	TRAMO: TACUBAYA - OBSERVATORIO		
	SUB-TRAMO: TACUBAYA - EC. OBSERVATORIO		
	SOBRE-ELEVACIONES		
	CURVA Nº 77 Y 78		
ESCALA:	FECHA: FEB./16/71	DIBUJO: I. S. T. M. E.	PLANO NO.: 71-VI-116 III-38 S
SOMETIDO	NO. DE PROYECTO	APROBADO	

21.021.118-38