
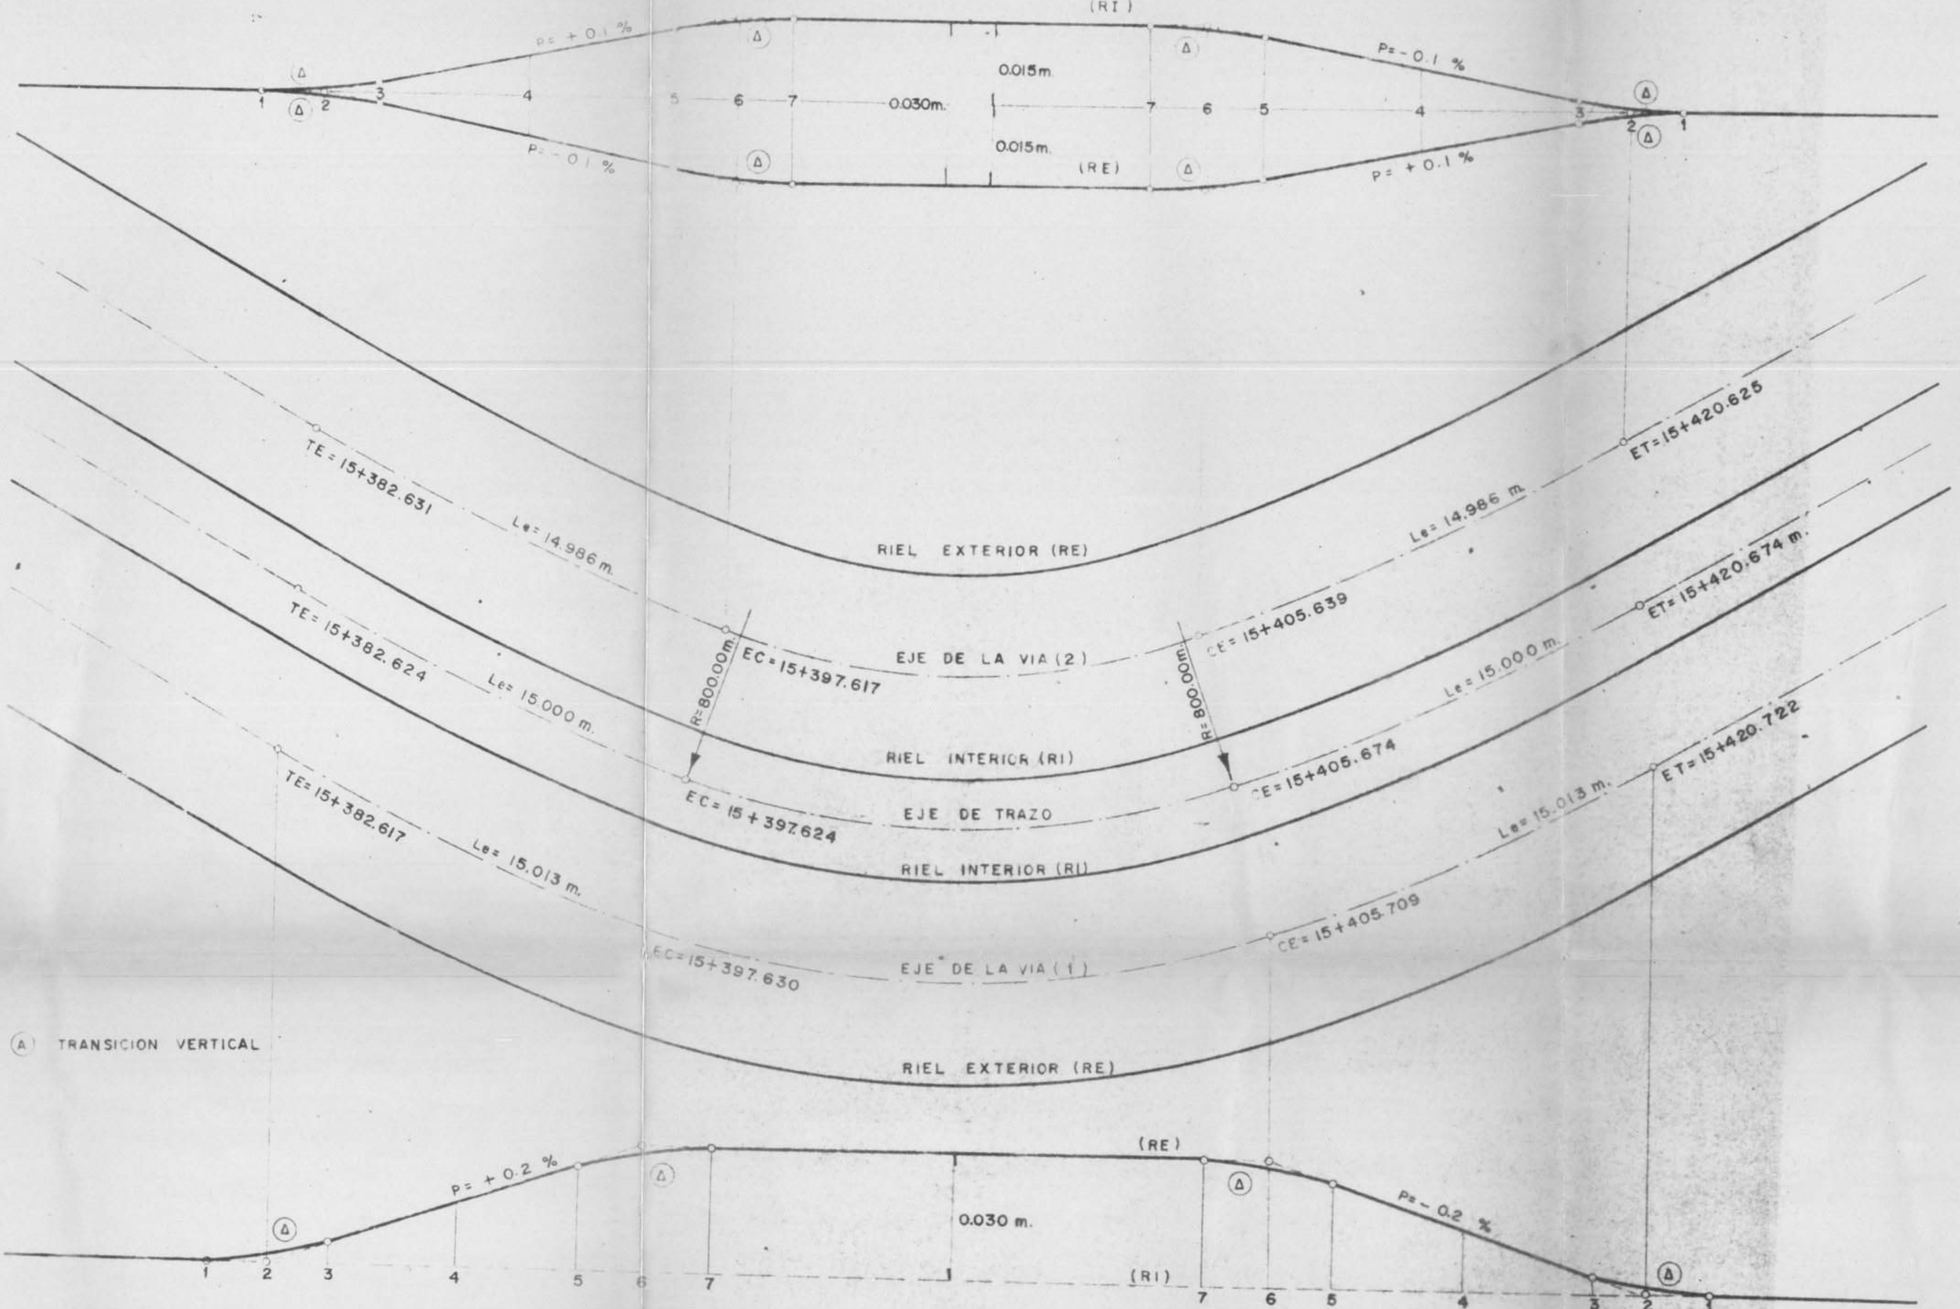


Nº DE SECCION	DIST.	SOBRE ELEVACION TOTAL	R.E VIA (2)	R.I VIA (2)	CADENAMIENTOS		ENTRE VIA
1		0.000	0.000	0.000	15+381.381	15+421.875	
	1.250						
2 TE. ET.		0.000	0.000	0.000	15+382.631	15+420.625	
	1.250						
3		0.002	-0.001	+0.001	15+383.881	15+419.375	
	6.243						
4		0.014	-0.007	+0.007	15+390.124	15+413.132	
	6.243						
5		0.028	-0.014	+0.014	15+396.367	15+406.889	
	1.250						
6 EC. CE.		0.030	-0.015	+0.015	15+397.617	15+405.639	
	1.250						
7		0.030	-0.015	+0.015	15+398.867	15+404.389	

2.900 m.

Nº DE SECCION	DIST.	SOBRE ELEVACION TOTAL	R.E VIA (1)	R.I VIA (1)	CADENAMIENTOS		ENTRE VIA
1		0.000	0.000	0.000	15+380.120	15+423.219	
	2.497						
2 TE. ET.		0.001	+0.001	0.000	15+382.617	15+420.722	
	2.497						
3		0.005	+0.005	0.000	15+385.114	15+418.225	
	5.009						
4		0.015	+0.015	0.000	15+390.123	15+413.215	
	5.009						
5		0.025	+0.025	0.000	15+395.133	15+408.206	
	2.497						
6 EC CE		0.029	+0.029	0.000	15+397.630	15+405.709	
	2.497						
7		0.030	+0.030	0.000	15+400.127	15+403.212	

2.900 m.

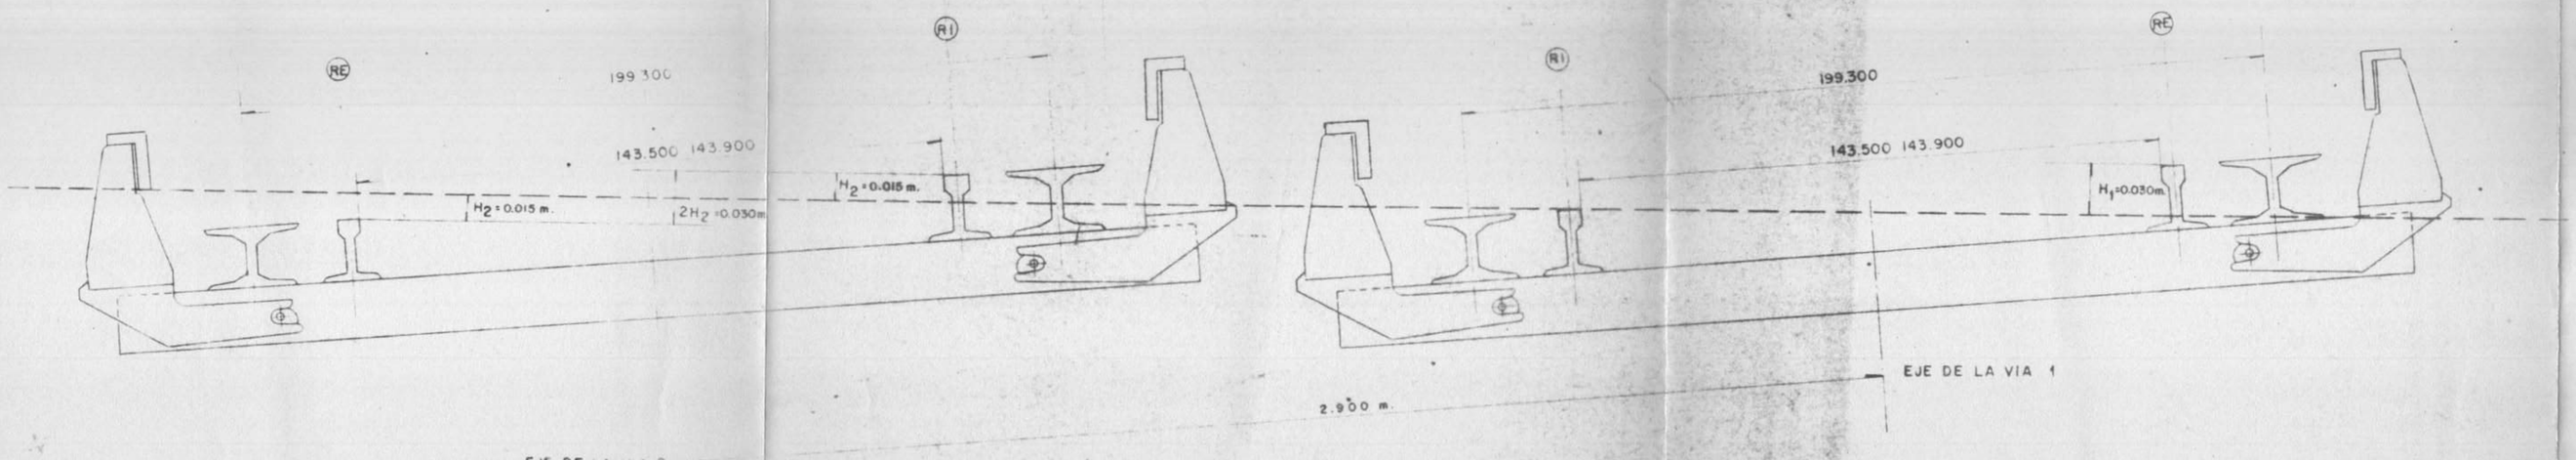

FECHA	MODIFICACION	APROBO

STC
SISTEMA DE TRANSPORTE COLECTIVO
METRO
DEPARTAMENTO DEL DISTRITO FEDERAL

LINEA Nº 1
TRAMO: TACUBAYA-OBSERVATORIO
SUB-TRAMO: F.C. CUERNAVACA-OBSERVATORIO
SOBRE-ELEVACIONES
CURVA Nº 79 Y 80

ESCALA	FECHA	DIBUJO	PLANO NO
	FEB. 15 '71	I. S. T. M. E.	71-VL-118 III-39SE

S.O.F.R.E.T.H. SCT
JEFE DE PROYECTO
APROBADO

01.621:118-39