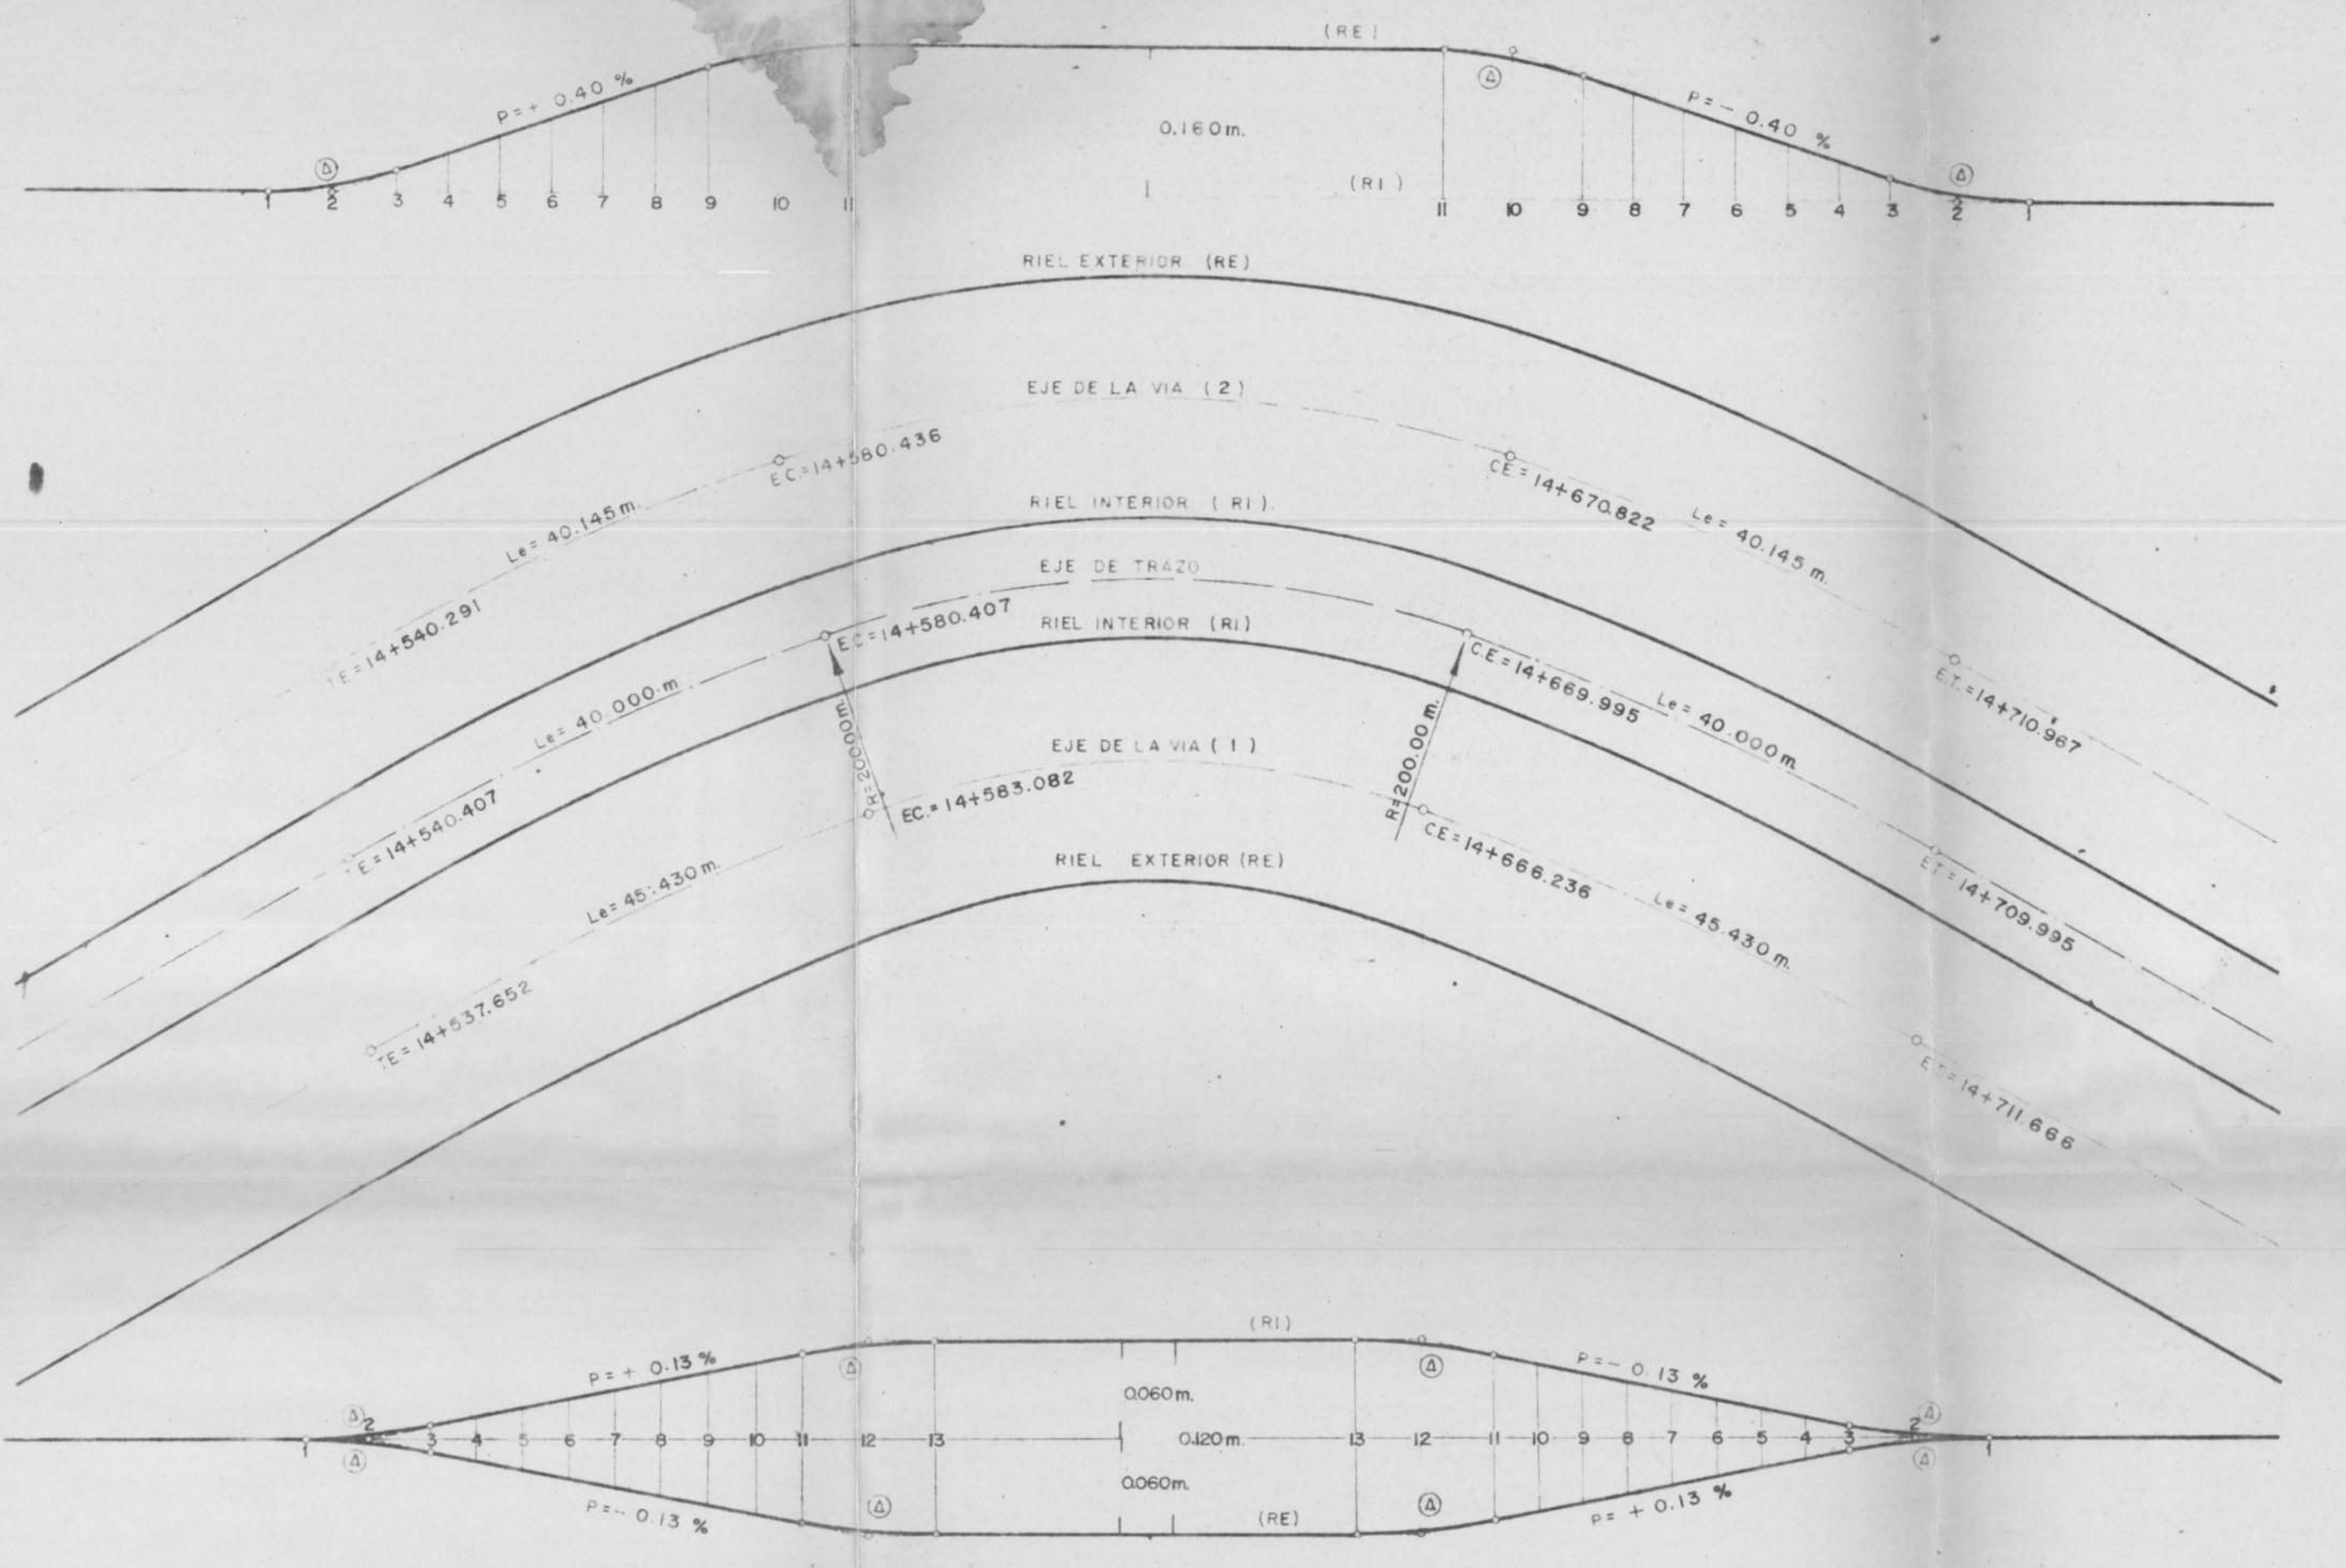

Ⓐ TRANSICION VERTICAL

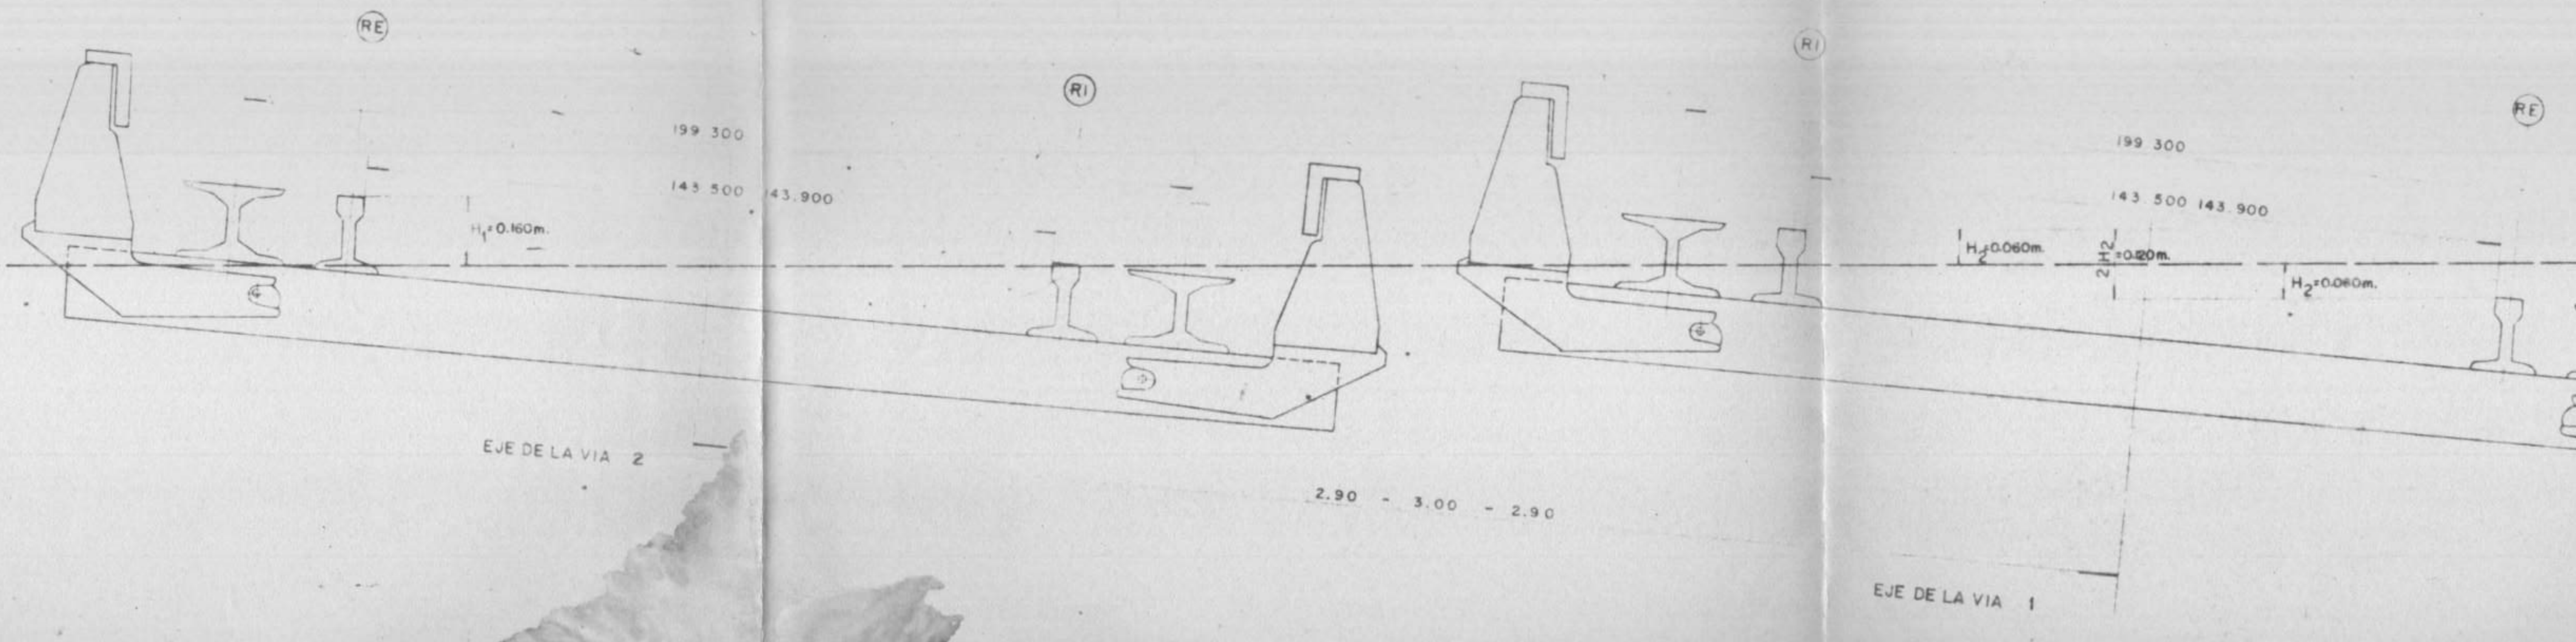

NUM DE SECCION	DISTANCIA	SOBRE-ELEVACION TOTAL	R E VIA (2)	R I VIA (2)	CADENAMIENTOS		ENTRE-VIA
1		0.000	0.000	0.000	14+535.310	14+715.948	2.90 - 3.00 - 2.90
	4.981						
2 TE. ET.		0.005	+0.005	0.000	14+540.291	14+710.967	
	4.981						
3		0.020	+0.020	0.000	14+545.272	14+705.986	
	5.030						
4		0.040	+0.040	0.000	14+550.302	14+700.955	
	5.030						
5		0.060	+0.060	0.000	14+555.333	14+695.925	
	5.030						
6		0.080	+0.080	0.000	14+560.363	14+690.894	
	5.030						
7		0.100	+0.100	0.000	14+565.394	14+685.864	
	5.030						
8		0.120	+0.120	0.000	14+570.424	14+680.833	
	5.030						
9		0.140	+0.140	0.000	14+575.455	14+675.803	
	4.981						
10 EC. CE.		0.155	+0.155	0.000	14+580.436	14+670.822	
	4.981						
11		0.160	+0.160	0.000	14+585.417	14+665.841	

NUM. DE SECCION	DISTANCIA	SOBRE-ELEVACION TOTAL	R E VIA (1).	R I VIA (1)	CADENAMIENTOS.		ENTRE-VIA
1		0.000	0.000	0.000	14+536.002	14+713.316	2.90 - 3.00 - 2.90
	1.650						
2 TE. ET.		0.002	-0.001	+0.001	14+537.652	14+711.666	
	1.650						
3		0.004	-0.002	+0.002	14+539.302	14+710.016	
	5.266						
4		0.018	-0.009	+0.009	14+544.568	14+704.750	
	5.266						
5		0.032	-0.016	+0.016	14+549.834	14+699.483	
	5.266						
6		0.046	-0.023	+0.023	14+555.101	14+694.217	
	5.266						
7		0.060	-0.030	+0.030	14+560.367	14+688.951	
	5.266						
8		0.074	-0.037	+0.037	14+565.633	14+683.685	
	5.266						
9		0.088	-0.044	+0.044	14+570.899	14+678.418	
	5.266						
10		0.102	-0.051	+0.051	14+576.166	14+673.152	
	5.266						
11		0.116	-0.058	+0.058	14+581.432	14+667.886	
	1.650						
12 EC. CE.		0.118	-0.059	+0.059	14+583.082	14+666.236	
	1.650						
13		0.120	-0.060	+0.060	14+584.732	14+664.586	

FECHA
MODIFICACION
APROBO

STC
SISTEMA DE TRANSPORTE COLECTIVO
METRO
DEPARTAMENTO DEL DISTRITO FEDERAL
SOFRETU

LINEA Nº1

TRAMO: TACUBAYA - OBSERVATORIO
SUB-TRAMO: TACUBAYA - F.C. CUERNAVACA

SOBRE - ELEVACIONES

CURVA Nº 73 Y 74

ESCALA
FECHA FEB.- 19 -71
DIBUJO L.S.C.M.E.
PLANO NO. 71-VI.-118 III-486-SE
NO. BO. PROYECTO
APROBADO

01.021.118-36