
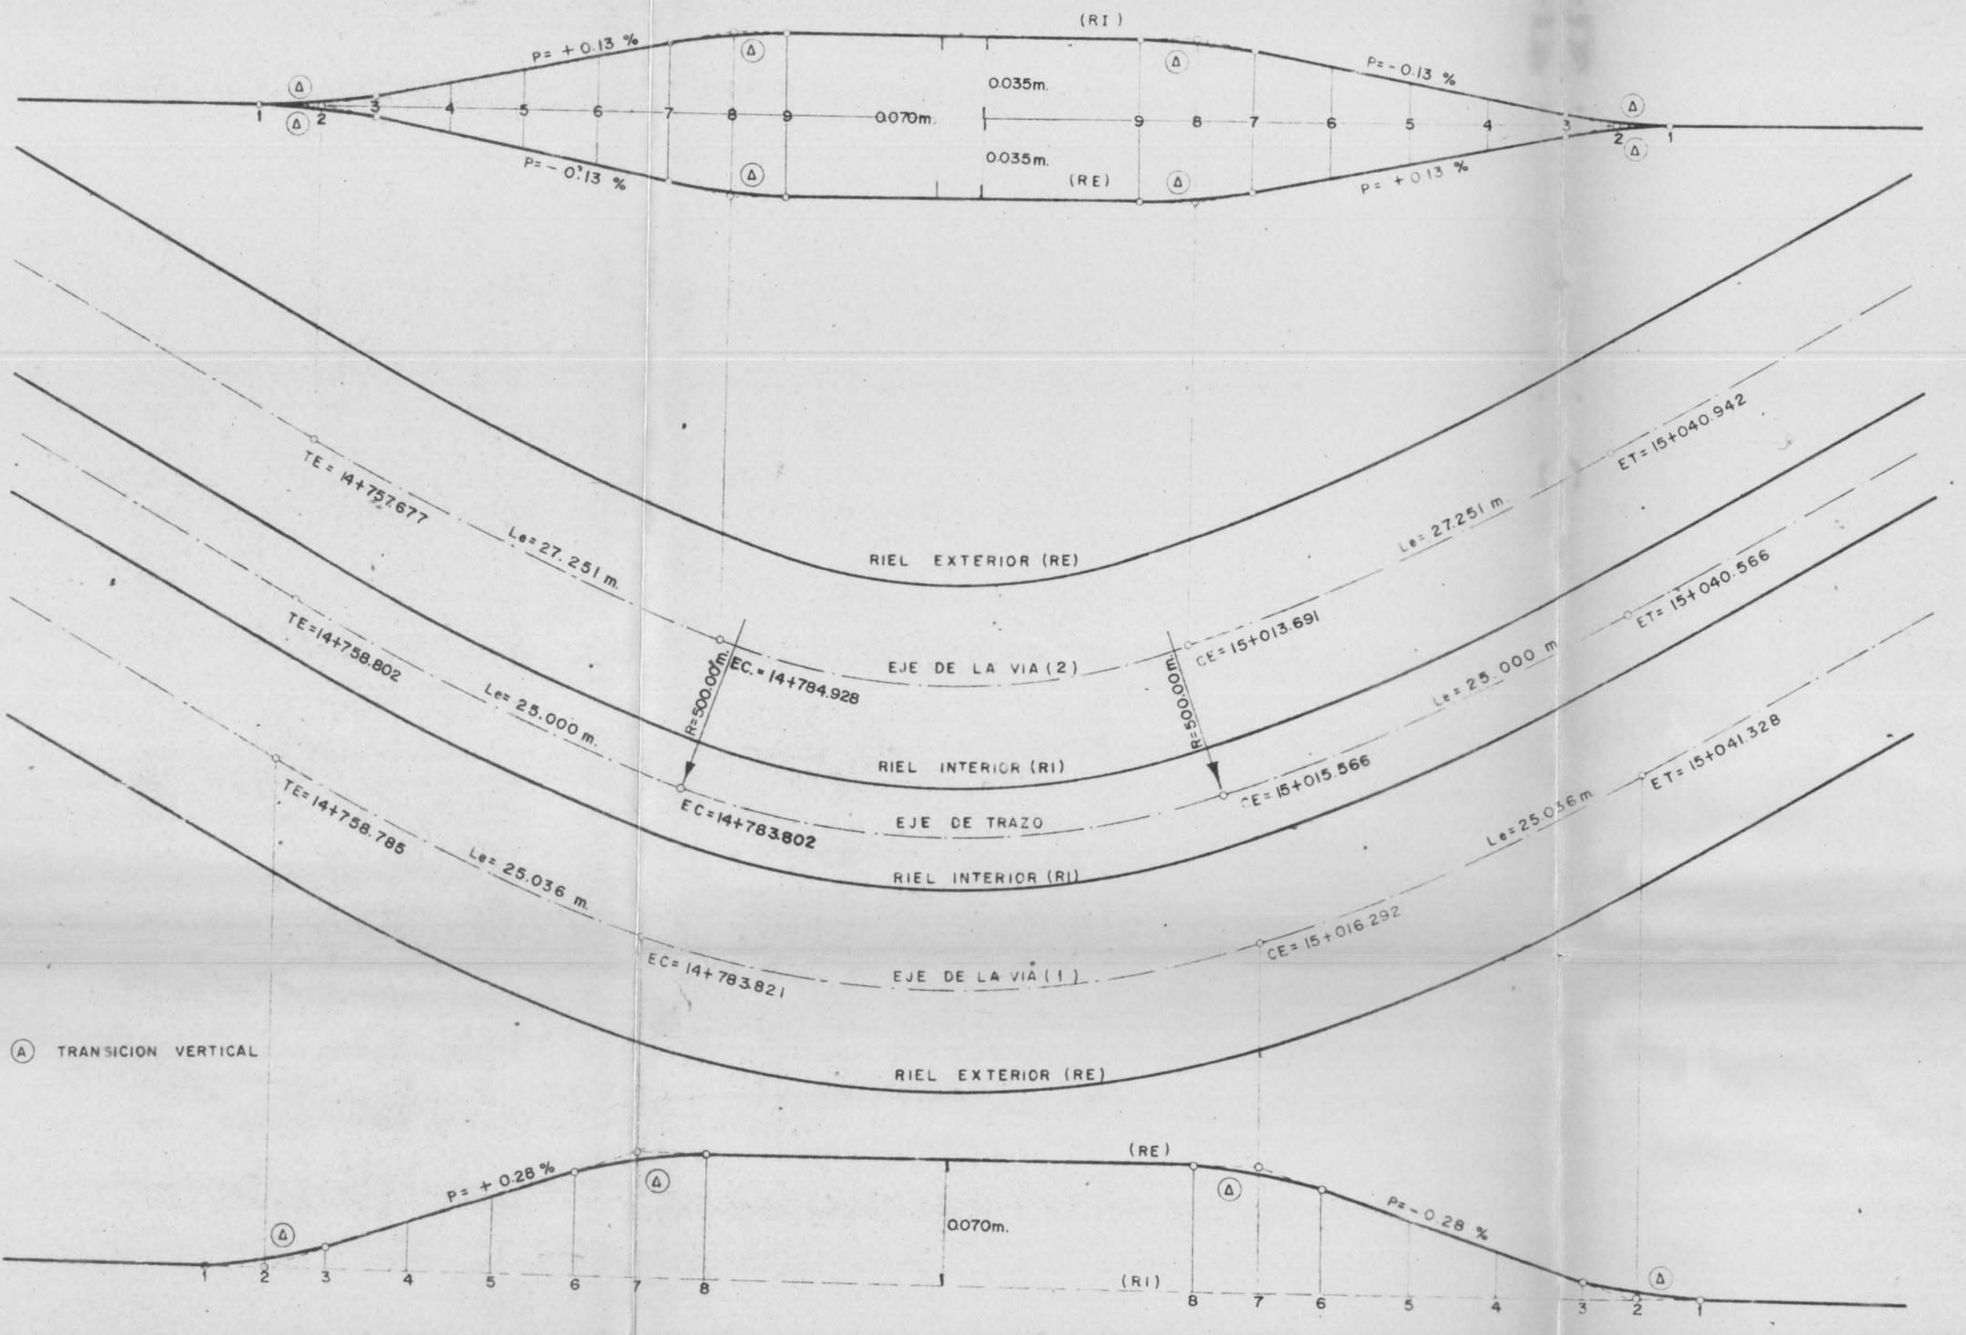


Nº DE SECCION	DIST	SOBRE. ELEVACION TOTAL	R.E VIA (2)	R.I VIA (2)	CADENAMIENTOS		ENTRE VIA
1		0.000	0.000	0.000	14+756.072	15+042.547	
2 TE. ET.	1.605	0.002	-0.001	+0.001	14+757.677	15+040.942	
3	1.605	0.004	-0.002	+0.002	14+759.282	15+039.337	
4	6.010	0.020	-0.010	+0.010	14+765.292	15+033.326	2.90 - 2.91 - 2.90
5	6.010	0.036	-0.018	+0.018	14+771.302	15+027.316	
6	6.010	0.052	-0.026	+0.026	14+777.312	15+021.306	
7	6.010	0.066	-0.033	+0.033	14+783.323	15+015.296	
8 EC. CE.	1.605	0.068	-0.034	+0.034	14+784.928	15+013.691	
9	1.605	0.070	-0.035	+0.035	14+786.533	15+012.086	

Nº DE SECCION	DIST.	SOBRE ELEVACION TOTAL	R.E VIA (1)	R.I VIA (1)	CADENAMIENTOS		ENTRE VIA
1		0.000	0.000	0.000	14+755.291	15+044.822	
2 TE. ET.	3.494	0.002	+0.002	0.000	14+758.785	15+041.328	
3	3.494	0.010	+0.010	0.000	14+762.279	15+037.834	
4	6.016	0.027	+0.027	0.000	14+768.295	15+031.818	
5	6.016	0.044	+0.044	0.000	14+774.311	15+025.802	2.90 - 2.91 - 2.90
6	6.016	0.060	+0.060	0.000	14+780.327	15+019.786	
7 EC. CE.	3.494	0.068	+0.068	0.000	14+783.821	15+016.292	
8	3.494	0.070	+0.070	0.000	14+787.315	15+012.798	

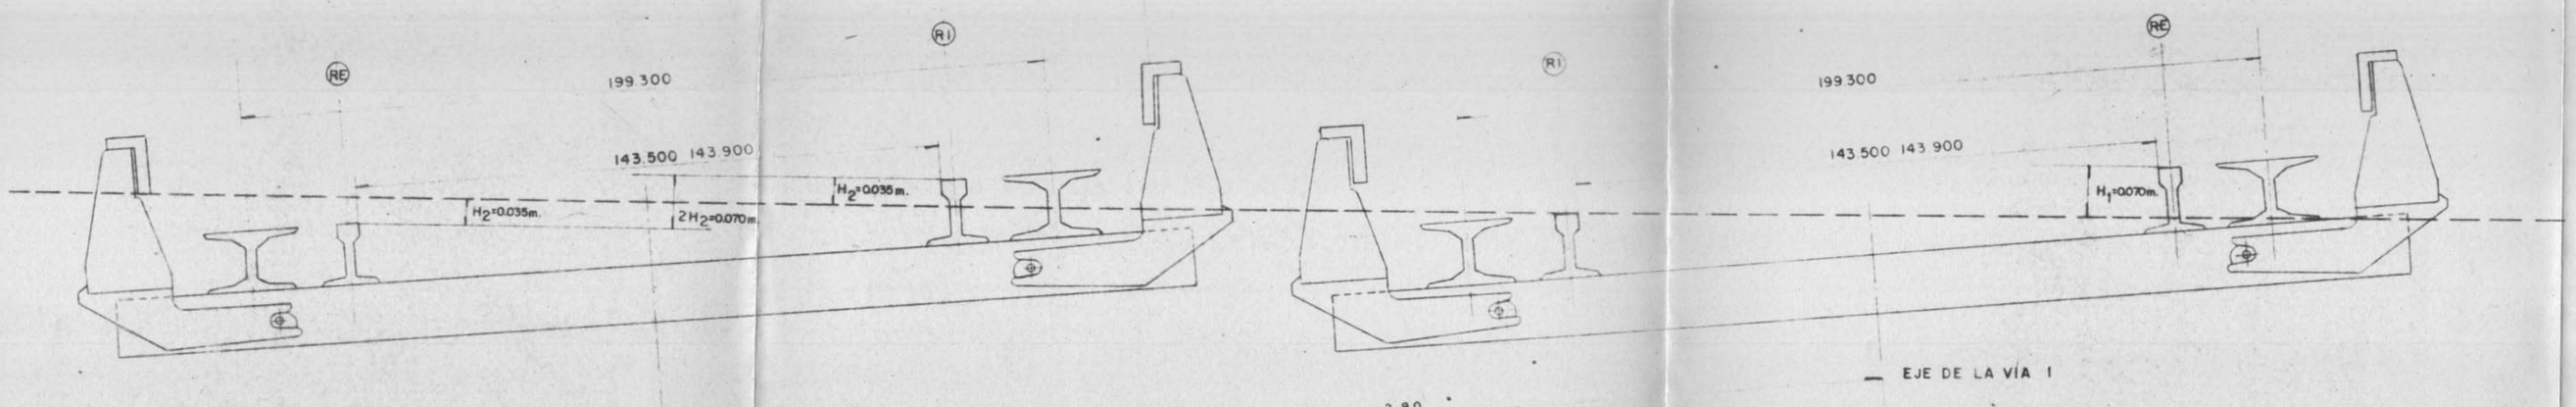

FECHA	MODIFICACION	APROBO

STC
SISTEMA DE TRANSPORTE COLECTIVO
METRO
DEPARTAMENTO DEL DISTRITO FEDERAL

LINEA Nº 1
TRAMO: TACUBAYA - OBSERVATORIO
SUB-TRAMO: TACUBAYA-AV. CUERNAVACA
SOBRE-ELEVACIONES
CURVA Nº 75 Y 76

ESCALA	FECHA	DIBUJO	PLANO NO
	FEB./17/'71	I.S.T.M.E.	71-VI-118 III-37-SE
VO.BO. PROYECTO		APROBADO	

SOFRETU

29

12-811-180-0

Medalla 01.02.118-27