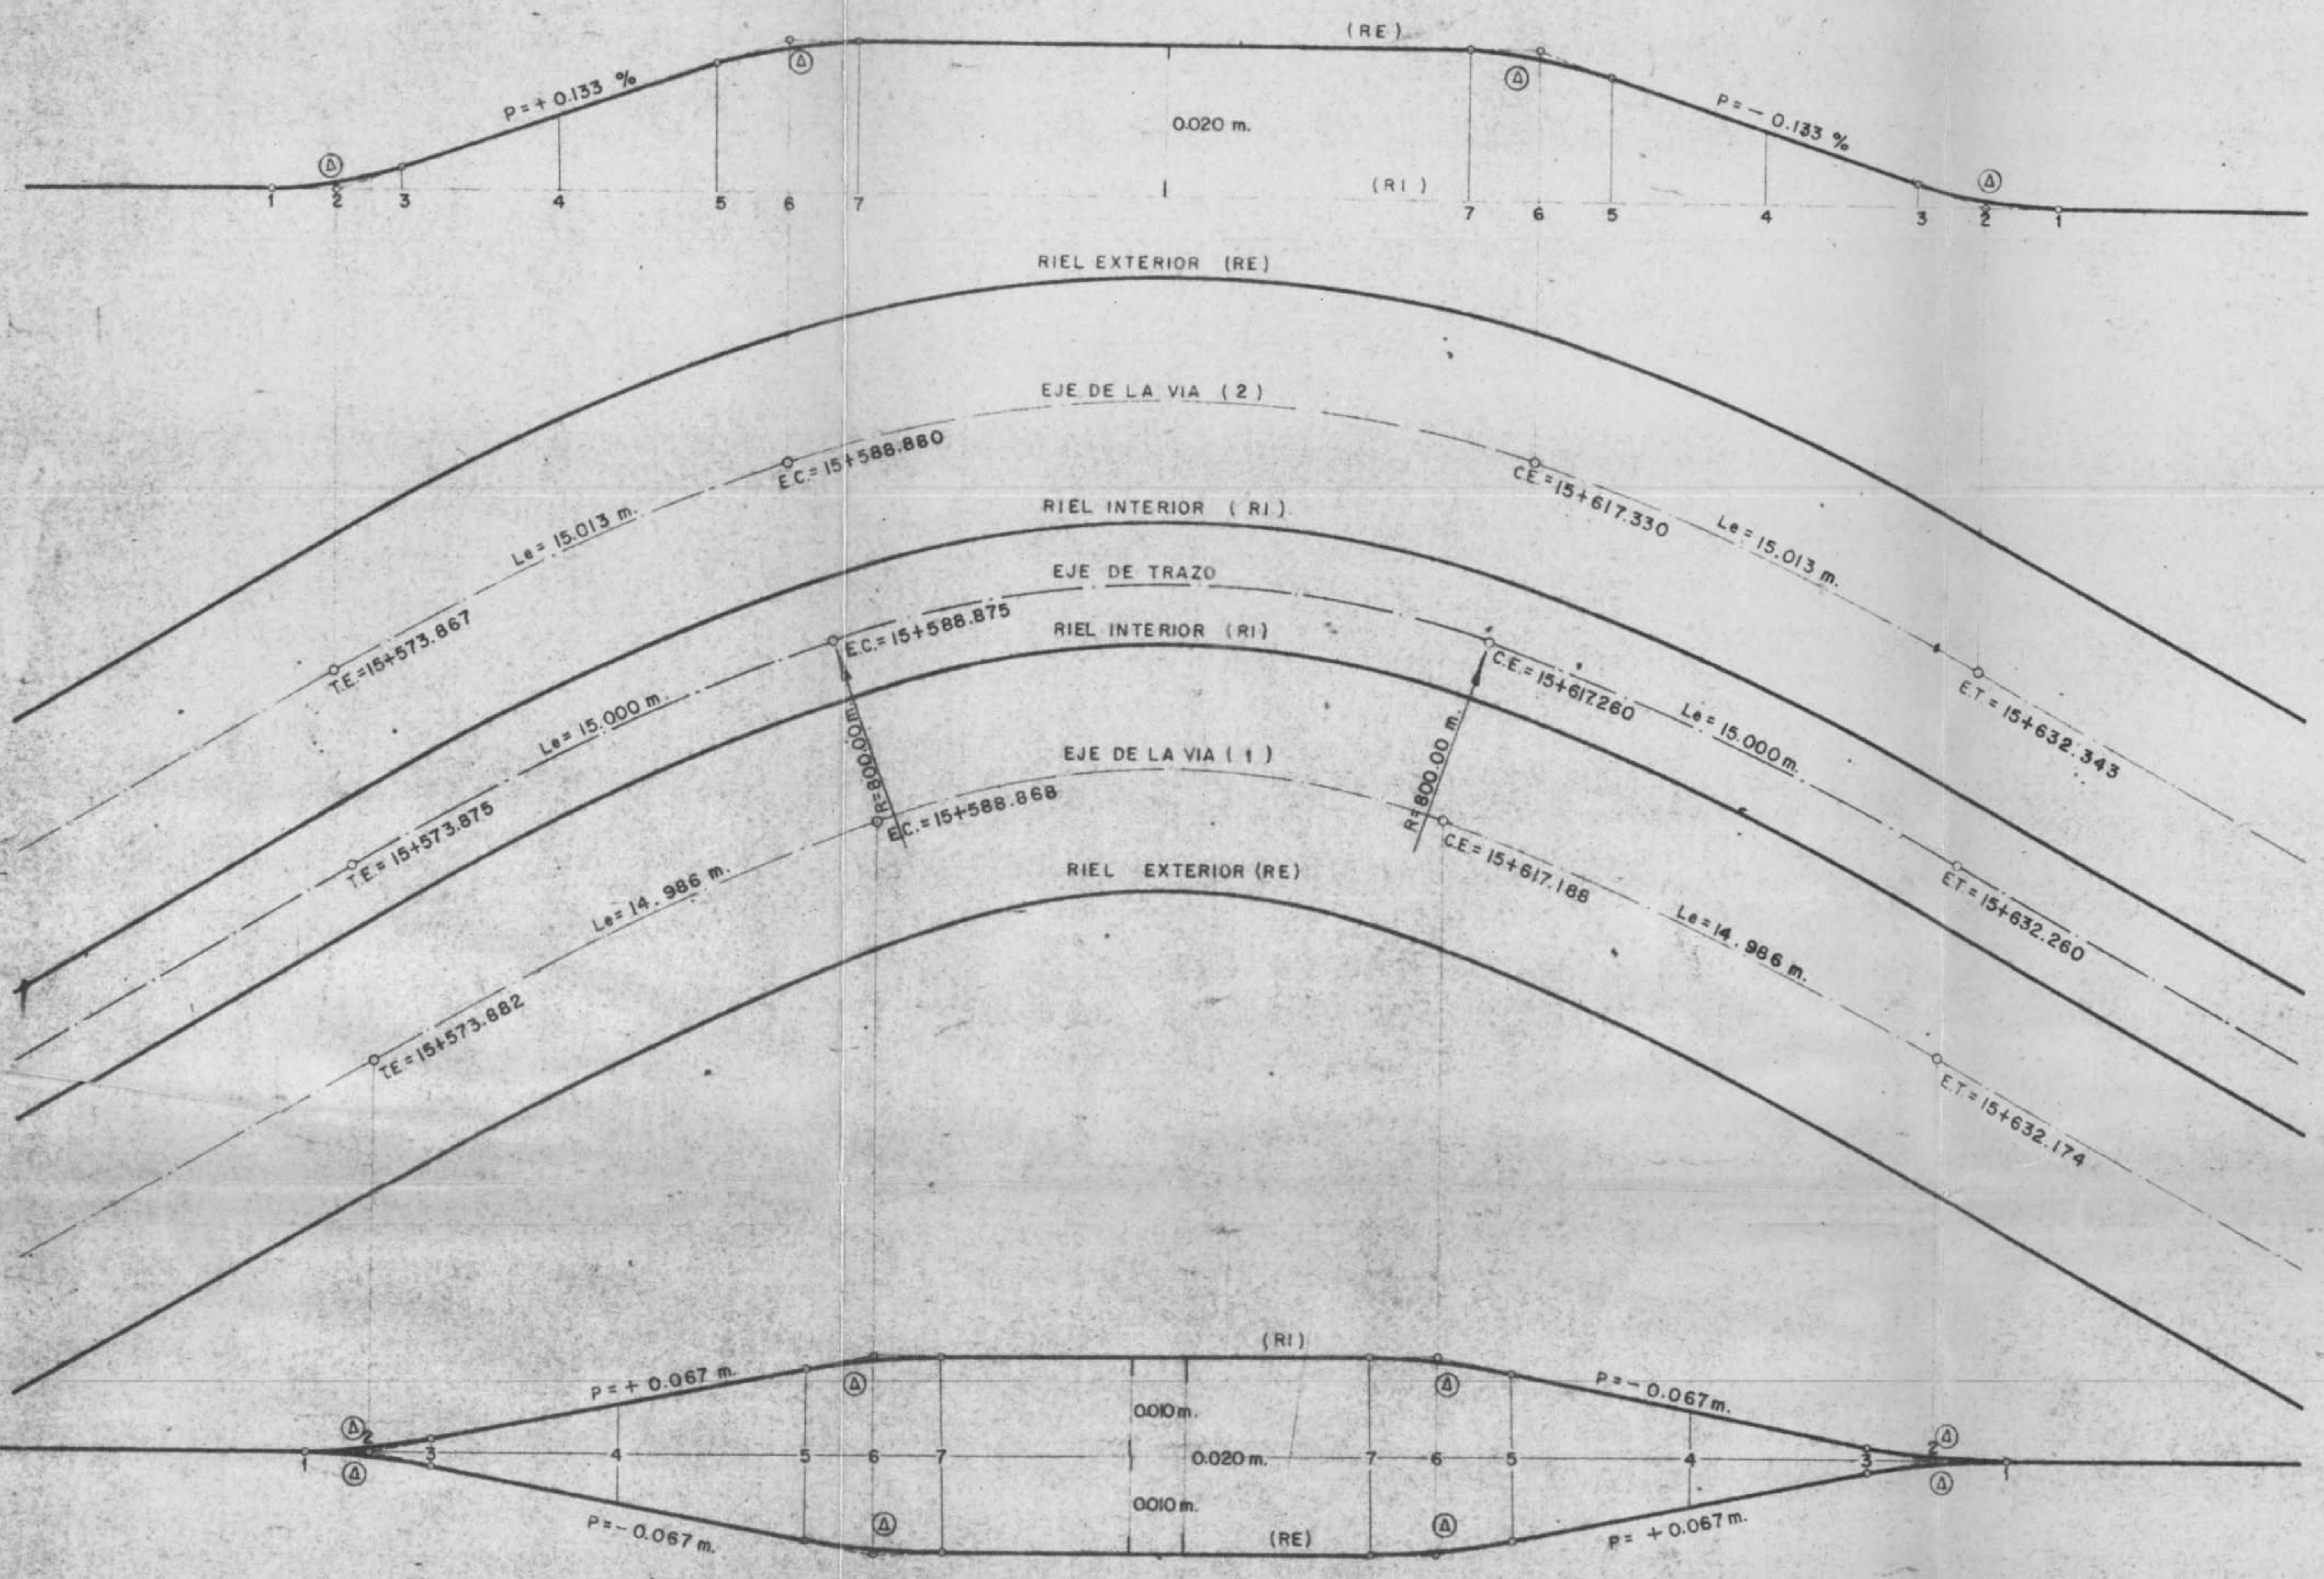

Ⓐ TRANSICION VERTICAL

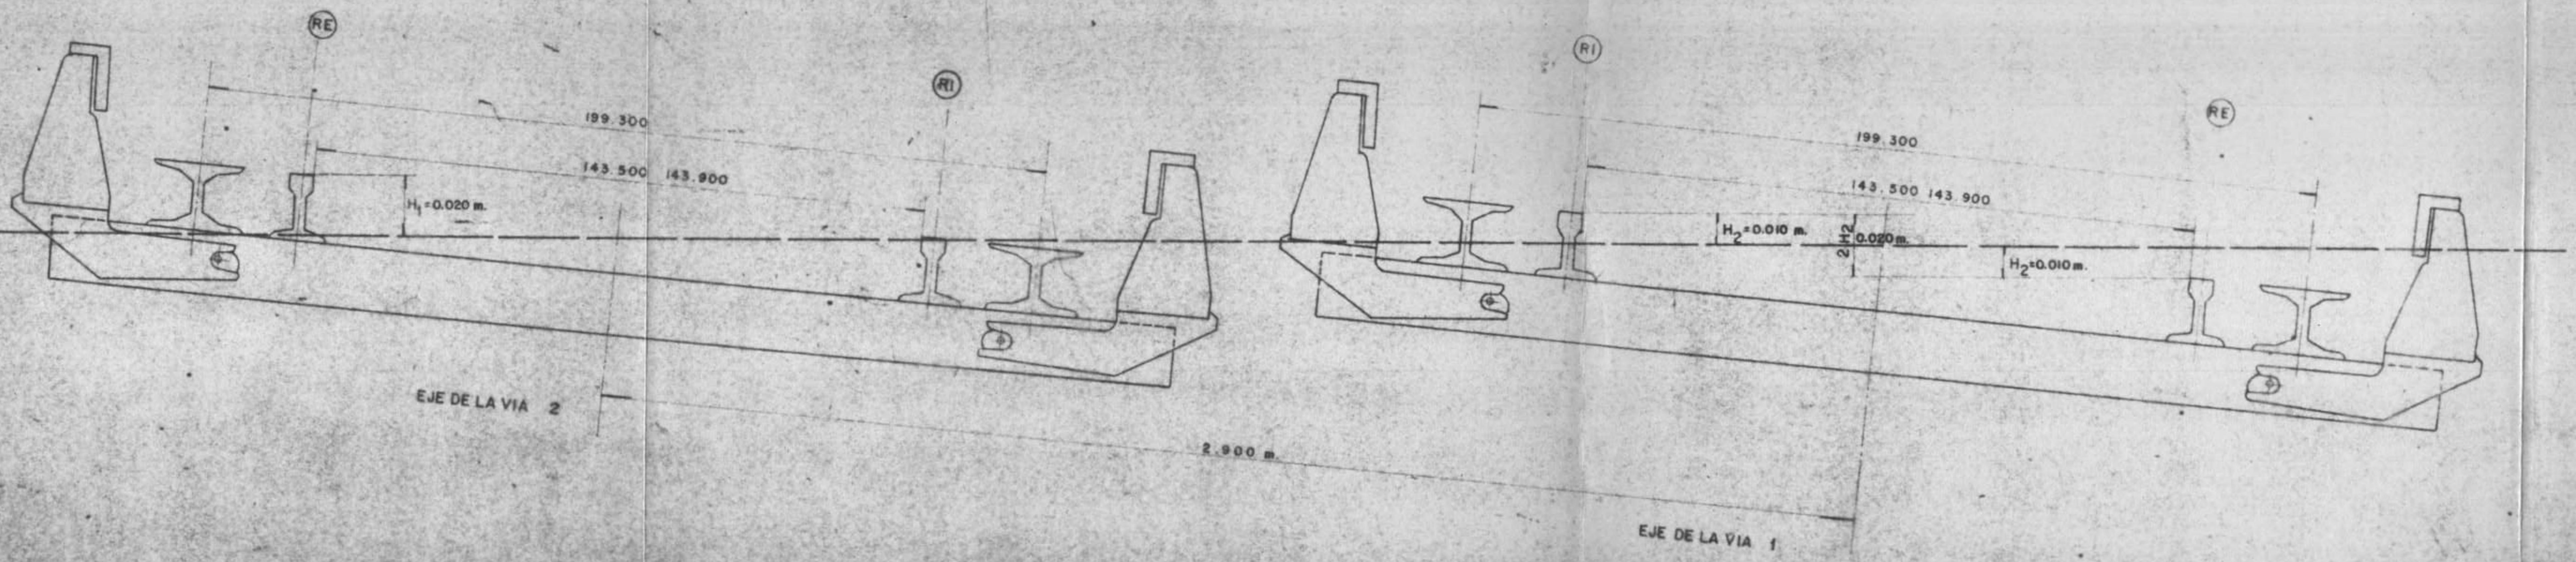

NUM. DE SECCION	DISTANCIA	SOBRE-ELEVACION TOTAL	R E VIA (2).	R I VIA (2).	CADENAMIENTOS		ENTRE-VIA.
1		0.000	0.000	0.000	15+572.202	15+634.008	2.900 m.
	1.665						
2 TE. ET.		0.001	+0.001	0.000	15+573.867	15+632.343	
	1.665						
3		0.002	+0.002	0.000	15+575.532	15+630.678	
	5.841						
4		0.010	+0.010	0.000	15+581.373	15+624.837	
	5.841						
5		0.018	+0.018	0.000	15+587.215	15+618.995	
	1.665						
6 EC. CE.		0.019	+0.019	0.000	15+588.880	15+617.330	
	1.665						
7		0.020	+0.020	0.000	15+590.545	15+615.665	

NUM. DE SECCION	DISTANCIA	SOBRE-ELEVACION TOTAL.	R E VIA (1)	R I VIA (1).	CADENAMIENTOS.		ENTRE-VIA
1		0.000	0.000	0.000	15+573.048	15+633.008	2.900 m.
	0.834						
2 TE. ET.		0.000	−0.000	+0.000	15+573.882	15+632.174	
	0.834						
3		0.002	−0.001	+0.001	15+574.716	15+631.340	
	6.659						
4		0.010	−0.005	+0.005	15+581.375	15+624.681	
	6.659						
5		0.018	−0.009	+0.009	15+588.034	15+618.022	
	0.834						
6 EC. CE.		0.020	−0.010	+0.010	15+588.868	15+617.188	
	0.834						
7		0.020	−0.010	+0.010	15+589.702	15+616.354	

30

FECHA
MODIFICACION
APROBO

STC
SISTEMA DE TRANSPORTE COLECTIVO
METRO
DEPARTAMENTO DEL DISTRITO FEDERAL

LINEA Nº1
TRAMO: TACUBAYA - OBSERVATORIO
SUB-TRAMO: F.F.C.C. CUERNAVACA-OBSERVATORIO.
SOBRE - ELEVACIONES
CURVA Nº 83 Y 84

ESCALA
FECHA FEB./11/71
DIBUJO I.S.T.M.E.
PLANO No. 71-VL-118, III-41SE
VO. BO. PROYECTO
APROBADO
S.O.F.R.E.T.U.

01/021: 118 41

01.021.118-41