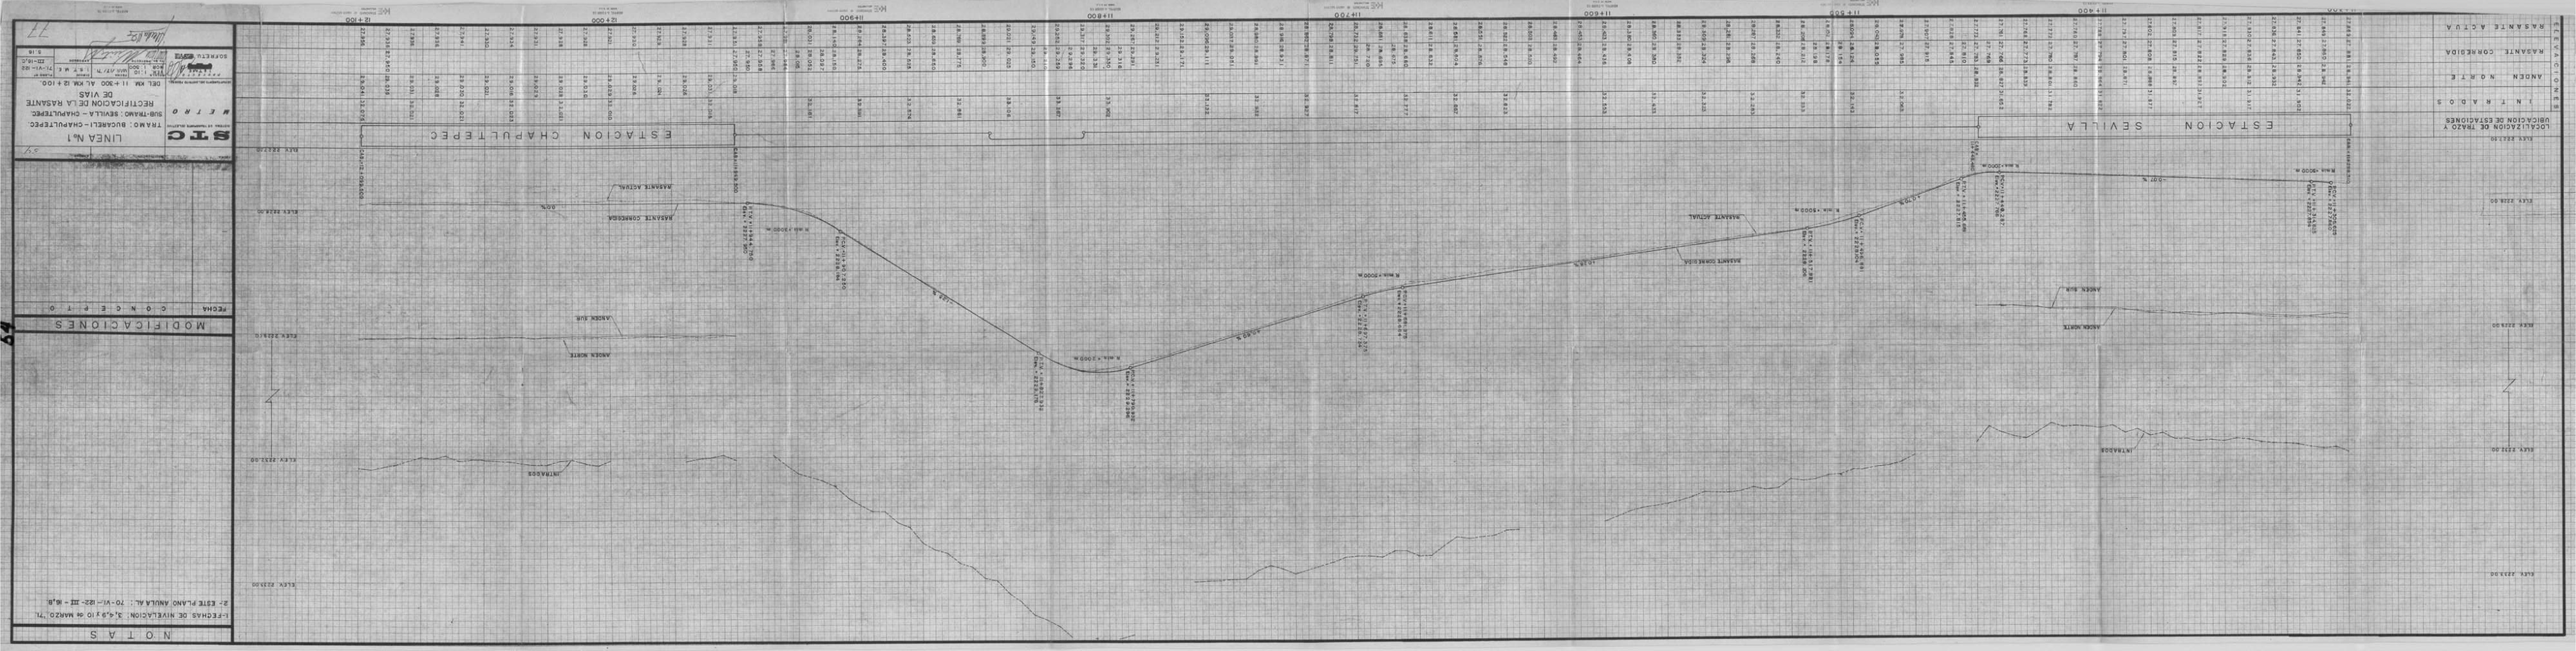

NOTAS
1-FECHAS DE NIVELACION: 3,4,9 Y 10 de MARZO '71
2- EJE PLANO AMULA AL: 70-W-122- III - M.R.
MODIFICACIONES
FECHA C O N C E P T O
STC
LINEA N°1
TRAMO: BUCARELI-CHAPULTEPEC
SUB-TRAMO: SEVILLA - CHAPULTEPEC
RECTIFICACION DELA RASANTE
DE VIAS
METRO
DEL KM 11+700 AL KM 12+100
SOMETIDA POR
ESTACION CHAPULTEPEC
ESTACION SEVILLA
LOCALIZACION DE TRAZO Y
UBICACION DE ESTACIONES
INTERADOS
ANDEN NORTE
MASANTE CONTRABOVEDA
RASANTE ACTUAL
ANDEN NORTE
ANDEN SUR
MASANTE ACTUAL
MASANTE CONTRABOVEDA
ANDEN SUR
ANDEN NORTE
INTRADOS
INTRADOS