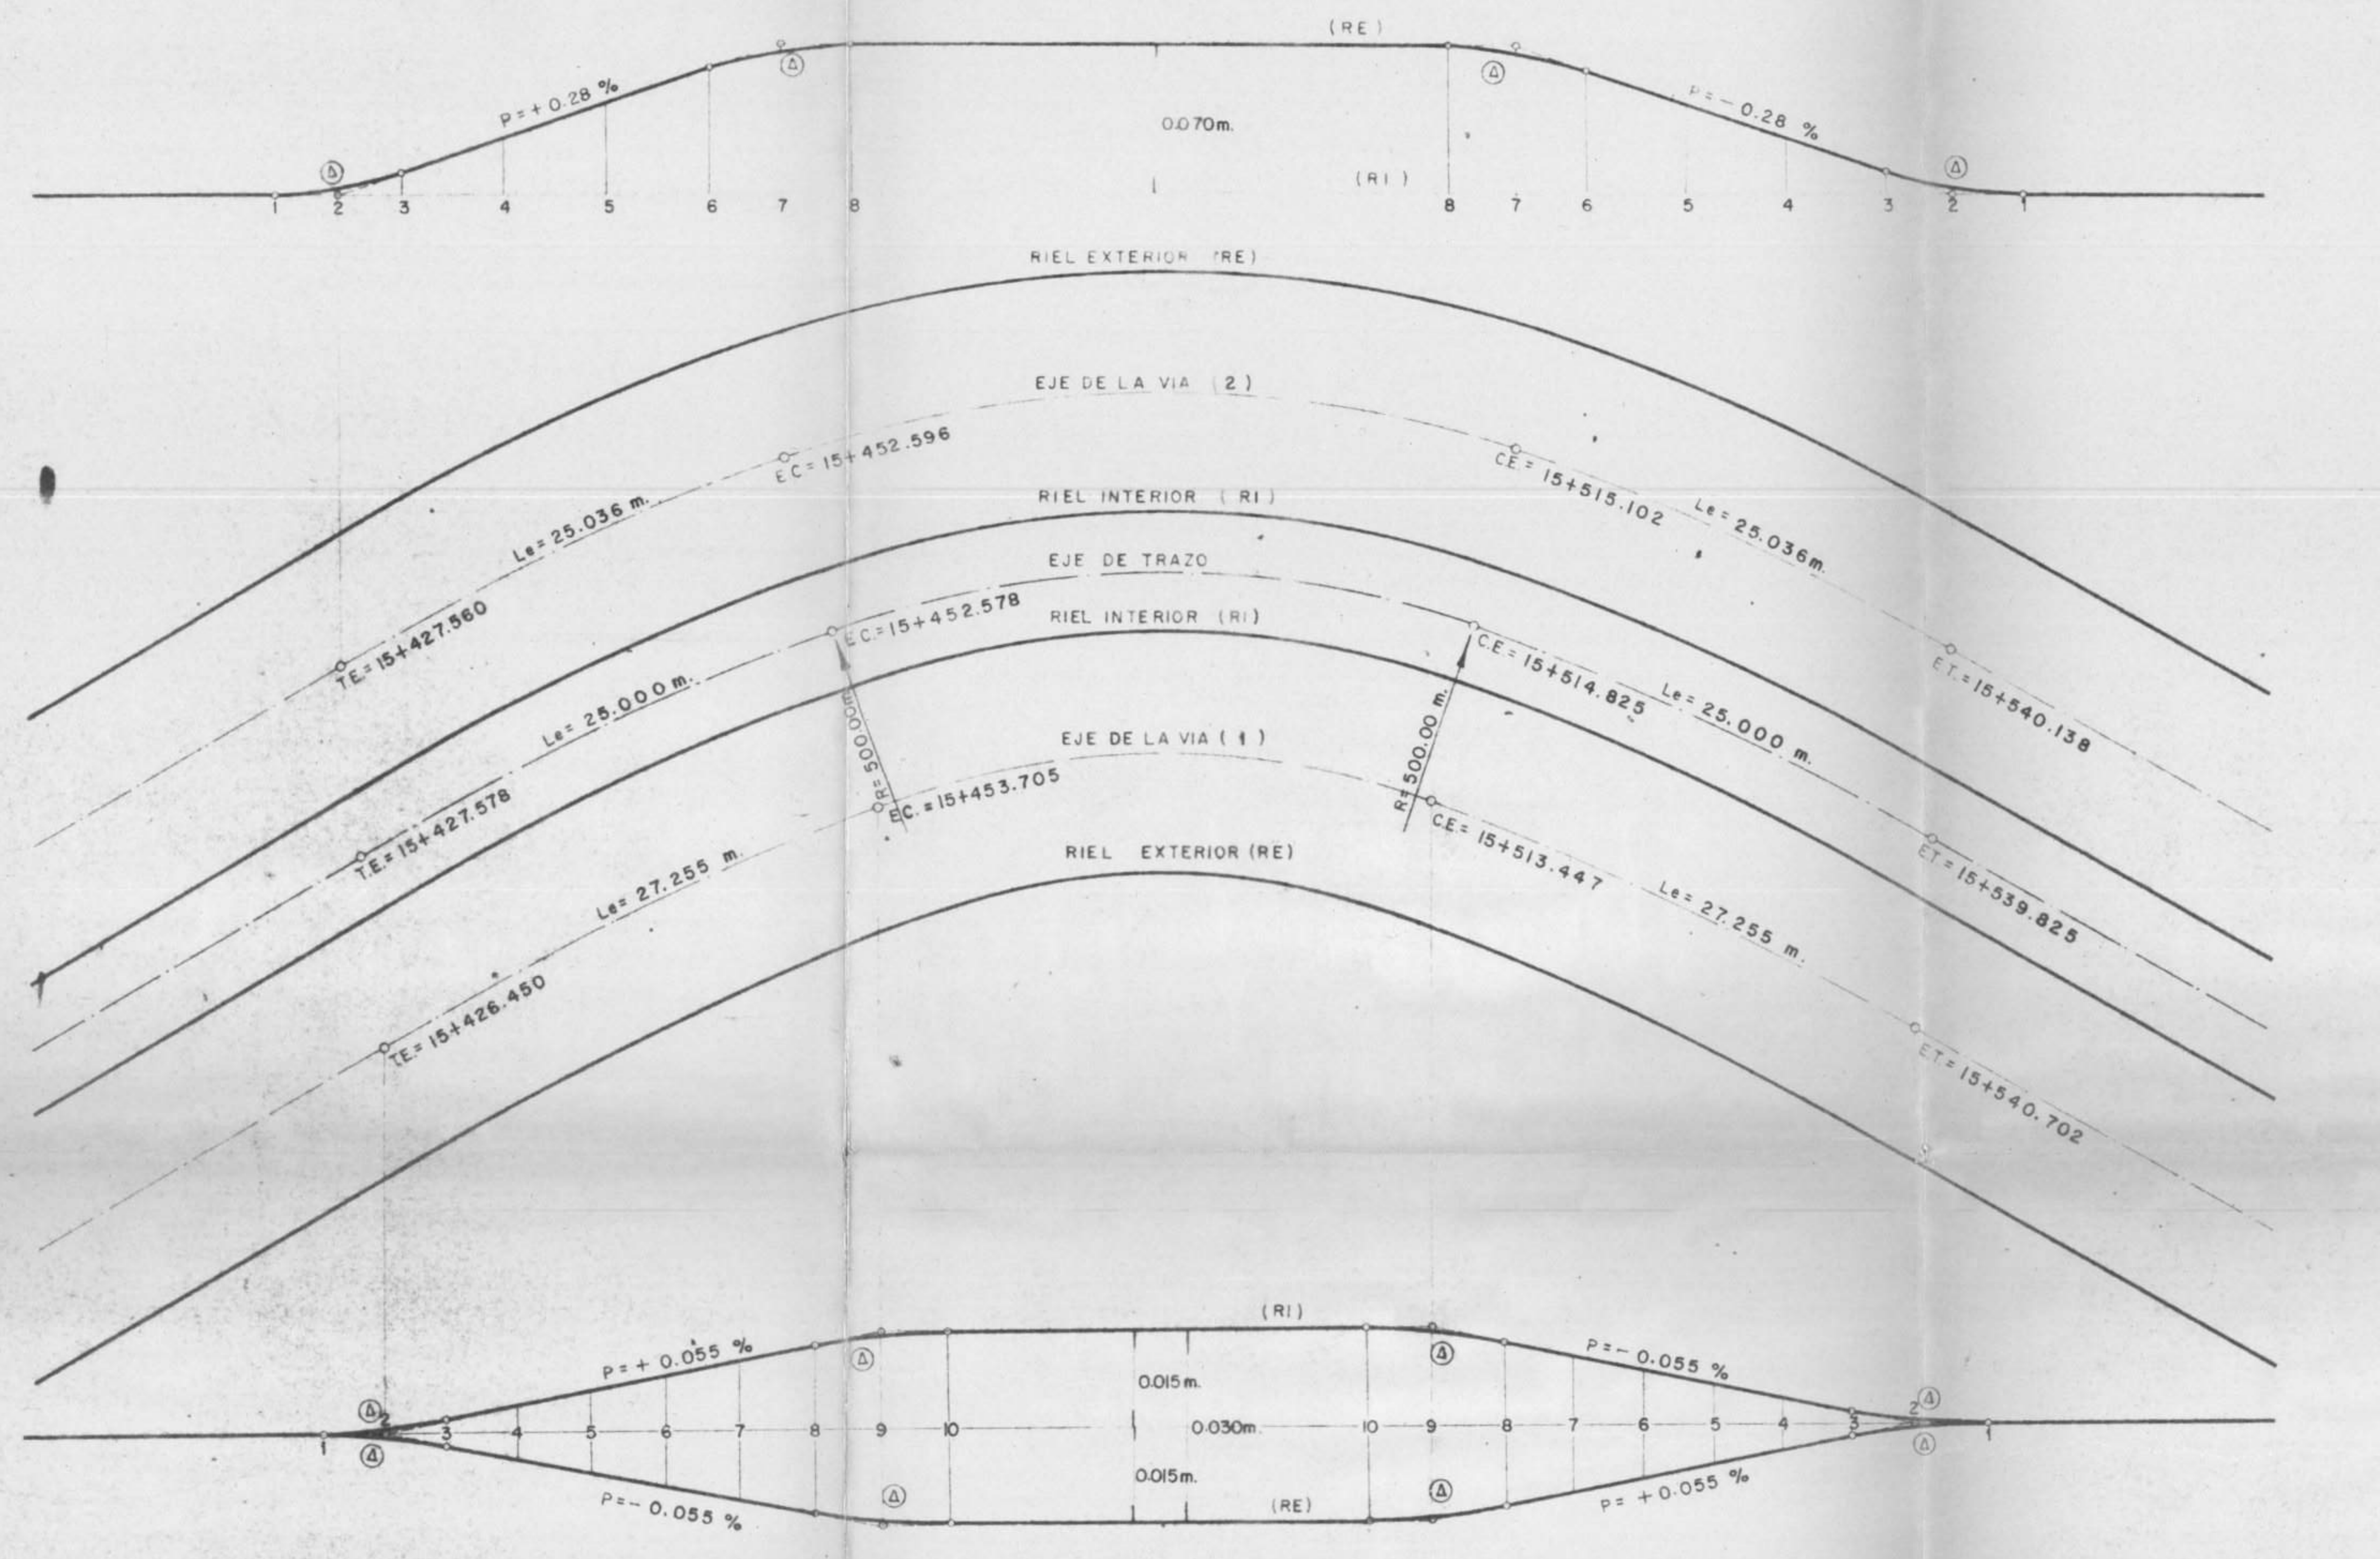

Ⓐ TRANSICION VERTICAL

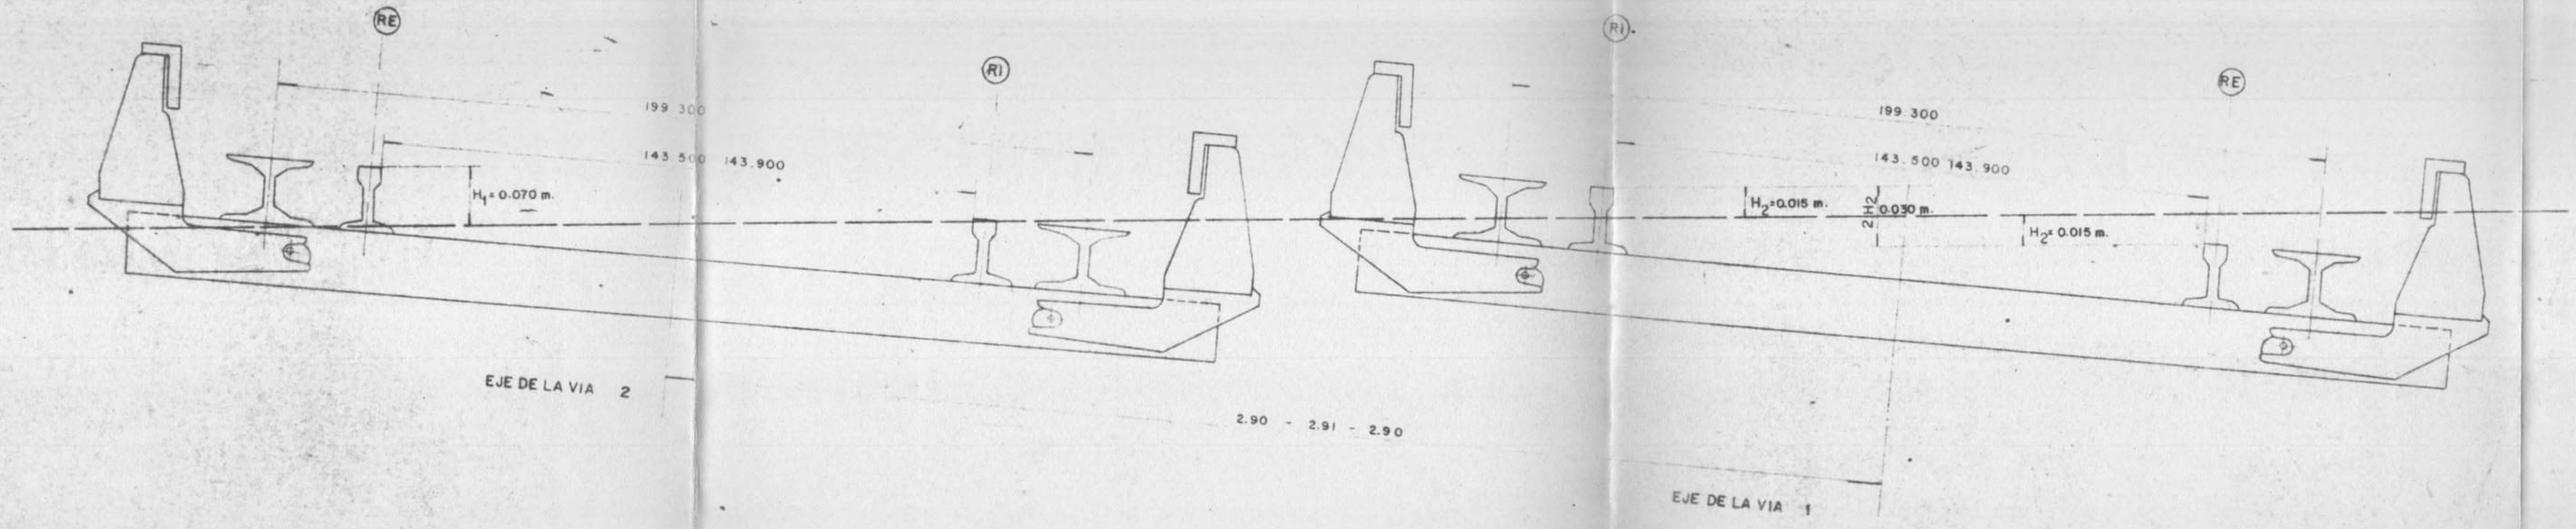

NUM. DE SECCION	DISTANCIA	SOBRE-ELEVACION TOTAL	R E VIA (2).	R I VIA (2)	CADENAMIENTOS		ENTRE-VIA.
1		0.000	0.000	0.000	15+424.065	15+543.633	2.90 - 2.91 - 2.90
	3.495						
2 TE. ET.		0.002	+0.002	0.000	15+427.560	15+540.138	
	3.495						
3		0.010	+0.010	0.000	15+431.055	15+536.643	
	6.015						
4		0.027	+0.027	0.000	15+437.070	15+530.627	
	6.015						
5		0.044	+0.044	0.000	15+443.085	15+524.612	
	6.015						
6		0.060	+0.060	0.000	15+449.101	15+518.597	
	3.495						
7 EC. CE.		0.068	+0.068	0.000	15+452.596	15+515.102	
	3.495						
8		0.070	+0.070	0.000	15+456.091	15+511.607	

NUM. DE SECCION	DISTANCIA	SOBRE-ELEVACION TOTAL	R E VIA (1)	R I VIA (1).	CADENAMIENTOS.		ENTRE-VIA
1		0.000	0.000	0.000	15+425.763	15+541.389	2.90 - 2.91 - 2.90
	0.687						
2 TE. ET.		0.000	-0.000	+0.000	15+426.450	15+540.702	
	0.687						
3		0.000	-0.000	+0.000	15+427.137	15+540.015	
	5.176						
4		0.006	-0.003	+0.003	15+432.313	15+534.838	
	5.176						
5		0.012	-0.006	+0.006	15+437.489	15+529.662	
	5.176						
6		0.018	-0.009	+0.009	15+442.665	15+524.486	
	5.176						
7		0.024	-0.012	+0.012	15+447.841	15+519.310	
	5.176						
8		0.030	-0.015	+0.015	15+453.018	15+514.134	
	0.687						
9 EC. CE.		0.030	-0.015	+0.015	15+453.705	15+513.447	
	0.687						
10		0.030	-0.015	+0.015	15+454.392	15+512.760	

29

FECHA	MODIFICACION	APROBO

STC
SISTEMA DE TRANSPORTE COLECTIVO
M E T R O
DEPARTAMENTO DEL DISTRITO FEDERAL
SOFRETU

LINEA Nº1
TRAMO: TACUBAYA - OBSERVATORIO
SUB-TRAMO: FC. CUERNAVACA-OBSERVATORIO

SOBRE - ELEVACIONES

CURVA Nº 81 Y 82

ESCALA	FECHA	DIBUJO	PLANO No.
	FEB-12-71	I.S.T.M.E.	71-VI-48 III-40SE
Vo. Bo. PROYECTO		APROBADO	

01.021:118-40

01.021:118-40