
Interstation: SALTO DEL AGUA
BALDÉRAS

MÉTRO DE MEXICO

LIGNE N° 1

DEVERS

COURBE N° 38

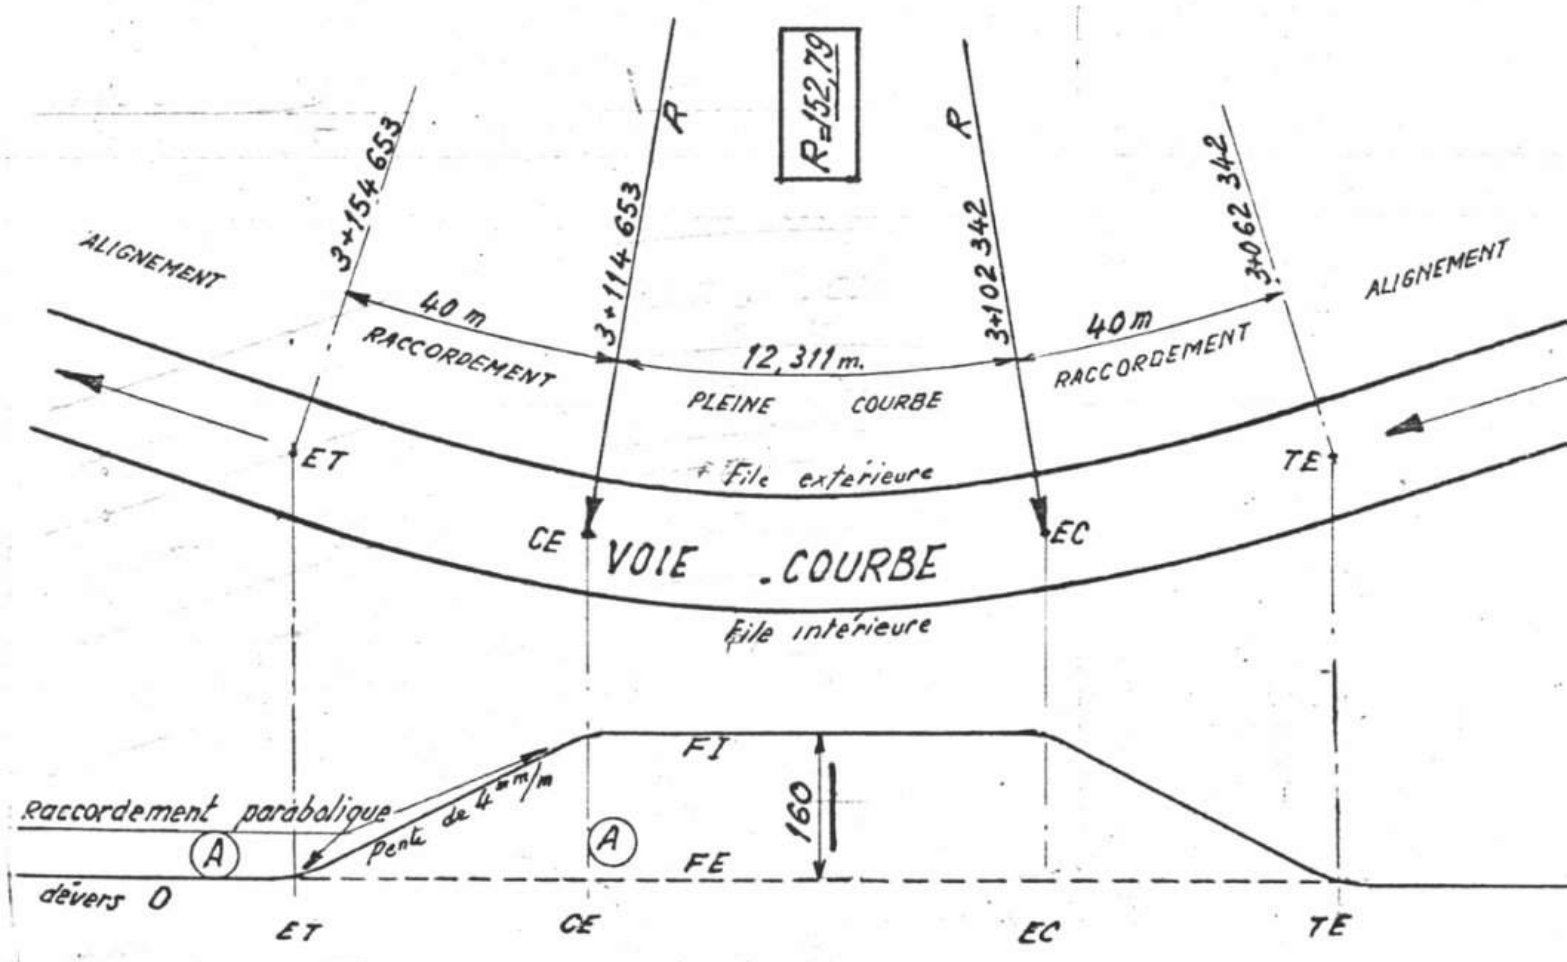

CÔTÉ . GRAND RAYON

COURBE

(A) Raccordement parabolique de la forme $y = 0,0002\,x^2$

Paris le 16 Juillet 1968

TV 442