Interstation : CHAPULTEPEC
JUANACATLAN

S.T.C.
Departamento de Vias
y Estructuras
Seccion de Mantenimiento
de Vias


MÉTRO DE MEXICO

TV-474

LIGNE N° 1

DEVERS

COURBES N° 53 et N° 54

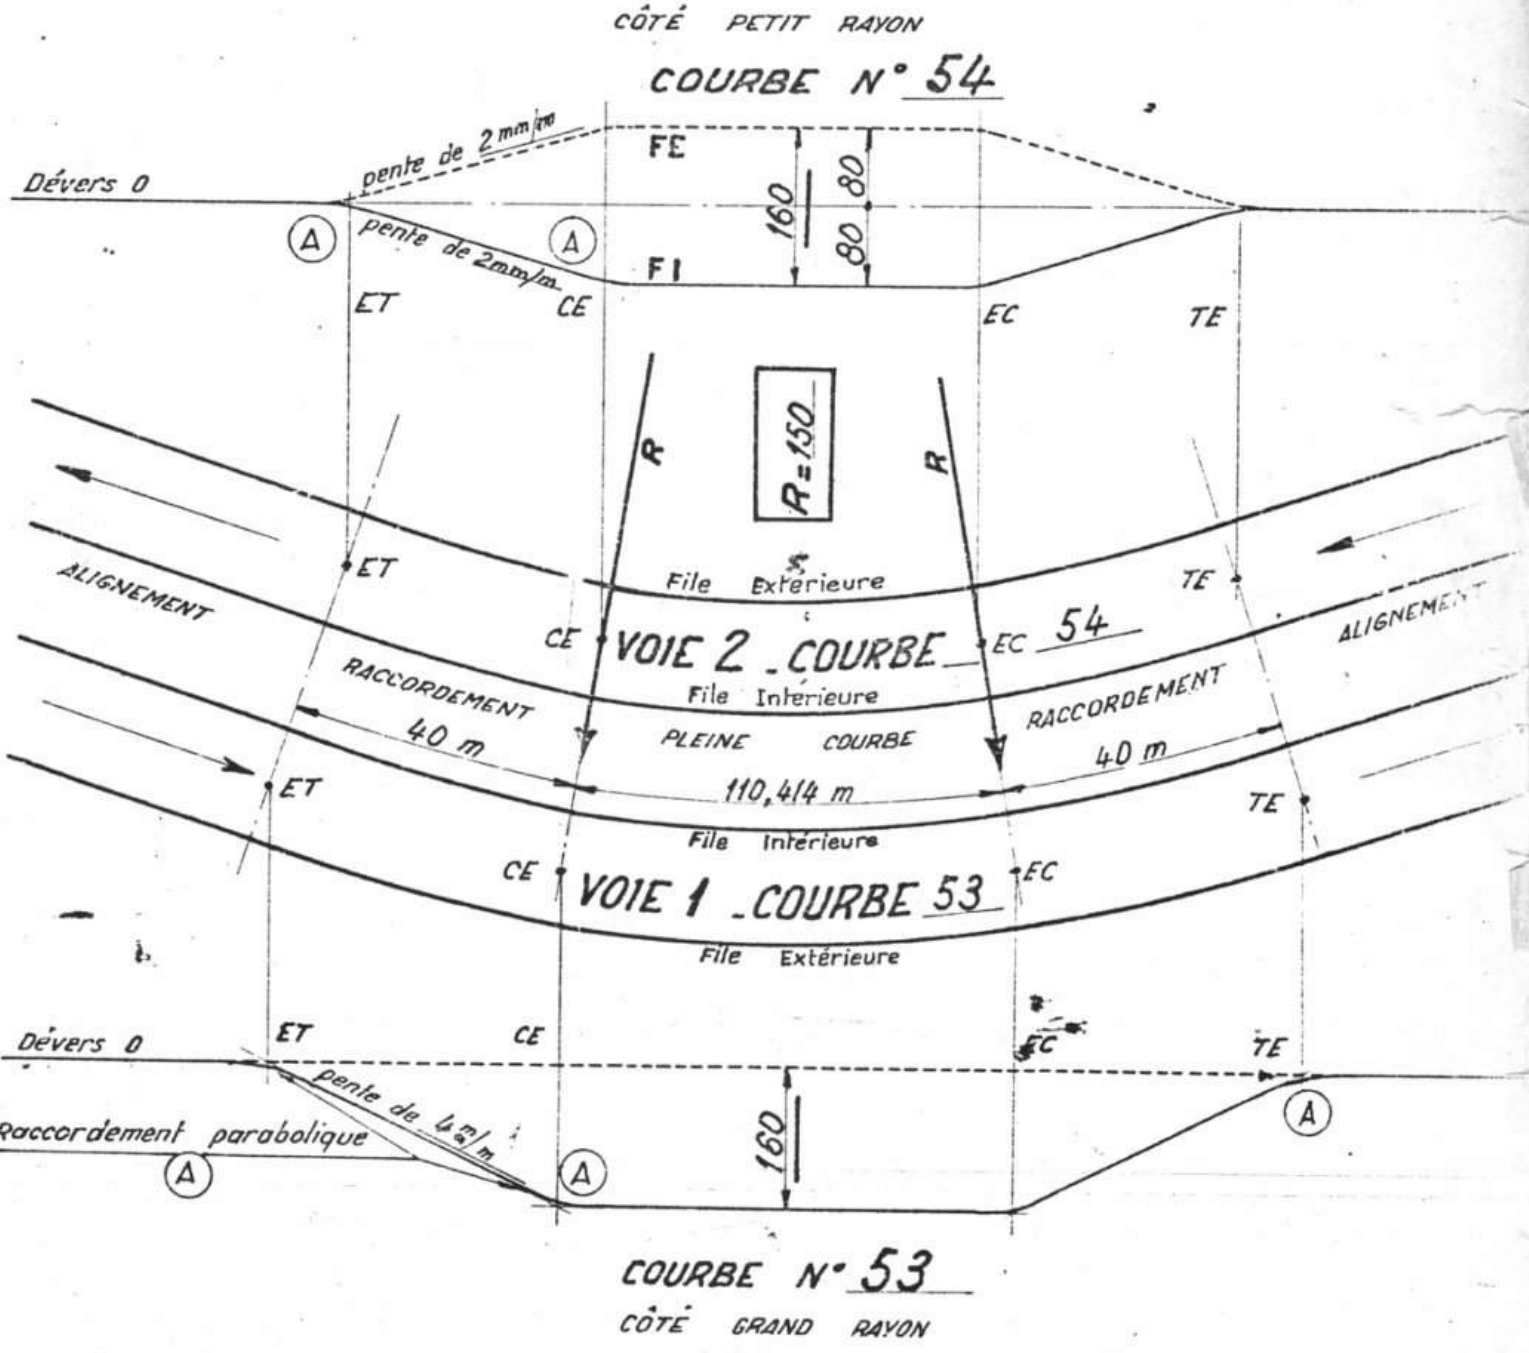

TV 474

(A) Raccordement parabolique de la forme $y = 0{,}0002\,x^2$