MÉTRO DE MEXICO

Interstation SAN LAZARO
LA CANDELARIA


TV-425

7

LIGNE N° 1

DEVERS

COURBES N° 11 et N° 12

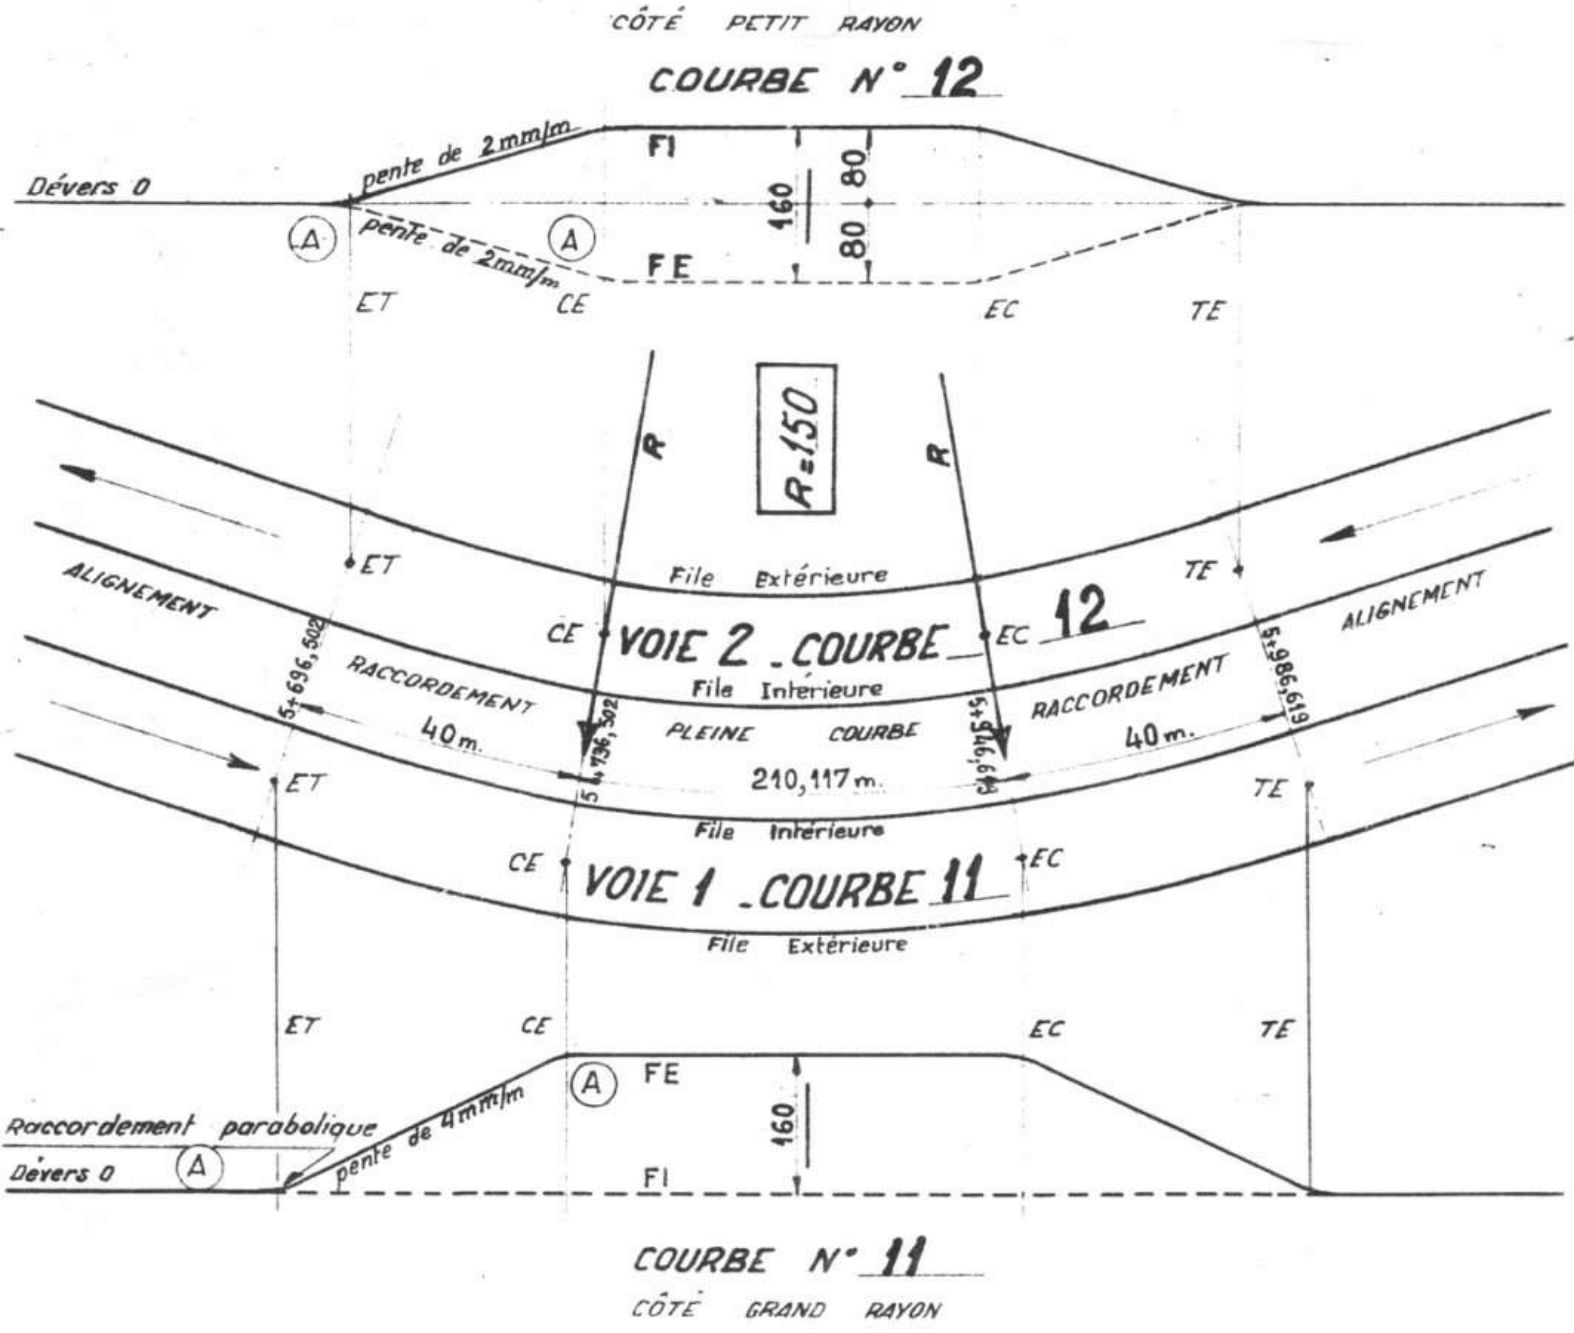

Paris le 16 Juillet 1968

TV 425

(A) Raccordement parabolique de la forme $y = 0,0002\,x^2$