Interstation
INSURGENTES
SEVILLA

MÉTRO DE MEXICO

30


LIGNE N° 1

DEVERS

COURBES N°49 et N°50

CÔTÉ GRAND RAYON

COURBE N° 50

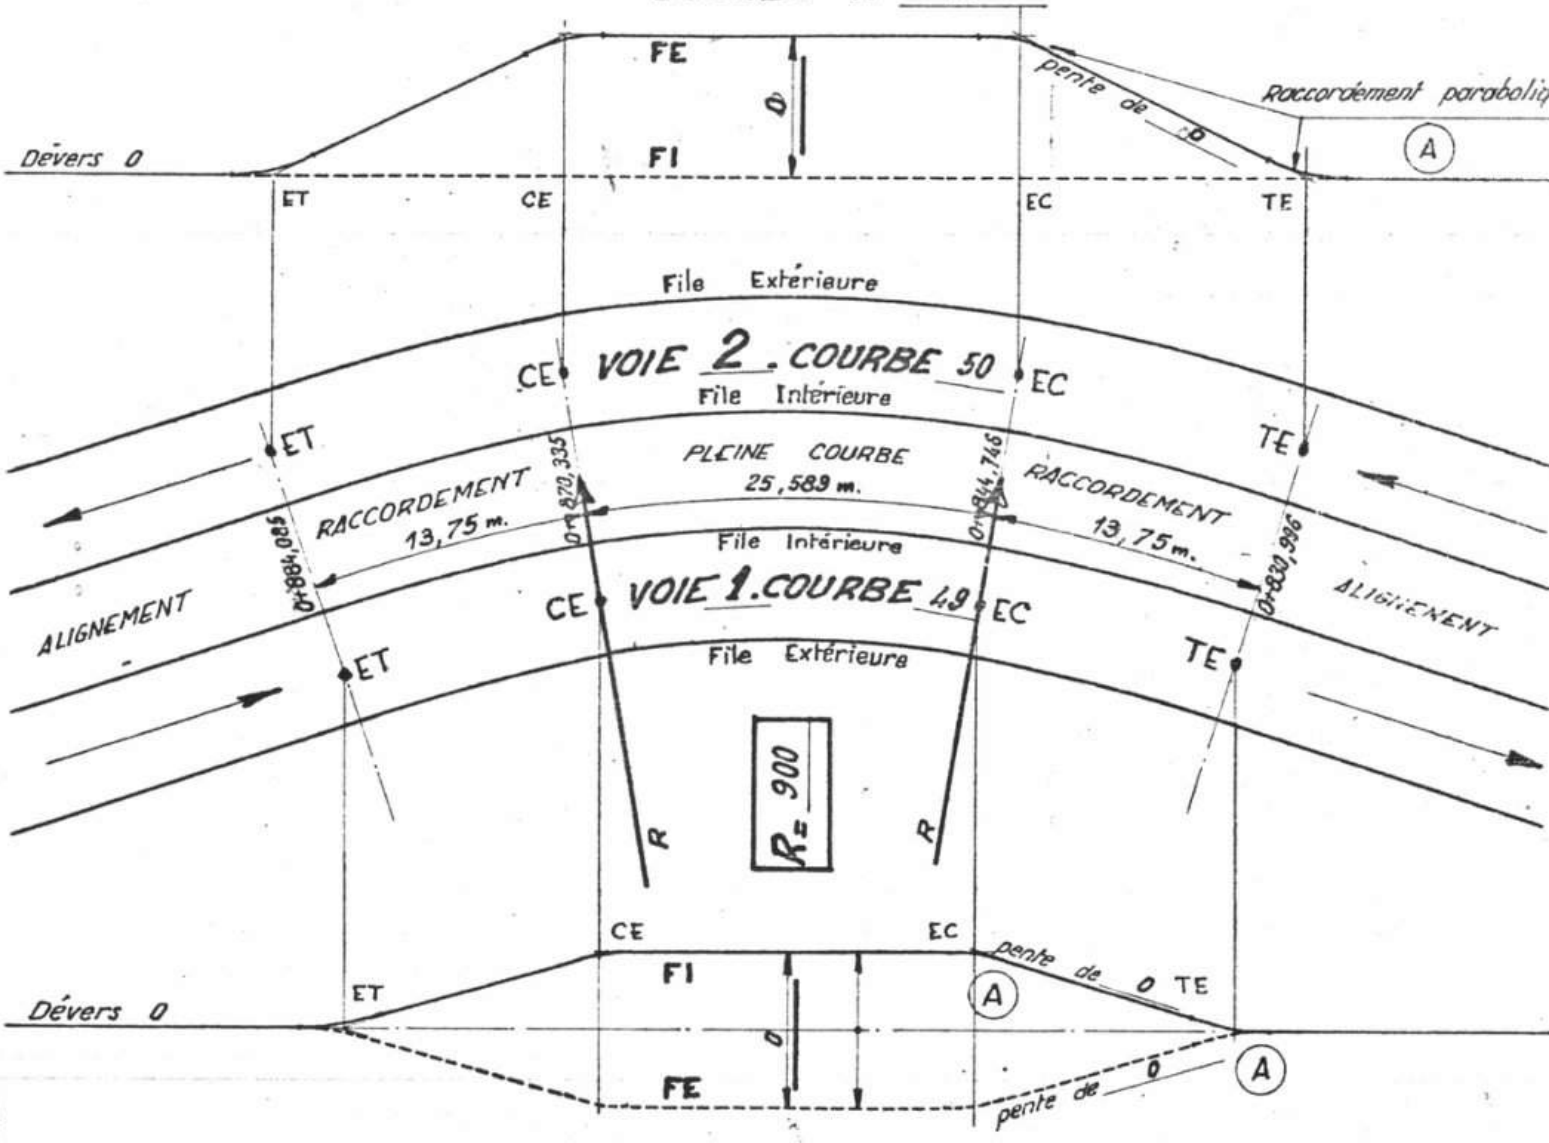

COURBE N° 49

CÔTÉ PETIT RAYON

Paris le 16 Juillet 1968

TV 448

(A) Raccordement parabolique de la forme $y = 0,0002x^2$