Interstation: SEVILLA
CHAPULTEPEC

MÉTRO DE MEXICO

31


LIGNE N° 1

DEVERS

COURBES N° 51 et N° 52

CÔTÉ GRAND RAYON

COURBE N° 52

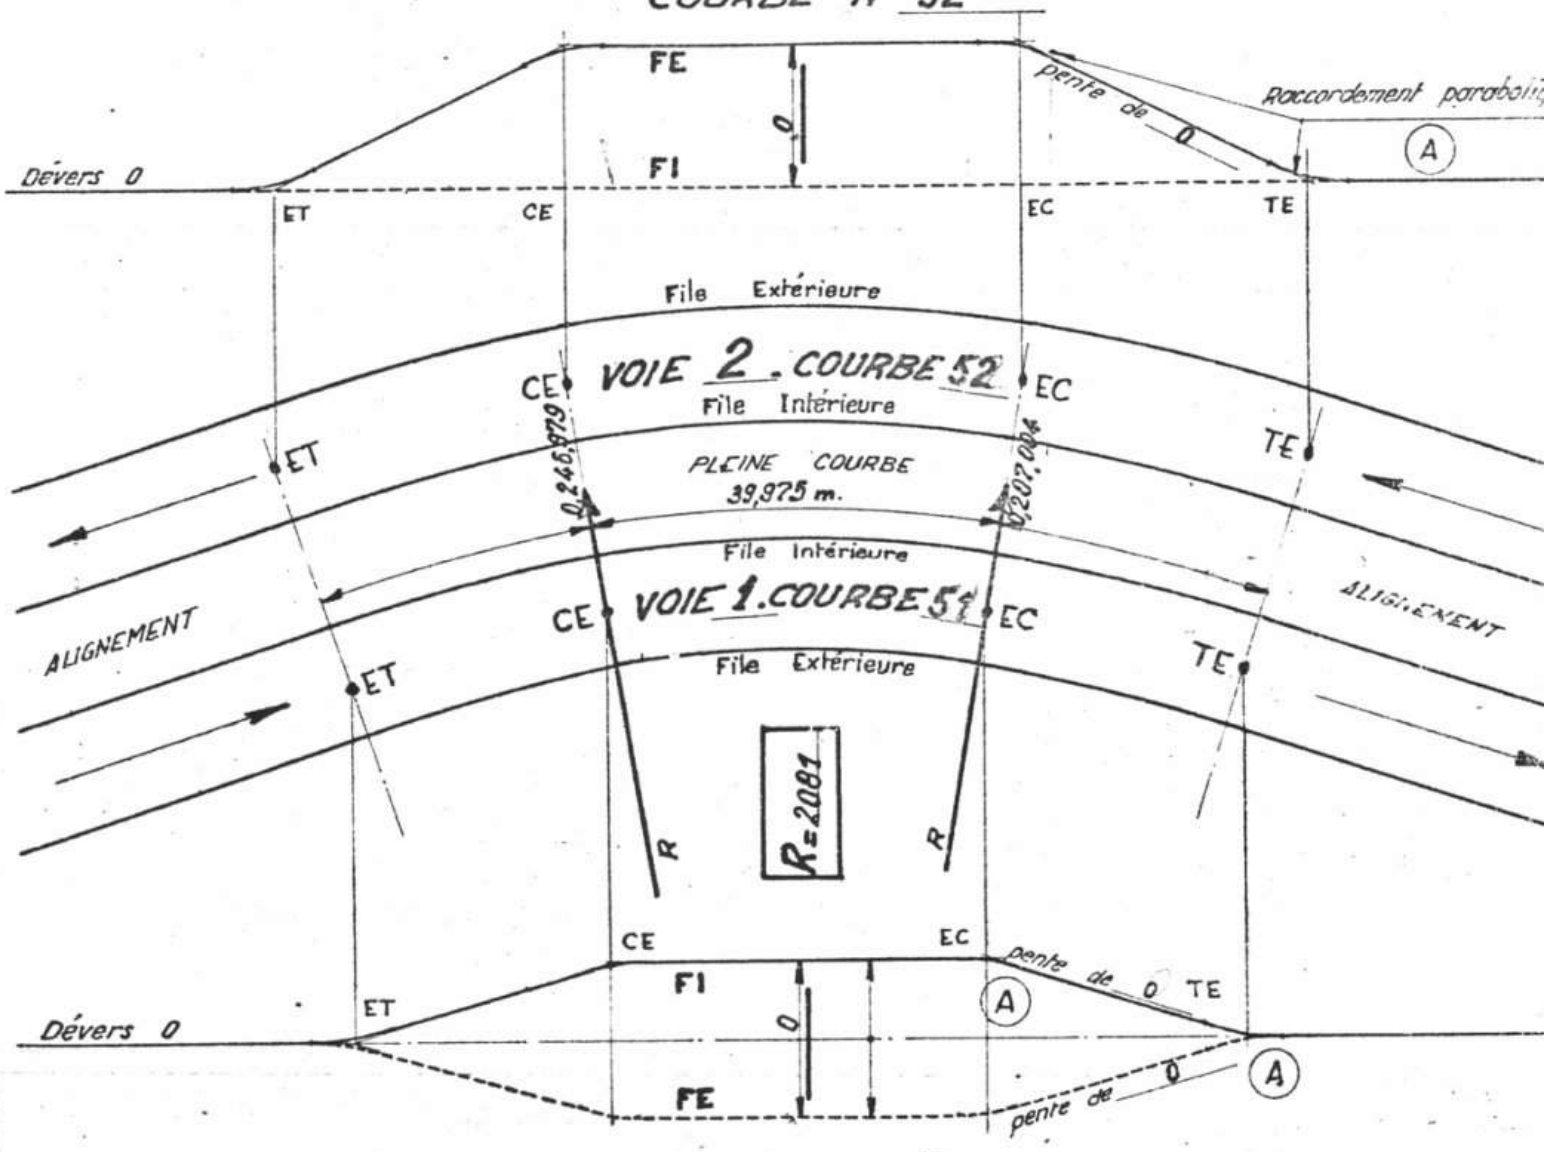

COURBE N° 51

CÔTÉ PETIT RAYON

Paris le 16 Juillet 1968

TV 449

(A) Raccordement parabolique de la forme $y = 0,0002x^2$