Interstation CHAPULTEPEC
JUANACATLAN


S.T.C.
Departamento de Vias
y Estructuras
Seccion de Mantenimiento
de Vias

MÉTRO DE MEXICO TV-475

LIGNE N° 1

DEVERS

COURBES N°55 et N°56

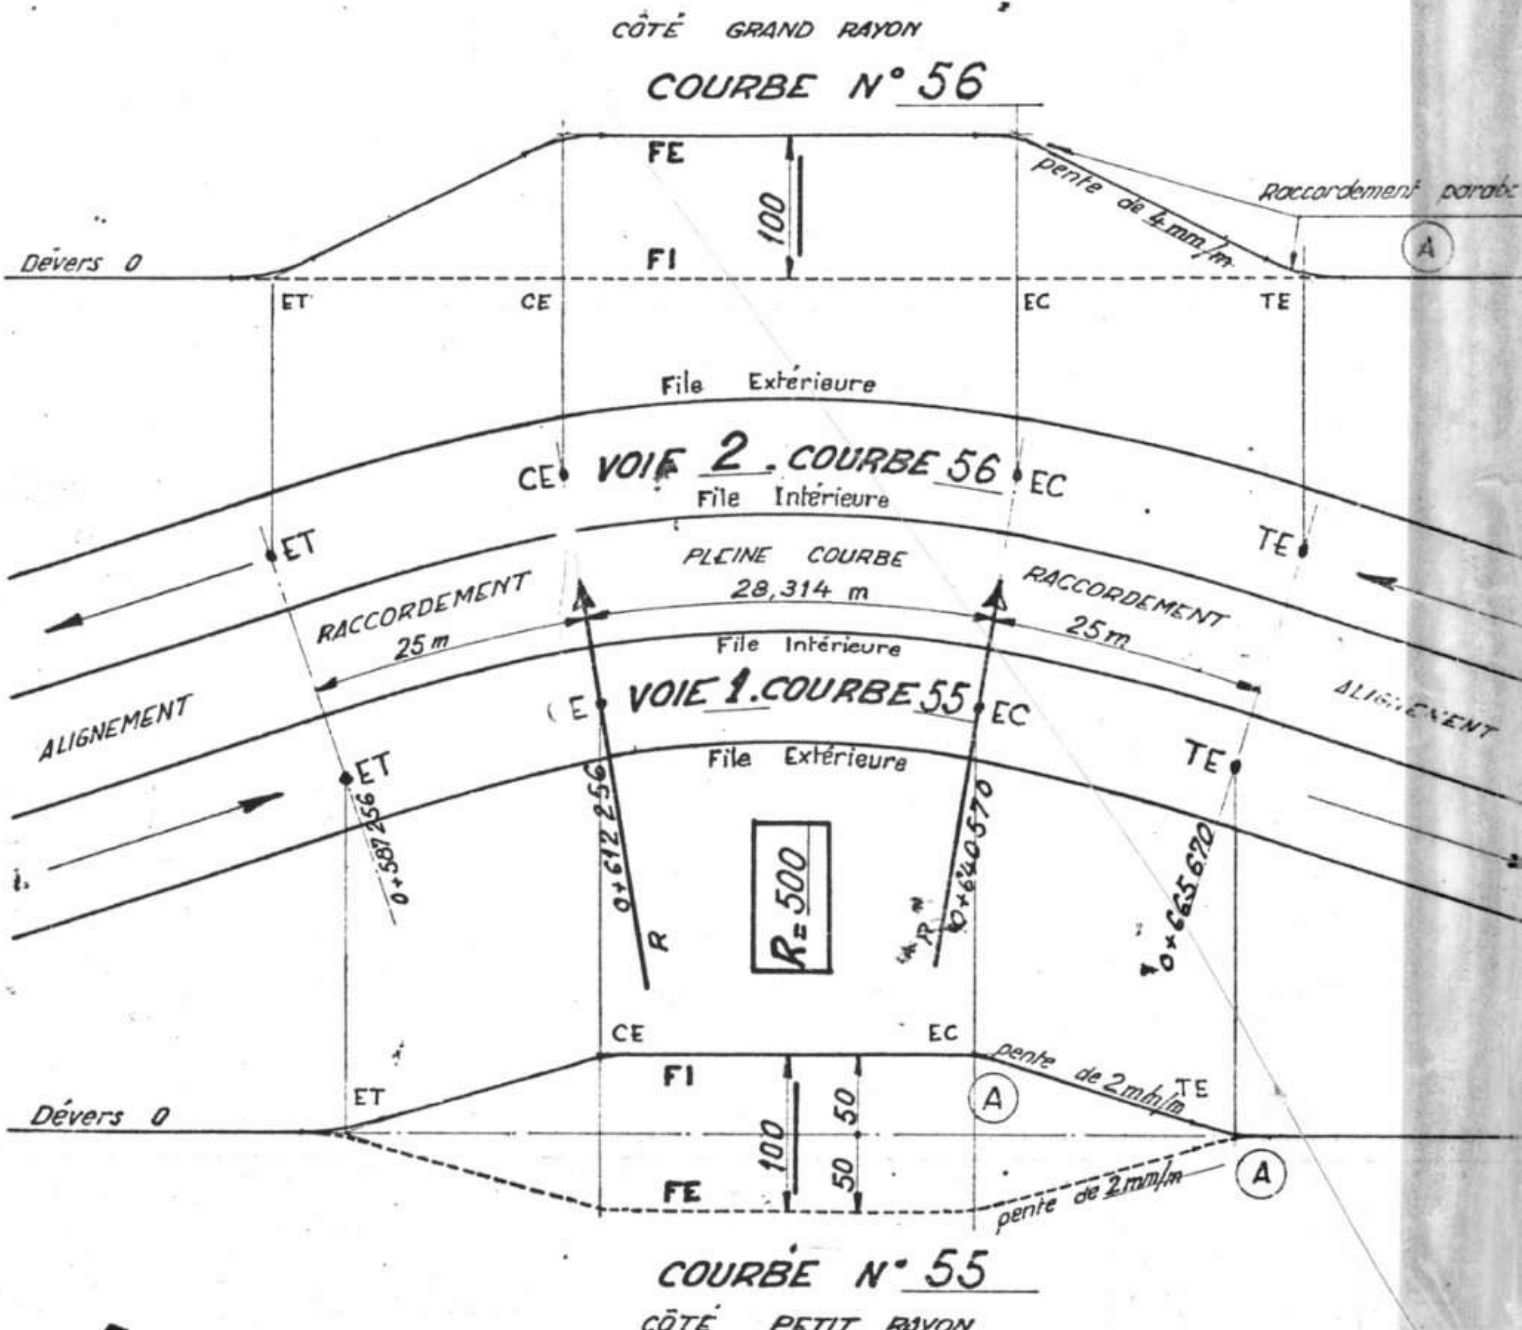

TV 475

(A) Raccordement parabolique de la forme $y = 0,0002x^2$