Interstation : CHAPULTEPEC
JUANACATLAN

MÉTRO DE MEXICO

TV-476

S.T.C.

Departamento de Vias y Estructuras
Seccion de Mantenimiento de Vias


LIGNE N° 1

DEVERS

COURBES N° 57 et N° 58

CÔTÉ PETIT RAYON

COURBE N° 58

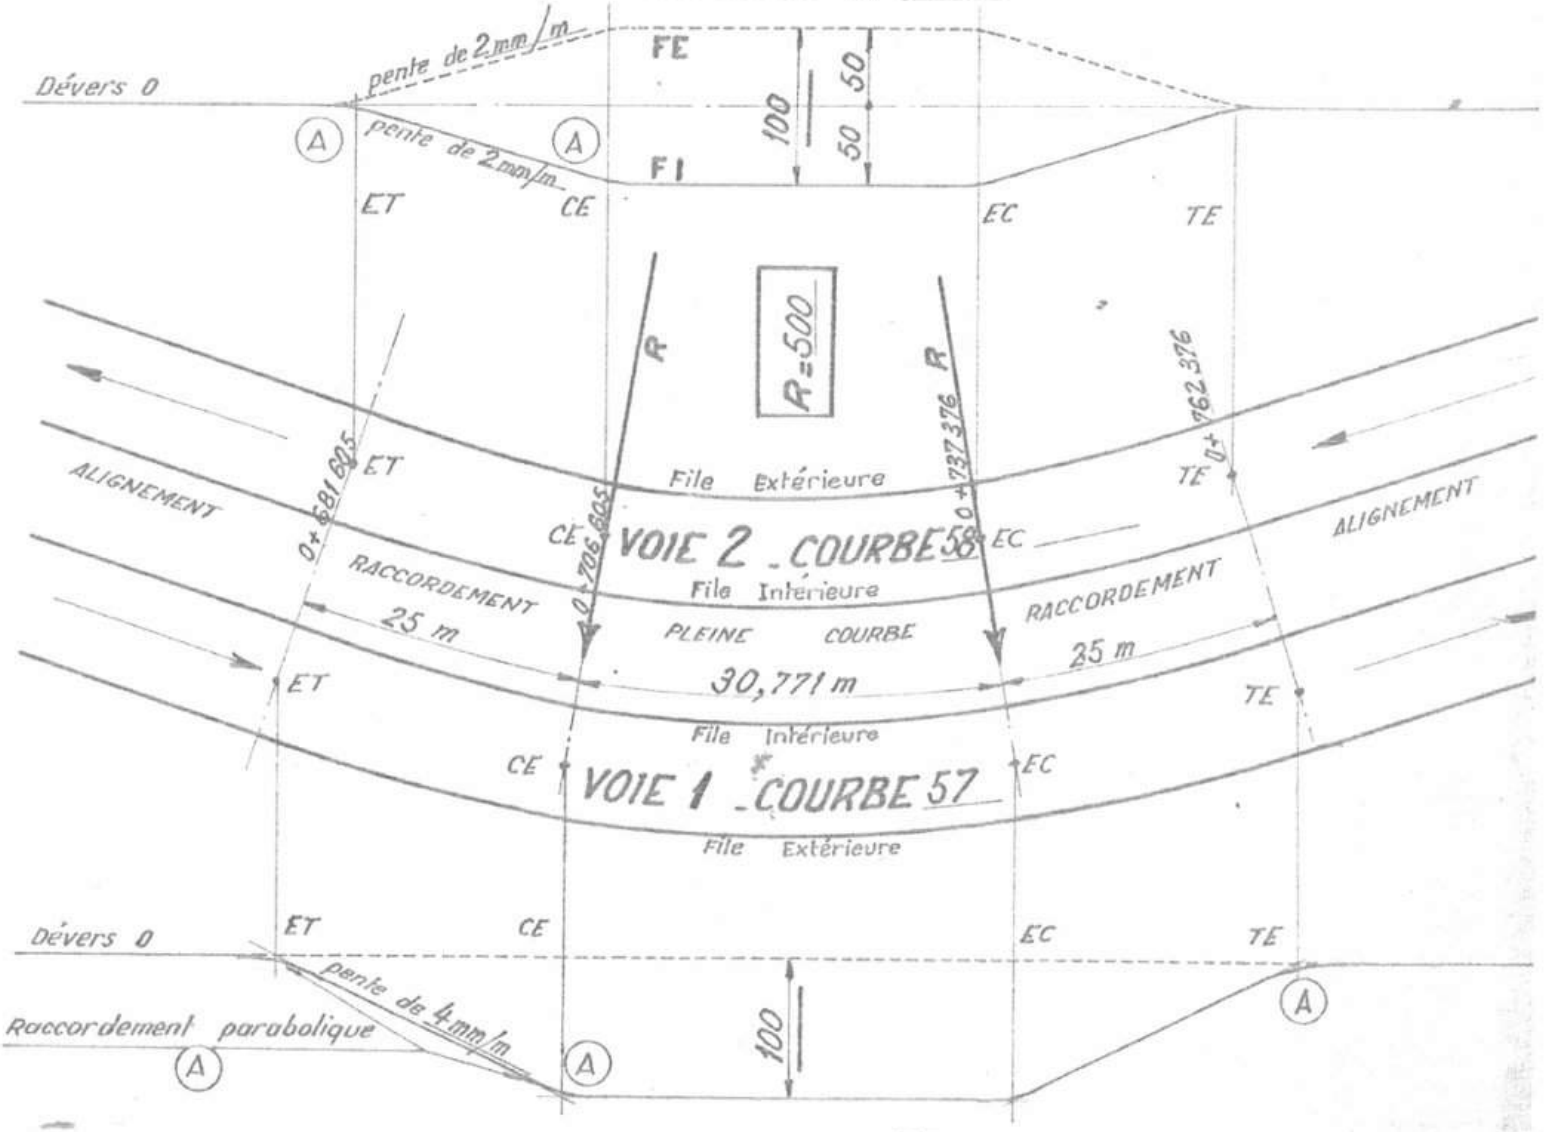

COURBE N° 57

CÔTÉ GRAND RAYON

TV 476