Interstation

SAN LAZARO
LA CANDELARIA

MÉTRO DE MEXICO

TV-424


6

LIGNE N° 1

DEVERS

COURBES N° 9 et N° 10

CÔTÉ PETIT RAYON

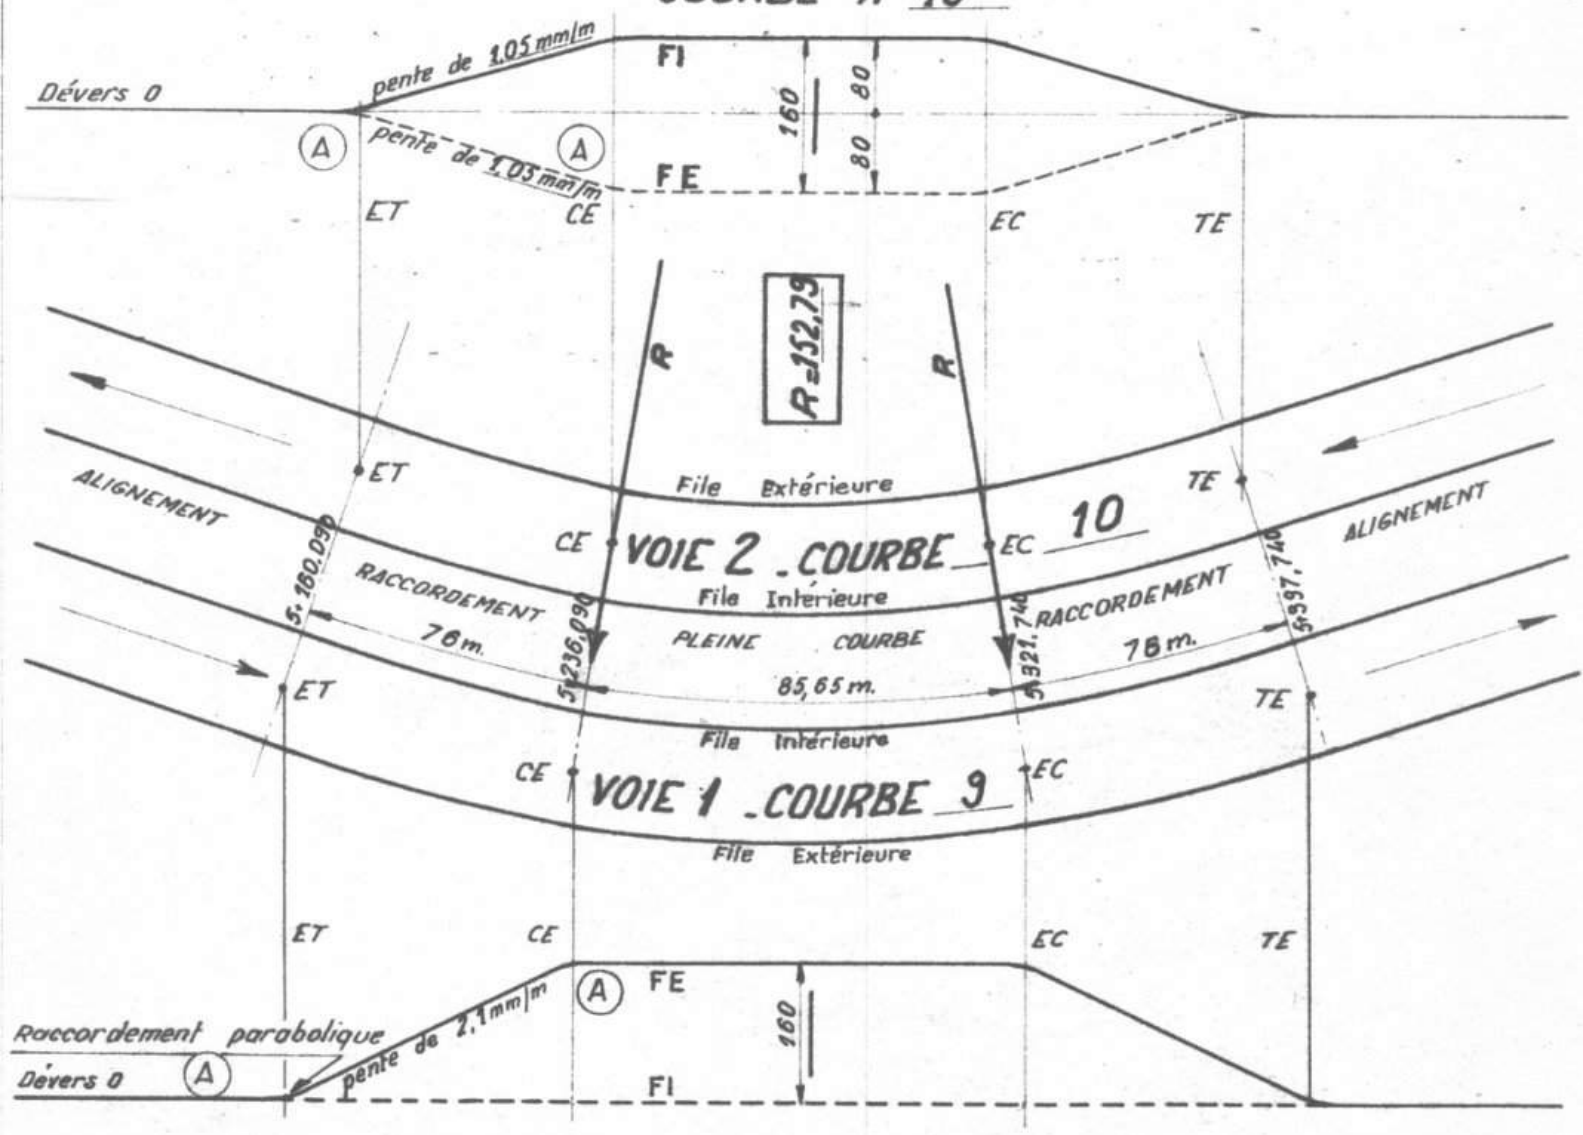

CÔTÉ GRAND RAYON

Paris le 16 Juillet 1968

TV 424

(A) Raccordement parabolique de la forme $y = 0,0002\ x^2$