

- Coupe AA -

Echelle ½

Coupe au droit d'une attache de piste

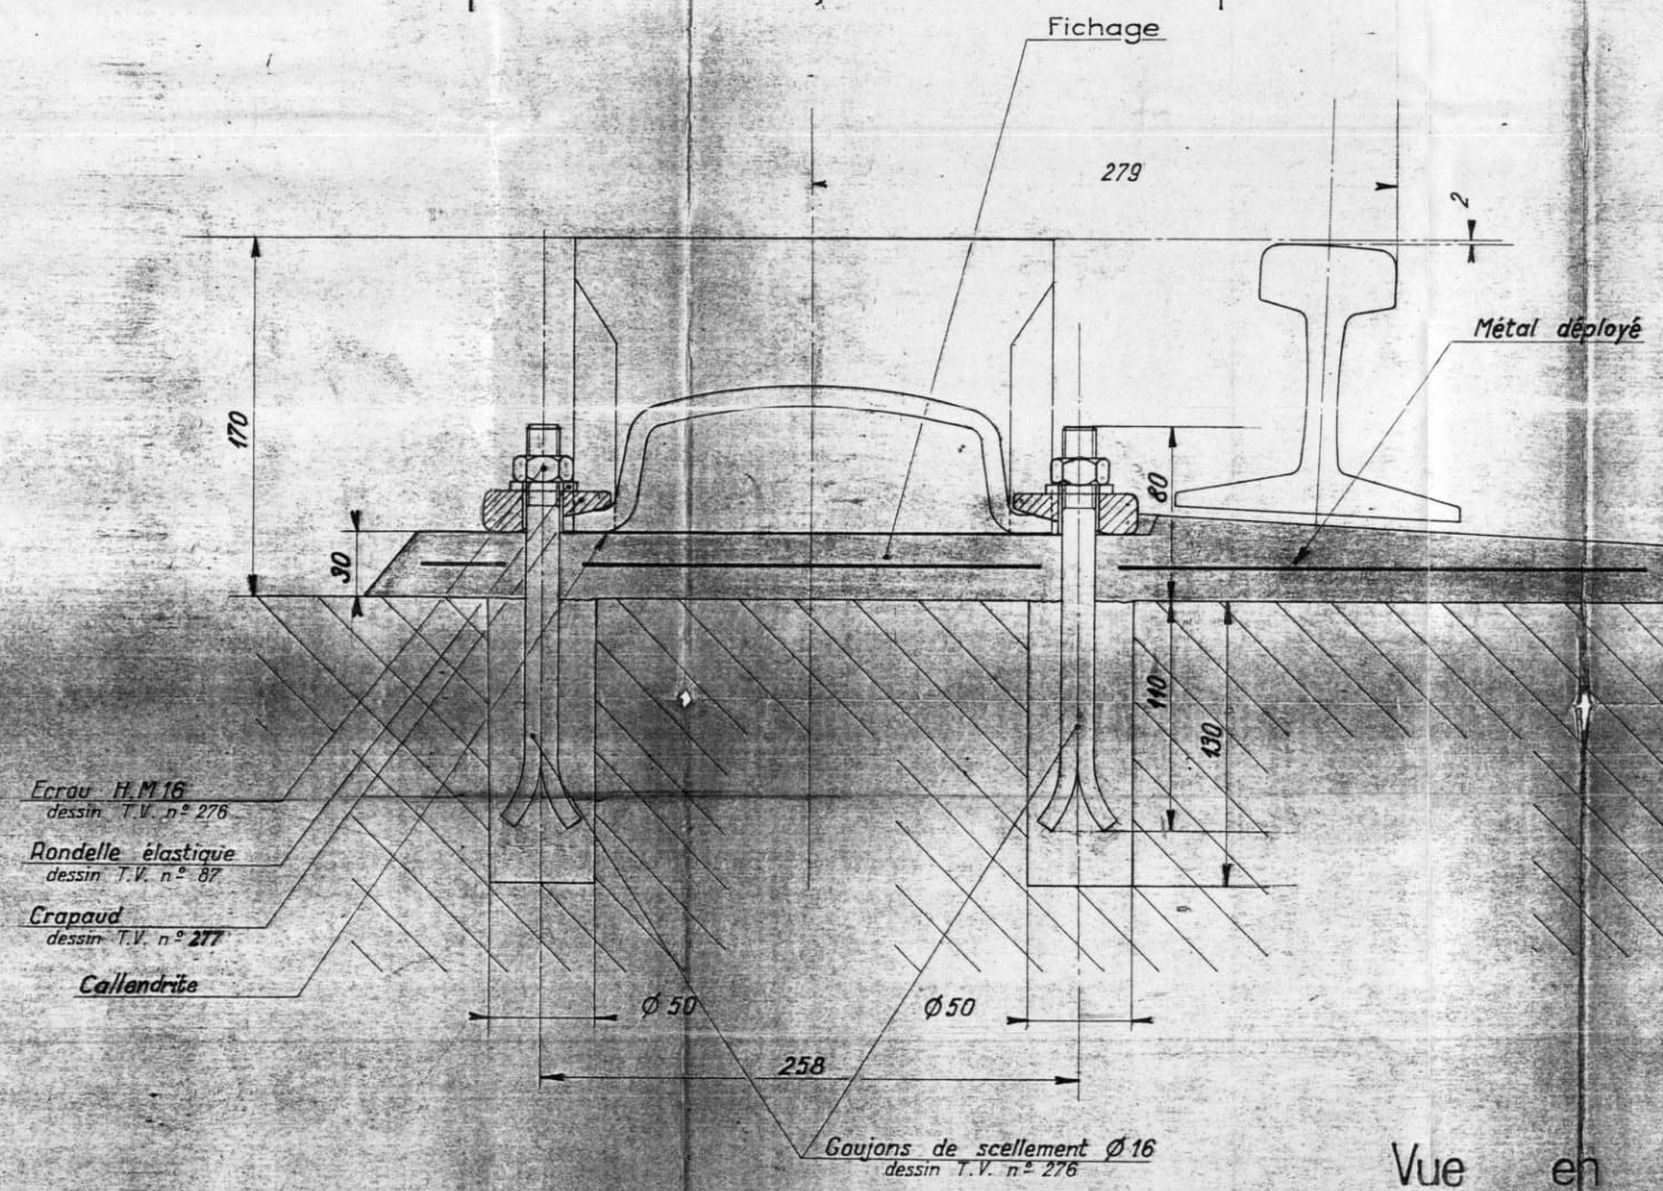


Coupe au droit d'une attache de rail

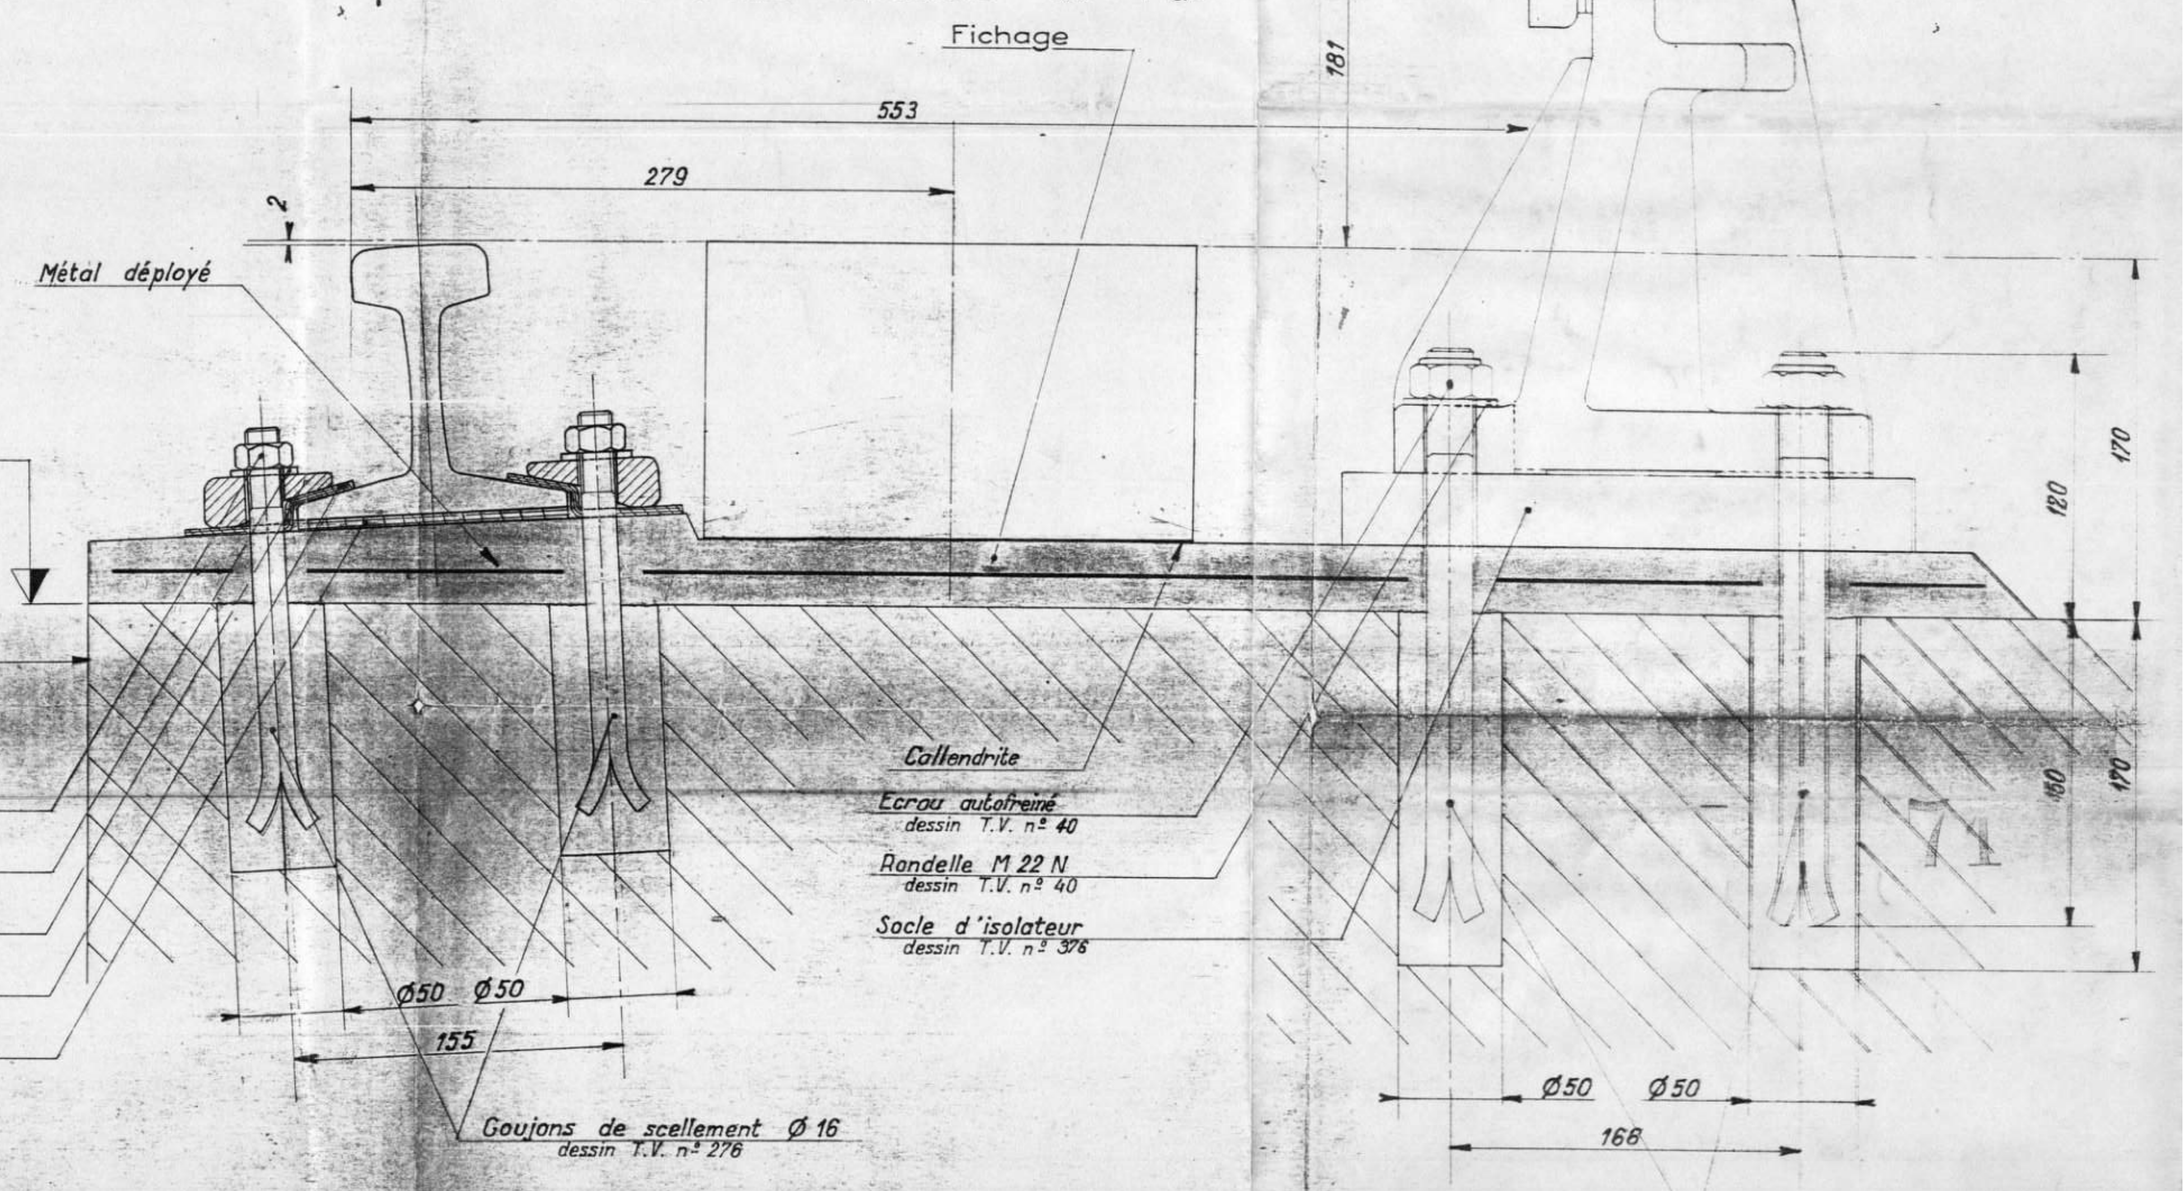

Vue en plan

Plan de pose schématique de la fosse _Dessin TV 370
indiquant la repartition des pièces de roulement

Echelle 1/50

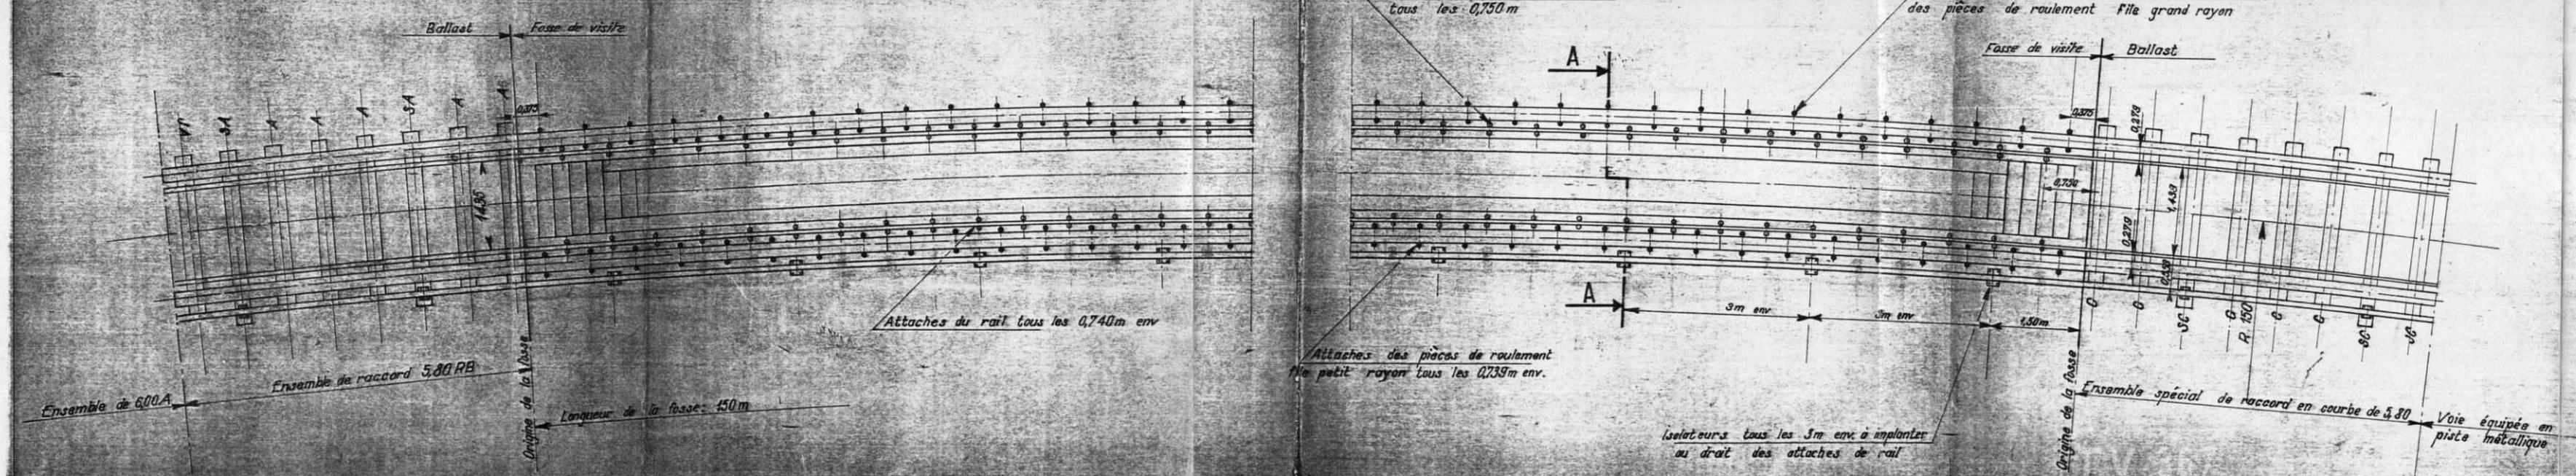

VOIE ISOLÉE

METRO DE MEXICO

LIGNE N° 1

TERMINUS CHAPULTEPEC

POSE DE LA VOIE SUR LA FOSSE DE VISITE

ECH.	DATE : 25. 1. 1968
Div.	DESS : Piéro
	VERIF : Patenaude

L'Ingénieur en Chef

L'Ingénieur Chef de Division

I.S.T.M.E.

S.O.F.R.E.T.U. S.G.T.E.

MODIFICATIONS

TV 367