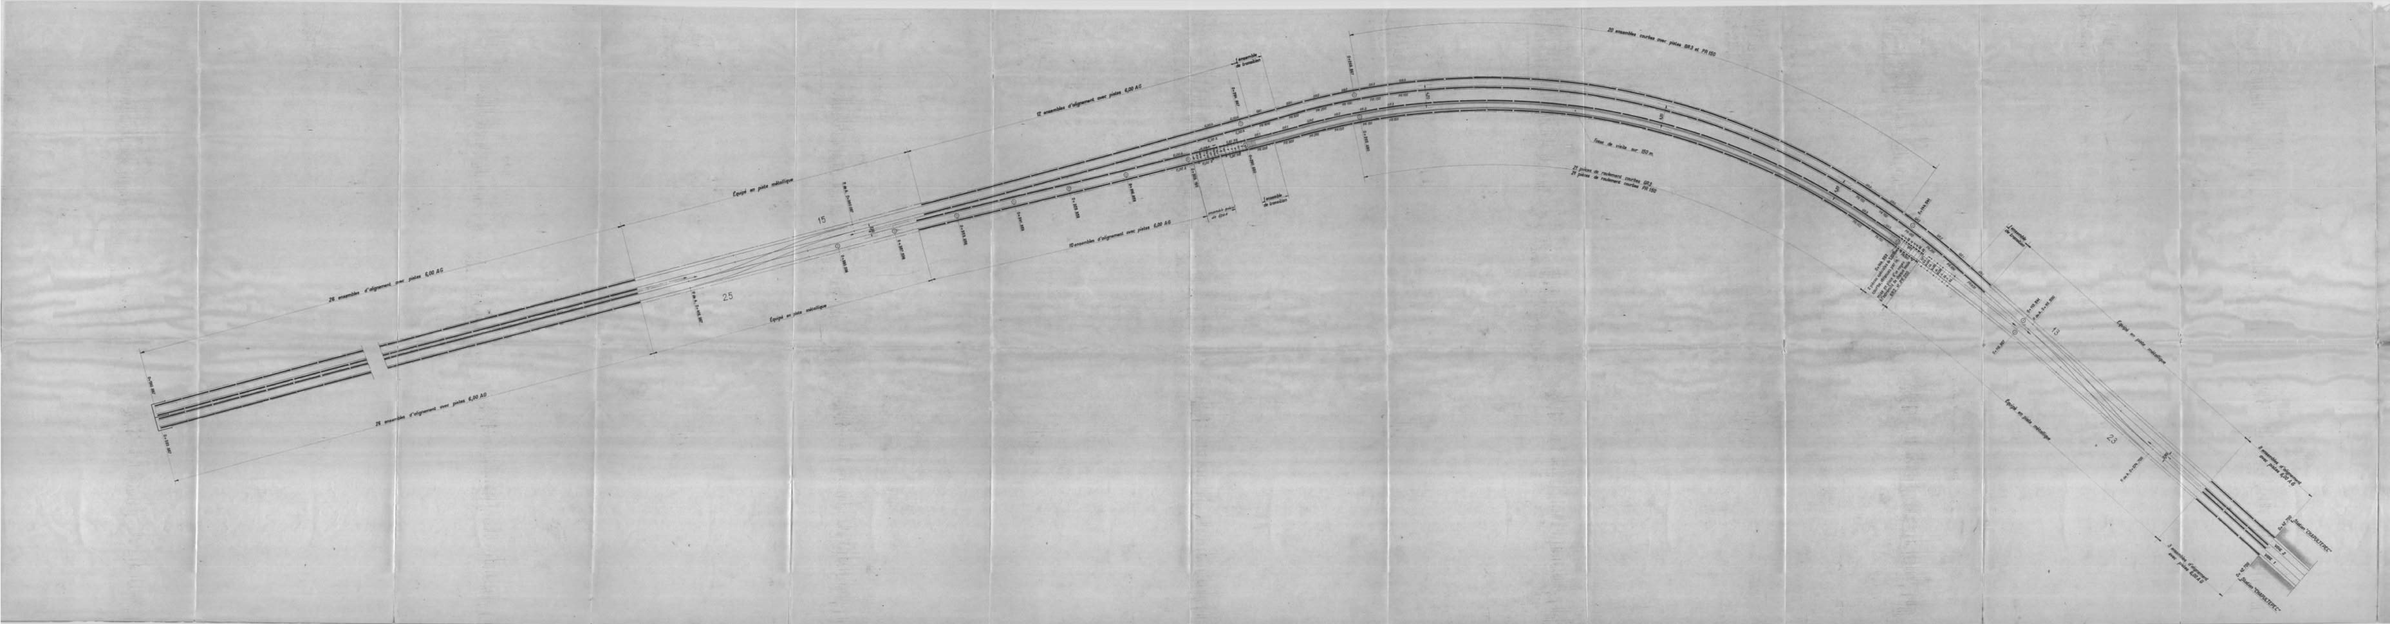

25 ensembles d'alignement avec pistes 6,00 AS
Equipé en piste métallique
15
25
15 ensembles d'alignement avec pistes 6,00 AS
Equipé en piste métallique
25 ensembles d'alignement avec pistes 6,00 AS
Equipé en piste métallique
22 ensembles courbes avec pistes 884 et 79,00
Voies de visite sur 102 m.
22 pistes de roulement courbes 827
22 pistes de roulement courbes 79,00
Equipé en piste métallique
23
Equipé en piste métallique
METRO DE MEXICO
LIGNE N°1
Terminus "CHAPULTEPEC"
PLAN DE POSE SCHÉMATIQUE
ISTME
SATEB
TV 370