MÉTRO DE MEXICO

6

LIGNE N°1

Intercalation BALDERAS - SALTO DEL AGUA

COMMUNICATION N° 25 - ZA2

Tg 0,13 à gauche entrevoie de 3,15 m

Vernis Becki

Conforme au plan d'ensemble N°TV140 sauf les indications de présent dessin

COMMUNICATION N° 14 - ZA1

Tg 0,13 à gauche entrevoie de 3,15 m

Vernis Becki appareil N° ZA1 . Vernis individuels appareil N° 14

Conforme au plan d'ensemble N°TV144 sauf les indications de présent dessin

BRANCHEMENT N° 24

Tg 0,15 à droite Vernis individuels

Conforme au plan d'ensemble N°TV140 sauf les indications de présent dessin

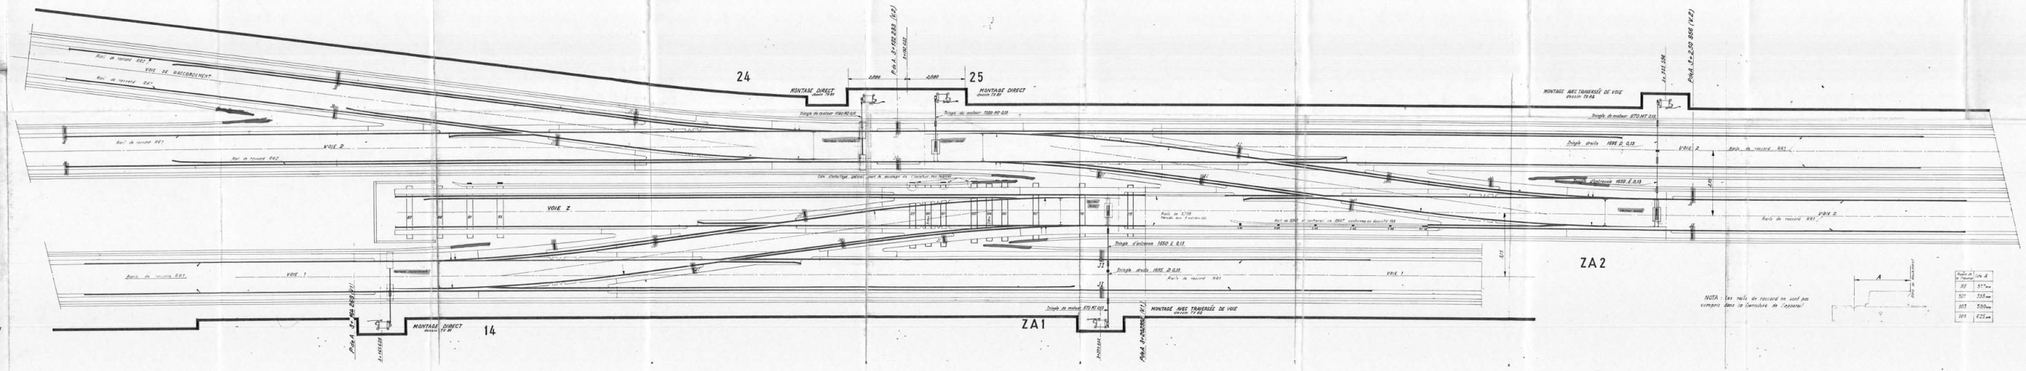
PLAN DE POSE

Echelle 0,02

Paris le 18 Février 1968

L'Ingénieur en Chef

TV N° 388


24
25
14
ZA1
ZA2
VOIE 1
VOIE 2
MONTAGE DIRECT
MONTAGE AVEC TRAVERSÉE DE VOIE
Joint d'entrevoie 1500 à 0,15
Joint d'entrevoie 1400 à 0,13
Joint d'entrevoie 1500 à 0,15
Joint de rattrapage
Joint de rattrapage 1500 à 0,15
Joint de rattrapage 1400 à 0,13
Joint de rattrapage 1500 à 0,15
Joint de rattrapage 1500 à 0,15
Joint de rattrapage 1500 à 0,15