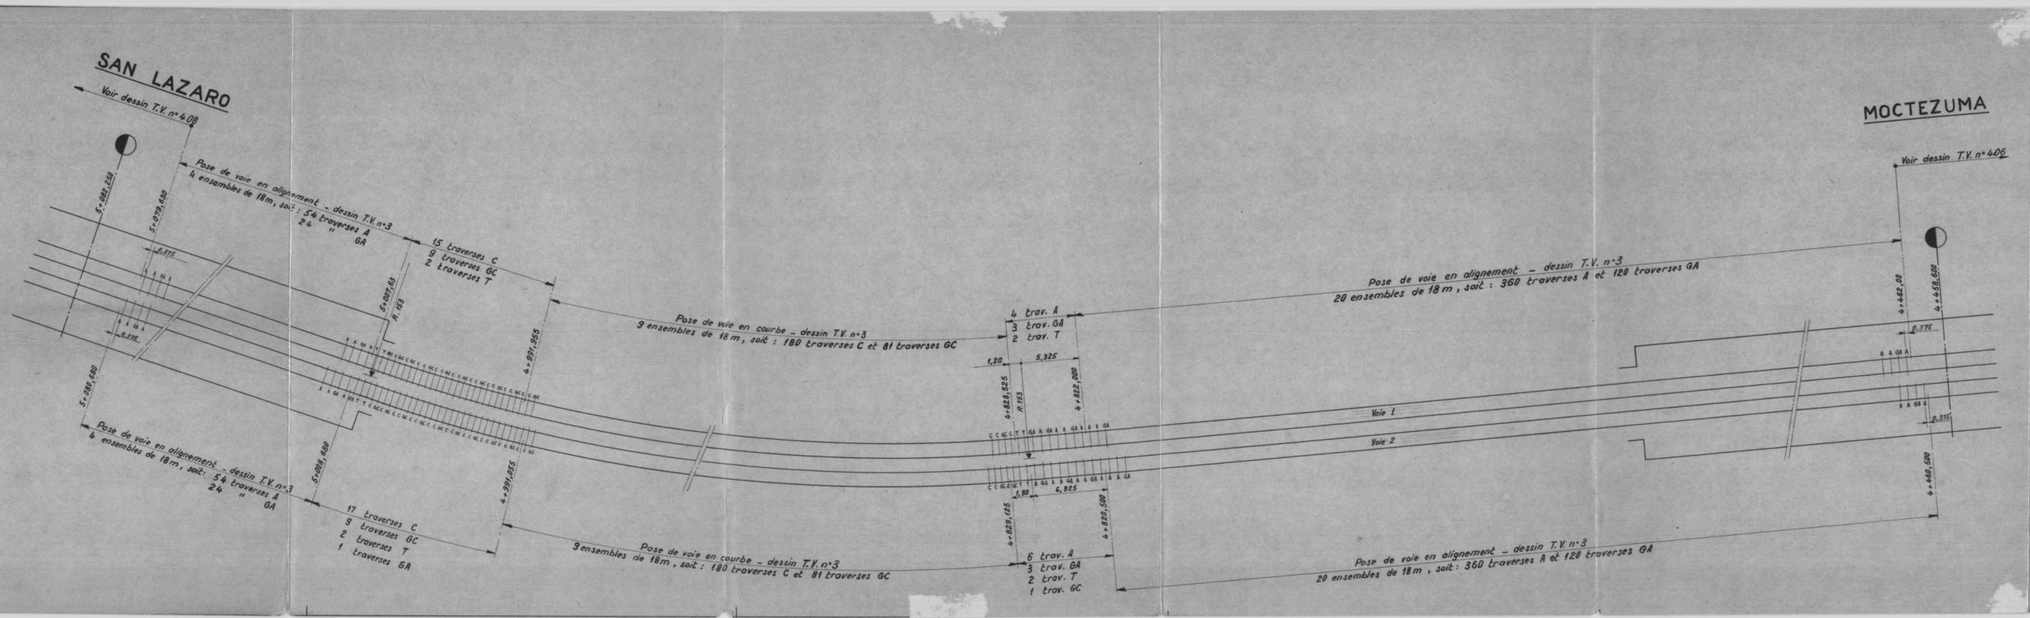


NOTA – Le travelage défini ci dessus au droit des joints isolants sera réalisé ultérieurement après implantation de ceux-ci, en resserrant à 0,480 m les 2 traverses encadrant le joint et en régularisant l'espacement des traverses les plus voisines

METRO DE MEXICO
LIGNE N°1

ECH	PLAN DE POSE SCHEMATIQUE DES VOIES	DATE 3 Juillet 68
1/2	INTERSTATION	DESS. Bollard
	MOCTEZUMA SAN LAZARO	VERIF. Rousseau
	VOIE 1 DU PK. 4+462,000 AU PK. 5+079,630	
	VOIE 2 DU PK. 4+460,500 AU PK. 5+080,680	

L'Ingénieur en Chef — 05 — L'Ingénieur Chef de Division

I.S.T.M.E

S.O.FRE.T.U — S.G.T.E

MODIFICATIONS

TV 407