
SALTO DEL AGUA

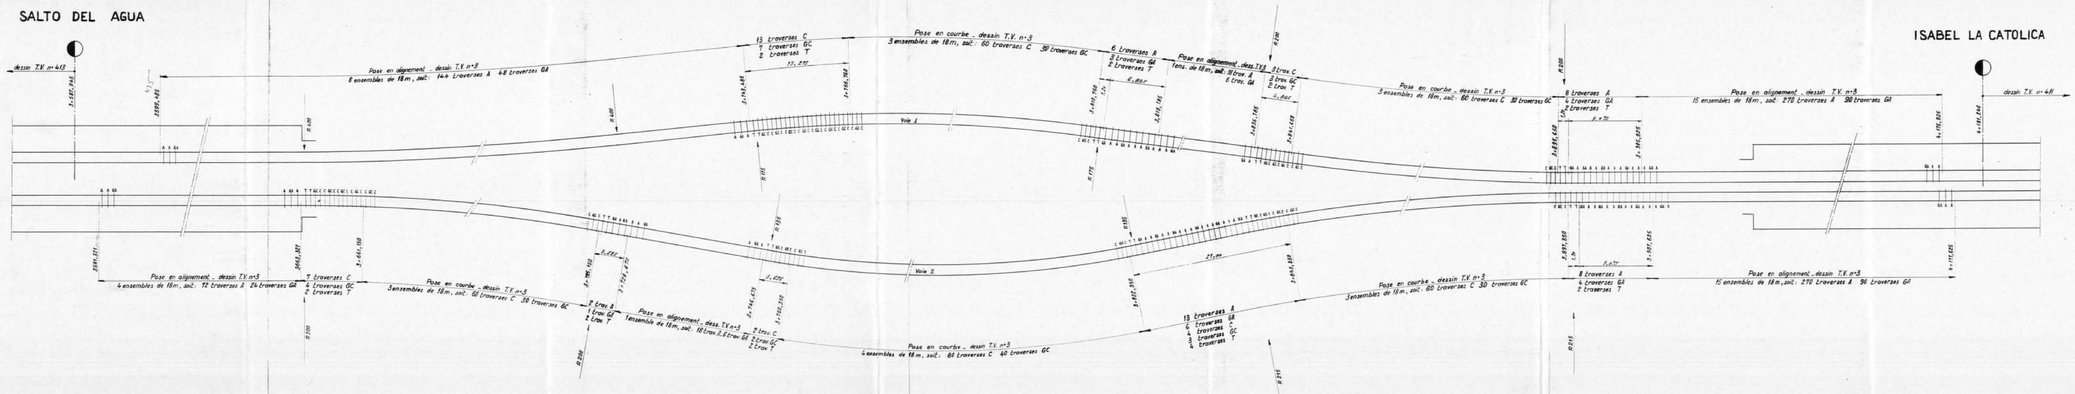

ISABEL LA CATOLICA

NOTA.- Le traveloge ou droit des joints isolants sera réalisé ultérieurement après implantation de ceux-ci, en resserrant de 0,400 m les deux traverses encadrant les joints et en régularisant l'espacement des traverses voisines.

METRO DE MEXICO
LIGNE N°1

ECH	PLAN DE POSE SCHEMATIQUE DES VOIES	DATE: 9 Juillet 68
1/2000	INTERSTATION: SALTO DEL AGUA - ISABEL LA CATOLICA	DESS: Bakhirat
	VOIE 1 DU PK 3+550,480 AU PK 4+170,925	VERIF: Schmitz
	VOIE 2 DU PK 3+551,321 AU PK 4+171,825	

L'Ingénieur en Chef
P.

M. L'Ingénieur Chef de Division
Examiné

I.S.T.M.E

S.O.FRETU S.G.T.E

MODIFICATIONS

TV 412