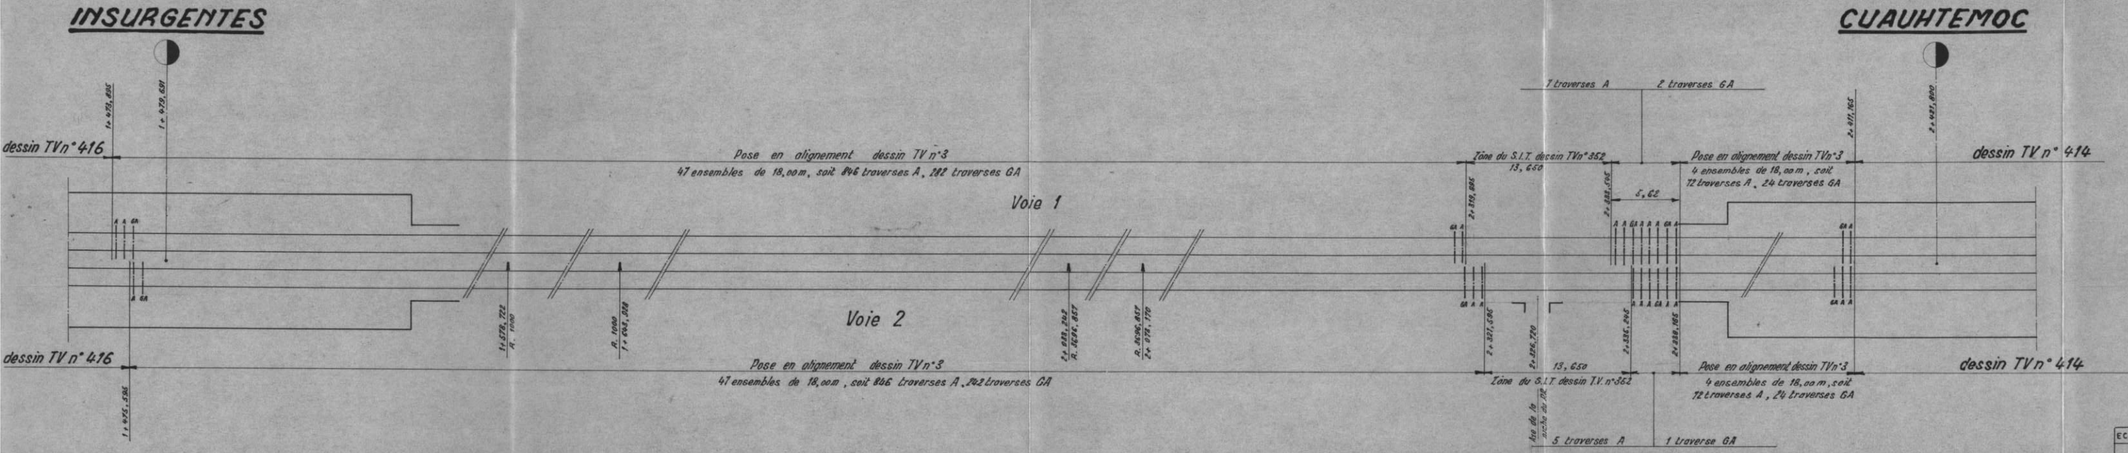



NOTA : le traveloge au droit des joints isolants sera réalisé ultérieurement après implantation de ceux-ci, en resserrant à 0,900m les deux traverses encadrant les joints et en régularisant l'espacement des traverses voisines

METRO DE MEXICO
LIGNE N° 1

| ECH. | PLAN DE POSE SCHEMATIQUE DES VOIES | DATE : 9 Juillet 1968 |
|---|---|---|
| 1/200 | INTERSTATION<br>INSURGENTES – CUAUHTEMOC<br>VOIE 1 DU PK 1+473, 895 AU PK 2+411,165<br>VOIE 2 DU PK 1+475, 595 AU PK 2+411,165 | DESS. Cinturel<br>VERIF |

L'Ingenieur en Chef

P.O. L'Ingénieur Chef de Division

I.S.T.M.E.

S.O.F.R.E.T.U. S.G.T.E.

TV 415

MODIFICATIONS