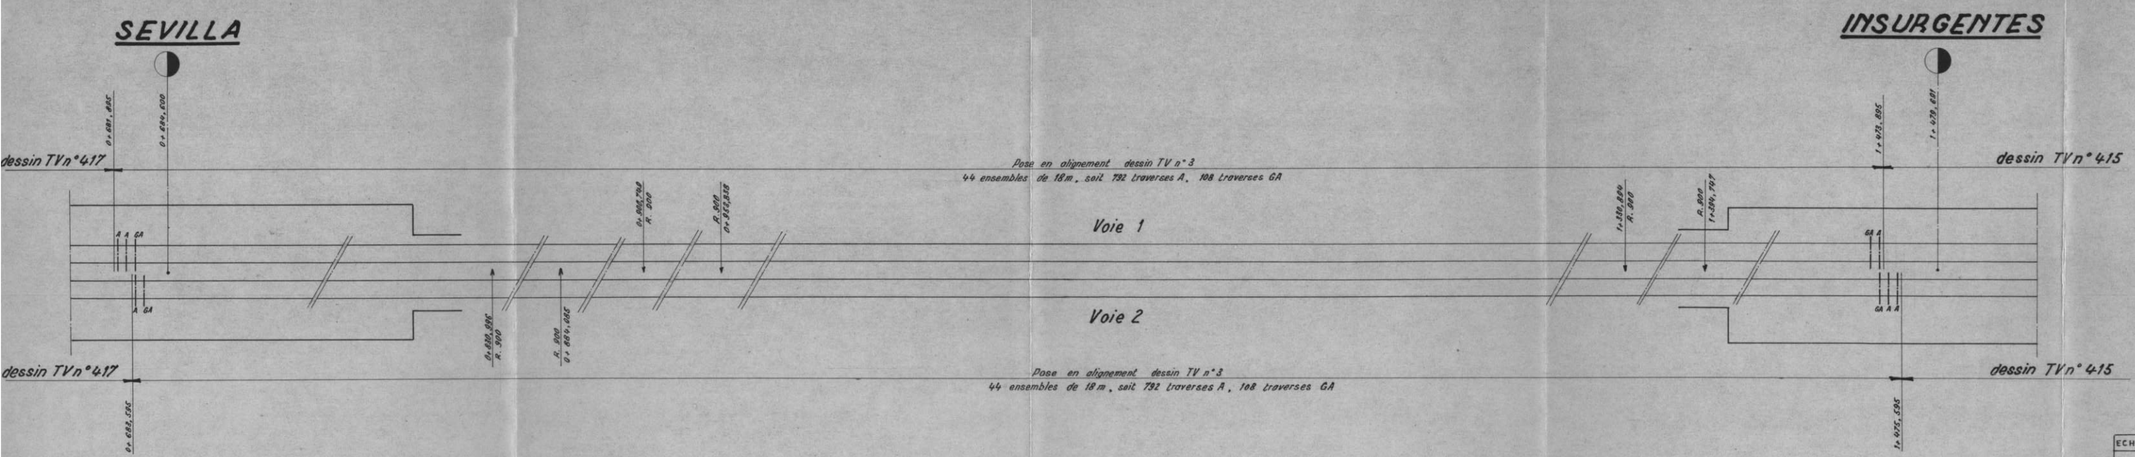


Note: le travelage au droit des joints isolants sera réalisé ultérieurement après implantation de ceux-ci, en resserrant à 0,400 m les deux traverses encadrant les joints et en régularisant l'espacement des traverses voisines

METRO DE MEXICO

LIGNE Nº 1

ECH. 1/200	PLAN DE POSE SCHEMATIQUE DES VOIES INTERSTATION SEVILLA - INSURGENTES VOIE 1 DU PK 0+681,895 AU PK 1+473,895 VOIE 2 DU PK 0+688,595 AU PK 1+475,595	DATE: 9 Juillet 1968 DESS: Cinturel VERIF L'Ingénieur en Chef Pour L'Ingénieur Chef de Division

I.S.T.M.E.

S.O.F.R.E.T.U. S.G.T.E.

MODIFICATIONS

TV 416