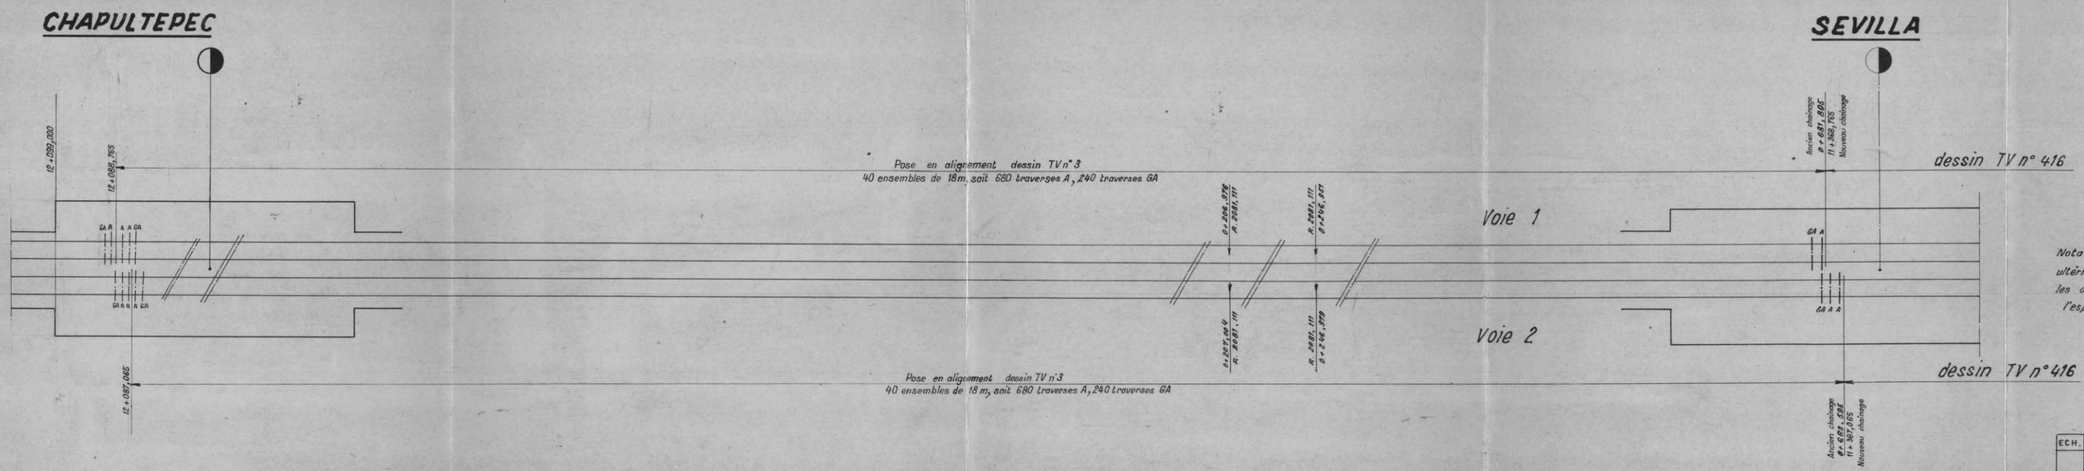


Nota: le travelage au droit des joints isolants sera réalisé ultérieurement après implantation de ceux-ci, en resserrant à 0,40 m les deux traverses encadrant les joints et en régularisant l'espacement des traverses voisines

METRO DE MEXICO

LIGNE N° 1

ECH. 1/200

PLAN DE POSE SCHEMATIQUE DES VOIES

INTERSTATION

CHAPULTEPEC - SEVILLA

VOIE 1 DU PK 11+368,765 AU PK 12 +088,765

VOIE 2 DU PK 11+387,065 AU PK 12 +087,065

DATE : 9 Juillet 1968

DESS Cintrel

VERIF

L'Ingenieur en Chef

PO L'Ingénieur Chef de Division

I.S.T.M.E.

S.O.F.R.E.T.U.

S.G.T.E.

TV 417

A — Suppression de la communication 11+21 le 3 Janv. 1969

MODIFICATIONS

A