Interstation

SAN LAZARO
LA CANDELARIA

MÉTRO DE MEXICO

TV-424

6


LIGNE N° 1

DEVERS

COURBES N° 9 et N° 10

CÔTÉ PETIT RAYON

COURBE N° 10

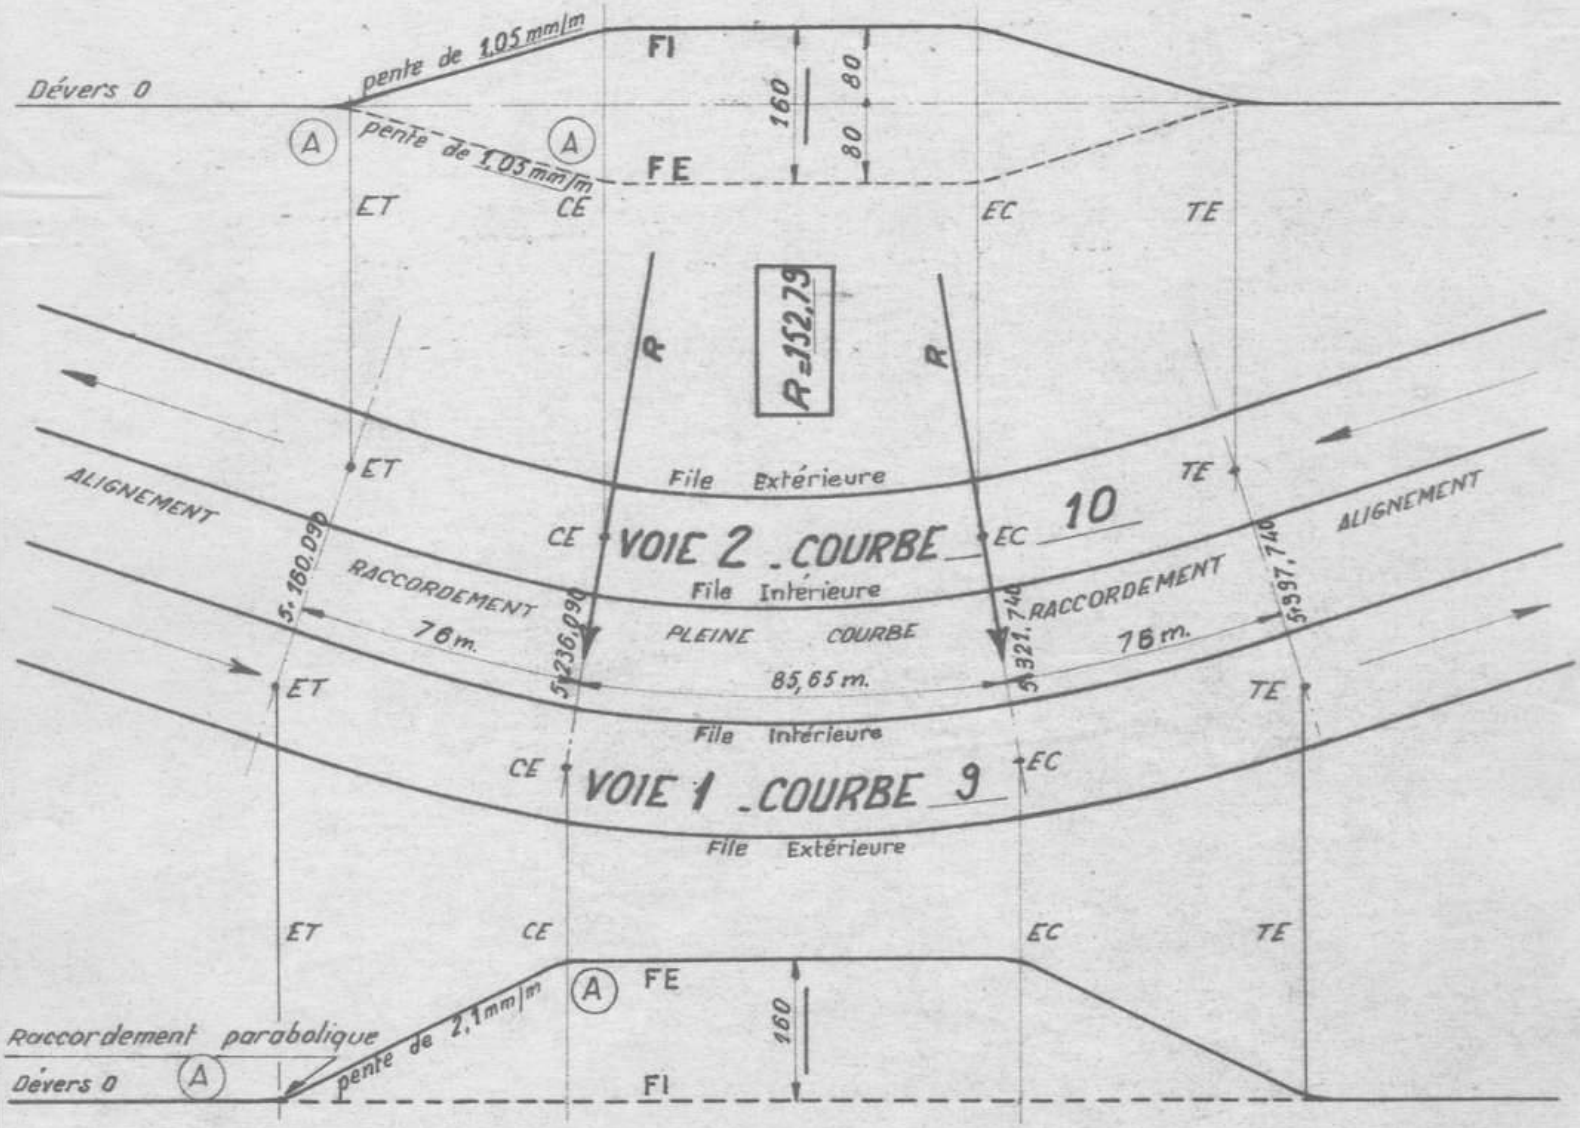

COURBE N° 9

CÔTÉ GRAND - RAYON

Paris le 16 Juillet 1968

TV 424

(A) Raccordement parabolique de la forme $y = 0,0002\ x^2$