Interstation
PINO SUAREZ
ISABEL LA CATOLICA

MÉTRO DE MEXICO

TV-432

14


LIGNE N° 1

DEVERS

COURBES N°25 et N°26

CÔTÉ GRAND RAYON

COURBE N° 26

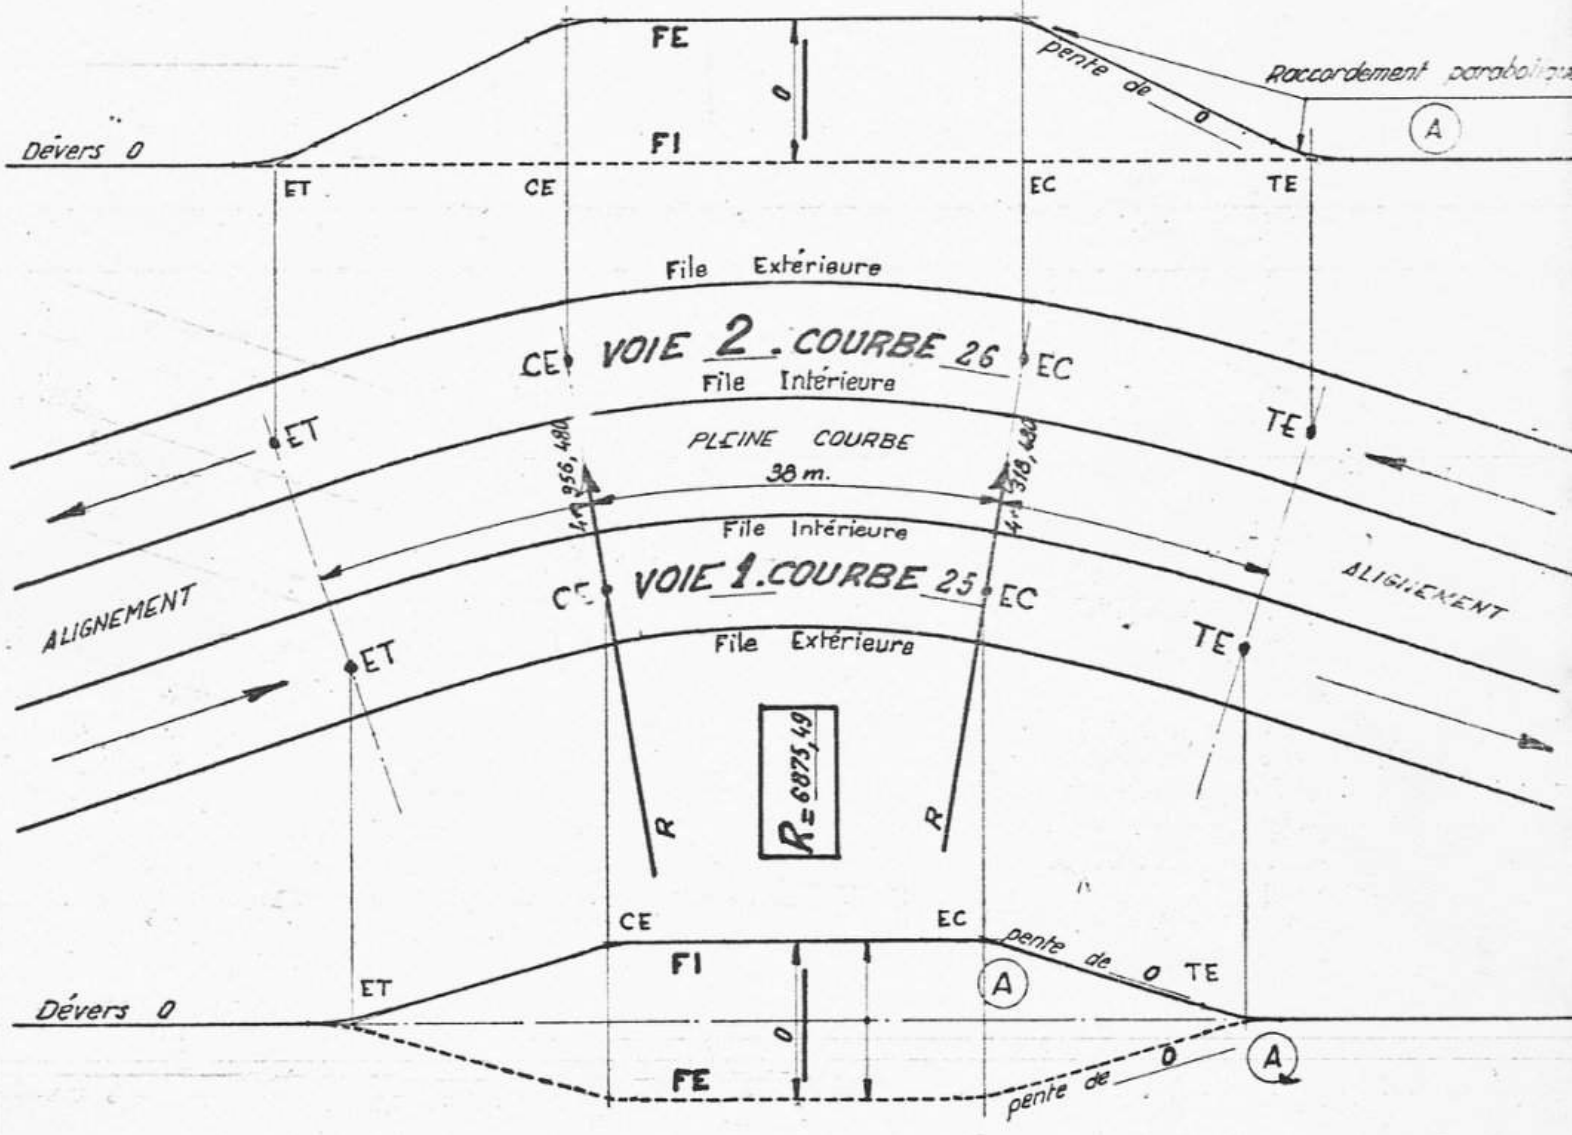

COURBE N° 25

CÔTÉ PETIT RAYON

Paris le 16 Juillet 1968

TV 432

(A) Raccordement parabolique de la forme $y = 0,0002x^2$