
Interstation: SALTO DEL AGUA
BALDÉRAS

# MÉTRO DE MEXICO

## LIGNE N° 1

## DEVERS

## COURBE N° 38

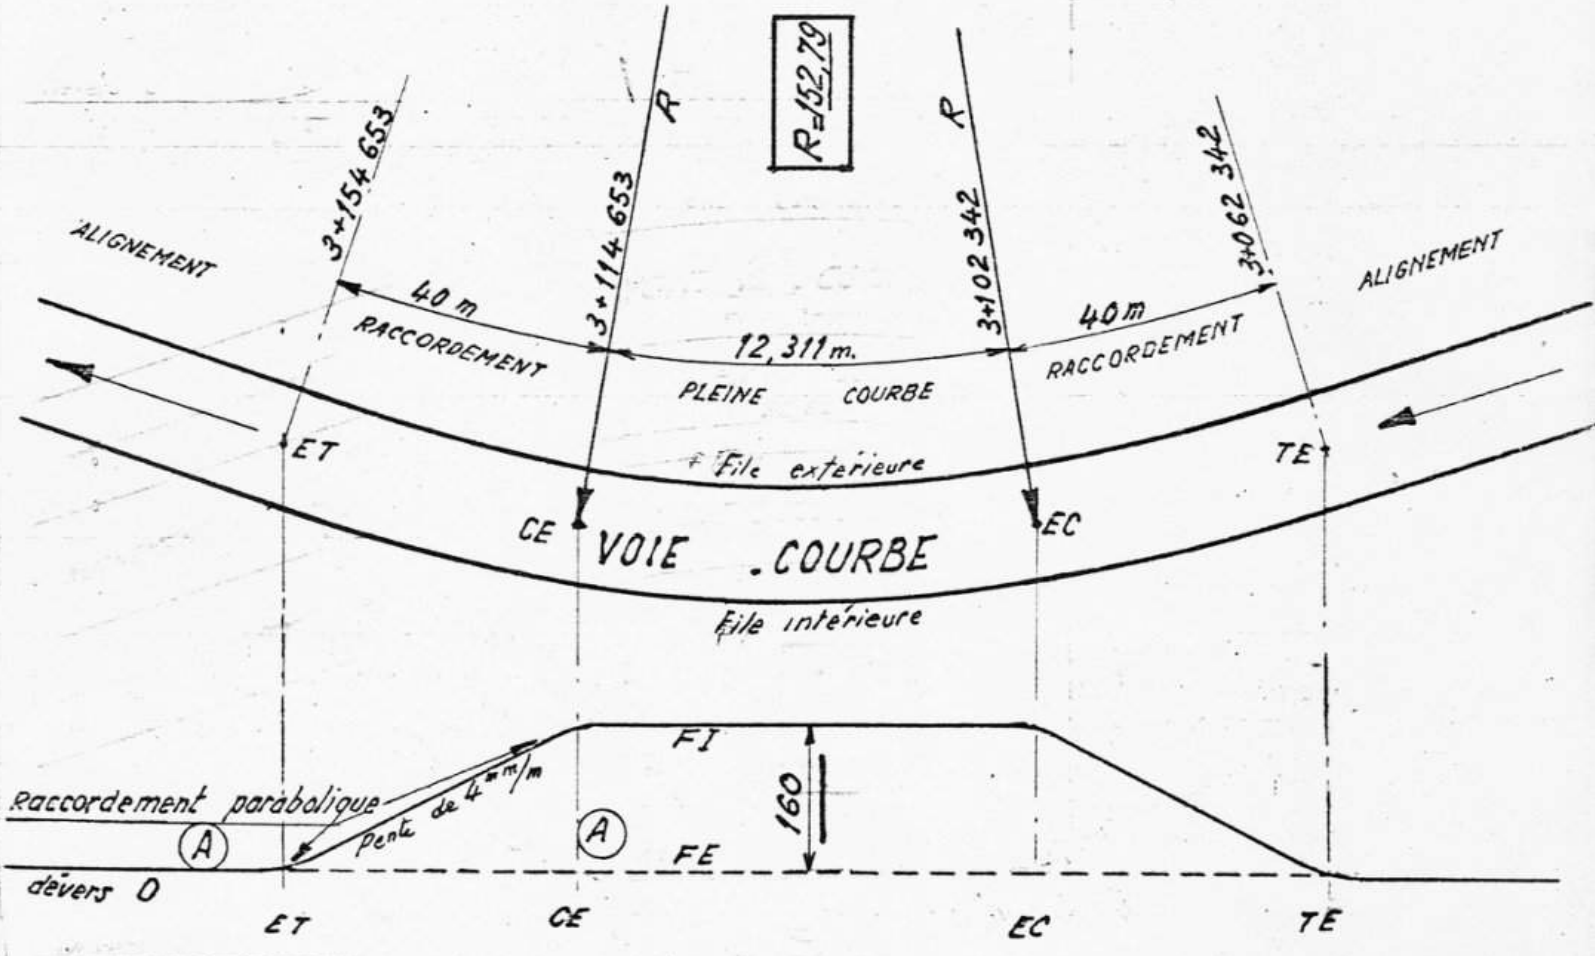


CÔTÉ . GRAND RAYON

COURBE

(A) Raccordement parabolique de la forme $y = 0{,}0002\,x^2$

Paris le 16 Juillet 1968

TV 442