Interstation : BALDERAS
CUAUHTEMOC


MÉTRO DE MEXICO

25

LIGNE N° 1

DEVERS

COURBES N° 39 et N° 40

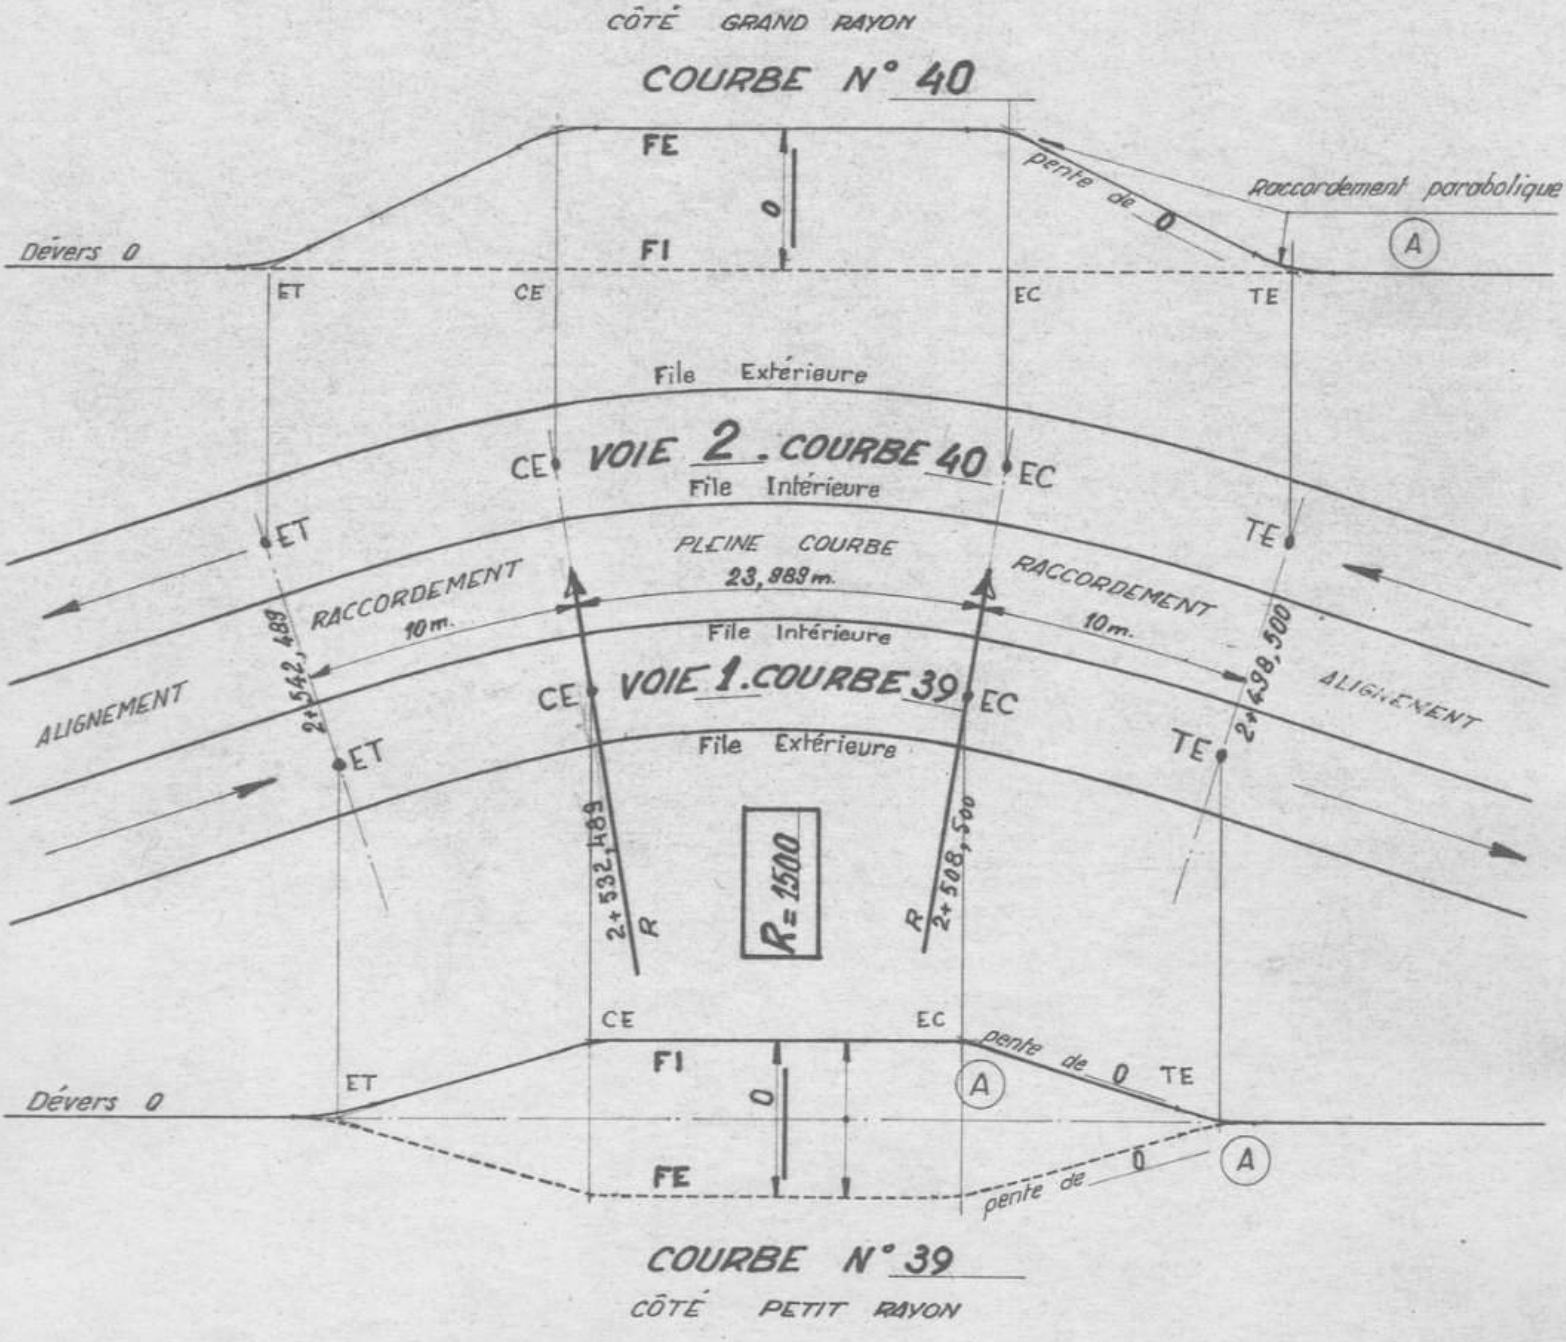

Paris le 16 Juillet 1968

TV 443

(A) Raccordement parabolique de la forme $y = 0{,}0002x^2$