Interstation CHAPULTEPEC
JUANACATLAN

S.T.C.
Departamento de Vias
y Estructuras
Seccion de Mantenimiento
de Vias

MÉTRO DE MEXICO TV-475


LIGNE N° 1

DEVERS

COURBES N°55 et N°56

CÔTÉ GRAND RAYON

COURBE N° 56

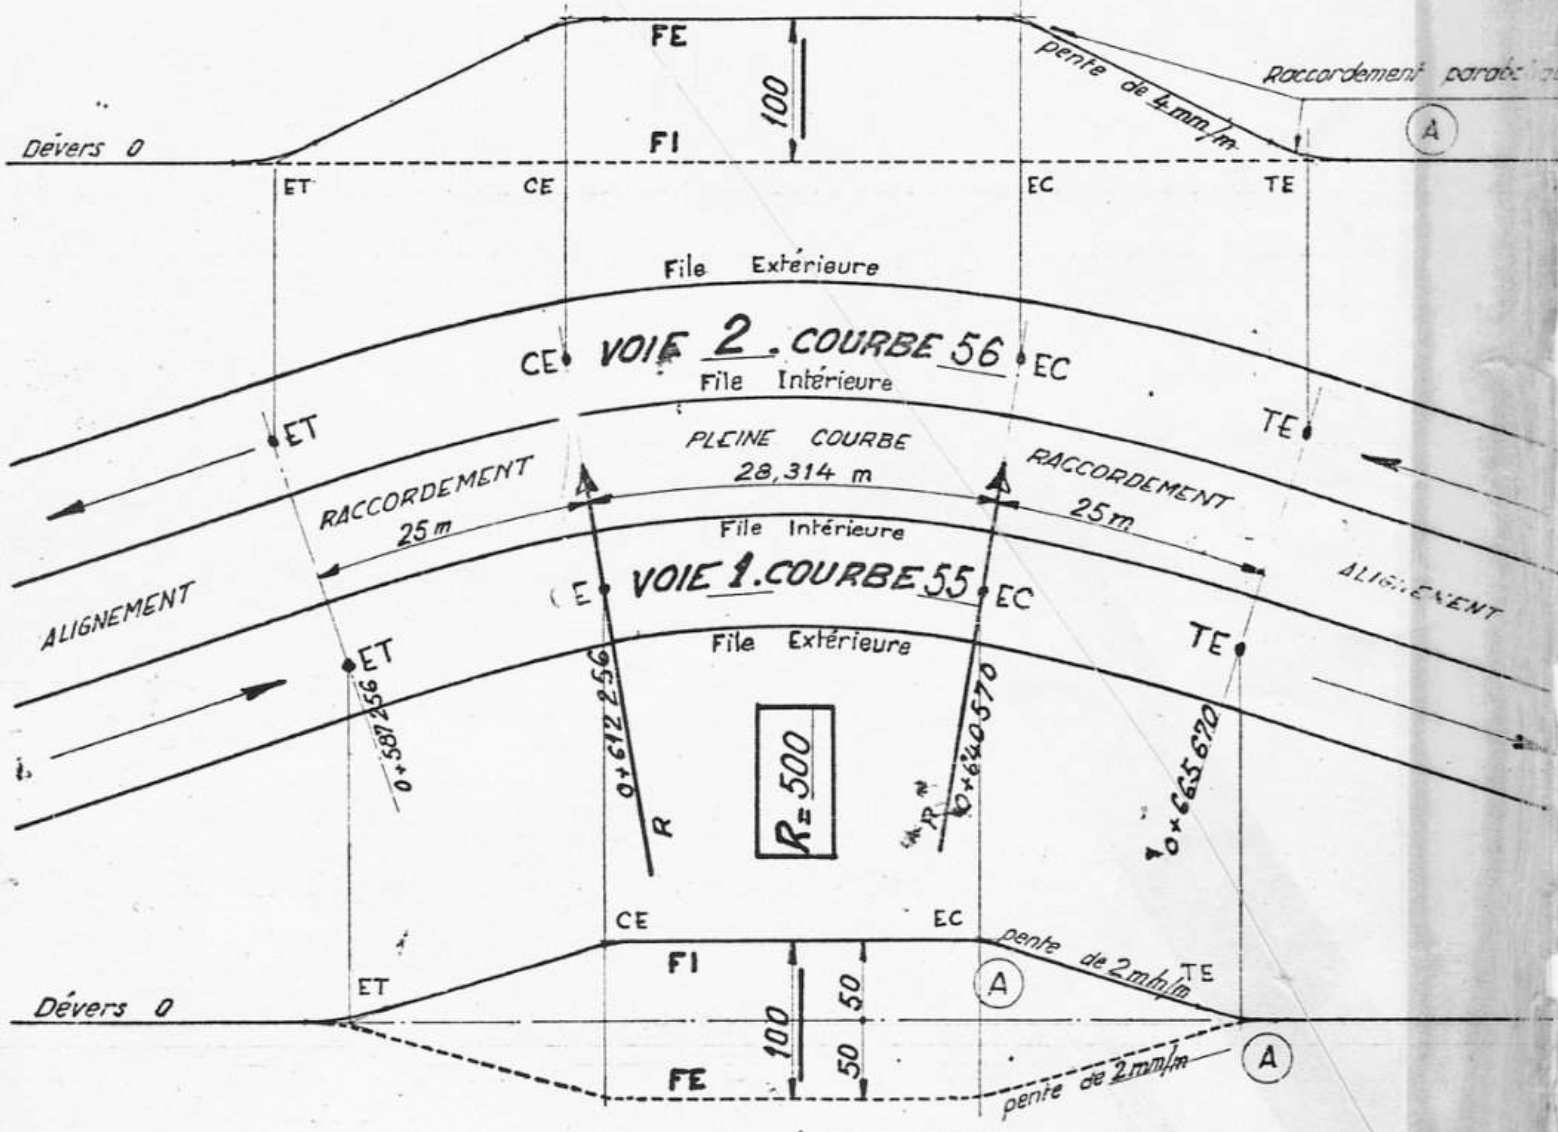

COURBE N° 55

CÔTÉ PETIT RAYON

TV 475

(A) Raccordement parabolique de la forme $y = 0,0002x^2$