Interstation : CHAPULTEPEC
JUANACATLAN

S.T.C.
Departamento de Vias
y Estructuras
Seccion de Mantenimiento
de Vias

MÉTRO DE MEXICO


TV-476

4

LIGNE N° 1

DEVERS

COURBES N° 57 et N° 58

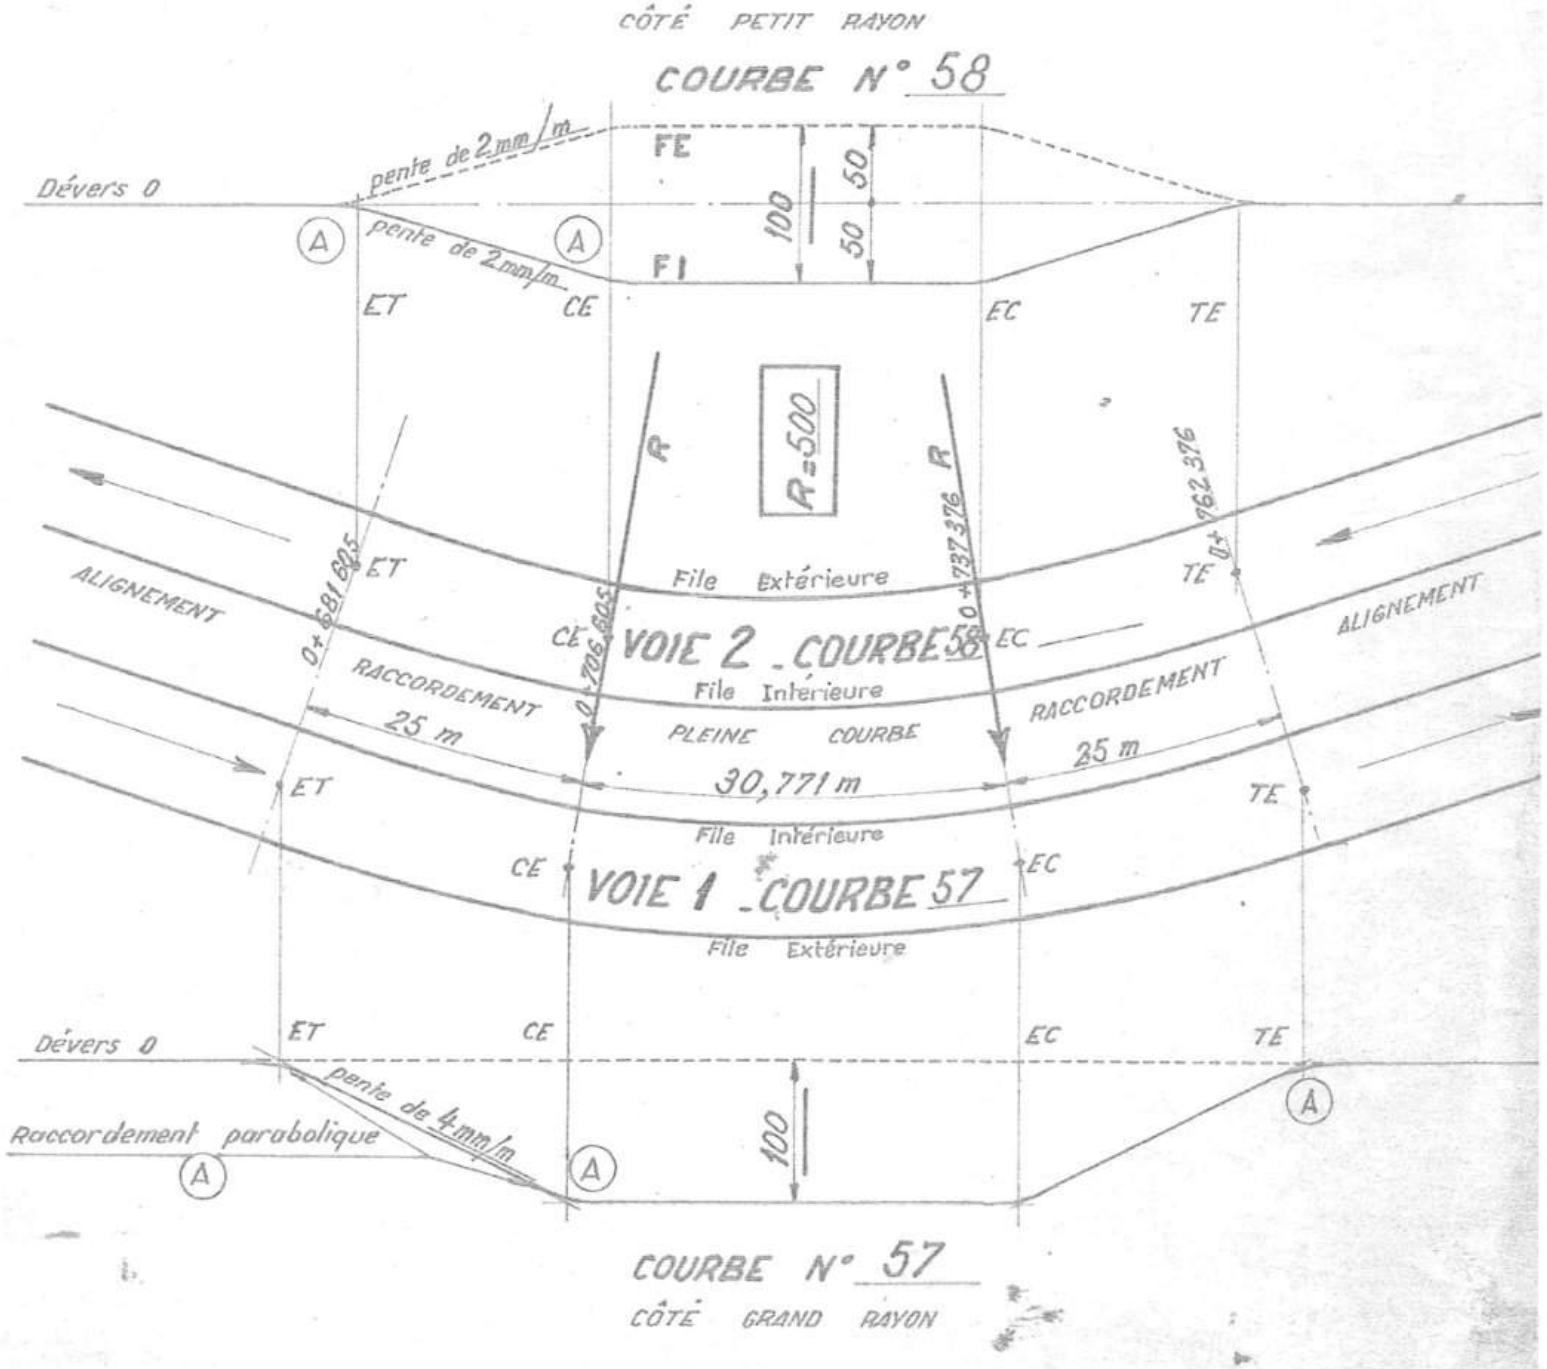

TV 476