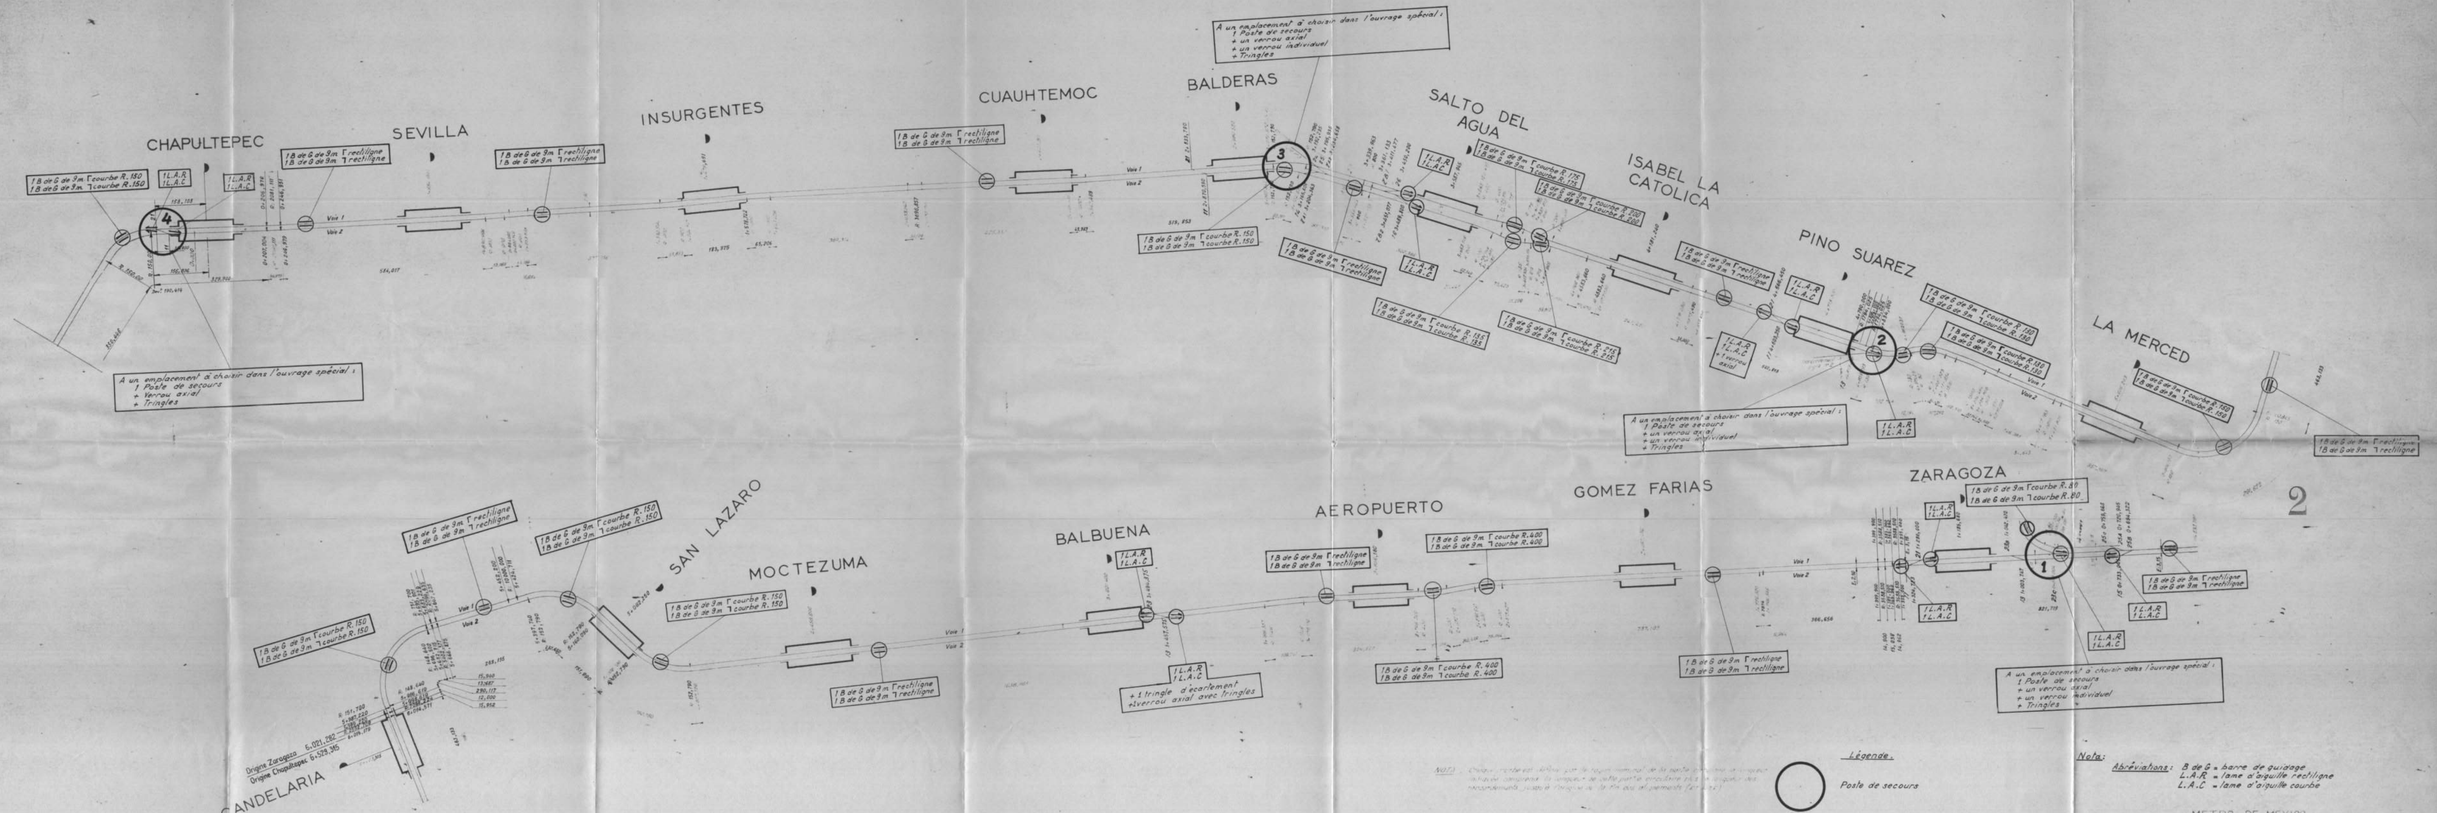

CHAPULTEPEC
SEVILLA
INSURGENTES
CUAUHTEMOC
BALDERAS
SALTO DEL AGUA
ISABEL LA CATOLICA
PINO SUAREZ
LA MERCED
SAN LAZARO
MOCTEZUMA
BALBUENA
AEROPUERTO
GOMEZ FARIAS
ZARAGOZA
LA CANDELARIA
A un emplacement à choisir dans l'ouvrage spécial :
+ 1 Poste de secours
+ un verrou axial
+ un verrou individuel
+ Tringles
+ 1 tringle d'écartement et verrou axial avec tringles
1 B de G de 9m Trectiligne
1 B de G de 9m Tcourbe R. 150
1 B de G de 9m Tcourbe R. 175
1 B de G de 9m Tcourbe R. 200
1 B de G de 9m Tcourbe R. 400
1 B de G de 9m Tcourbe R. 600
1 B de G de 9m Tcourbe R. 80
1 L.A.R
1 L.A.C
Légende.
Poste de secours
Dépot secondaire
Note:
Abréviations : B de G = barre de guidage
L.A.R = lame d'aiguille rectiligne
L.A.C = lame d'aiguille courbe
METRO DE MEXICO
LIGNE N°1
MATÉRIEL DE VOIE POUR INTERVENTIONS URGENTES
IMPLANTATION DES POSTES DE SECOURS ET DES DÉPOTS SECONDAIRES
DATE : 13 MAI 1969
DESS. MALLOT. R
VERIFIÉ
APPROUVÉ
ISTME
SOFRETU
SGTE
TV 621