TV-633

METRO DE MEXICO

4

LIGNE N° 1

TERMINUS OBSERVATORIO

BRANCHEMENT N° 13 B

Tg 0,13 à droite _ Verrou axial _

BRANCHEMENT N° 13 C

Tg 0,13 à gauche . Verrou axial _

PLAN DE POSE

3/ Modification pour coupure des barres de courant dans les appareils 13c et 13b et pour le passage des cheminements.
2/ Modifié le 20 Avril 1970 . Pose de 2 barres de guidage appareil 13 B, voie C
1/ Modifié le 5 janv 1970 d'après les dessins 70 XI 103 III 550 et TV

TV 633³

9,721 m
6,686 m
Montage N°1 de l'isolateur sur plateau suivant dessin TV n°60
Montage N°3 de l'isolateur sur plateau suivant dessin TV n°60
Voie A
Voie B
Voie C
13 C
13 B
20,236 m
Contrerail C3
Rail de raccord
Zone équipée de l'appareil
CHEMINEMENT
Coter de calage
TV 631

SCHEMA D'INFLEXION DES RAILS RR2 - RR4 (App. 13C)

SCHEMA D'INFLEXION DES RAILS RR1 - RR3 (App 13C)

MODIFICATIONS DES CONTRERAILS C3 DE L'APPAREIL 13C

" voie directe "

"Coté voie déviée"

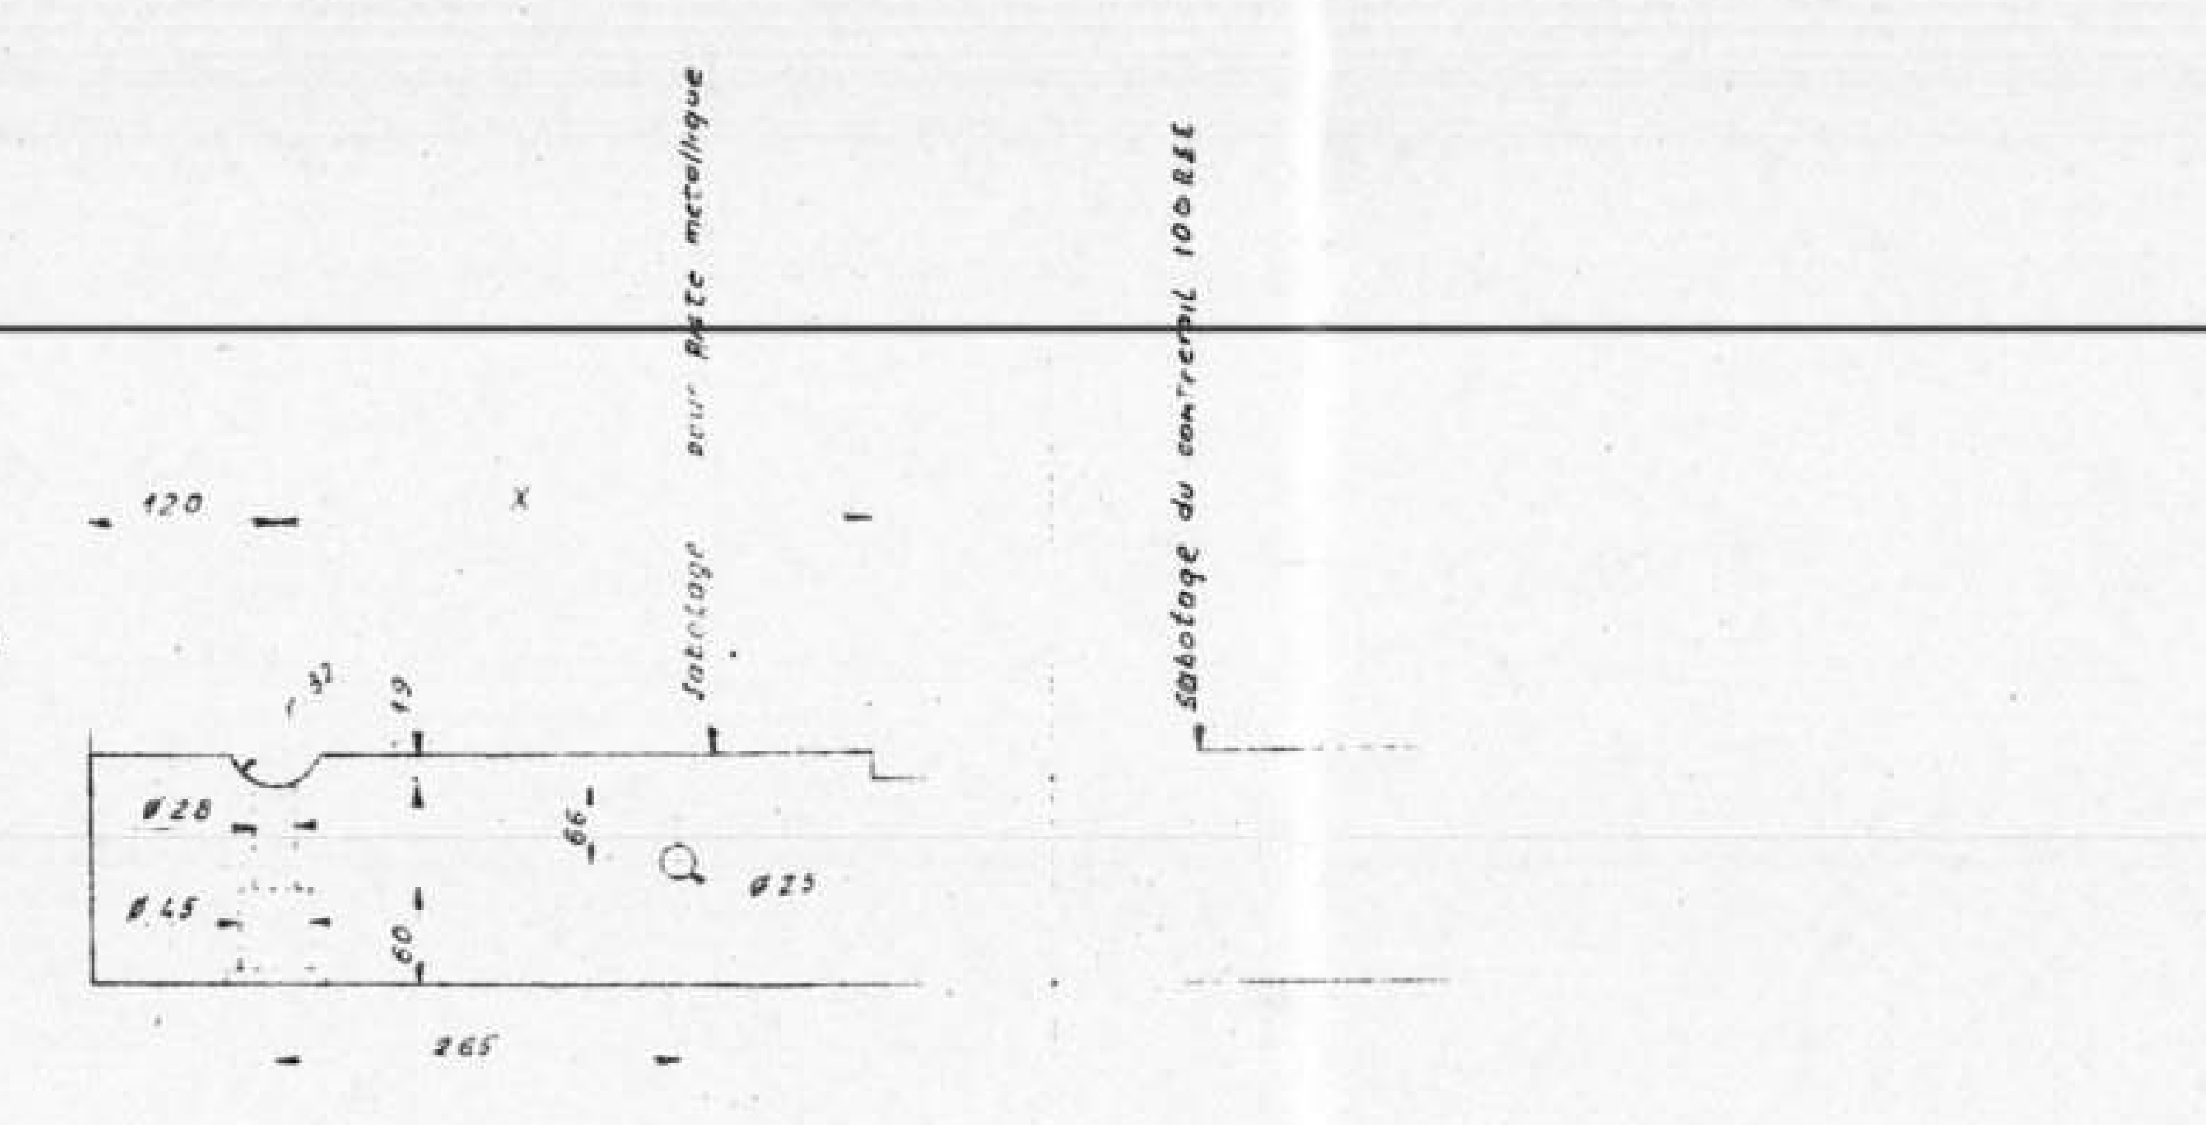
120
265
Sabotage sur poste métallique
Sabotage du contrerail 100 EE

DESIGNATIONS	LONGUEURS	COTE X
Traverse A	2,80	523
Traverse B	2,70	474
Traverse C	2,70	426
Buton E	1,50	
Buton F	1,50	
Buton G	1,50	523
Buton H	1,50	474
Buton J	1,50	426

Pose du isolateur sur plateau
Montage n°3
Butons non sabotes

Pose du isolateur sur plateau dessin
Montage n°1
Sabotes pour rail et contrerail

	App 13B	App 13C
Les traverses A remplacent les traverses	52 55	54 64
Les traverses B remplacent les traverses	58 57	56.66
Les traverses C remplacent les traverses		58 68