
TV-813


2

CONTRERAIL DE 18,00 m

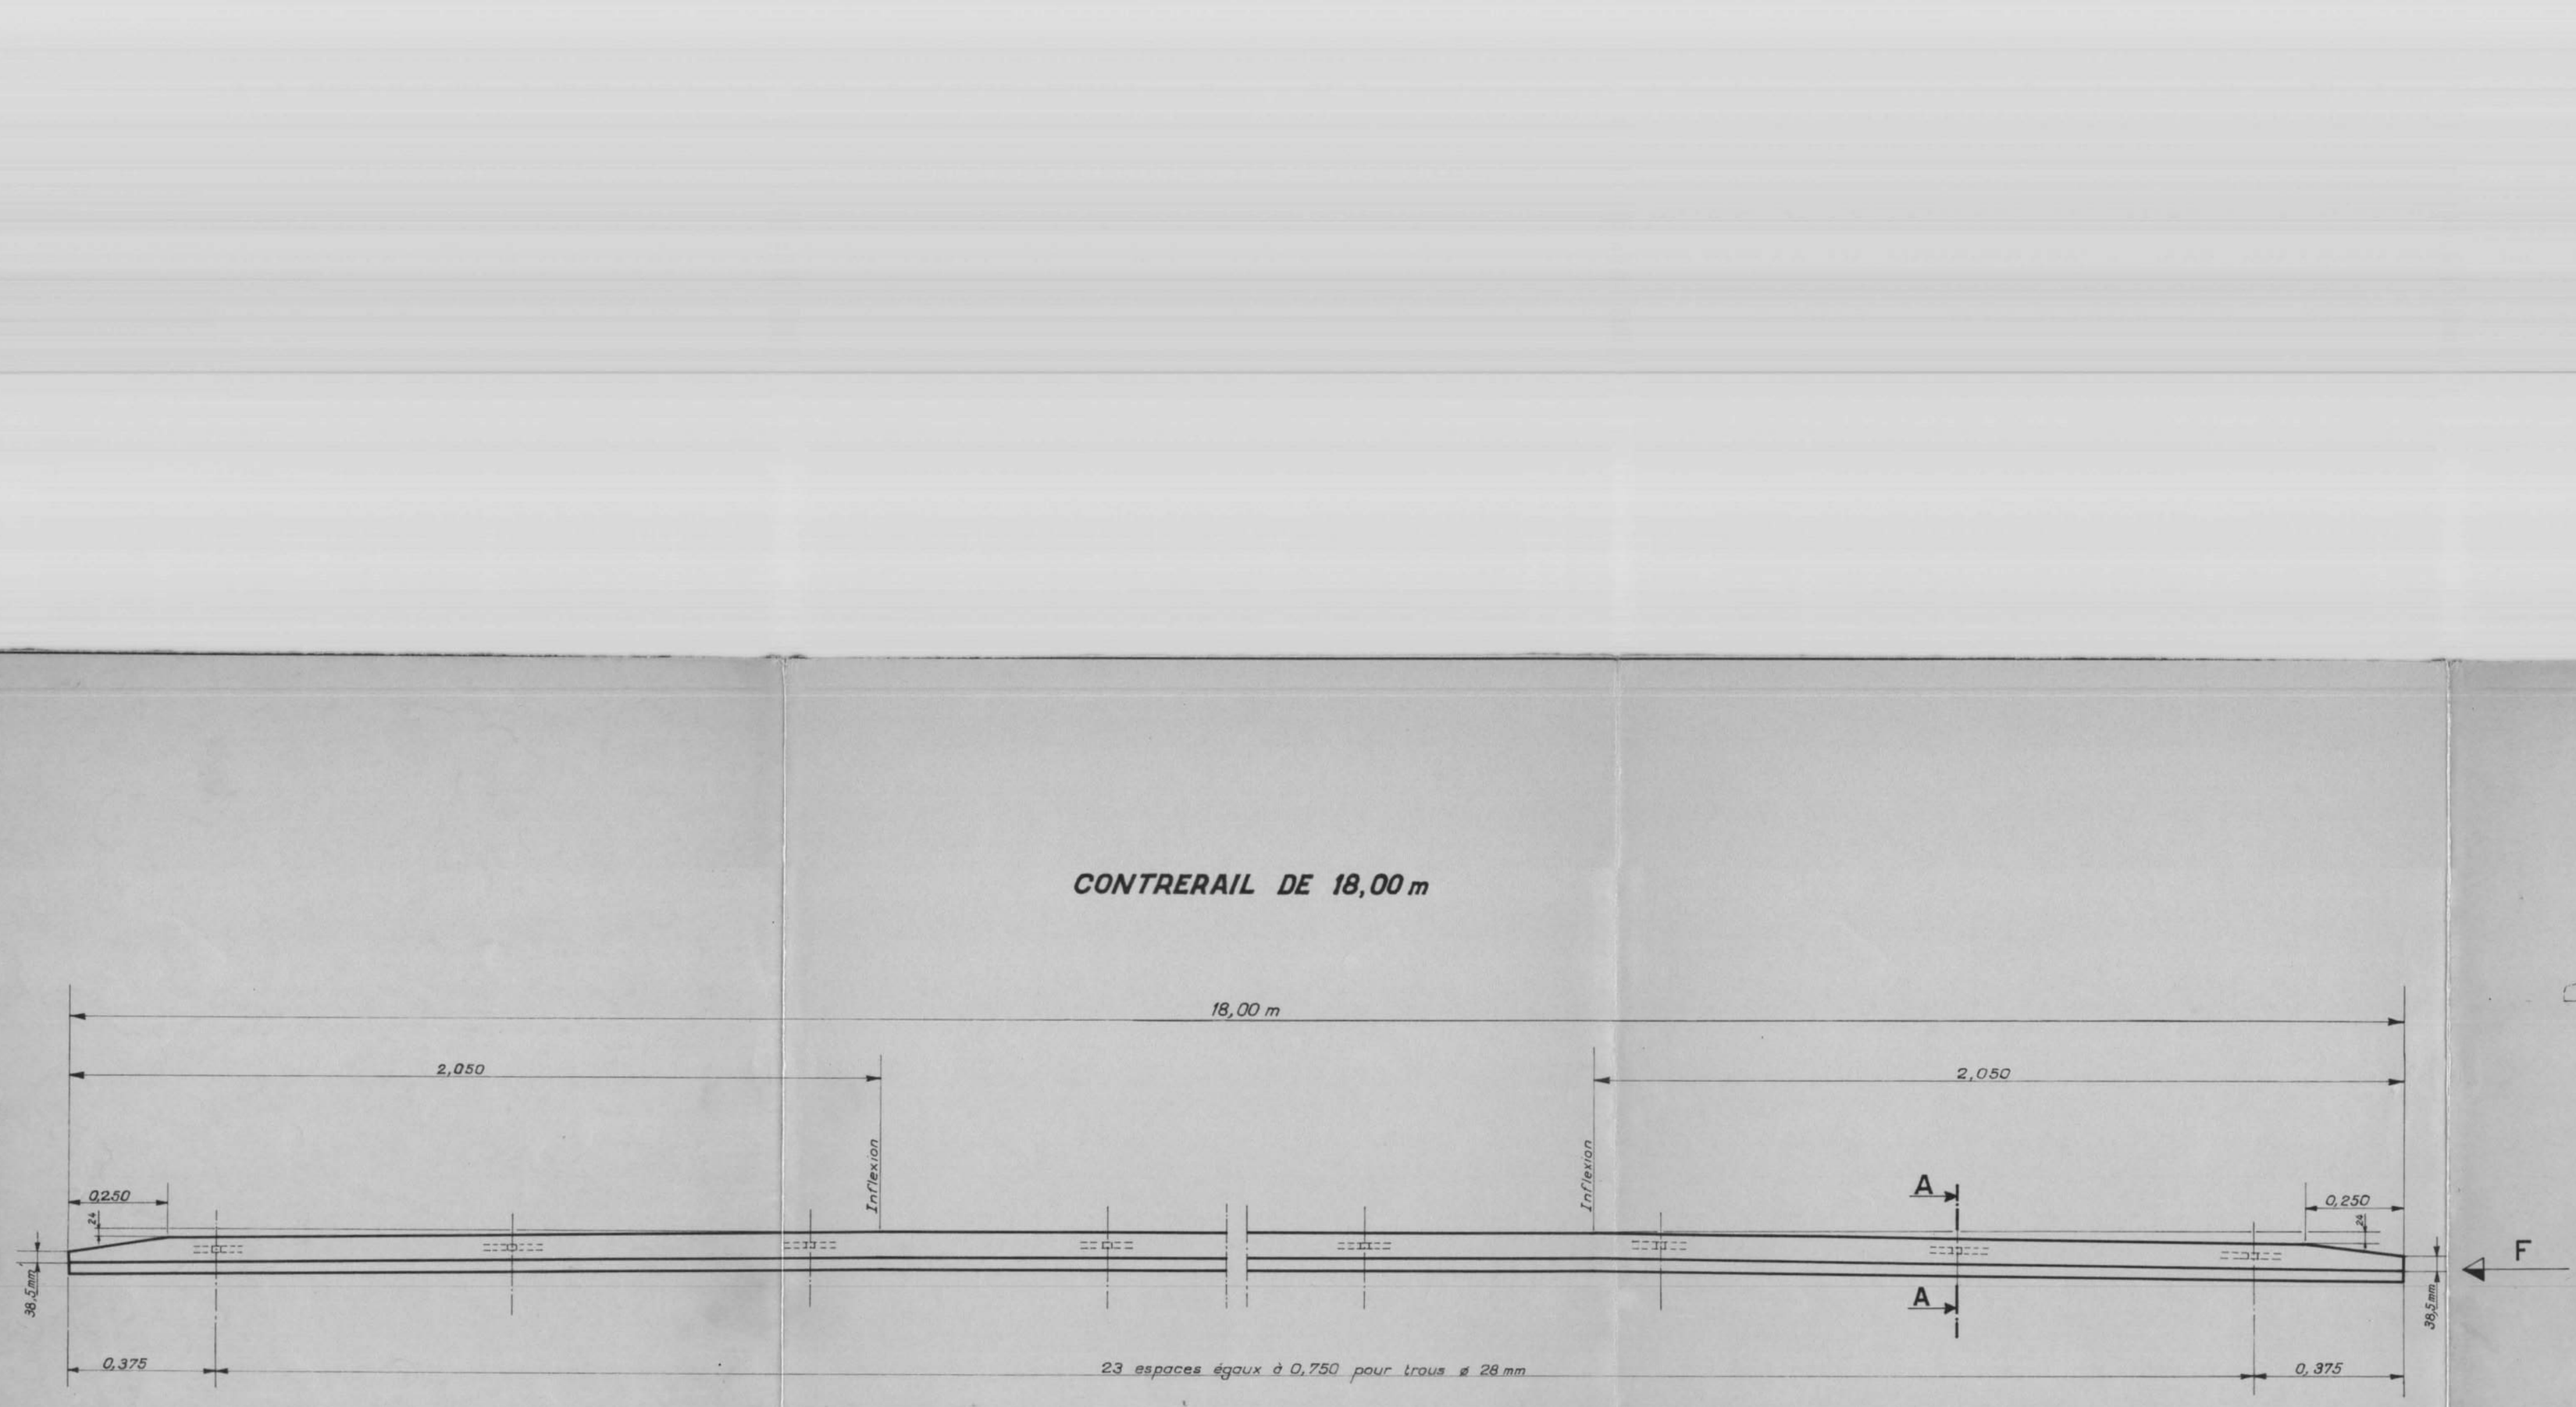


TV813

COUPE AA

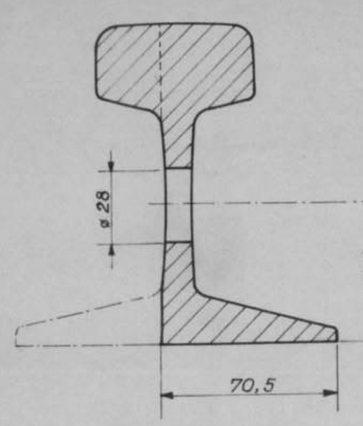

VUE SUIVANT "F"

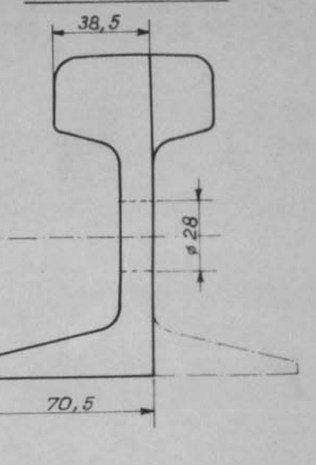

NOTA : Pour le contrerail sur file intérieure (voir dessin TV n°805)

MÉTRO DE MEXICO

LIGNE N° 1 TERMINUS "ZARAGOZA"

Echelle	POSE DE CONTRERAILS AU DROIT D'UNE COUPURE DE BARRE DE GUIDAGE ET DE PRISE DE COURANT	DATE : 17 Avril 1970
0,1		DESS : ESTEVE . J .
0,5	CONTRERAIL	VER : Traisnel

L'Ingénieur en Chef

L'Ingénieur Chef de Division

MODIFICATIONS

I.S.T.M.E

S.O.F.R.E.T.U S.G.T.E

TV 813