TU-820

2

CONTRERAIL COURBE DE 11,00m SUR FILE PETIT RAYON

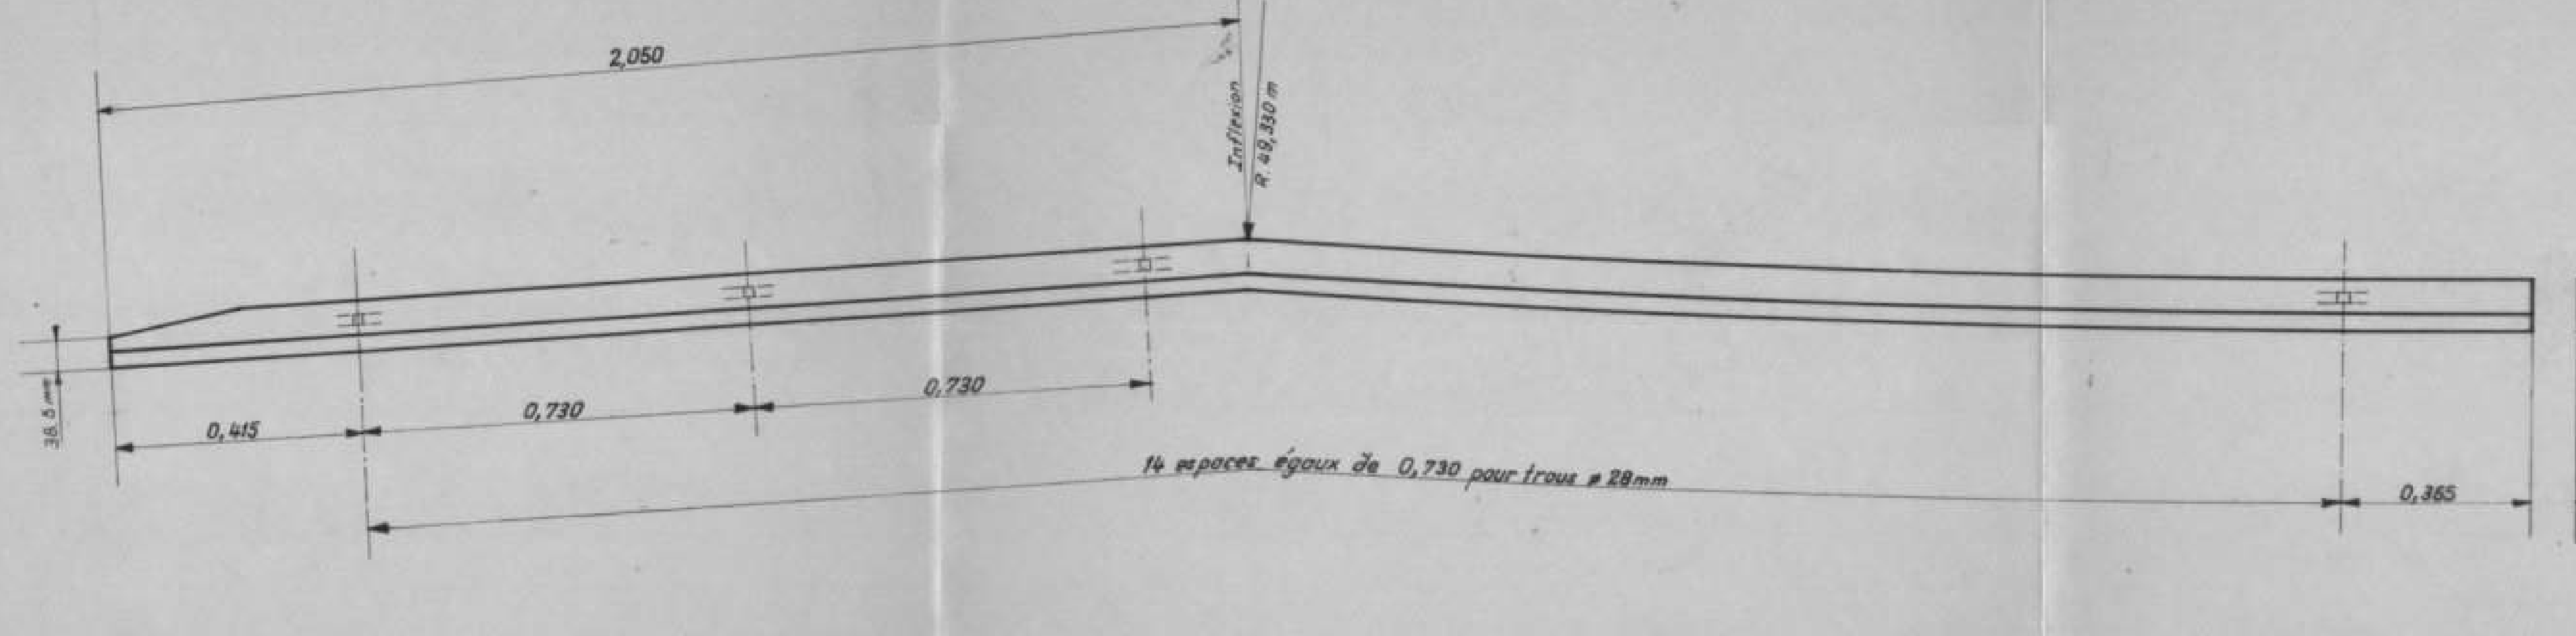

CONTRERAIL COURBE DE 11,00m SUR FILE PETIT RAYON

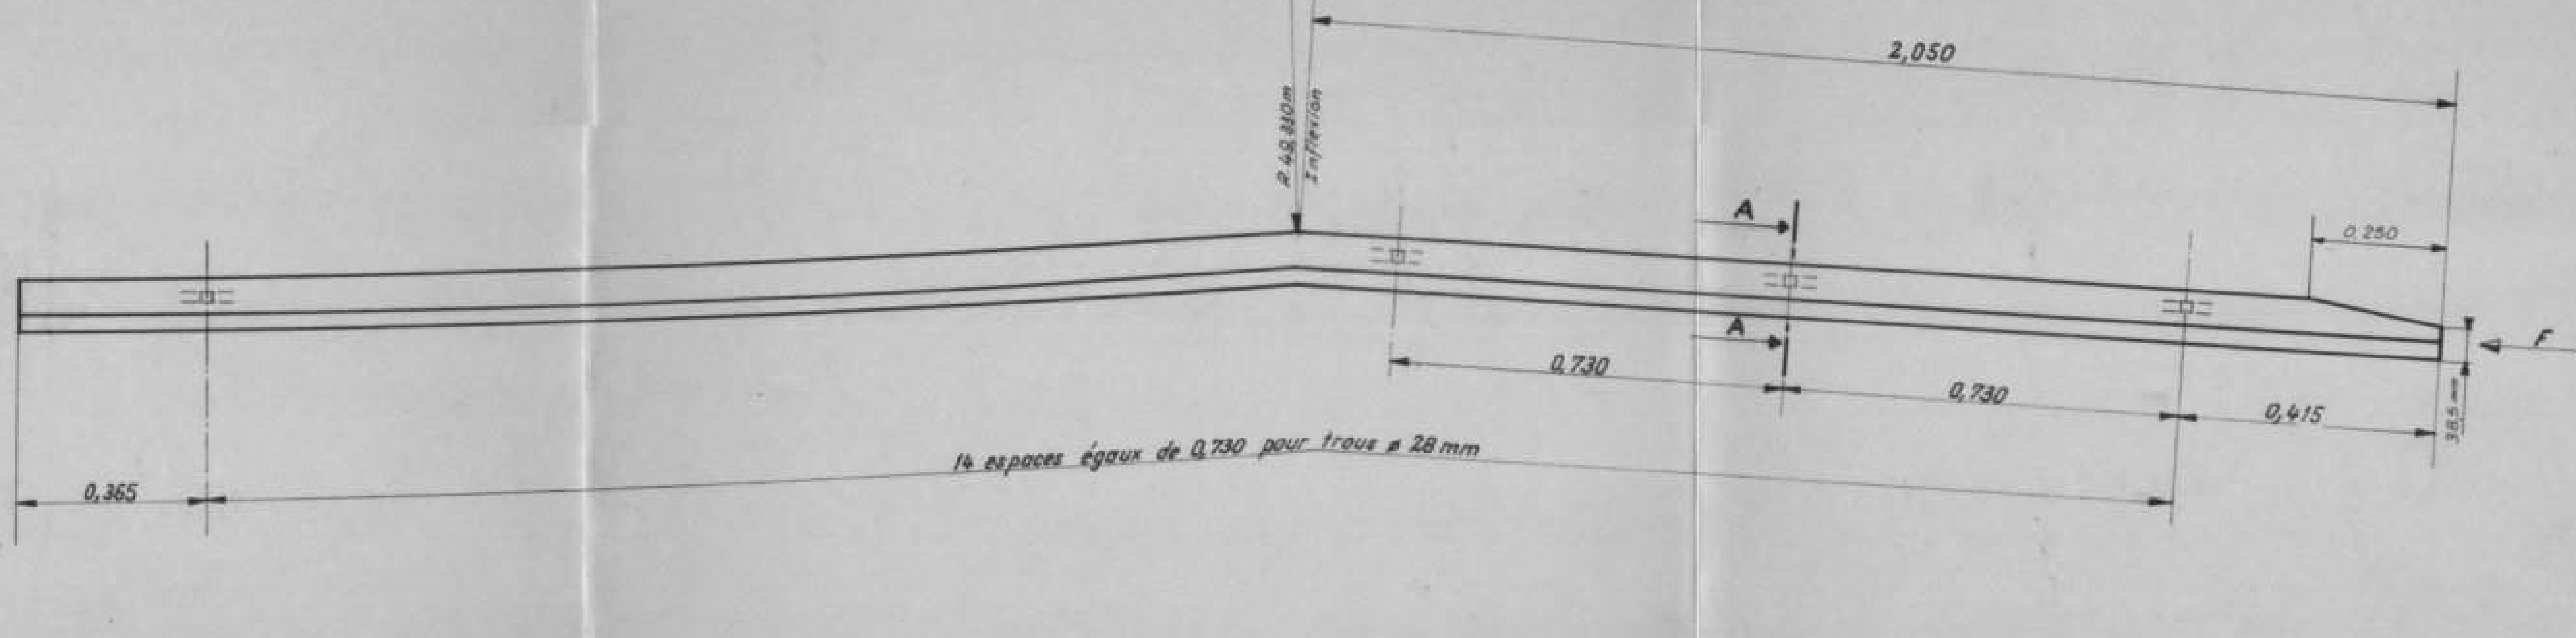

CONTRERAIL COURBE DE 18,00m SUR FILE GRAND RAYON

SCHÉMA D'INFLEXION DES CONTRERAILS DE 11m

_1 contrerail conforme au schéma
_1 contrerail symétrique au schéma

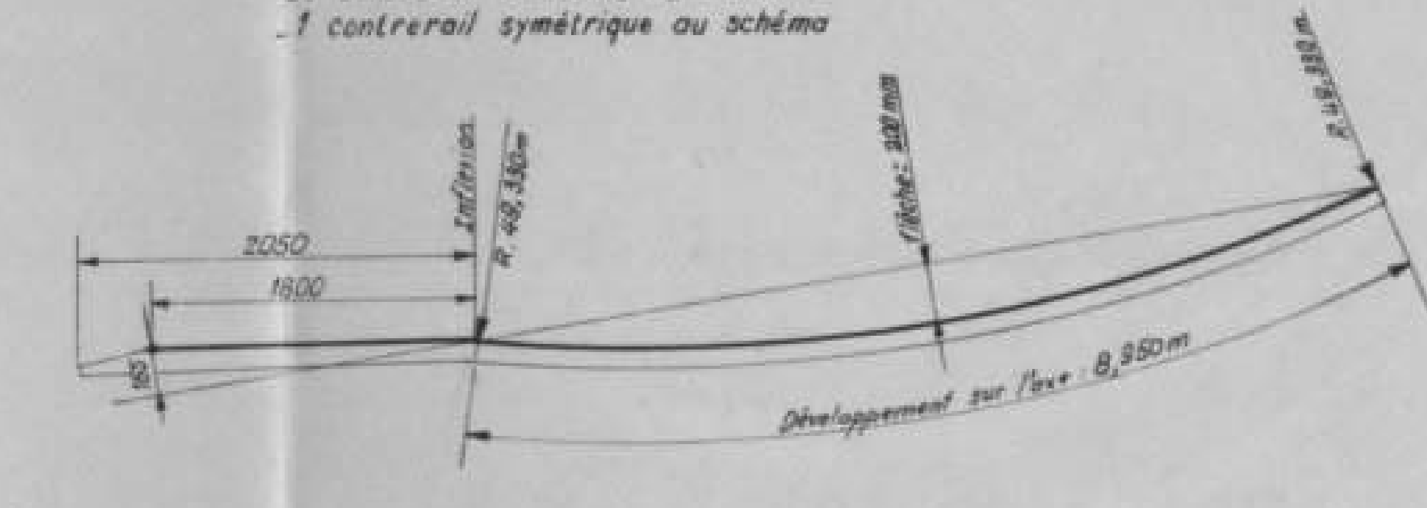

SCHÉMA D'INFLEXION DU CONTRERAIL SUR FILE GRAND RAYON

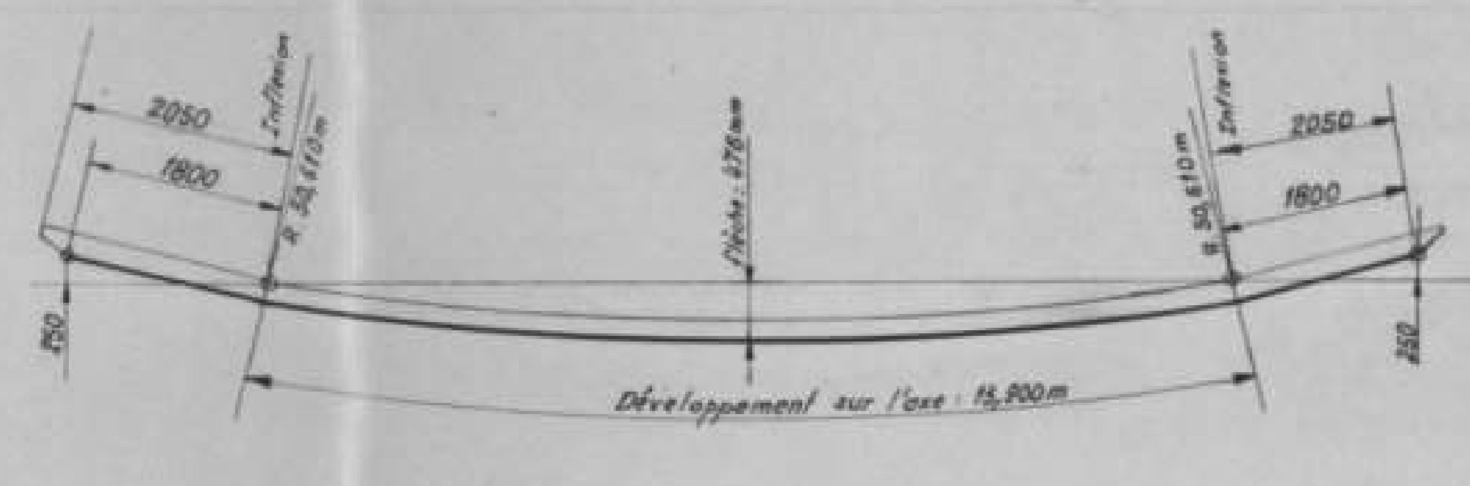

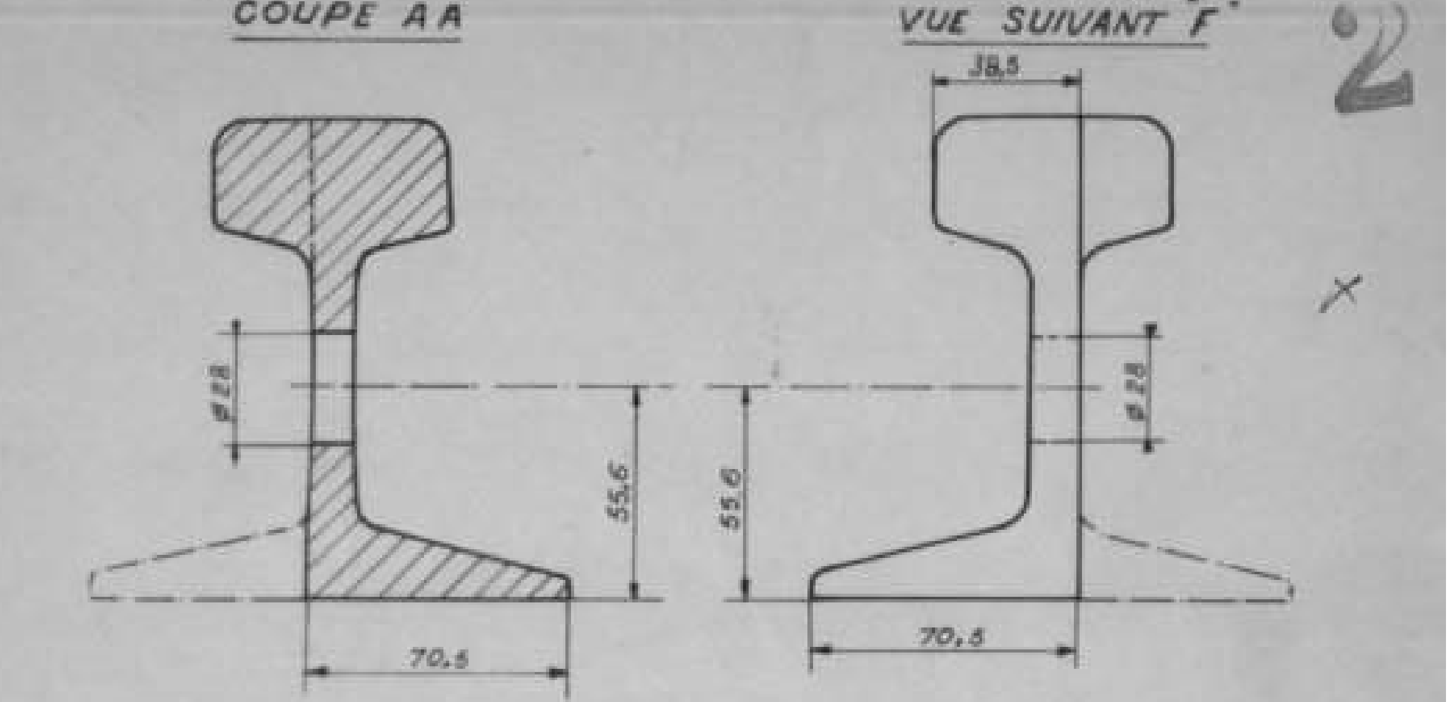

METRO DE MEXICO
RACCORDEMENT ENTRE LES LIGNES N°s 1 et 2
Station PINO-SUAREZ

Échelle	POSE DE CONTRERAILS AU DROIT D'UNE COUPURE DE BARRE DE GUIDAGE ET DE PRISE DE COURANT EN TALON DE L'APPAREIL N°13 SUR LA LIGNE N°1 CONTRERAILS	DATE : 29 Avril 1970 DESS : ESTÈVE J. VER : FRANÇOIS
0,1 0,5		

L'Ingénieur en Chef

L'Ingénieur
Chef de Division

MODIFICATIONS

I.S.T.M.E
S.O.F.R.E.T.U S.G.T.E
TV 820