METRO DE MEXICO


TERMINAL OBSERVATORIO

CORTES DE BARRA GUIA

PARA CRUCETAS

SOBRE VIA "C"

PARA PASO DE PEATONES

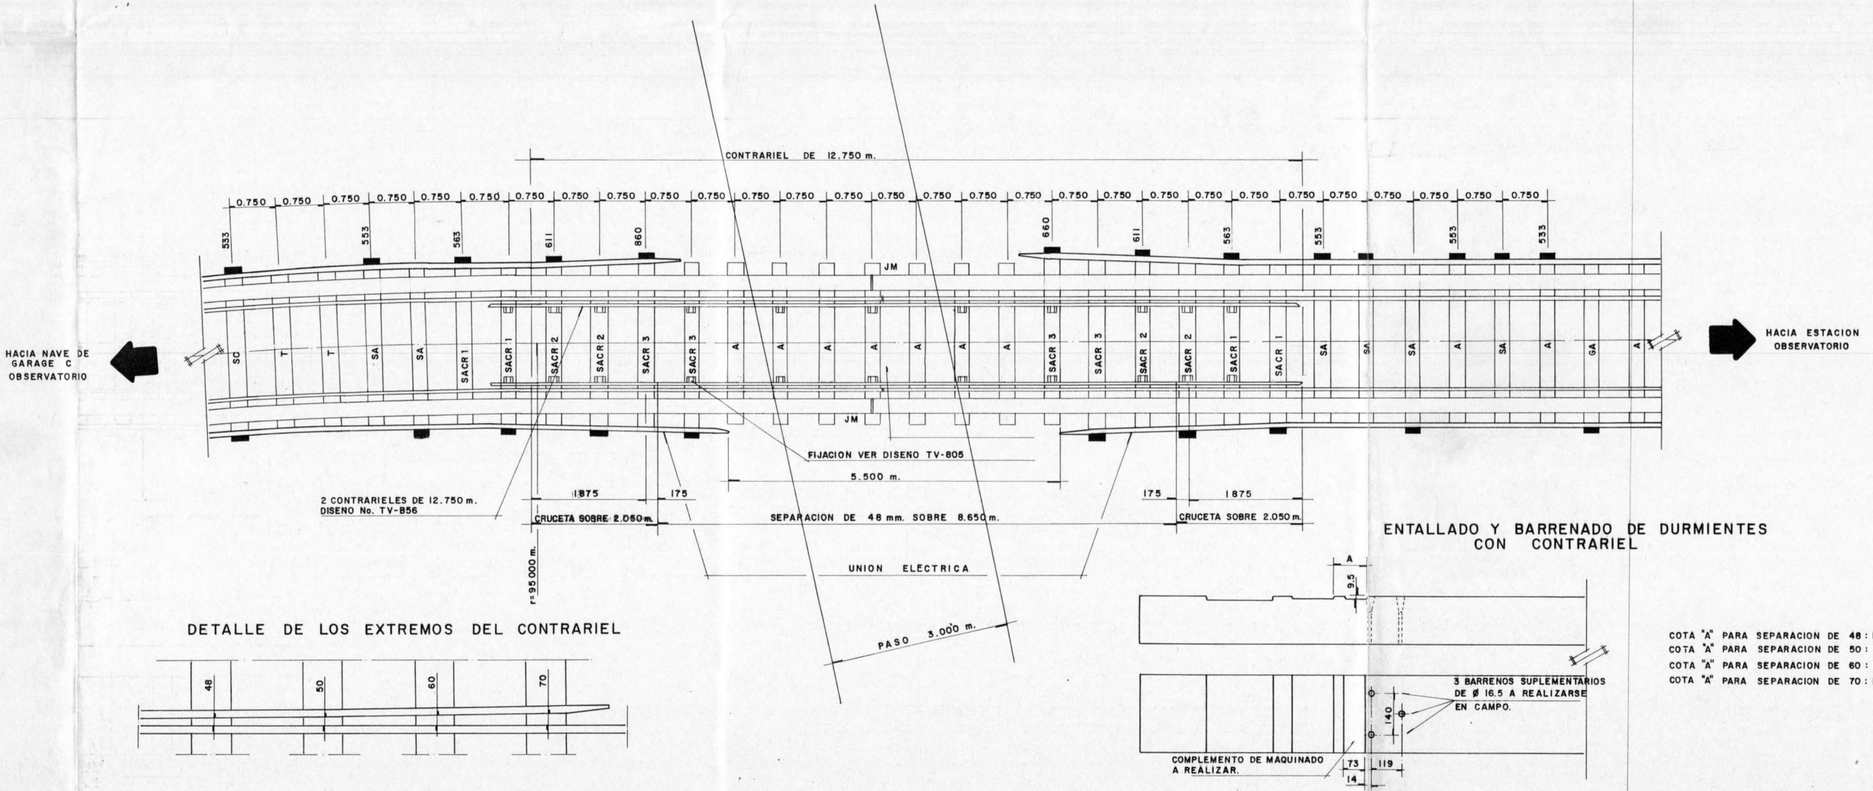

DETALLE DE LOS EXTREMOS DEL CONTRARIEL

ENTALLADO Y BARRENADO DE DURMIENTES CON CONTRARIEL

COTA "A" PARA SEPARACION DE 48 : 116
COTA "A" PARA SEPARACION DE 50 : 118
COTA "A" PARA SEPARACION DE 60 : 128
COTA "A" PARA SEPARACION DE 70 : 138

TV-856