TV-857 LR

RÉGIE AUTONOME DES TRANSPORTS PARISIENS
DIRECTION DES SERVICES TECHNIQUES
SERVICE DE LA VOIE

6

METRO DE MEXICO

TERMINUS OBSERVATORIO


COUPURES DE BARRE CORNIÈRE
PAR CROSSETTES
SUR VOIE D

POUR PASSAGE DU CHEMINEMENT


Echelle: 0,2

Paris le 6.8.1970
l'Ingénieur en Chef
Chef du Service de la Voie


V. 857

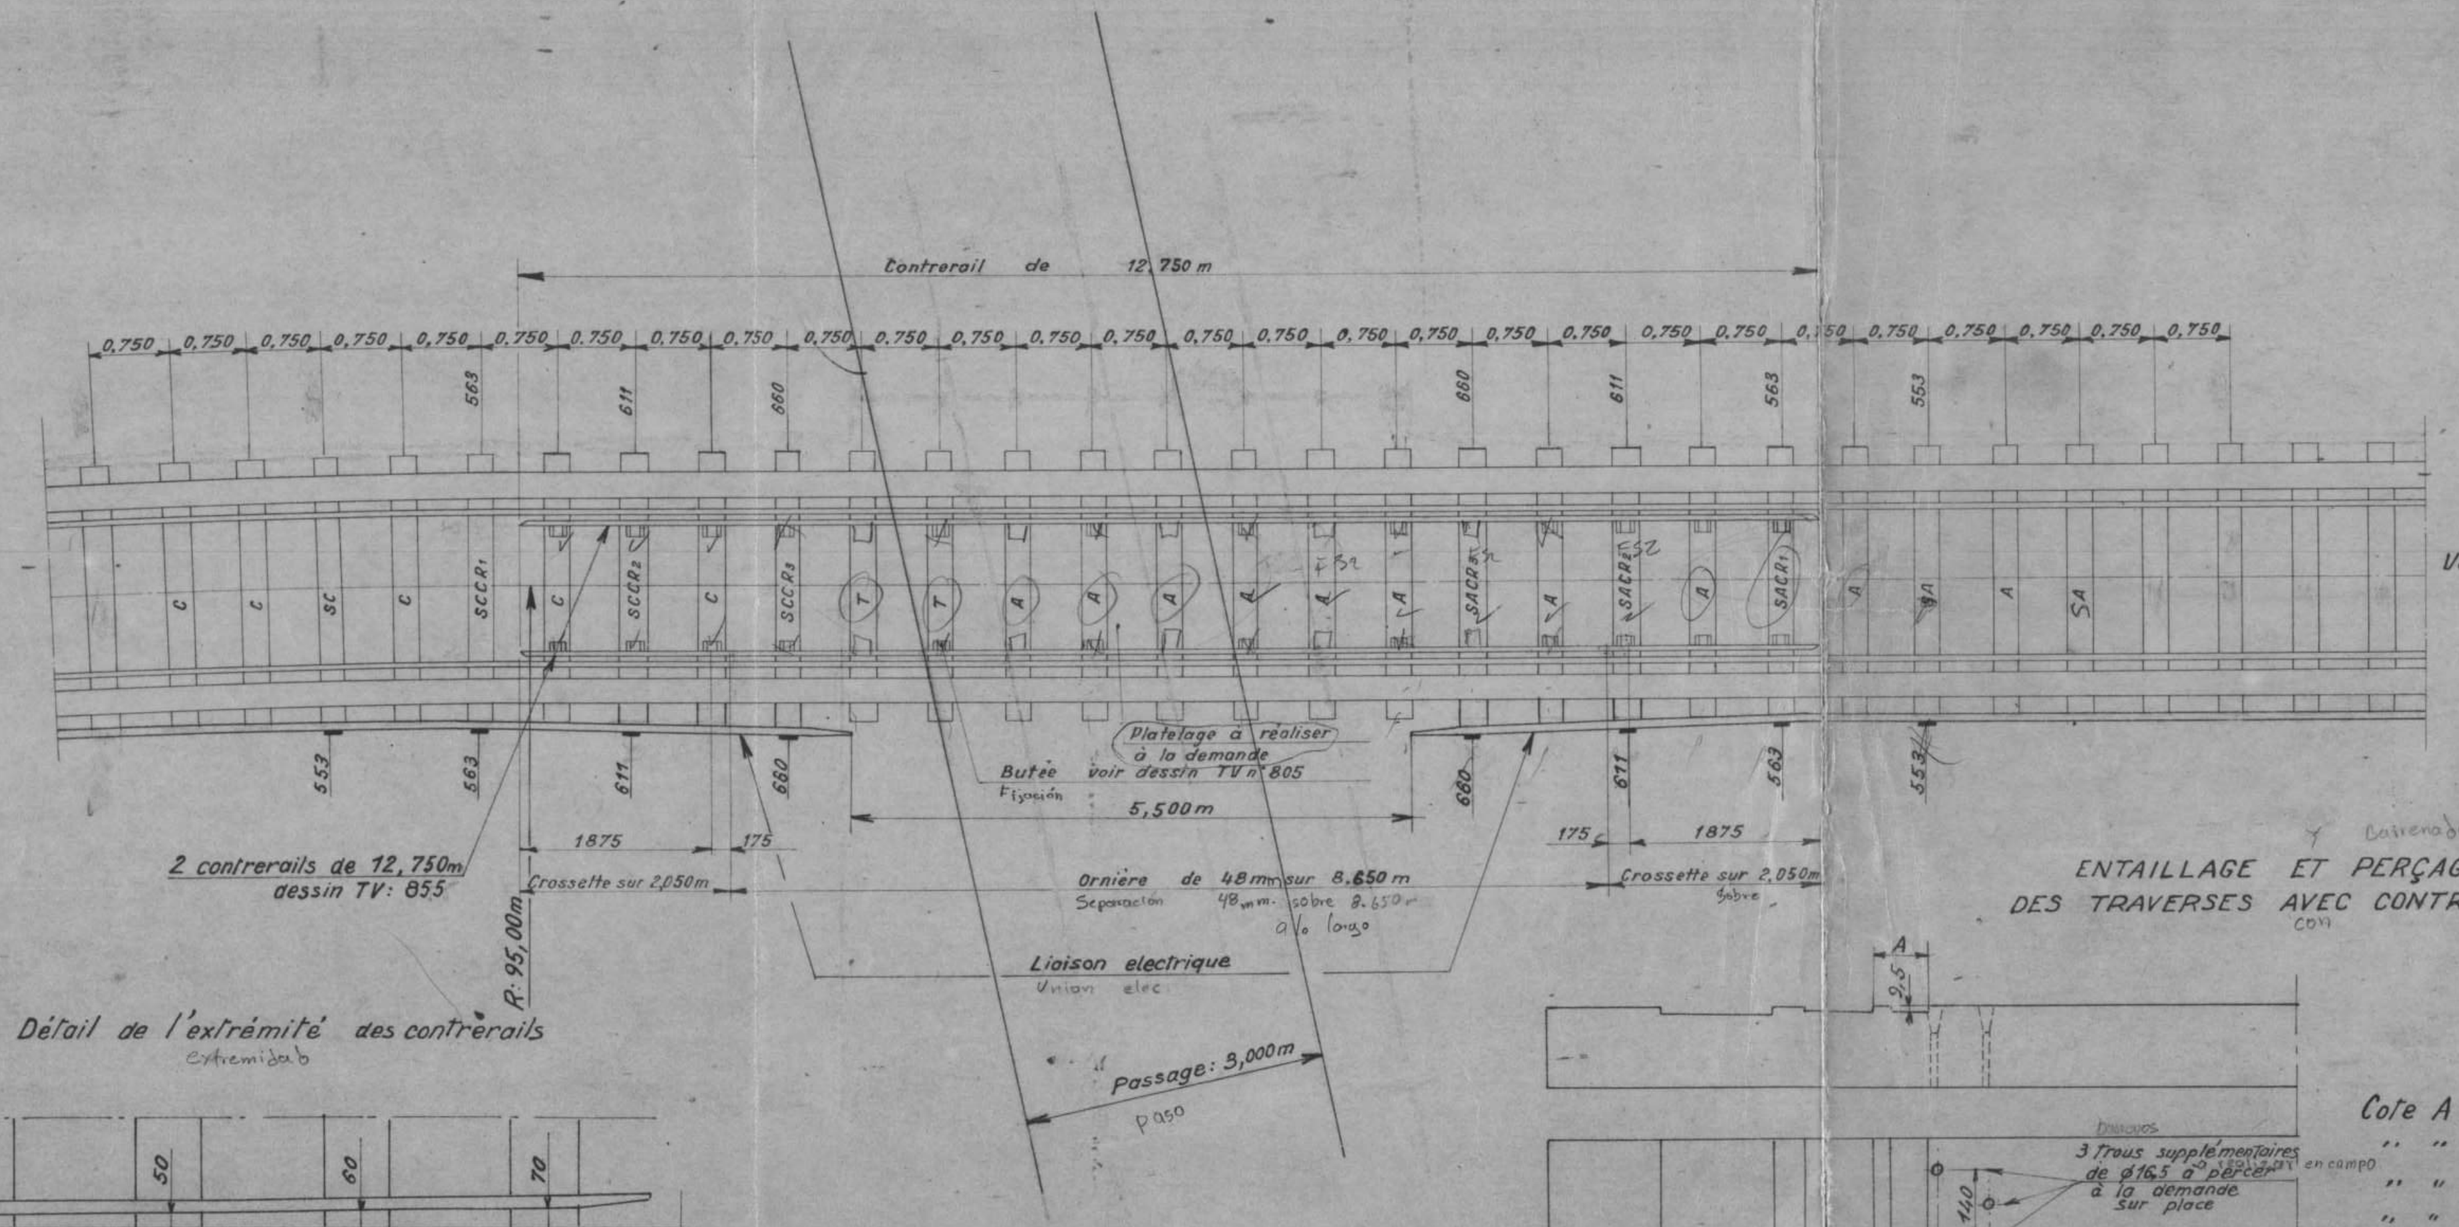

Détail de l'extrémité des contrerails

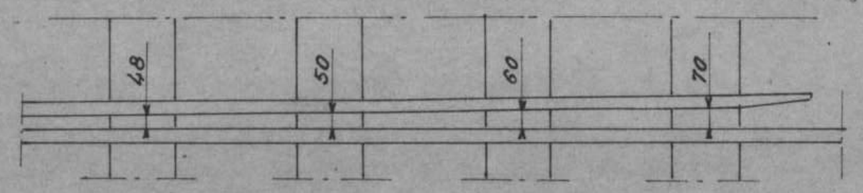

ENTAILLAGE ET PERÇAGE DES TRAVERSES AVEC CONTRERAIL

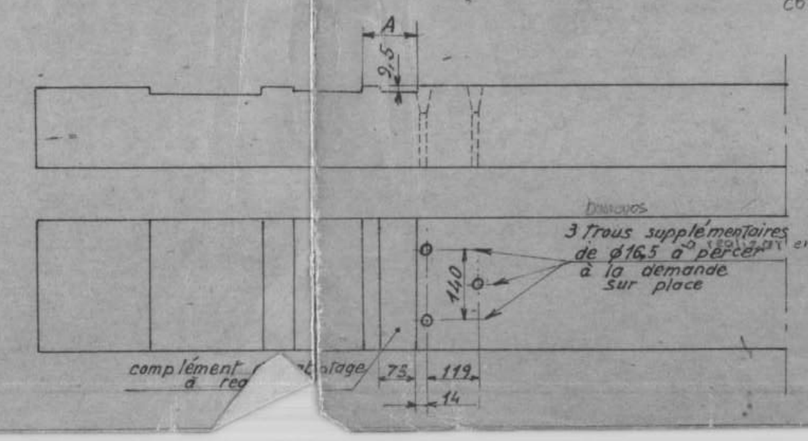

Cote A pour ornière de 48 : 116
" " " " de 50 : 118
" " " " de 60 : 128
" " " " de 70 : 138