NOTE A L'ATTENTION DU CONSTRUTEUR DES APPAREILS DE VOIE

_ DANS LES APPAREILS 6011 (COTÉ VOIE DIRECTE) ET 6012, 6013, 6014 (COTÉ VOIE DÉVIÉE) LES TÊTES DES TRAVERSES N° 1 ET N° 2 SERONT A COUPER A 0,500M. DU BORD DE ROULEMENT DE LA PIÈCE MOULÉE.

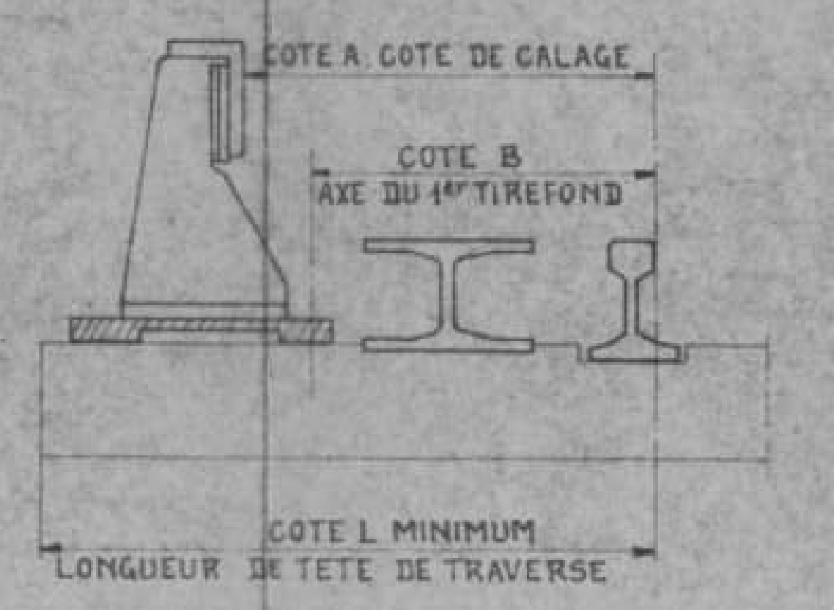

MISE EN PLACE DES CROSSETTES ET DES BARRES LATÉRALES AU DROIT DES APPAREILS DE VOIE

NUMEROS DES APPAREILS	VOIE	TYPE DE CROSSETTE	TRAVERSES UTILISÉES	COTE A	COTE B	COTE L MINIMUM	OBSERVATIONS
6011	DIRECTE	CROSSETTE DE GAUCHE DESSIN TV 353	6 9	652 590	558 496	970 907	
6012	DÉVIÉE	SYMETRIQUE AU PLAN TV 374	9 12 15	652 575 565	558 484 471	970 892 882	
6013	DÉVIÉE	SYMETRIQUE AU PLAN TV 374	9 12 15	652 575 565	558 484 471	970 892 882	
6014	DÉVIÉE	SYMETRIQUE AU PLAN TV 374	9 12 15	652 575 565	558 481 471	970 892 882	

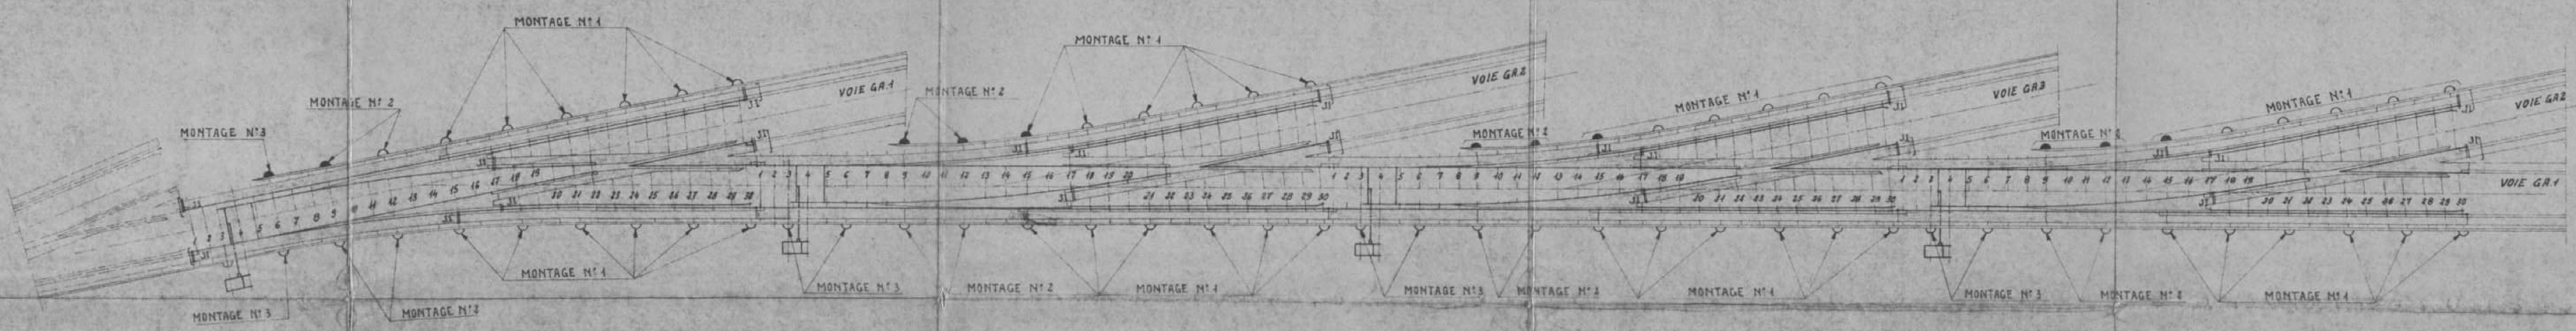

606

TV-877 2

6011
MANŒUVRE PAR MOTEUR

6012
MANŒUVRE PAR MOTEUR

6013
MANŒUVRE PAR MOTEUR

6014
MANŒUVRE PAR MOTEUR

MATÉRIEL AJOUTÉ

N° DES APPAREILS	PIÈCES AJOUTÉES
6011	5 JOINTS ISOLANTS DE RAIL 3 JOINTS ISOLANTS DE PISTE_END-POST DE 140 3 JOINTS ISOLANTS DE PISTE_END-POST DE 150 1 JOINT ISOLANT DE RAIL ET DE CONTRERAIL.
6012	3 JOINTS ISOLANTS DE RAIL 3 JOINTS ISOLANTS DE PISTE_END-POST DE 140. 1 JOINT ISOLANT DE PISTE_END-POST DE 150. 1 JOINT ISOLANT DE RAIL ET DE CONTRERAIL.
6013	3 JOINTS ISOLANTS DE RAIL 3 JOINTS ISOLANTS DE PISTE_END-POST DE 140 1 JOINT ISOLANT DE PISTE_END-POST DE 150. 1 JOINT ISOLANT DE RAIL ET DE CONTRERAIL.
6014	3 JOINTS ISOLANTS DE RAIL 3 JOINTS ISOLANTS DE PISTE_END-POST DE 140. 1 JOINT ISOLANT DE PISTE_END-POST DE 150. 1 JOINT ISOLANT DE RAIL ET DE CONTRERAIL

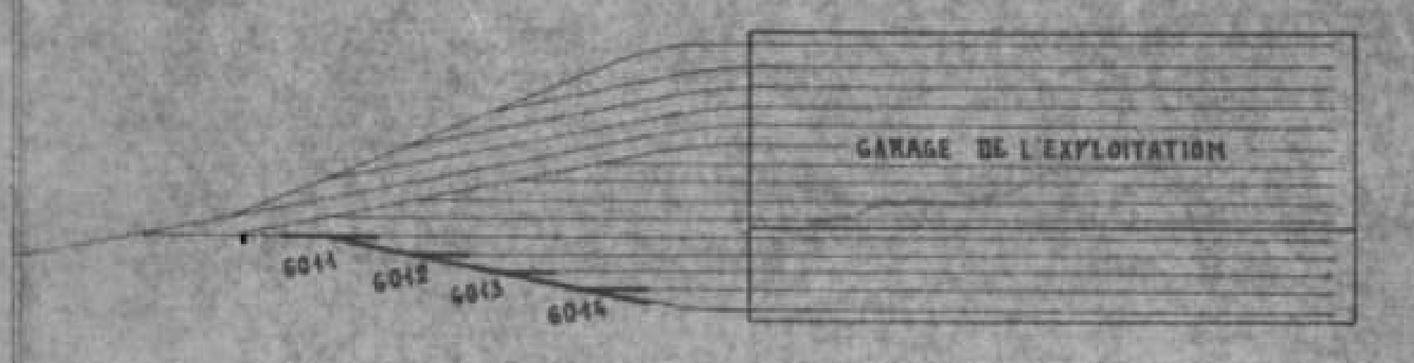

ÉQUIPEMENT TRACTION

_ LES COUPURES SERONT REALISÉES EN UTILISANT, SUIVANT LES CAS 2 TYPES DE CROSSETTES

CROSSETTES RECTILIGNES DE 7,500 M . PLAN TV 353
CROSSETTES COURBES DE 12,000 M . PLAN TV 374

_ L'IMPLANTATION DES CROSSETTES SE FERA EN PLAÇANT LA POINTE DE CHAQUE CROSSETTE A 0,600 M DE LA PREMIÈRE TRAVERSE SUPPORT

ISOLATEUR SUR PLATEAU POUR TÊTE DE TRAVERSE
COTE DE CALAGE A, B, L . VOIR TABLEAU
ISOLATEUR SUR PLATEAU POUR BARRE D'ALIMENTATION
COTE A' 553 _ COTE B 459 _ COTE L 870

RÉFÉRENCES

PLAN DE PIQUETAGE DES VOIES	PLAN TV 251
PLAN D'ENSEMBLE DES BRANCHEMENTS Tg 0,20 A GAUCHE	PLAN TV 189
PLAN D'ENSEMBLE DES BRANCHEMENTS Tg 0,20 A DROITE	PLAN TV 170
MONTAGE DES ISOLATEURS SUR PLATEAU (MONTAGE 1, 2 OU 3)	PLAN TV 60
FIXATION DES MOTEURS SUR TRAVERSES	PLAN TV
JOINTS ISOLANTS . MONTAGES DIVERS.	PLAN TV 126
JOINTS ISOLANTS _ DETAILS	PLAN TV 127
END-POST H 150.	PLAN TV 189.1

METRO DE MEXICO

ÉCH		DATE 26.1.1976
1/100	AGRANDISSEMENT DES ATELIERS DE ZARAGOZA GARAGE DE L'EXPLOITATION PLAN DE POSE DES APPAREILS N° 6011.6012.6013.6014	DESS. R.C VERIF.

S.T.C.
Departamento de Vias
y Estructuras
Seccion de Mantenimiento
de Vias
MODIFICATIONS

Le Responsable Technique

Le Vérificateur

SOFRETU
TV.877