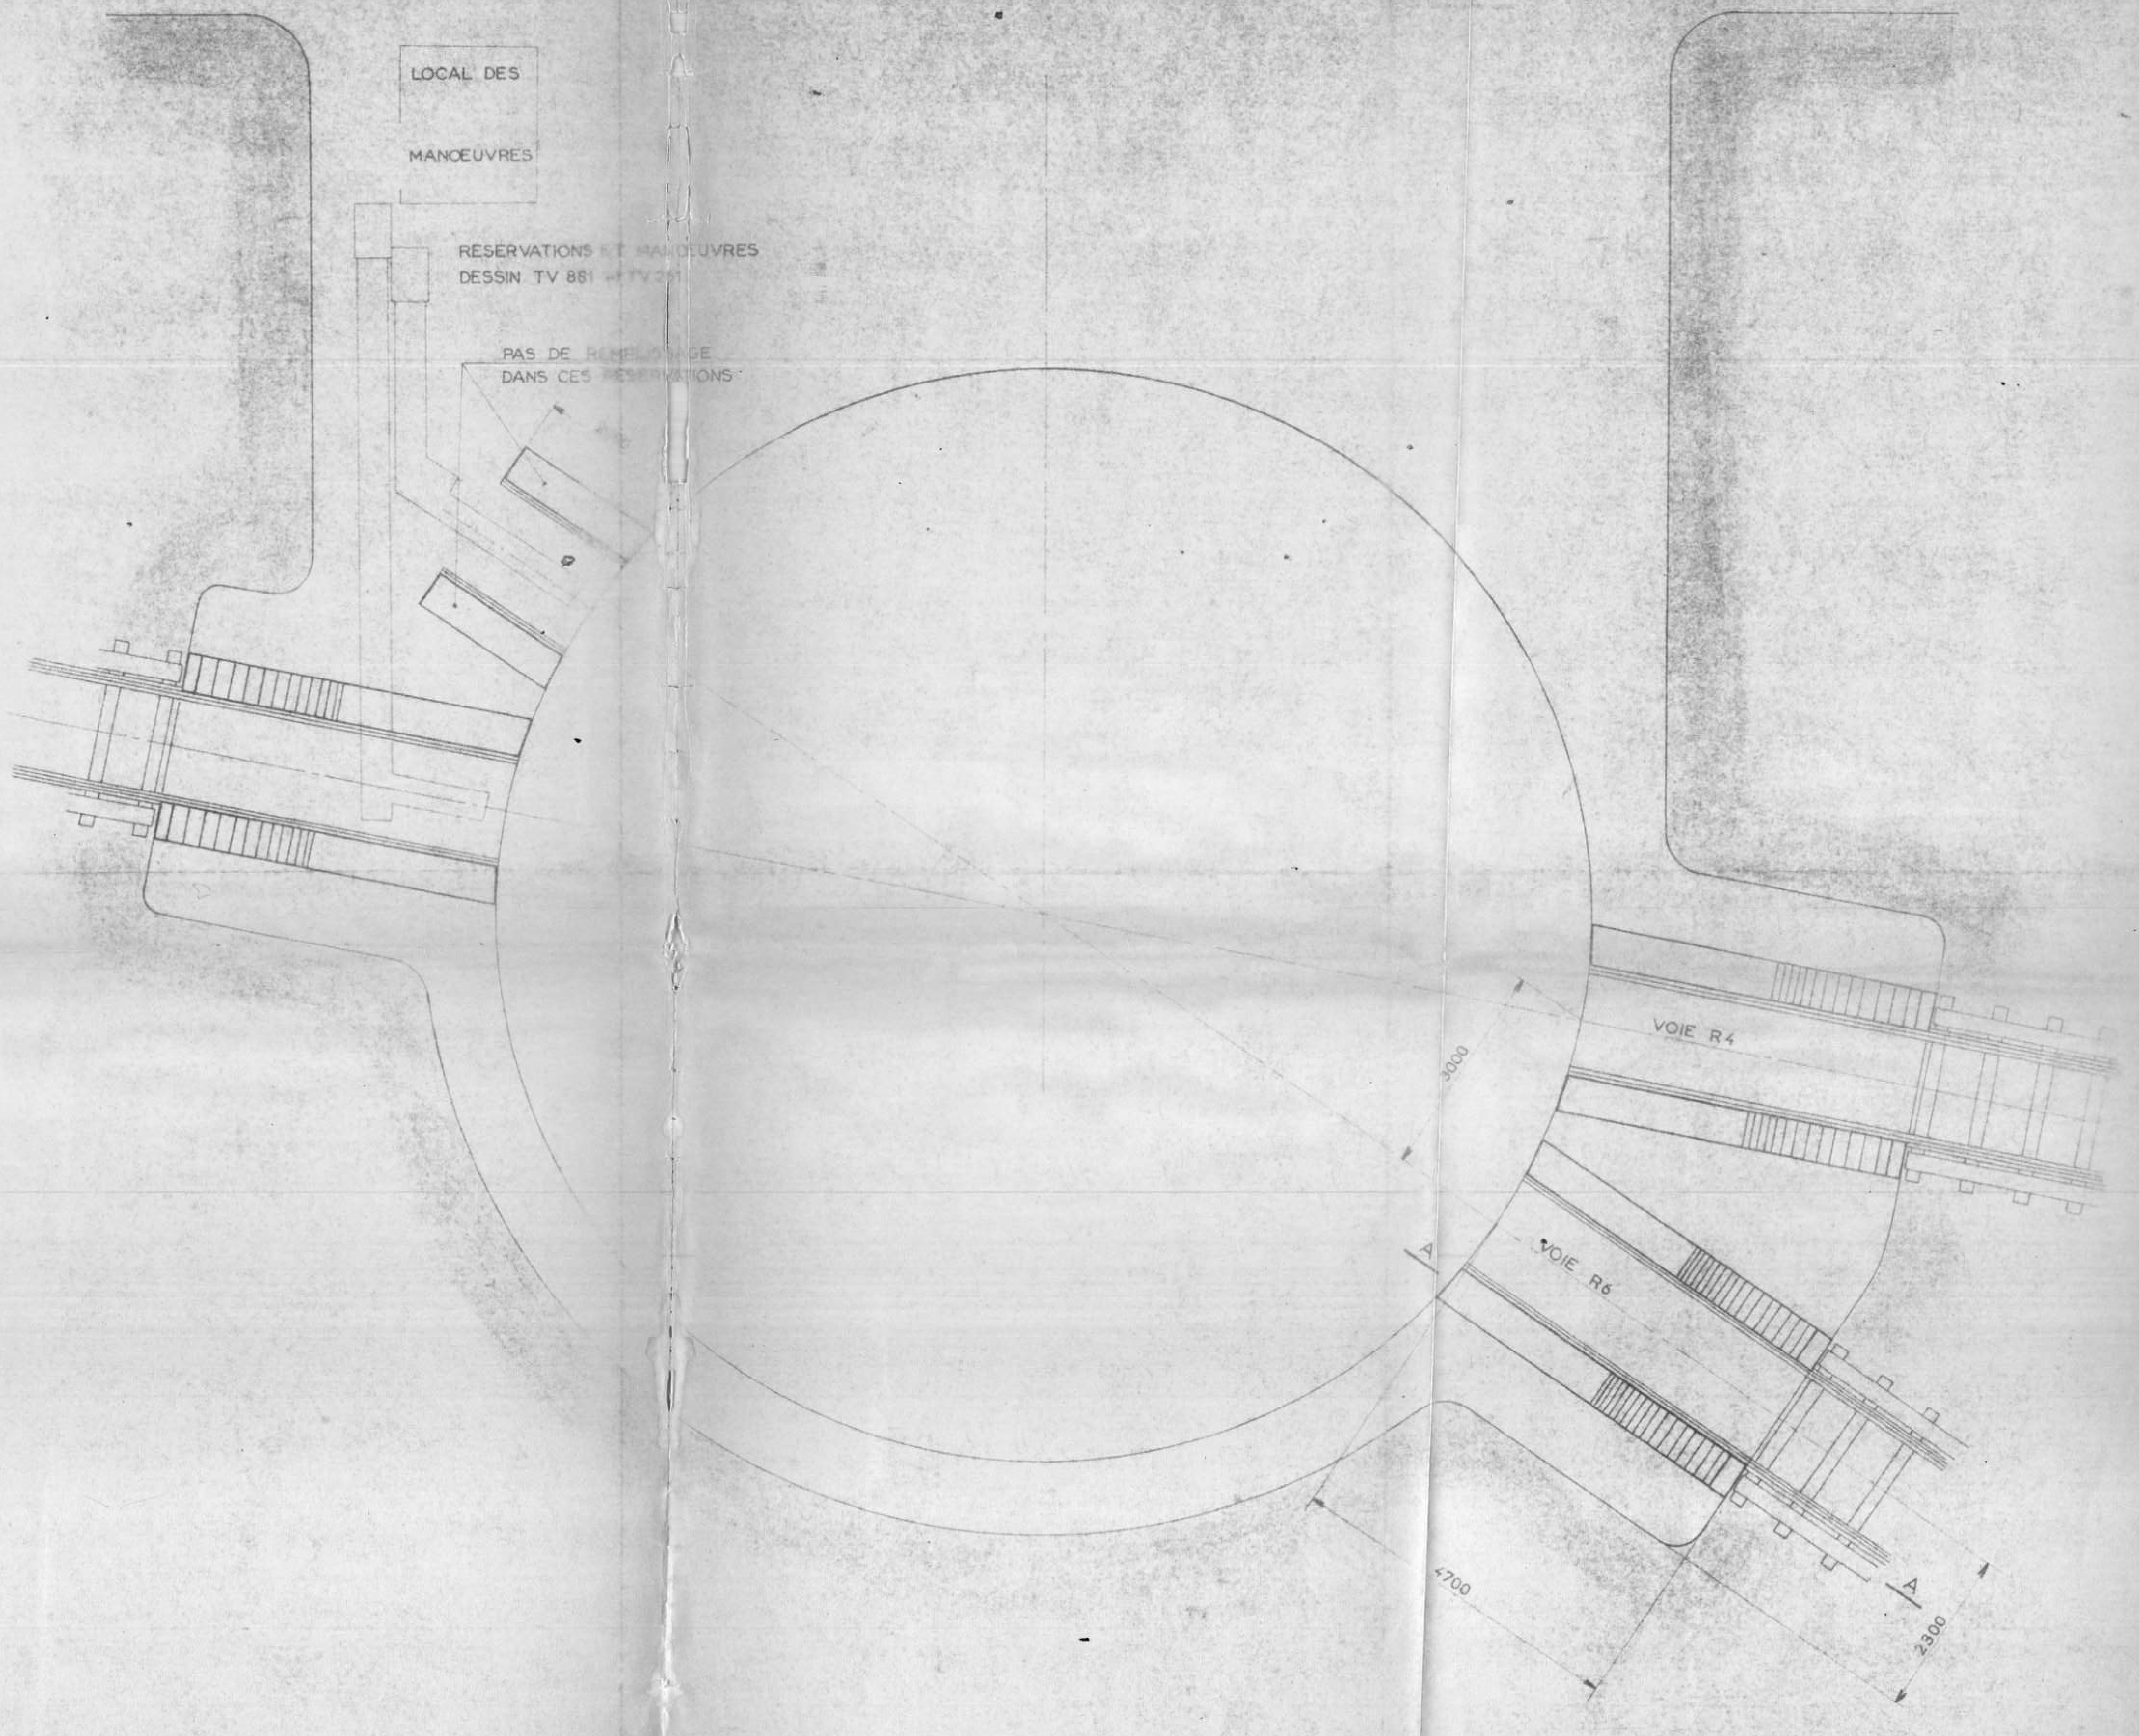

COUPE AA

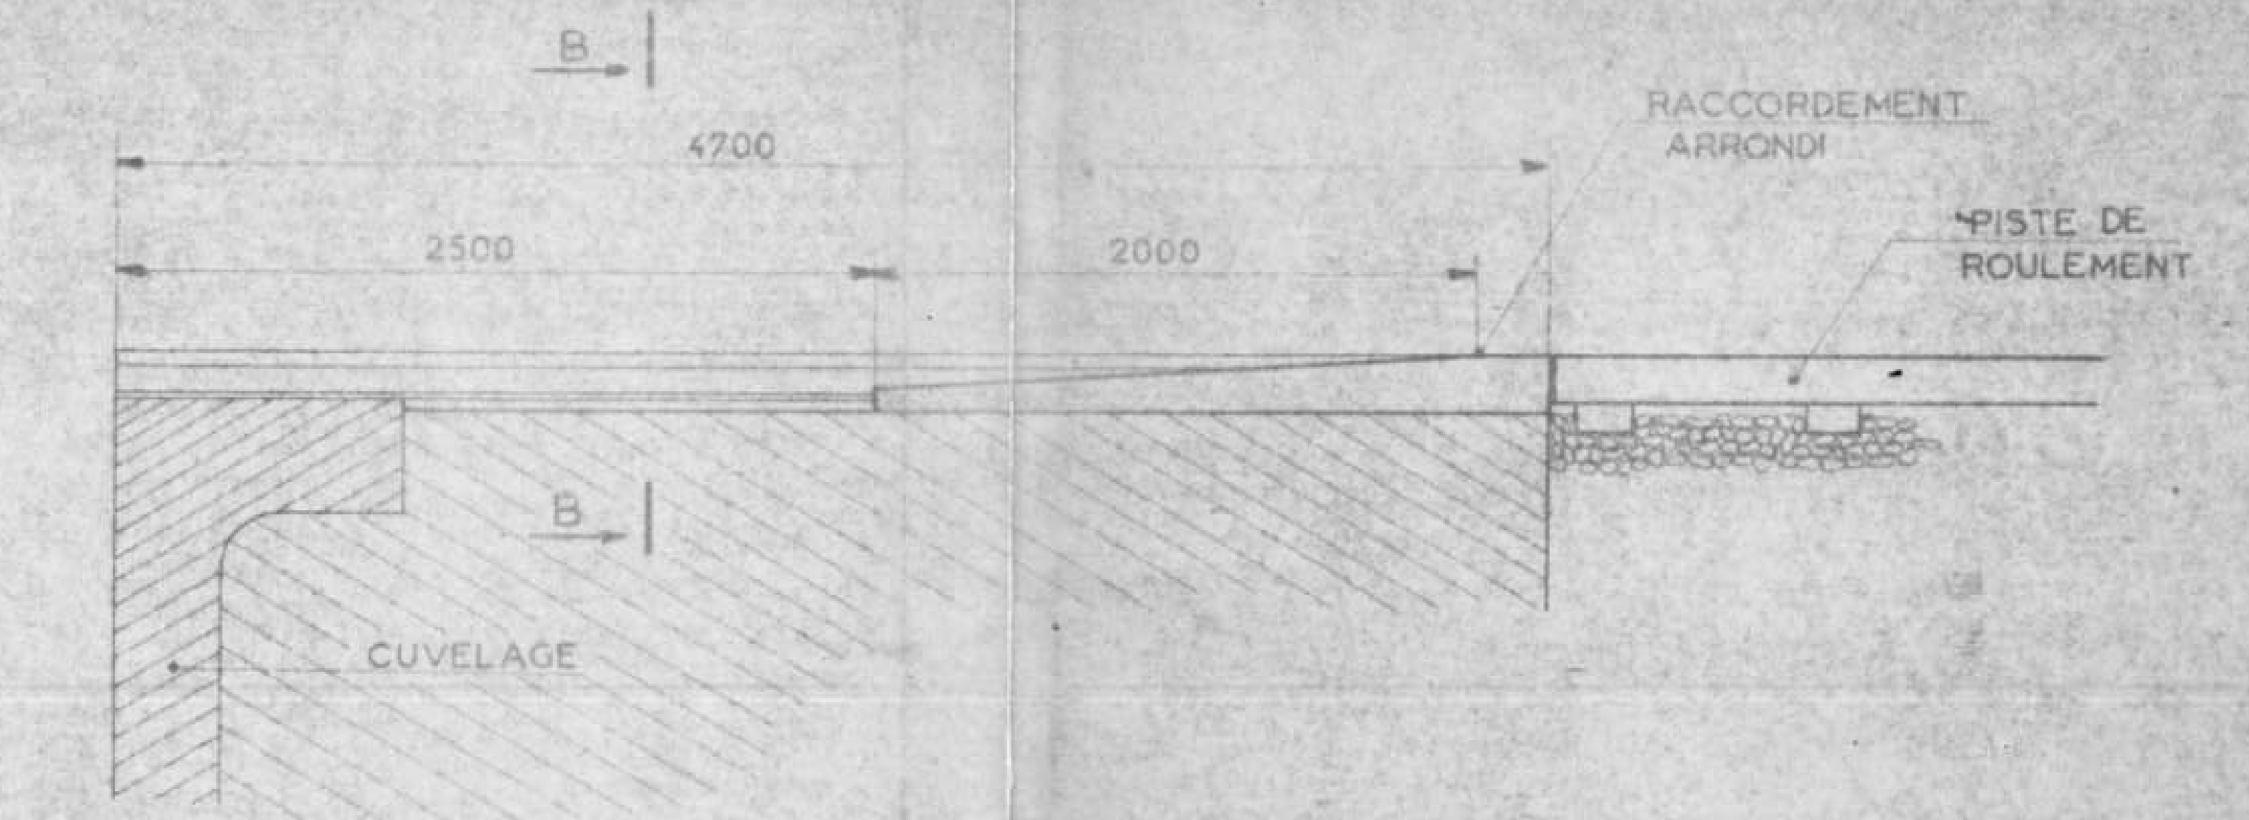

COUPE BB

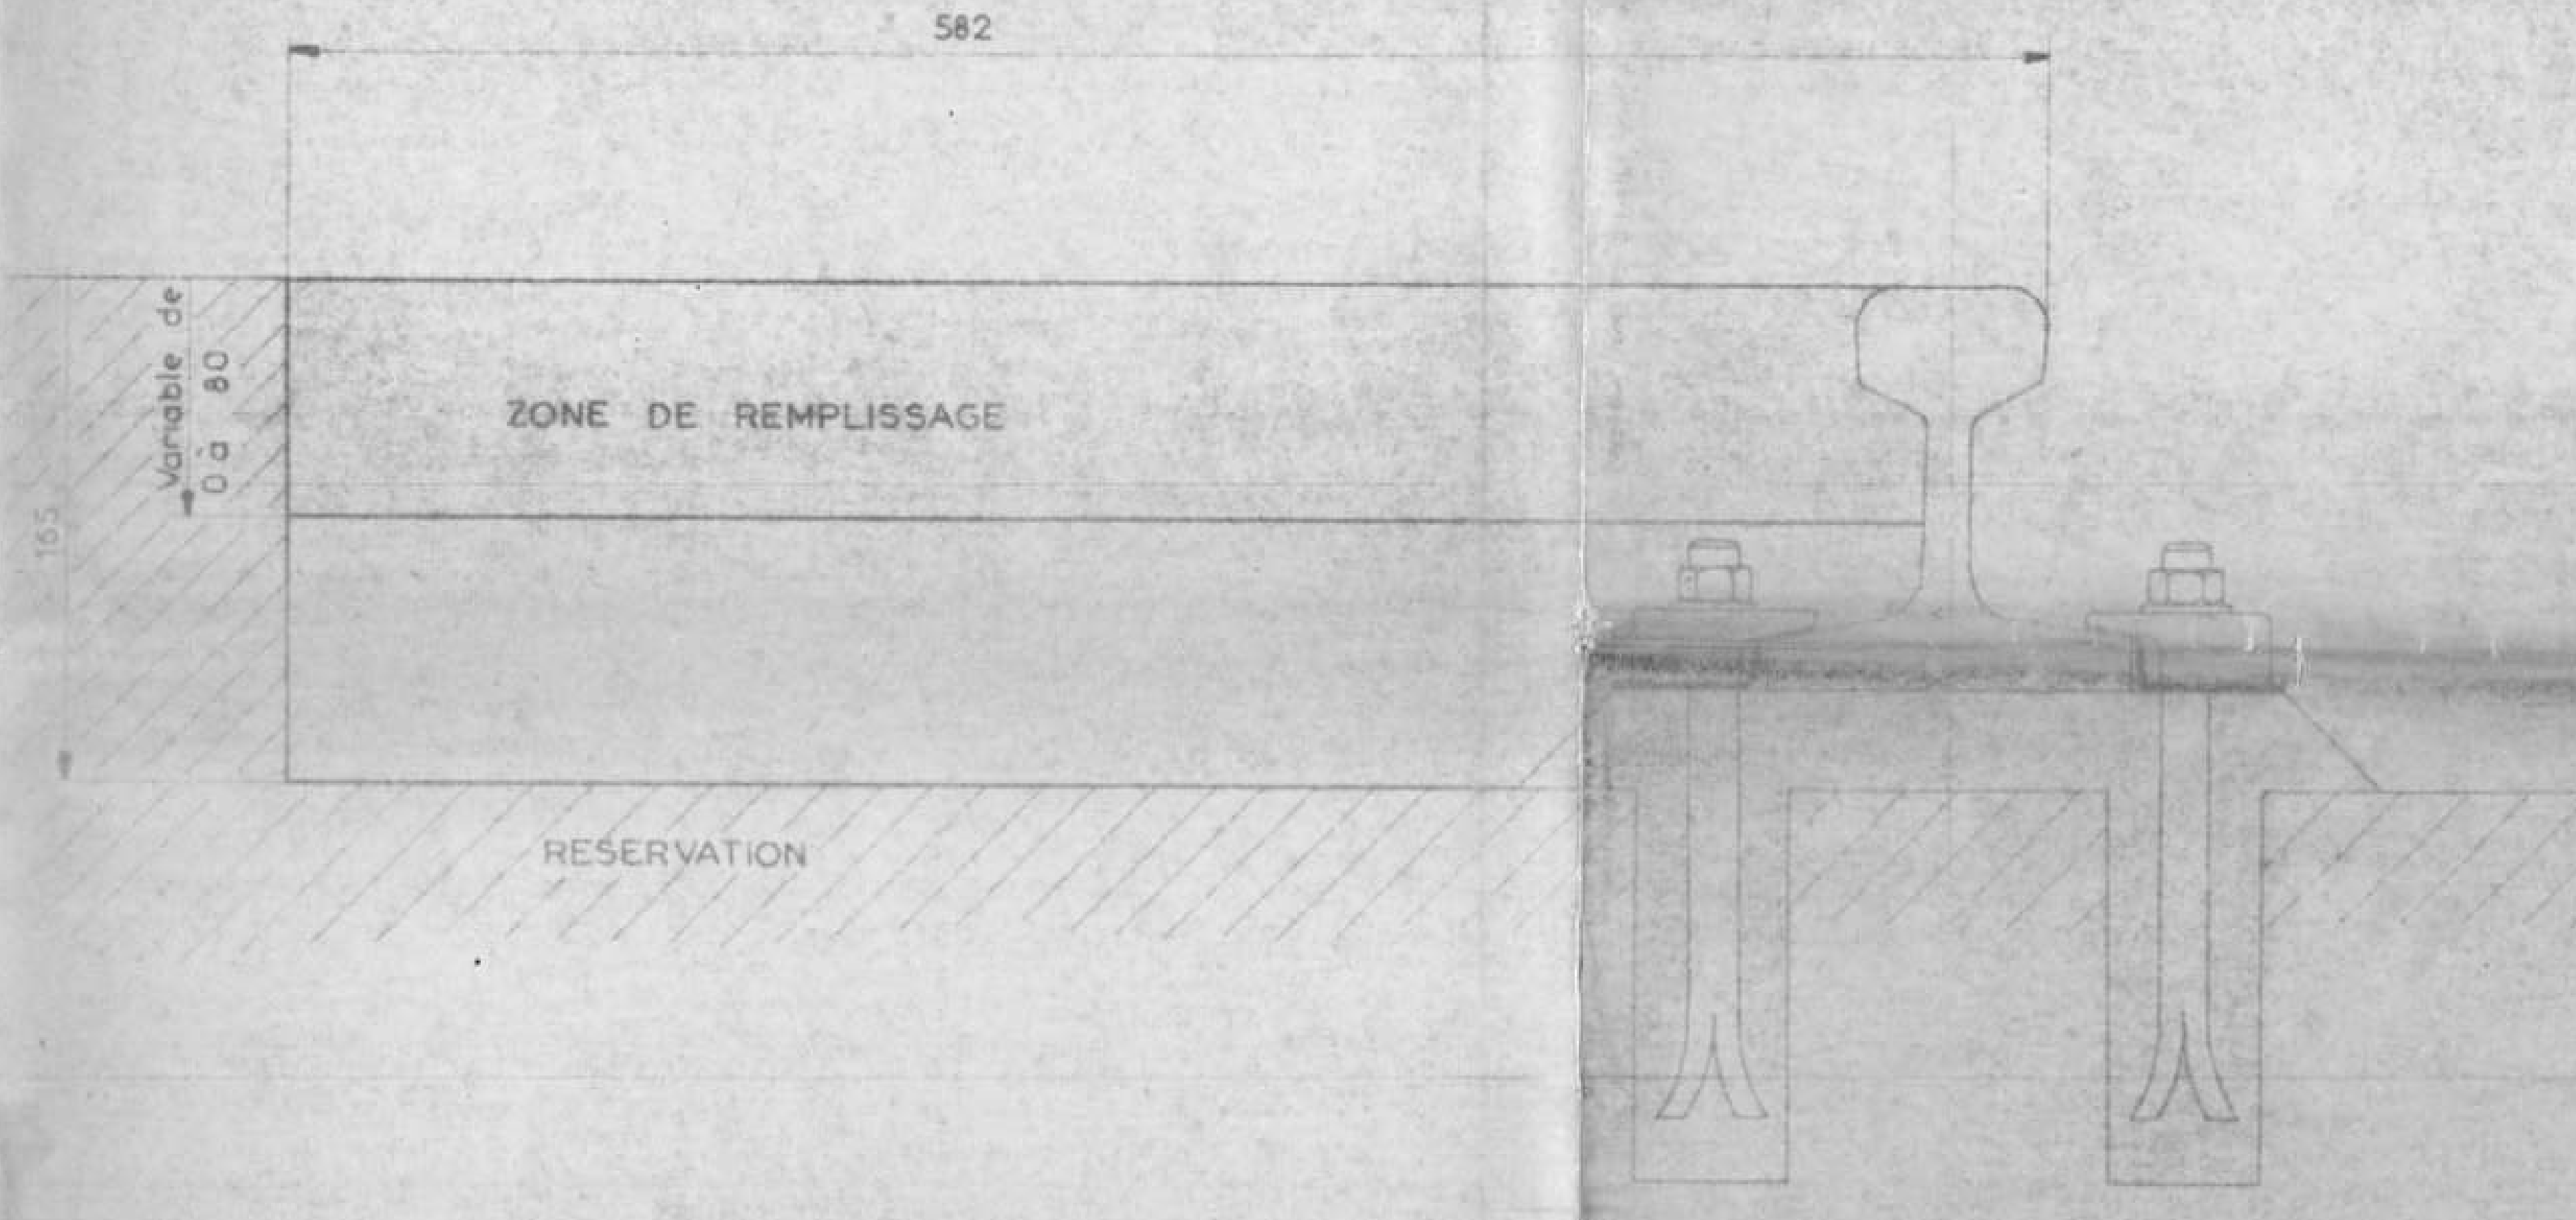

FIXATION DU RAIL SUIVANT DESSIN TV 276

TV-880

6

METRO DE MEXICO

ECH		
0,02 0,04 0,4	AGRANDISSEMENT DES ATELIERS DE ZARAGOZA POSE DE LA VOIE R6 AUX ABORDS DE LA PLAQUE TOURNANTE	DATE 26.1.76 DESS MF VERIF
MODIFICATIONS	Le Responsable technique Auff	Le Vérificateur Haurau
	S.O.F.R.E.T.U. **TV 880**	