COLOCACION DE LA VIA SOBRE DURMIENTE DE MADERA EN ZONA DE BALASTO.

SIN ESCALA

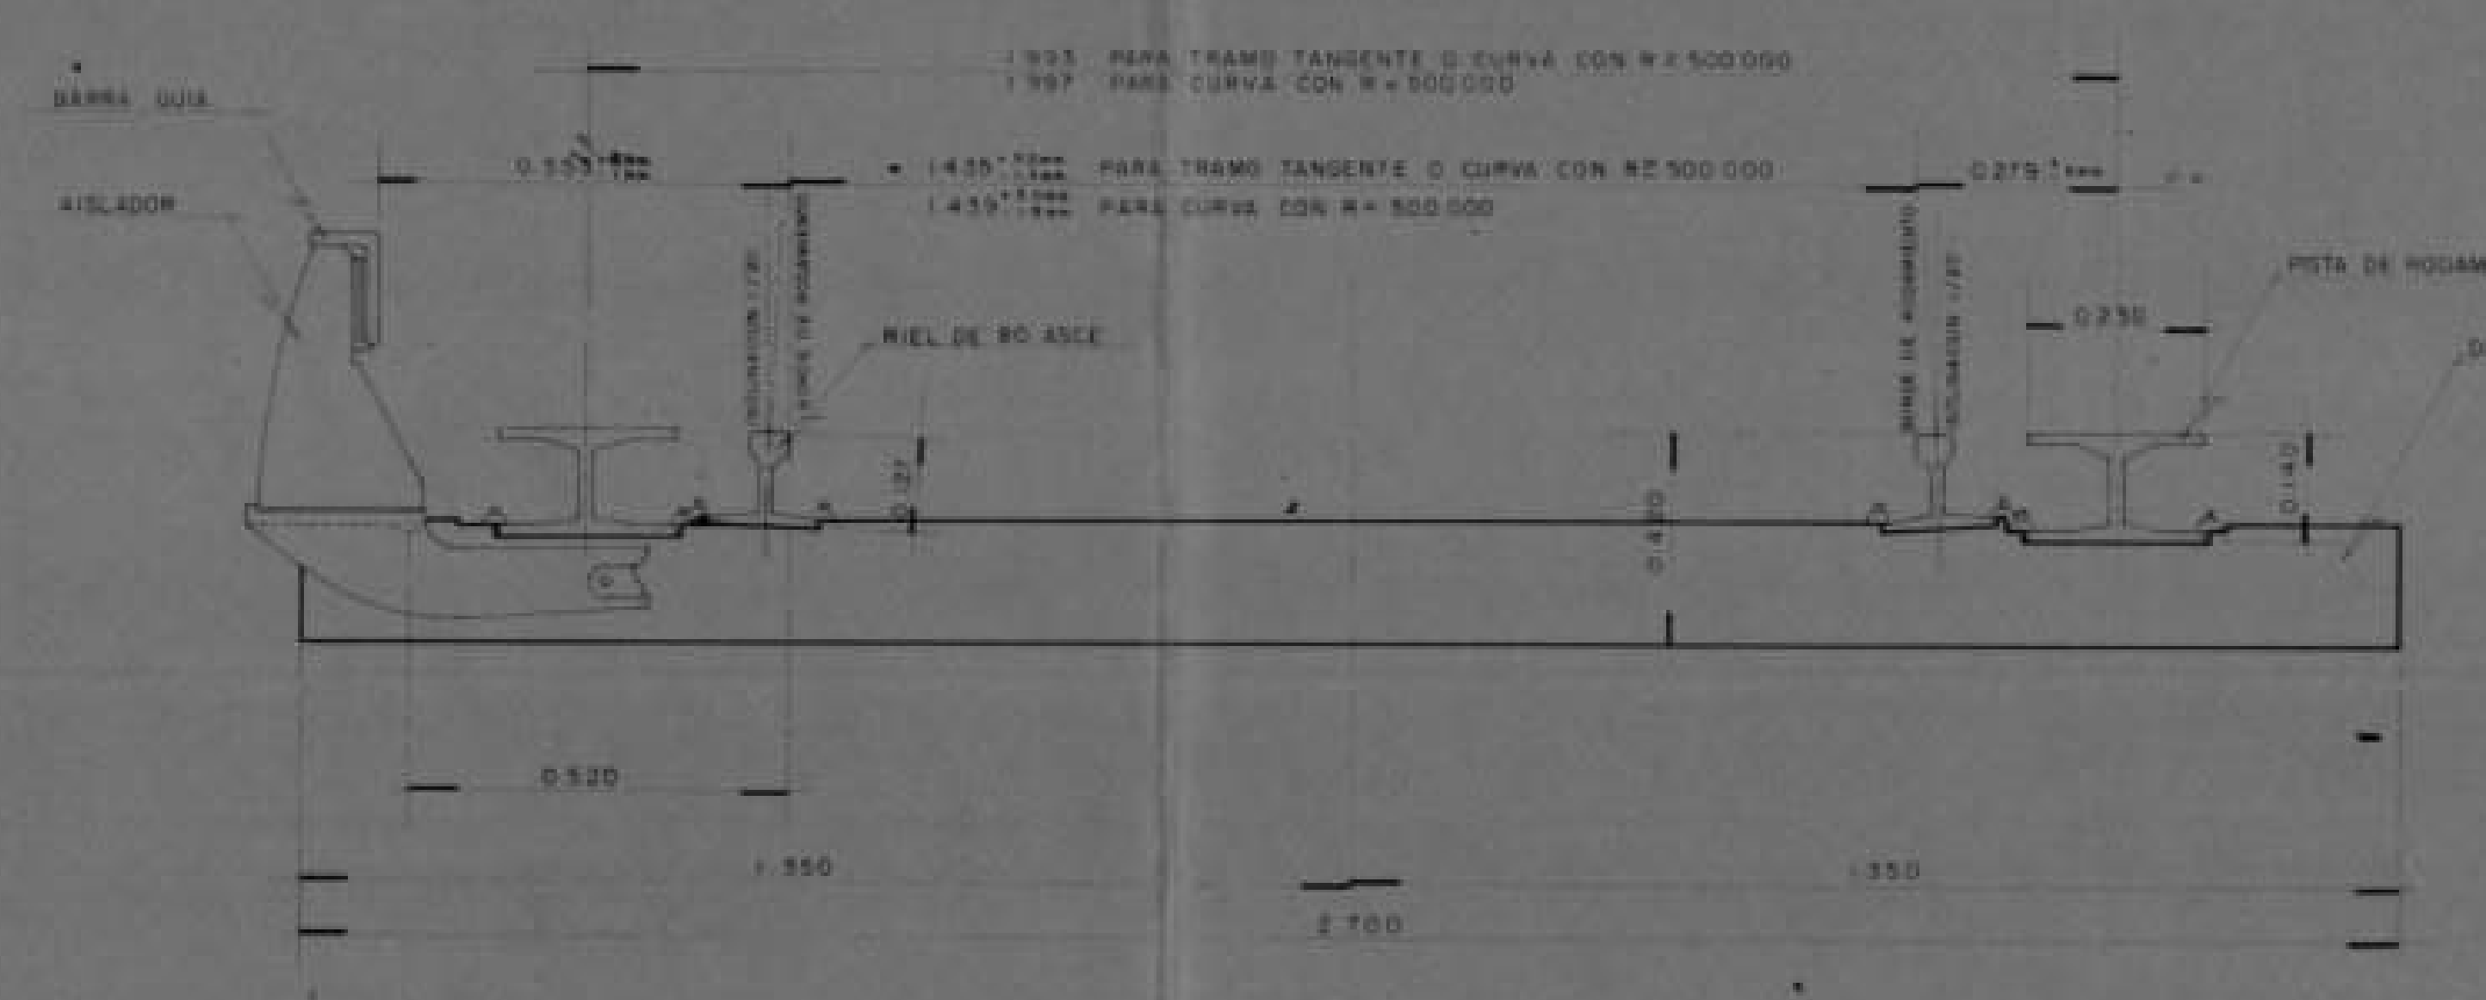
BARRA GUIA
AISLADOR
1.993 PARA TRAMO TANGENTE O CURVA CON R ≥ 500.000
1.997 PARA CURVA CON R < 500.000
0.553
1.435 PARA TRAMO TANGENTE O CURVA CON R ≥ 500.000
1.439 PARA CURVA CON R < 500.000
0.275
RIEL DE 80 ASCE
PISTA DE RODAMIENTO
0.230
DURMIENTE SOPORTE DE AISLADOR
0.127
0.140
0.520
1.350
1.350
2.700

COLOCACION DE LA VIA SOBRE DURMIENTE DE CONCRETO EN ZONA DE BALASTO. (TIPO "O")

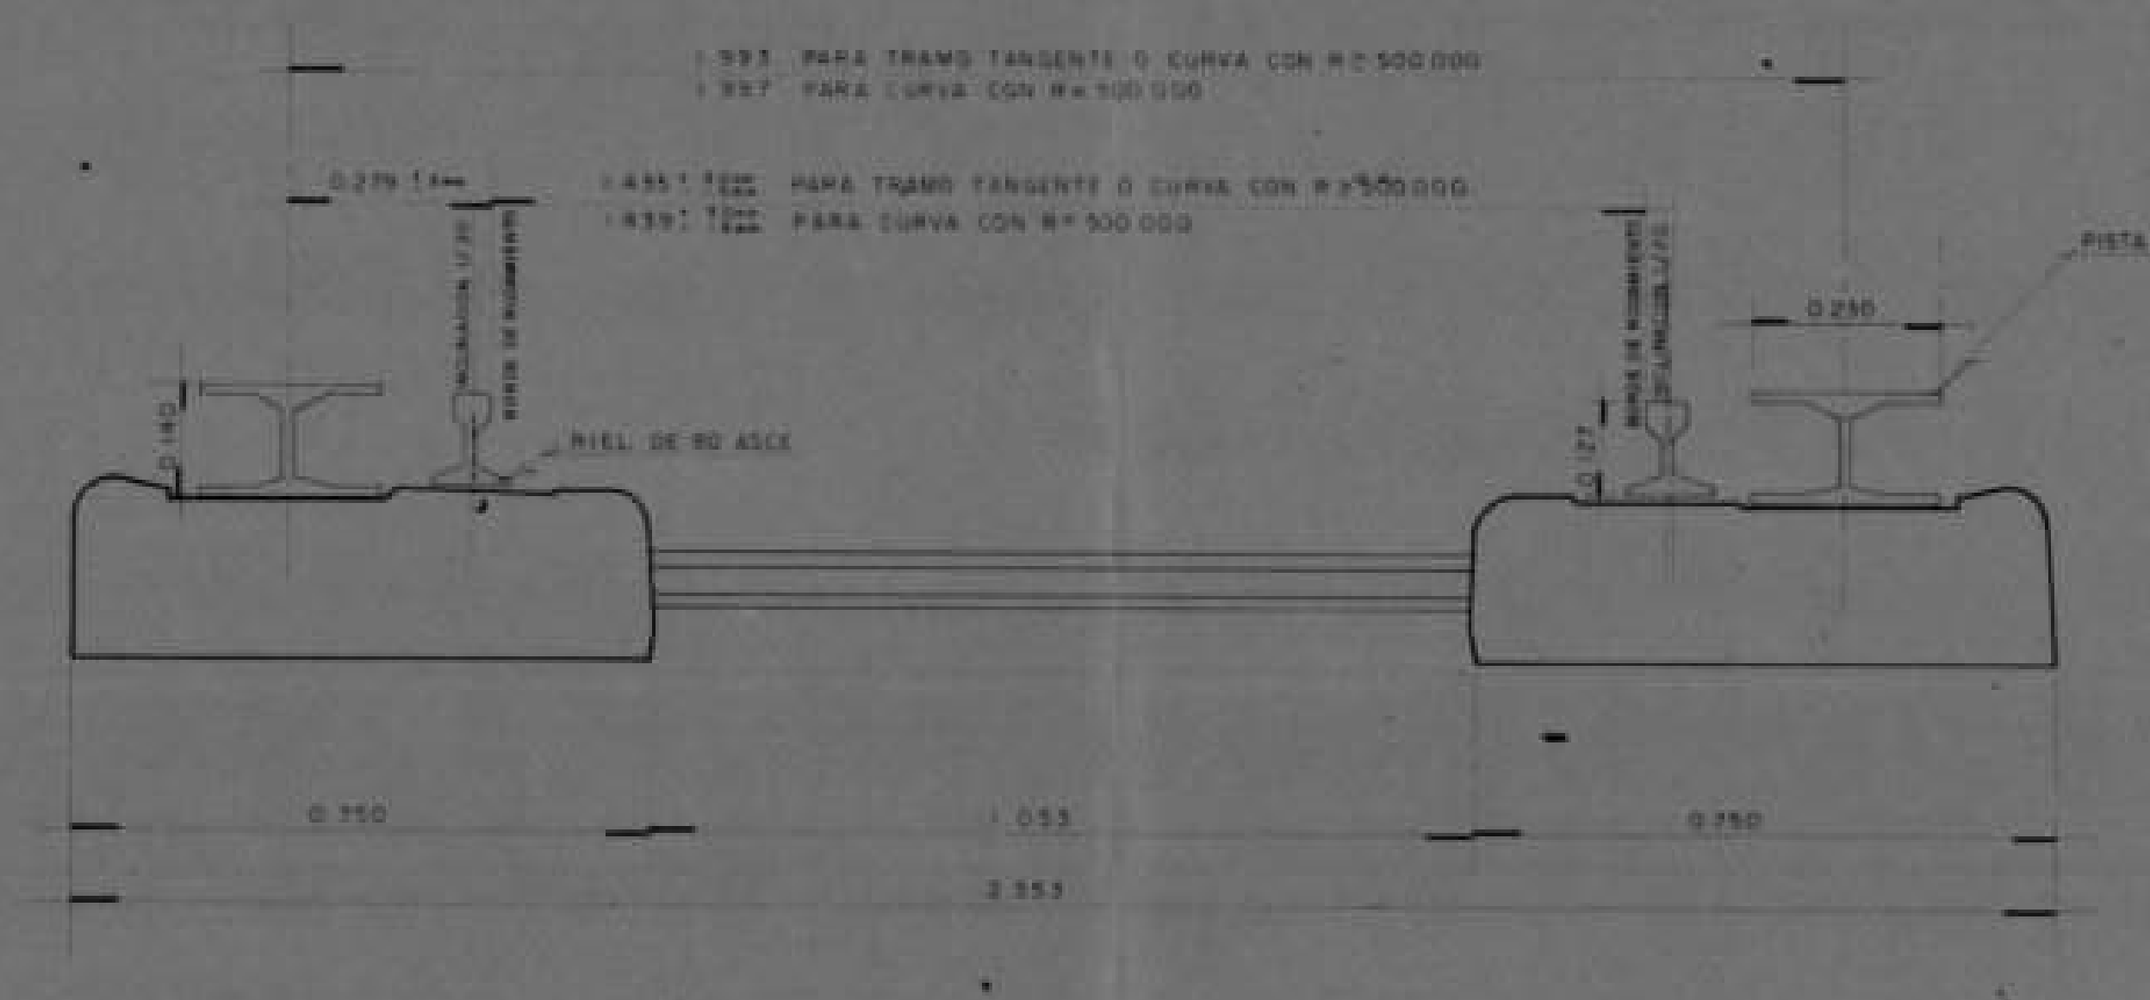
1.993 PARA TRAMO TANGENTE O CURVA CON R ≥ 500.000
1.997 PARA CURVA CON R < 500.000
0.275
1.435 PARA TRAMO TANGENTE O CURVA CON R ≥ 500.000
1.439 PARA CURVA CON R < 500.000
RIEL DE 80 ASCE
PISTA DE RODAMIENTO
0.230
0.140
0.127
0.750
1.053
0.750
2.553

NUMERO DE APARATO	AP 06.
MATERIAL SUPRIMIDO	1 DURMIENTE DE 2.400 (2) 1 DURMIENTE DE 4.100 (3) 5 MONTAJE DE AISLADORES SOBRE PLATILLO EN DURMIENTES (1,4,9,12,15)
MATERIAL AGREGADO	1 DURMIENTE DE 3.400 (2) 1 DURMIENTE DE 4.100 (3)
MATERIAL MODIFICADO	

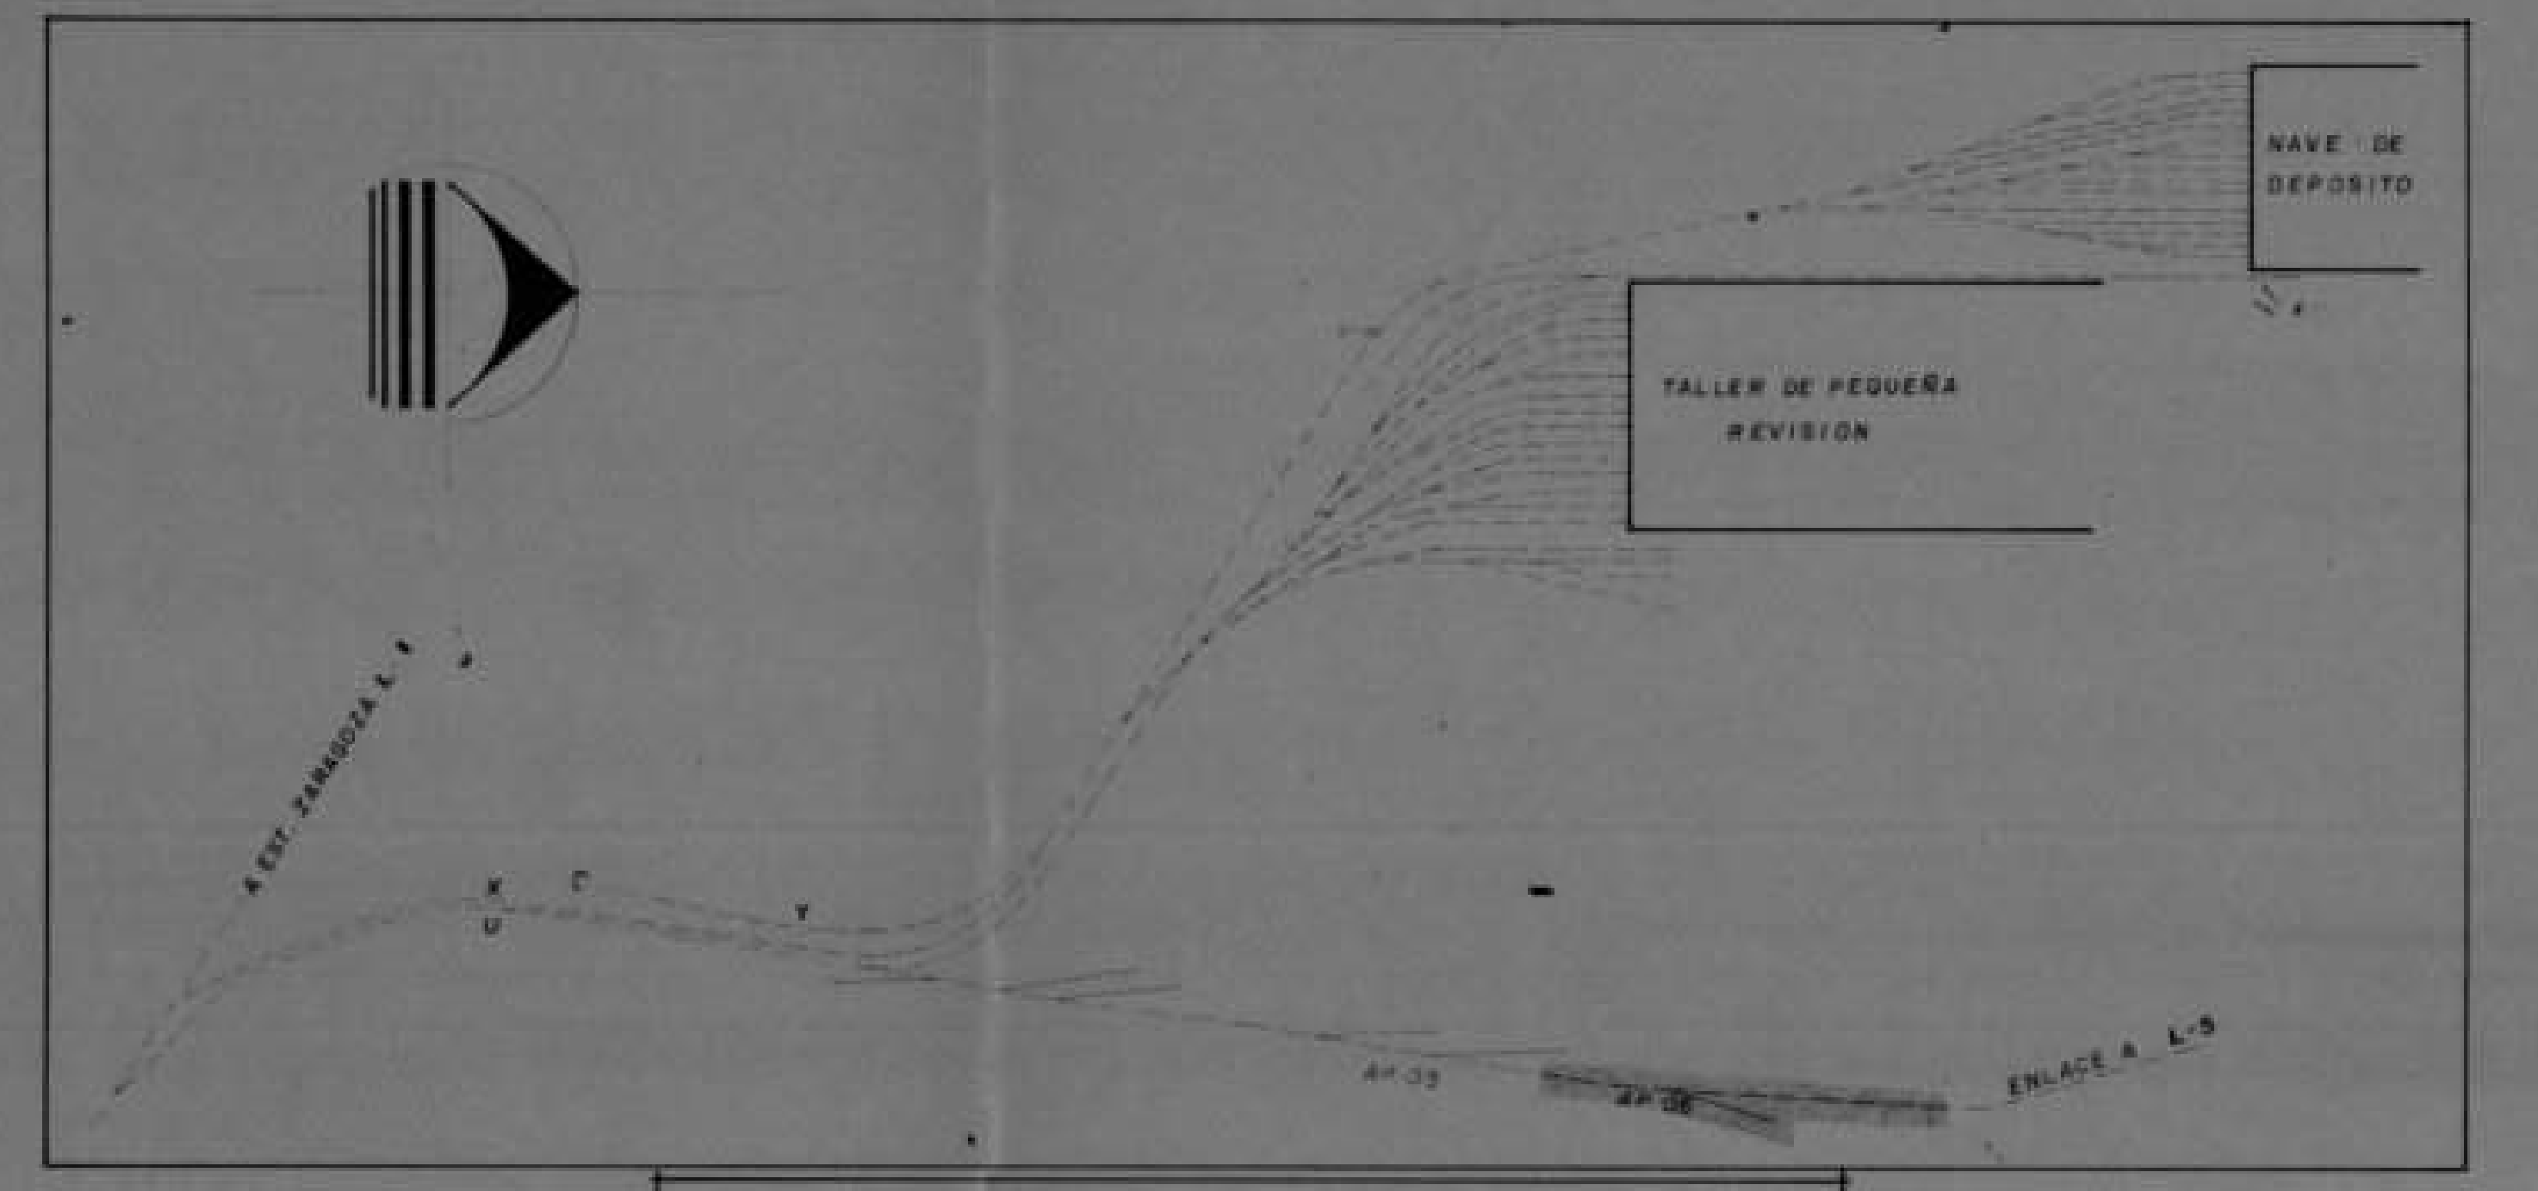
NAVE DE DEPOSITO
TALLER DE PEQUEÑA REVISION
ENLACE A L-5
AP 06

CROQUIS DE LOCALIZACION

NOTAS

1.- EL APARATO ESTA CONFORME AL PLANO DE CONJUNTO
No. 80-VI17-000-III-75-2611-P (ENLACE TS 0.20 A LA DER.)

2.- EL MOTOR DEL APARATO **06** NO SUFRIRA NINGUN CAMBIO, TANTO EN SU UBICACION COMO EN SU FIJACION

3.- ESTE PLANO SE COMPLEMENTA CON LOS SIGUIENTES PLANOS
No. 90-VI13-22248-III-09-221-P (IMPLANTACION DE VIA-TRAZO)
No. 90-VI4-22248-III-10-222-P (RECTIFICACION DE NIVELES)

4.- LAS CRUCETAS ESPECIALES DE 12.000 m ESTAN DE ACUERDO AL PLANO
No. 81-VI17-000-III-128-3784-P

5.- LA POSICION DE LAS CRUCETAS ESTAN CONFORME AL LEVANTAMIENTO FISICO DE CAMPO

6.- LA COTA "**A**" CORRESPONDIENTE A LA COTA "**B**" DE 0.553 ES DE 0.462

7.- LAS **6 J M** DE RIEL Y PISTA EXISTENTES SE ELIMINARAN, UNIENDOSE LOS PERFILES MEDIANTE SOLDADURA ALUMINOTERMICA

T.d.A. J.M.
PST 14359.382
APARATO 05
CONSULTAR PLANO No.
PC 14409.637
R= 500.000
PT 14427.820
R= 500.000
P.d.A. 14437.335
EMPALME
AL AP 06
4.500
RIEL DE 80 ASCE
RIEL DE 100 RE

DETALLE DE LAS CABEZAS DE LOS DURMIENTES
(AISLADOR SOBRE ZOCLO)

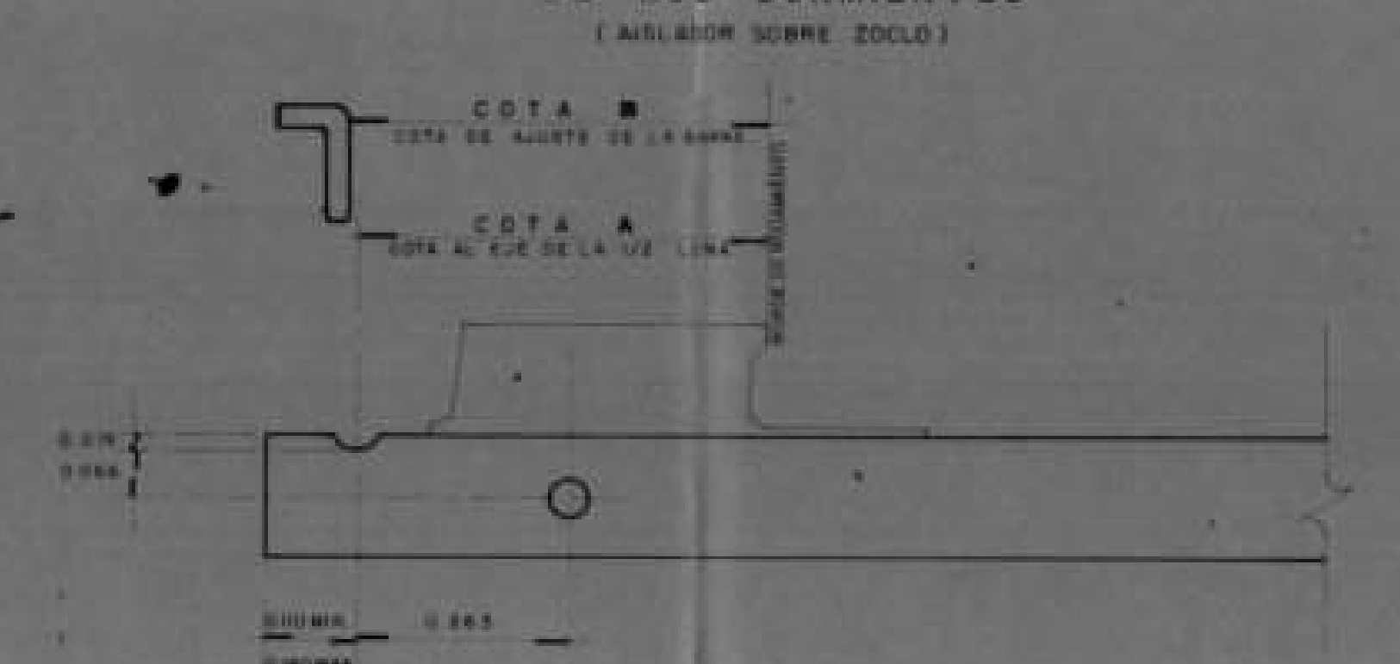
COTA B
COTA A

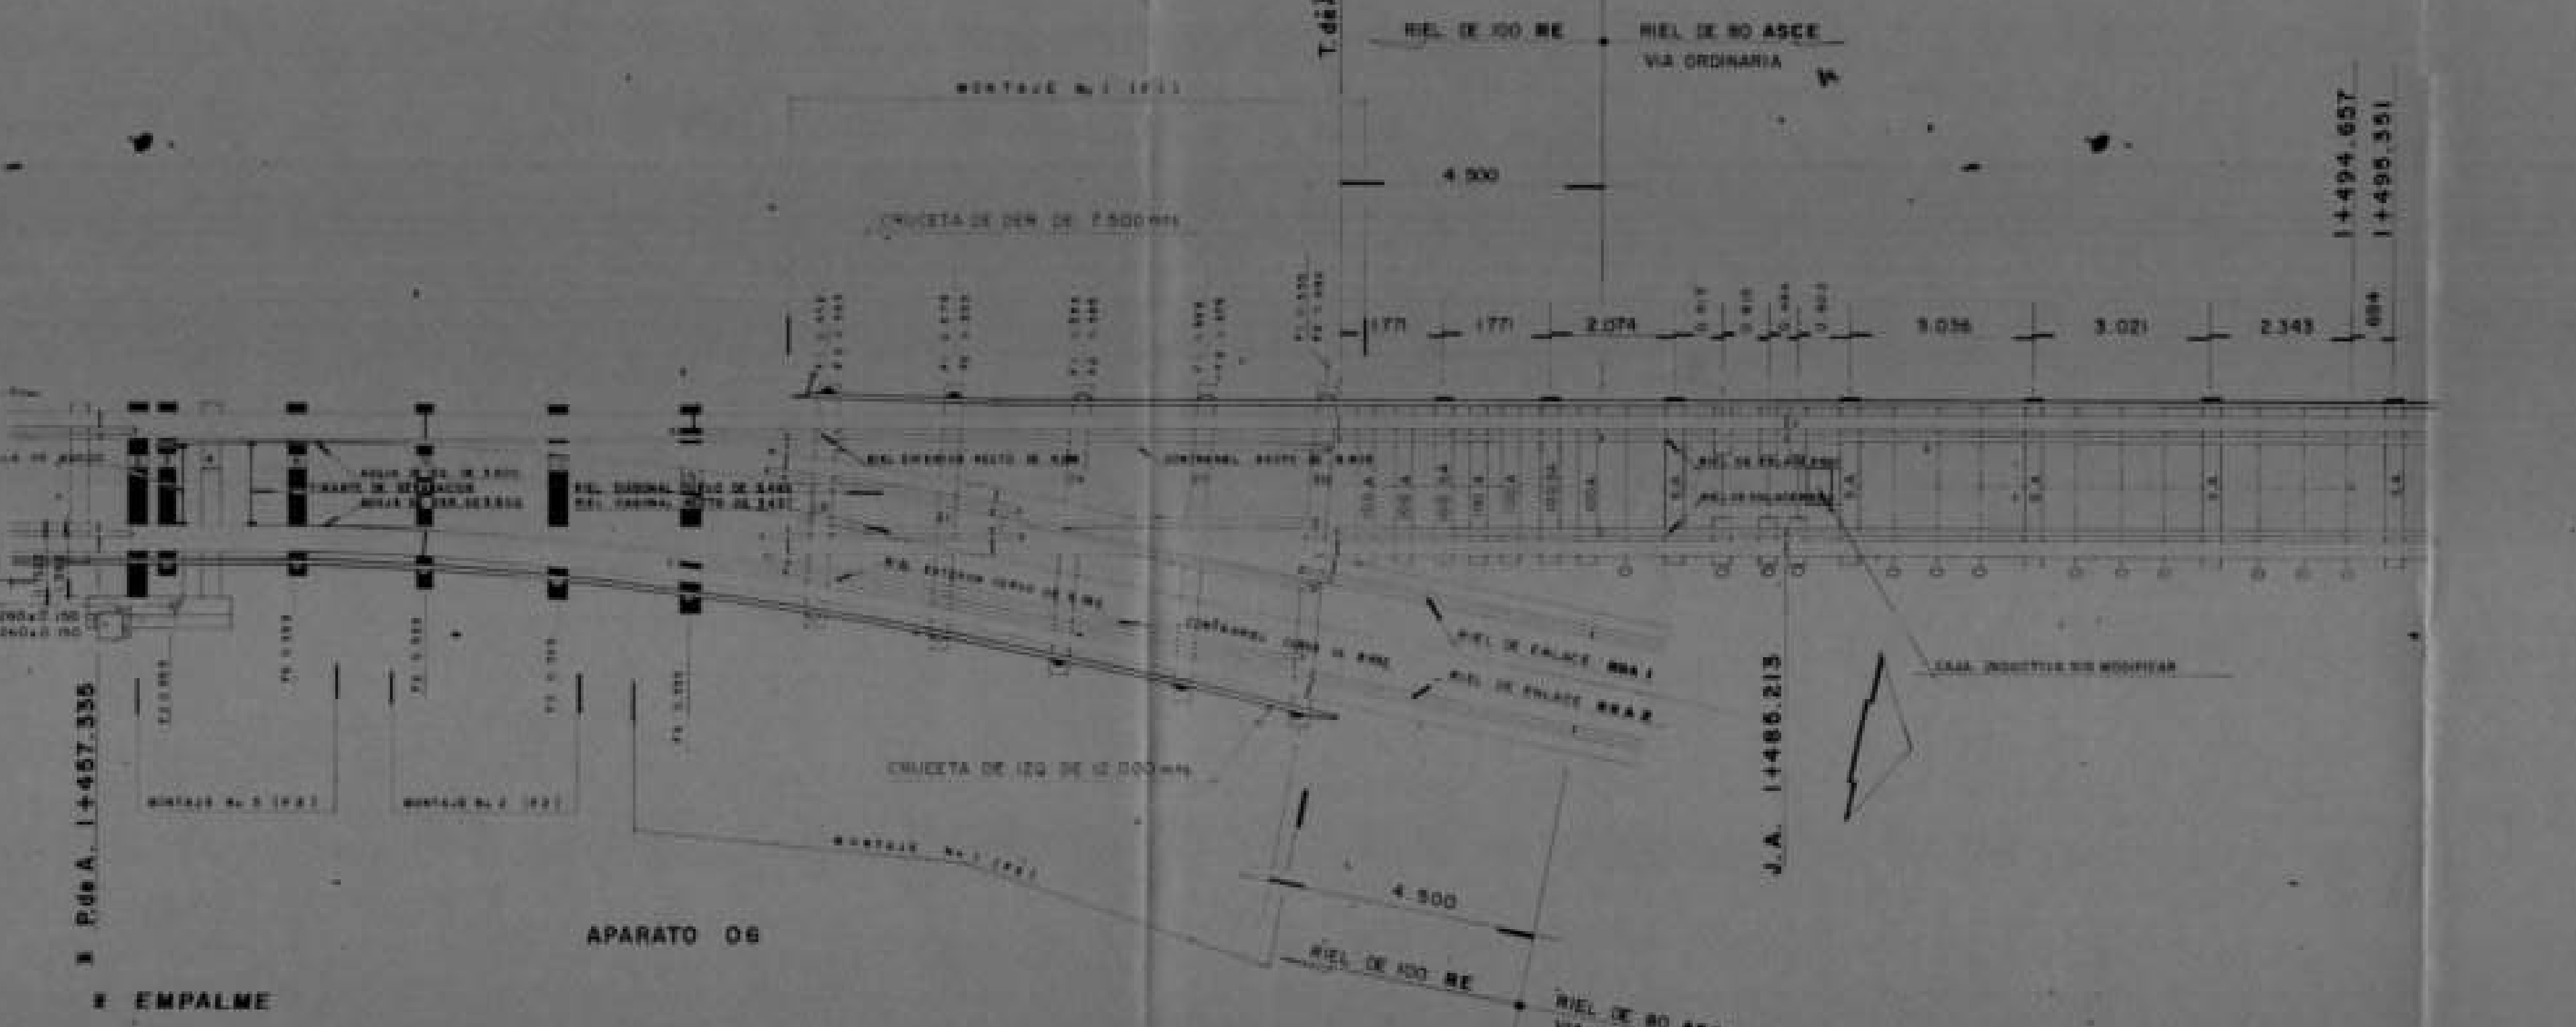
T.d.A. 14477.727
RIEL DE 100 RE
RIEL DE 80 ASCE VIA ORDINARIA
4.500
14494.657
14495.351
EJE DE TRAZO
J.A. 14485.213
A LINEA 5
P.d.A. 14437.335
EMPALME
APARATO 06
RIEL DE 100 RE
RIEL DE 80 ASCE VIA ORDINARIA

DETALLE DE LAS CABEZAS DE LOS DURMIENTES
(AISLADOR SOBRE PLATILLO)

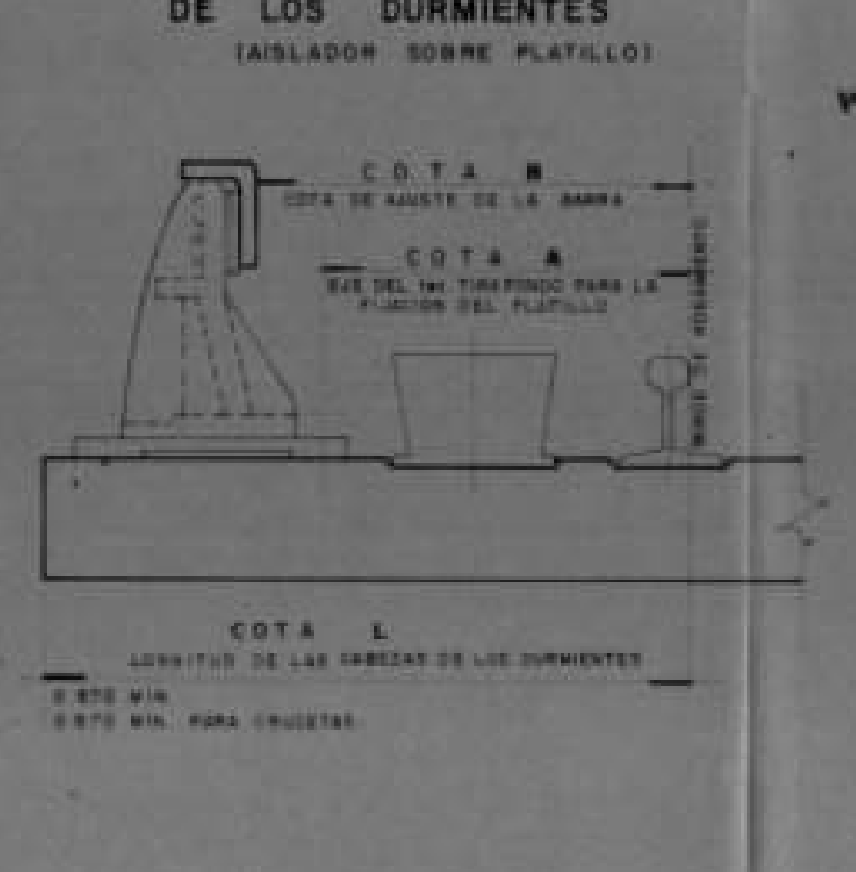
COTA B
COTA A

NUMERO DE APARATO	V I A	NUMERO DE DURMIENTES	MEDIDA B (mm)	MEDIDA A (mm)	TIPO DE CRUCETA
AP 06	DIRECTA	18 21 24	652 575 553 F1	561 499 462 F1	DE DERECHA DE 7.500
	DESVIADA	30 27 24 21	652 575 565 553 F2	561 499 474 462 F2	ESPECIAL DE 12.00 DE IZQUIERDA

RESUMEN GENERAL DE LA DISTRIBUCION DE DURMIENTES											
	TIPO DE DURMIENTES.										
V I A	O	S A	100 A	100 S A	100 SACR 1	100 SACR 2	100 SACR 3	SACR 1	SACR 2	SACR 3	
AP 05 al AP 06	88	28	8	1	1	1	1	1	1	1	
AP 06 ENLACE A LINEA 5	13	5	5	2							
TOTAL	101	33	13	3	1	1	1	1	1	1	

S I M B O L O G I A

▭	DURMIENTE SOPORTE DE AISLADOR Y DURMIENTE SOPORTE DEL PISO DE MANIOBRAS
▬	DURMIENTE NO CONFORME CON EL PLANO DE CONJUNTO.
◠	AISLADOR SOBRE PLATILLO PARA LA BARRA DE TOMA DE CORRIENTE
●	AISLADOR SOBRE PLATILLO PARA CRUCETA
J.A.	JUNTA AISLANTE A SUMINISTRAR CON EL APARATO DEL LADO DEL CORCHETE
▬	AISLADOR SOBRE ZOCLO PARA LA BARRA DE TOMA DE CORRIENTE

S I M B O L O G I A

▬	AISLADOR SOBRE ZOCLO
	EJE DE VIA
J.A.	EJE DE JUNTA AISLANTE
S.A.	DURMIENTE DE MADERA, SOPORTE DE AISLADOR SIN GUIADO PARA RIEL DE 80 ASCE EN TAN ó EN CURVA DE R ≥ 500.000 m
O	DURMIENTE ORDINARIO DE CONCRETO
100S.A.	DURMIENTE SOPORTE CON AISLADOR SIN GUIADO PARA RIEL DE 100 RE EN TAN ó EN CURVA DE R ≥ 500.000 m
100 A	DURMIENTE ORDINARIO PARA RIEL DE 100 RE EN TAN ó EN CURVA DE R ≥ 500.000 m
100SACR	DURMIENTE SOPORTE CON AISLADOR PARA CRUCETA EN RIEL DE 100 RE EN TAN ó EN CURVA DE R ≥ 500.000 m
SACR	DURMIENTE SOPORTE DE AISLADOR PARA CRUCETA EN TAN ó EN CURVA DE R ≥ 500.000 m

DEPARTAMENTO DEL DISTRITO FEDERAL **STC**
SISTEMA DE TRANSPORTE COLECTIVO

ING. GERARDO FERRANDO BRAVO
DIRECCION GENERAL

ING. FILIBERTO ZEPEDA TIJERINA
SUB-DIRECTOR DE OPERACION

ISTME
PROYECTO

PROYECTO:
REALINEACION Y RENIVELACION DE VIAS EN OPERACION
METRO

ARQ. JOSE LUIS BUENDIA MARTINEZ

ING. SERGIO RUELAS MONCAYO

LINEA 1
IMPLANTACION DE VIA-FIJACION DE VIA.
TRAMO: TALLERES ZARAGOZA
COLOCACION DEL AP **06** Y DISTRIBUCION DE DURMIENTES Y LOCALIZACION DE **JA** EN LA VIA DE ENLACE CON **LINEA 5**

ING. RICARDO PEREZ RUIZ
APROBO
ING. ISMAEL GONZALEZ TECUATL
REVISO
ING. GERARDO CASTILLO SORIANO

STC
ARQ. MANUEL MEZA ZATARAIN
STC
ING. SALOMON SOLAY ZYMAN
STC
ING. ROBERTO CASTAÑEDA CHAVEZ
STC
ING. ERASMO CUATECONTZI CASTELLANOS
STC
ING. MARCO A. ROCHA URBINA
STC
ING. ALFREDO NAVARRETE YAÑEZ

ESCALA
INDICADAS
ACOTACIONES
EN METROS
FECHA
ABRIL 1990

REVISO
PROYECTO
ARQ. MANUEL
PLANO No.
90-VI17-22248-III-11-232-P
MODIFICACION No. 0
ING. FERNANDO CASTRO E.

Dib. C. Vega F.