NUMERO DE APARATO	23-A	23-C	63-A	63-B
MATERIAL SUPRIMIDO	[illegible]	[illegible]	[illegible]	[illegible]
MATERIAL AGREGADO	[illegible]	[illegible]	[illegible]	[illegible]
MATERIAL MODIFICADO	[illegible]	[illegible]	[illegible]	[illegible]

NUMERO DE APARATO	V I A	NUMERO DE DURMIENTES	MEDIDA B (mm.)		MEDIDA A (mm.)		TIPO DE CRUCETA
23-C	DIRECTA	22 24 27	660 611 585 F.10	— — — F.5	659 586 520 F.10	— — — F.5	DE IZQ. DE 7.500
	DESVIADA	21 * 23 * 26 * 28 *	660 611 563 553 F.5	— — — — F.10	569 520 472 462 F.5	— — — — F.10	DE DER DE 7.500
	DIRECTA	18 18 15	660 611 563 F.10	— — — F.5	635 586 520 F.10	— — — F.5	DE DER. DE 7.500
63-A	DESVIADA	21 * 23 * 25 * 28 *	660 611 563 553 F.5	— 558 — — F.10	569 520 472 462 F.5	— 520 — — F.10	DE DER DE 7.500
63-B	DESVIADA	21 * 23 * 26 * 29 *	660 611 585 553 F.7	569 520 472 462 F.10	— 553 — — F.7	— 520 — — F.10	DE DER DE 7.500
	DIRECTA	67 65 63 61	660 611 585 563 F.10	— — — — F.9	659 586 553 520 F.10	— — — — F.9	DE DER. DE 7.300
	DESVIADA	70 68 66 64	660 611 585 553 F.7	— — — — F.9	629 586 529 520 F.7	— — — — F.9	DE IZQ. DE 7.500

* COLOCACION DE AISLADOR SOBRE PLATILLO

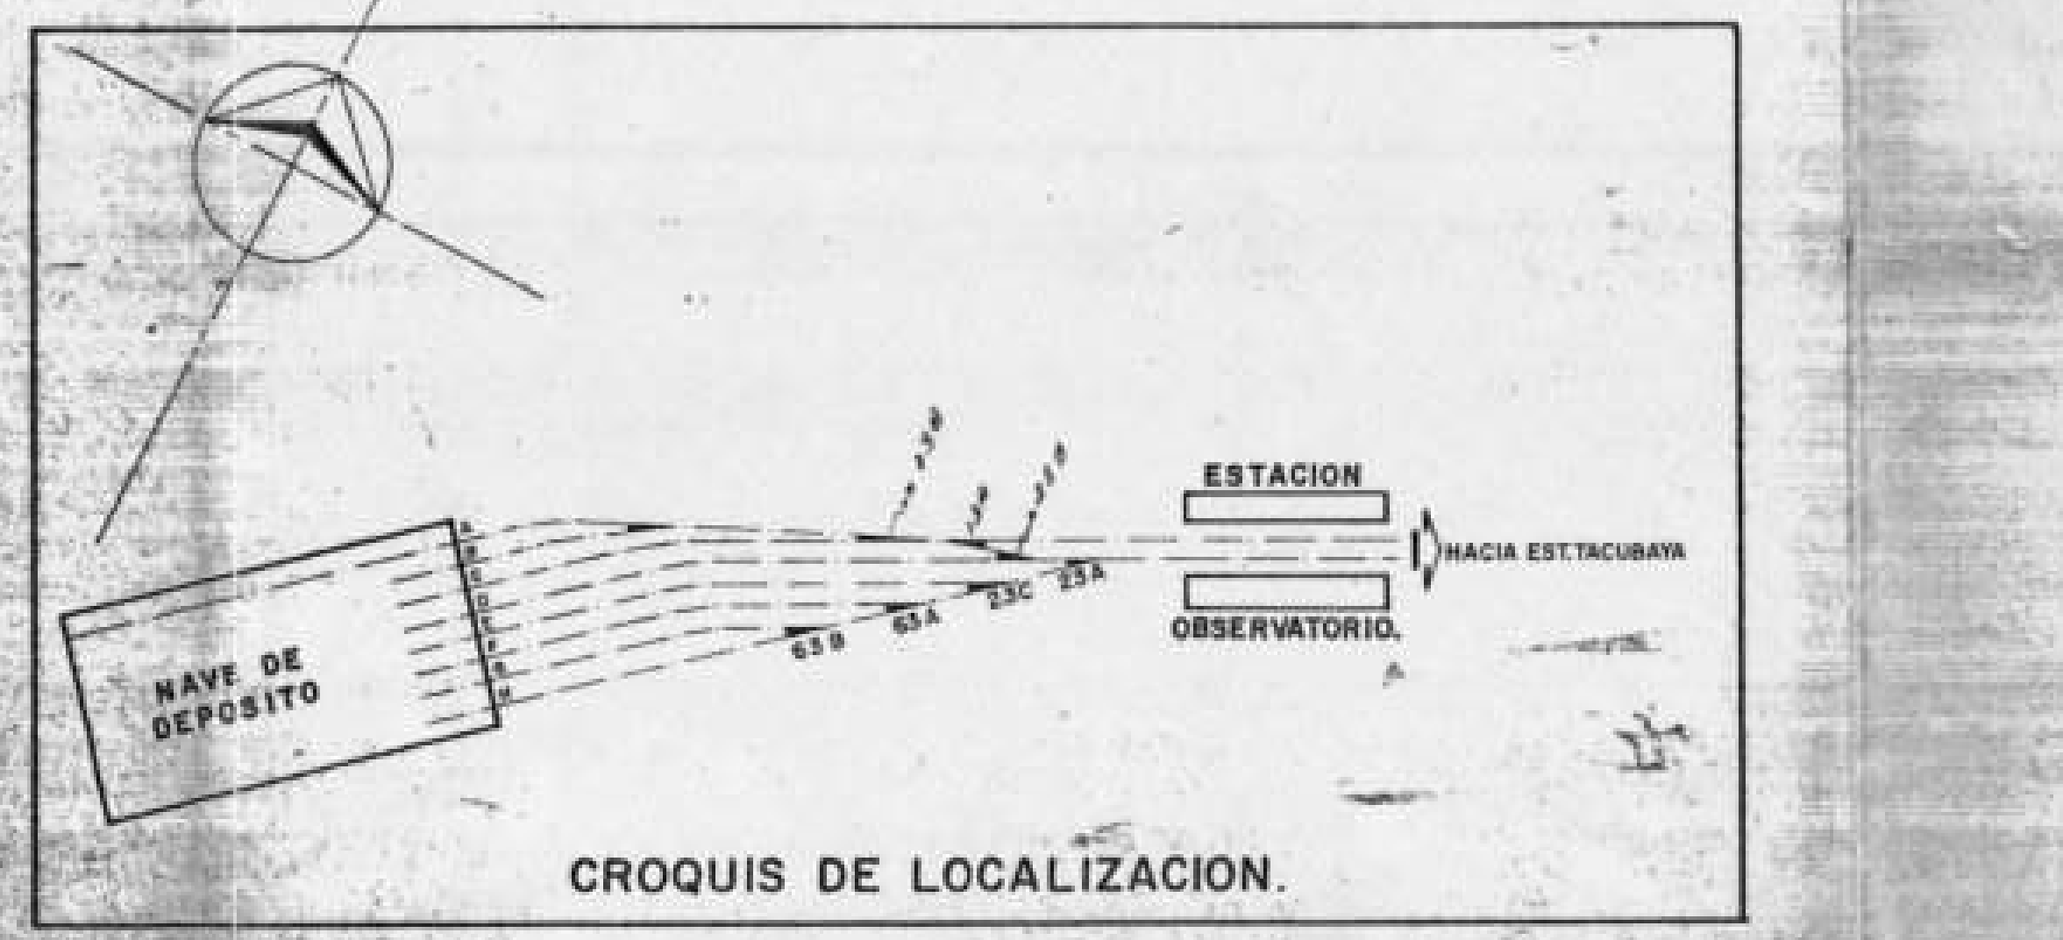
NAVE DE DEPOSITO
63 B
63 A
23C
23A
23 B
ESTACION
OBSERVATORIO.
HACIA EST. TACUBAYA

CROQUIS DE LOCALIZACION.

N O T A S :

1.-LOS APARATOS ESTAN CONFORME A LOS PLANOS DE CONJUNTO
84-VI.17-000-[III]-139-4277-P (ENLACE TG. 0.13 DERECHA)
90-VI.17-000-[III]-59-2595-P (ENLACE TG. 0.13 IZQUIERDA), EXCEPTO LAS INDICACIONES MENCIONADAS EN ESTE PLANO.

2.-LOS MOTORES ESTAN COLOCADOS CONFORME A LOS PLANOS
80-VI.17-000-[III]-90-2658-P MOD. 0 (VIA AL INTERPERIE, COLOCACION DE LOS MOTORES EN LOS APARATOS TG. 0.13 -- MONTAJE DIRECTO).

3.-REFERENCIAS:
90-VI.13-22232-[III]-1-35-P (PROY. DE IMPLANTACION DE VIA - TRAZO)
90-VI.16-22232-[III]-2-36-P (PROY. DE RECTIFICACION DE NIVELES DE RASANTE)

4.-LAS JUNTAS AISLANTES ESTAN UBICADAS DE ACUERDO AL LEVANTAMIENTO FISICO DE OBRA.

5.-LOS DURMIENTES CON AISLADOR DEBERAN UBICARSE EN LA POSICION INDICADA EN EL PRESENTE PLANO.

A NAVE DE DEPOSITO
VIA G
VIA H
VIA E
VIA F
APARATO 63 B
APARATO 63 A
APARATO 23 C
APARATO 23 B
APARATO 23 A
MONTAJE No. 1 (F-10)
MONTAJE No. 3 (F-10)
PLANCHA DE PROTECCION
EJE DE MOTOR
J.A.
PT = P. DE A. 15+956.462 S/V
15+946.438 S/V
CABECERA DE ESTACION
PC
A ESTACION OBSERVATORIO
VIA 2

DETALLE DE LAS CABEZAS DE LOS DURMIENTES
(AISLADOR SOBRE PLATILLO)

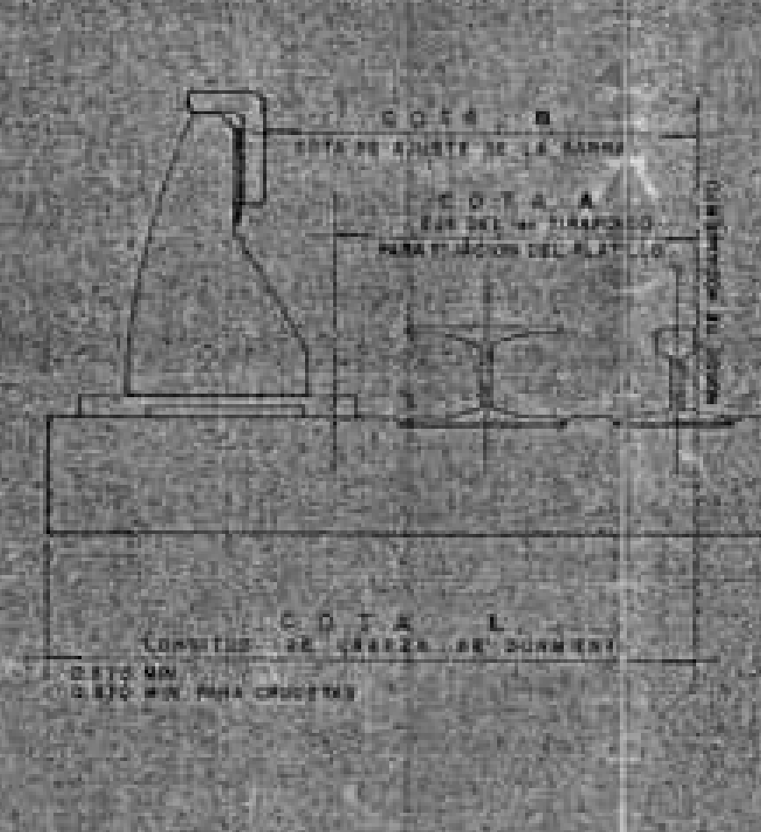

DETALLE DE LAS CABEZAS DE LOS DURMIENTES
(AISLADOR SOBRE ZOCLO)

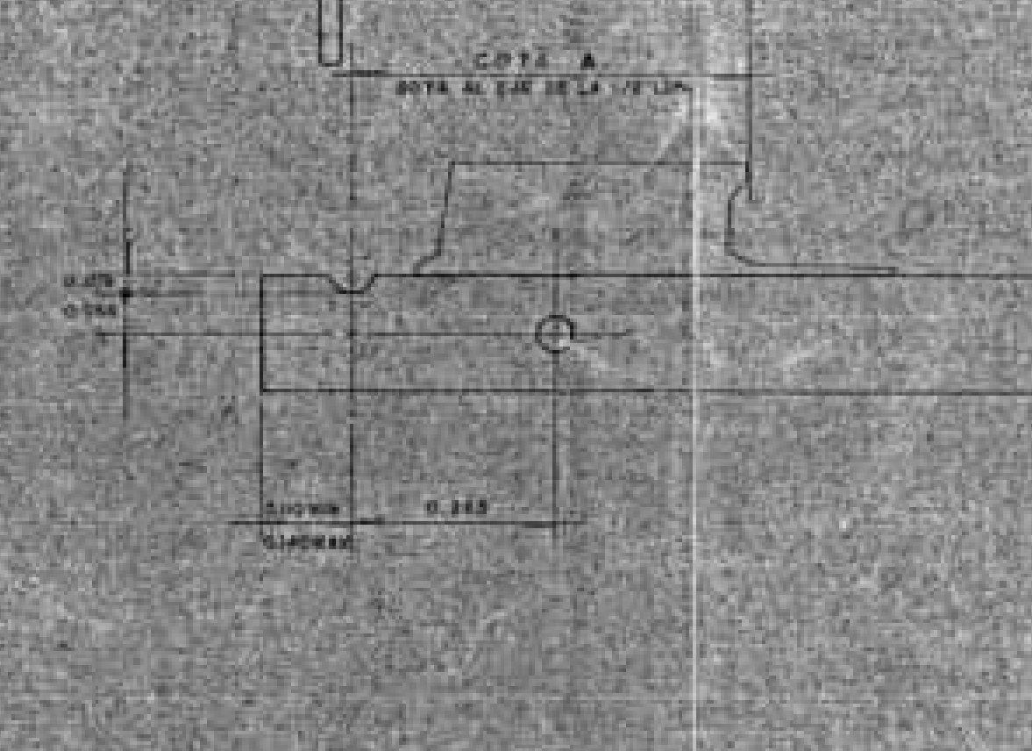

RESUMEN GENERAL DE DURMIENTES.		
TIPO DE DURMIENTES		
O	GC	GA
4	1	0

S I M B O L O G I A

- DURMIENTE SOPORTE DE AISLADOR Y DURMIENTE SOPORTE DEL PISO DE MANIOBRAS.
- DURMIENTE NO CONFORME CON EL PLANO DE CONJUNTO.
- AISLADOR SOBRE PLATILLO PARA LA BARRA DE TOMA DE CORRIENTE.
- AISLADOR SOBRE PLATILLO PARA CRUCETA.
- JUNTA AISLANTE A SUMINISTAR CON EL APARATO DEL LADO DEL CORCHETE.
- AISLADOR SOBRE ZOCLO PARA LA BARRA DE TOMA DE CORRIENTE.

5

DEPARTAMENTO DEL DISTRITO FEDERAL
STC
SISTEMA DE TRANSPORTE COLECTIVO

ING. GERARDO FERRANDO BRAVO.
DIRECCION GENERAL

ING. FILIBERTO ZEPEDA TIJERINA
SUB-DIRECTOR DE OPERACION

PROYECTO
PROYECTO:
REALINEACION Y RENIVELACION EN VIAS EN OPERACION
M E T R O

ARQ. JOSE LUIS BUENDIA MARTINEZ

ING. SERGIO RUELAS M.

LINEA-1
IMPLANTACION DE VIA - FIJACION DE VIA
TRAMO COLA-OBSERVATORIO
PLANO DE COLOCACION DE APARATOS
23-A, 23-C, 63-A, 63-B

ING. RICARDO PEREZ
APROBO
ING. ISMAEL GONZALEZ TECUATL
REVISO
ING. GERARDO CASTILLO S.
PROYECTO
ARQ. JAVIER SILVA ZALAPA

ARQ. MANUEL MEZA ZATARAIN.
ING. SALOMON SOLAY ZYMAN.
ING. ROBERTO CASTANEDA CHAVEZ.
ING. ERASMO CUATECONTZI CASTELLANOS

ESCALA: 1:100
ACOTACIONES: EN METROS
FECHA: AGOSTO - '90.

PLANO No: 90-VI.17-22232-[III]-05-39-P
MODIFICACION No

ING. FERNANDO ROCHA URBINA
STC: ING. ALFREDO NAVARRETE YAÑEZ
INPLAT: ING. FERNANDO CASTRO C.