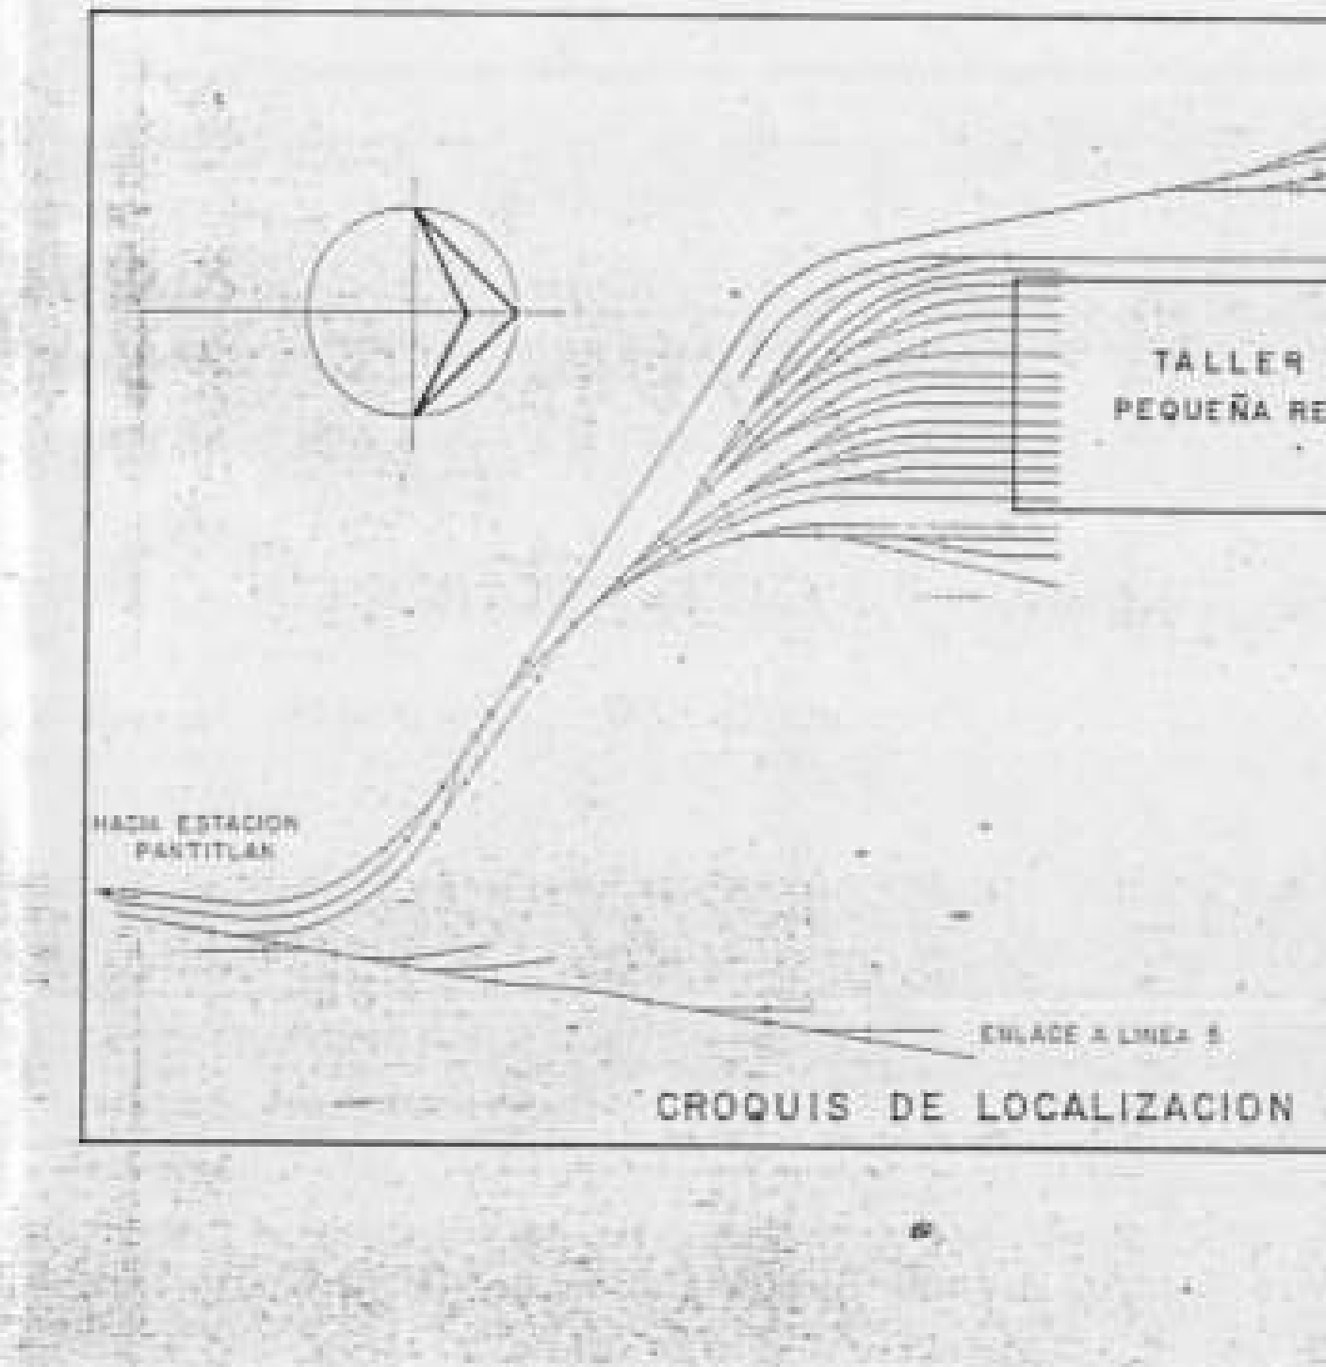

NOTAS:

1.- ESTE PLANO SE EJECUTO CON LAS "ESPECIFICACIONES PARA EL PROYECTO Y CONSTRUCCION DE LAS LINEAS DEL METRO DE LA CIUDAD DE MEXICO", EDITADAS POR COVITUR.

VOLUMEN I
LIBRO 2
PARTE 2.02
SECCION 2.02.03
CAPITULO 2.02.03.002
CLAUSULA 2.02.03.002. F

2.- SE COMPLEMENTA CON LOS PLANOS:
No. 89-VI.17-46012-III-02-P. (APARATOS 6006, 6007, 6008, 6009, 6010)
No. 89-VI.13-46012-III-09-P. (IMPLANTACION DE VIA - TRAZO)
No. 89-VI.16-46012-III-13-P. (RECTIFICACION DE NIVELES DE RASANTE)

3.- LA LONGITUD DE LAS VIAS SE CALCULO SOBRE LA PISTA DE MAYOR DESARROLLO Y LA DISTRIBUCION DE DURMIENTES SOBRE EL RIEL DE MAYOR DESARROLLO.

4.- LOS CADENAMIENTOS ESTAN REFERIDOS AL EJE DE VIA - TRAZO.

5.- EN CASO DE UTILIZAR DURMIENTES DE CONCRETO EN ZONA DE J.A., LA SEPARACION ENTRE LOS EJES DE DURMIENTES SERA DE 0.484 M

6.- LOS DURMIENTES CON AISLADOR CONSERVAN SU POSICION ORIGINAL.

RESUMEN GENERAL DE LA DISTRIBUCION DE DURMIENTES

VIA	TIPO DE DURMIENTES															
	SA	SC	O	100SA	100SC	100A	100C	100T	SACR1	SACR2	SACR3	SCCR1	100SACR1	100SACR2	100SACR3	A
G10	1	3	20	1	1	3	1	1	1	1	1					3
G 9	5		18	2		4			1	1	1					4
G 8	10		35	2		4			1	1	1					4
G 7	16		58	2		4			1	1	1					4
G 6	24		78	2		4			1	1	1					4
TOTAL	56	3	213	9	1	19	1	1	5	5	5					19

S I M B O L O G I A

AISLADOR SOBRE ZOCLO.
EJE DE VIA.
J.A. EJE DE JUNTA AISLANTE.
100SA DURMIENTE SOPORTE CON AISLADOR SIN GUIADO PARA RIEL DE IDORE EN TAN. ó EN CURVA DE R ≥ 500.000 M.
100SC DURMIENTE SOPORTE CON AISLADOR SIN GUIADO PARA RIEL DE IDORE CON CURVA DE R < 500.000 M.
100A DURMIENTE ORDINARIO PARA RIEL DE IDORE EN TAN. ó EN CURVA DE R ≥ 500.000 M.
DURMIENTE ORDINARIO PARA RIEL DE IDORE CON CURVA DE R < 500.000 M.
DURMIENTE DE TRANSICION DE RIEL DE IDORE, A — C, C — A.
DURMIENTE SOPORTE DE AISLADOR PARA CRUCETA EN TANG. ó EN CURVA DE R ≥ 500.000 M.
DURMIENTE SOPORTE DE AISLADOR PARA CRUCETA CON CURVA DE R < 500.000 M.
SOPORTE CON AISLADOR PARA CRUCETA EN RIEL DE IDORE EN TAN. ó EN CURVA CON R ≥ 500.000 M.
DE MADERA, SOPORTE DE AISLADOR SIN GUIADO PARA RIEL 80 ASCE EN TAN. ó EN CURVA CON R ≥ 500.000 M.
DE MADERA, SOPORTE DE AISLADOR SIN GUIADO PARA RIEL 80 ASCE EN CURVA DE R < 500.000 M.
ORDINARIO, DE CONCRETO.
ORDINARIO, DE MADERA.

COLOCACION DE LA VIA SOBRE DURMIENTE DE CONCRETO EN ZONA DE BALASTO

(TIPO "O")

ESC 1:10

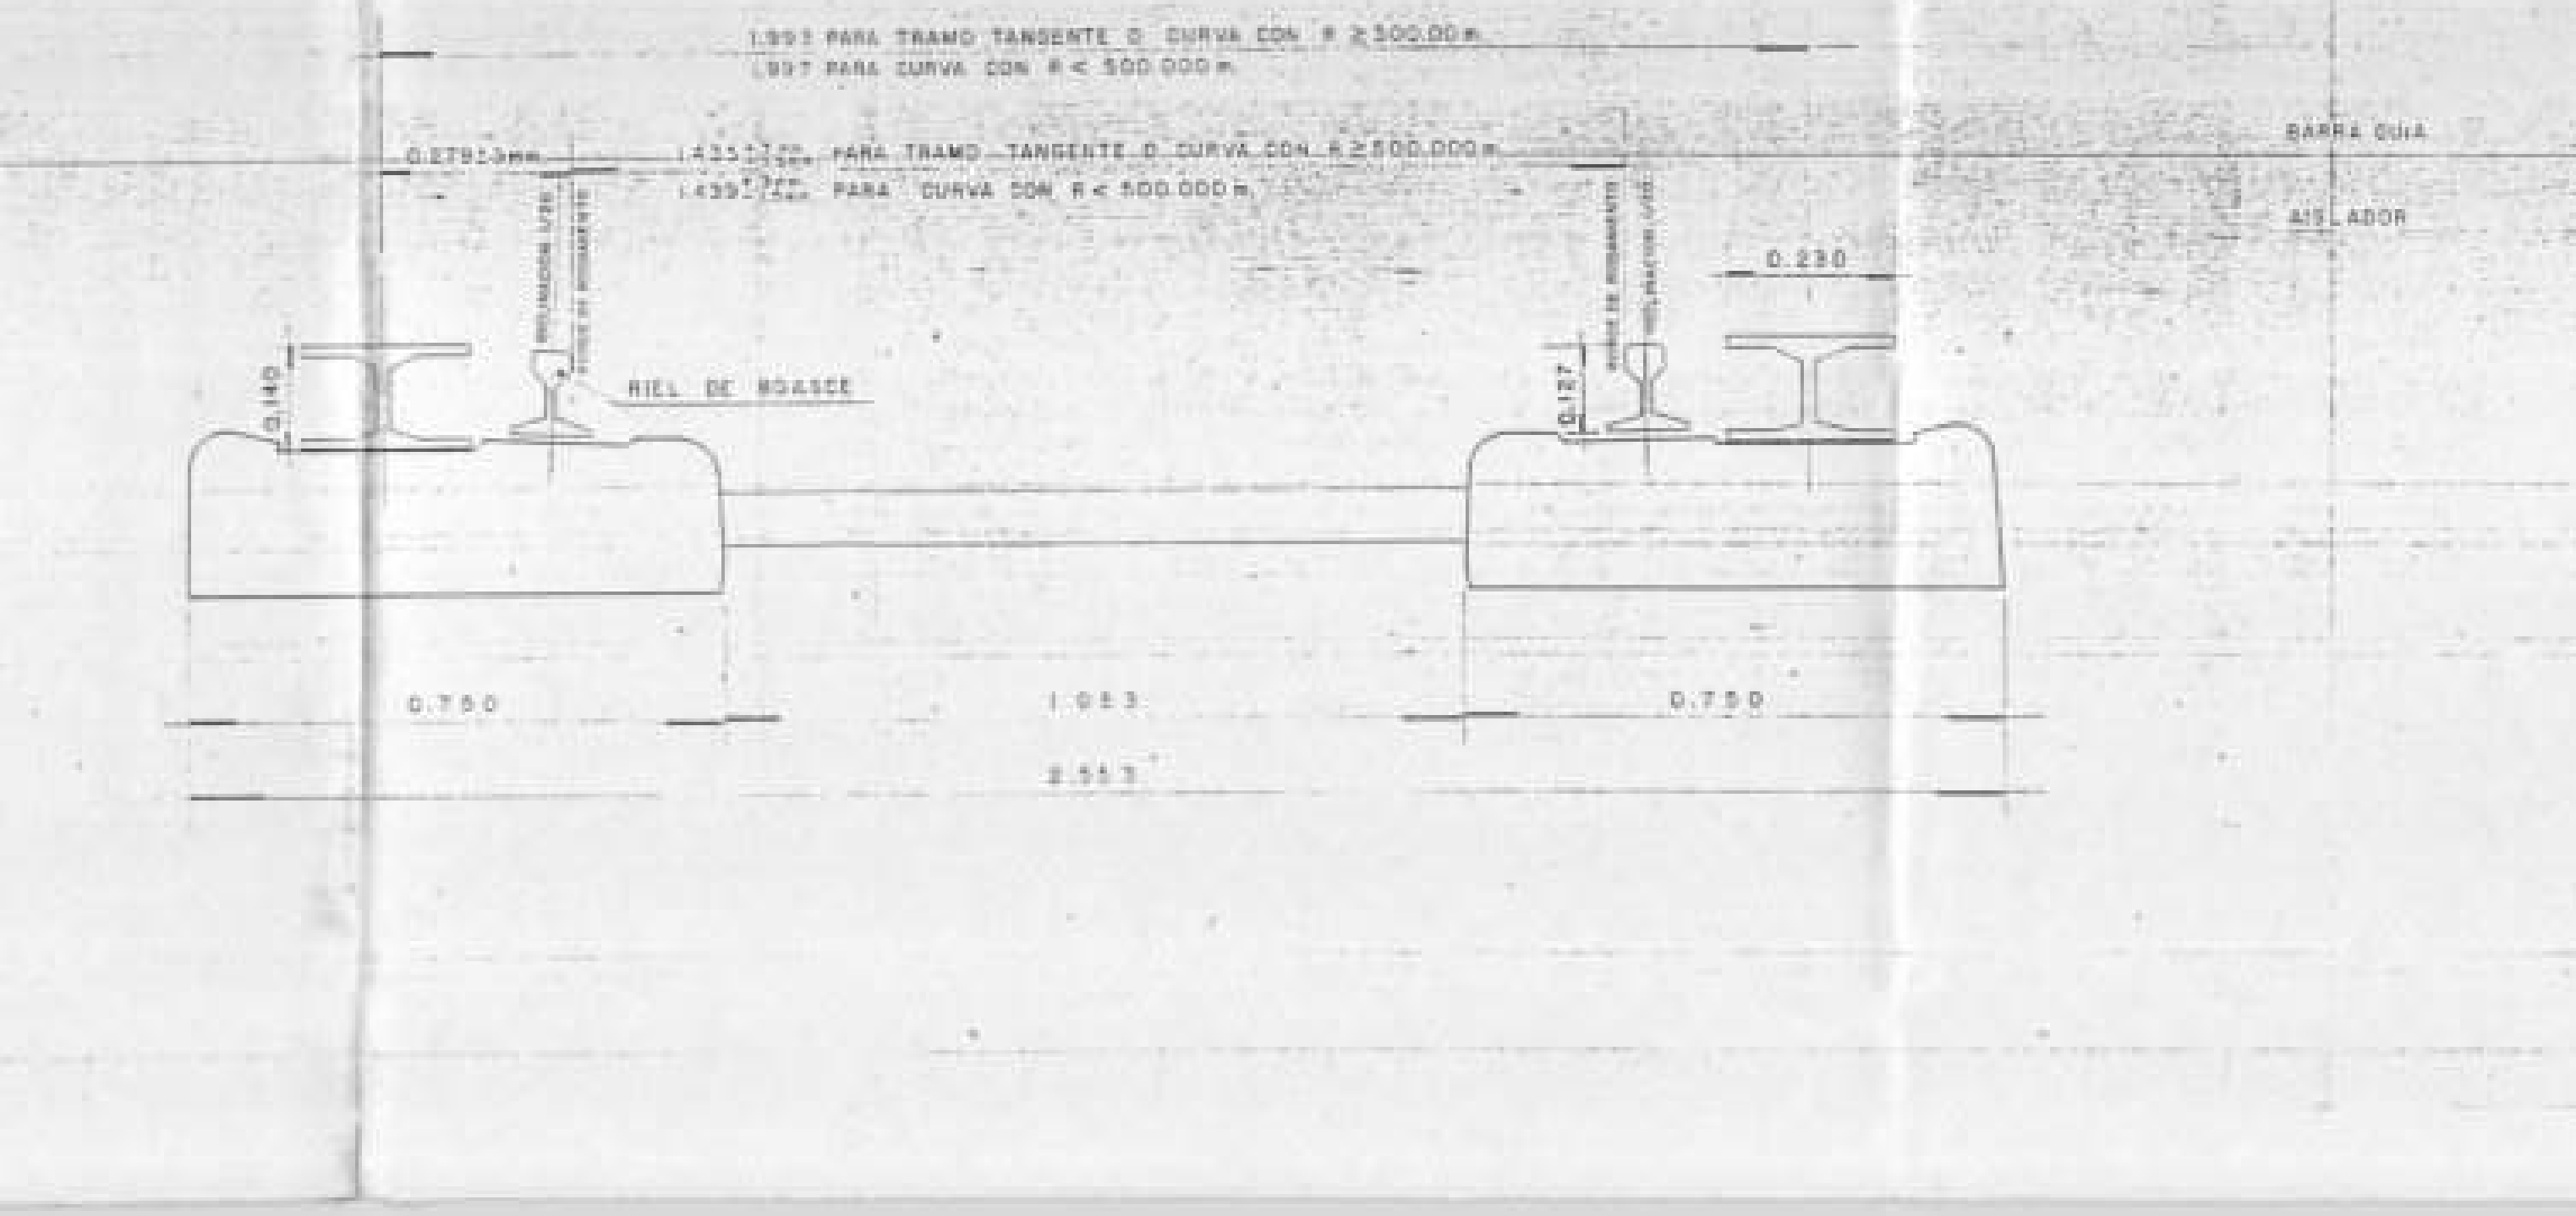
1.993 PARA TRAMO TANGENTE O CURVA CON R ≥ 500.00 m.
1.997 PARA CURVA CON R < 500.000 m.
0.279 ± 3 mm
1.435 PARA TRAMO TANGENTE O CURVA CON R ≥ 500.000 m.
1.439 PARA CURVA CON R < 500.000 m.
RIEL DE 80ASCE
0.140
0.127
0.230
BARRA GUIA
AISLADOR

COLOCACION DE LA VIA SOBRE DURMIENTE DE MADERA EN ZONA DE BALASTO

SIN ESCALA

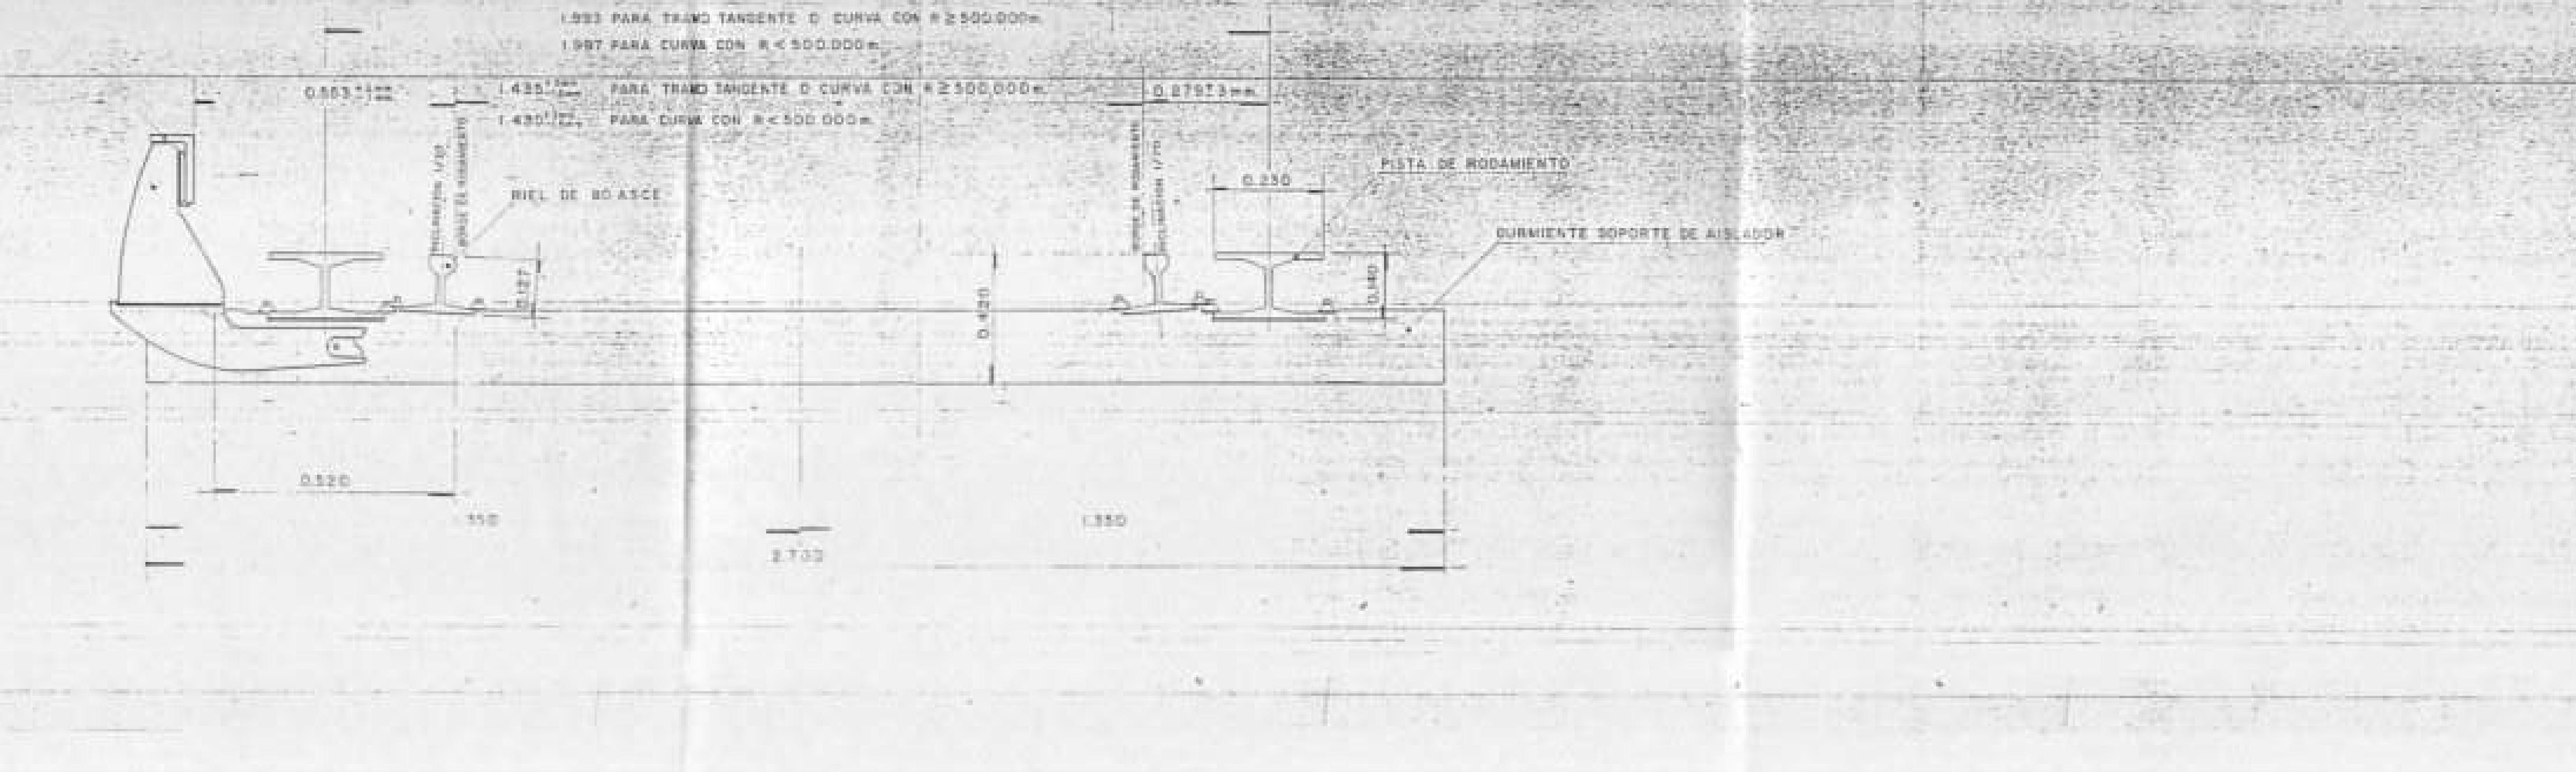
1.993 PARA TRAMO TANGENTE O CURVA CON R ≥ 500.000 m.
1.997 PARA CURVA CON R < 500.000 m.
0.553
1.435 PARA TRAMO TANGENTE O CURVA CON R ≥ 500.000 m.
1.439 PARA CURVA CON R < 500.000 m.
0.279 ± 3 mm
RIEL DE 80 ASCE
0.230
PISTA DE RODAMIENTO
DURMIENTE SOPORTE DE AISLADOR
0.420
0.140
0.127

TABLA DE DATOS COMPLEMENTARIOS

VIA	NUMERO DE CURVA	Δ	Rc	ST	Lc	Lc'	Lc"	I DISTANCIA	II DISTANCIA	III DISTANCIA	IV DISTANCIA	LONGITUD * TOTAL
10	1	1° 18' 35.8"	60.000	5.941	11.844	11.985	12.040	2.652	11.387			26.079
9										25.522		25.522
8										45.537		45.537
7										65.552		65.552
6										85.552		85.552

S I M B O L O G I A

Δ = DEFLEXION.
Rc = RADIO.
ST = SUBTANGENTE.
Lc = LONGITUD DE CURVA SOBRE EJE DE VIA.
Lc' = LONGITUD DE CURVA SOBRE RIEL DE MAYOR DESARROLLO.
Lc" = LONGITUD DE CURVA SOBRE PISTA DE MAYOR DESARROLLO.
I = DISTANCIA PC AL TALON DEL APARATO.
II = DISTANCIA PT A LA ZONA DE TRANSICION, CONCRETO/BALASTO.
III = DISTANCIA DEL TALON DE APARATO A LA ZONA DE TRANSICION, CONCRETO/BALASTO.
IV = DISTANCIA DEL TALON DE APARATO A LA PUNTA DE APARATO.
* = LONGITUD TOTAL: Lc" + I + II + III + IV.

DEPARTAMENTO DEL DISTRITO FEDERAL
STC
SISTEMA DE TRANSPORTE COLECTIVO

ING. GERARDO FERRANDO BRAVO
DIRECTOR GENERAL

ING. [illegible] ZEPEDA TIJERINA
DIRECTOR DE OPERACION

ELECTRO METRO S.A.
PROYECTO

PROYECTO:
REALINEACION Y RENIVELACION DE VIAS EN OPERACION
METRO

ING. PABLO GUERRA CARDEÑAS

ING. ALBERTO GONZALEZ CENICEROS

LINEA 1
IMPLANTACION DE VIA-FIJACION DE VIA
TRAMO: TALLERES-ZARAGOZA
DISTRIBUCION DE DURMIENTES, LOCALIZACION DE J.A. EN VIAS DE ACCESO A NAVE DE DEPOSITO.
VIAS G6 A G10

ARQ. JOSE LUIS [illegible] MARTINEZ
ARQ. GERARDO MUÑOZ GONZALES
ING. SERGIO RUELAS MONCAYO

S.T.C.
ARQ. MANUEL MEZA ZATARAIN

S.T.C.
ING. SALOMON SOLAY ZYMAN

S.T.C.
ING. ROBERTO CASTAÑEDA CHAVEZ

S.T.C.
ING. ERASMO CUATECONTZI CASTELLANOS

S.T.C.
ING. MARCO A. ROCHA URBINA

S.T.C.
ING. ALFREDO NAVARRETE YAÑEZ

ESCALA: INDICADAS
ACOTACIONES: EN METROS
FECHA: SEPTIEMBRE/89

APROBO: ING. ISMAEL GONZALEZ TECUATL
REVISO: ING. J. BARRIOS R.
PROYECTO: ARQ. J. [illegible]

PLANO No. 89-VI.17-46012-III-11-P

INPLAT