DETALLE DE LAS CABEZAS DE LOS DURMIENTES
(AISLADOR SOBRE ZOCLO)

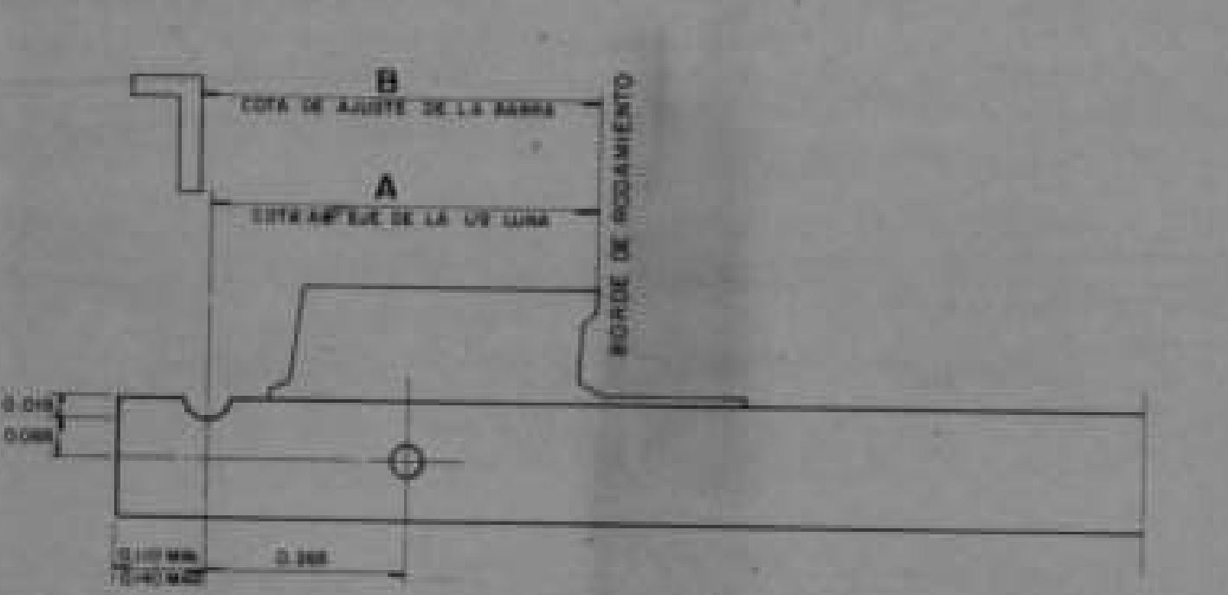
B
COTA DE AJUSTE DE LA BARRA
A
COTA AL EJE DE LA U9 LUNA
BORDE DE RODAMIENTO
0.015
0.065
0.110 MIN.
0.140 MAX.
0.365

DETALLE DE LAS CABEZAS DE LOS DURMIENTES
(AISLADOR SOBRE PLATILLO)

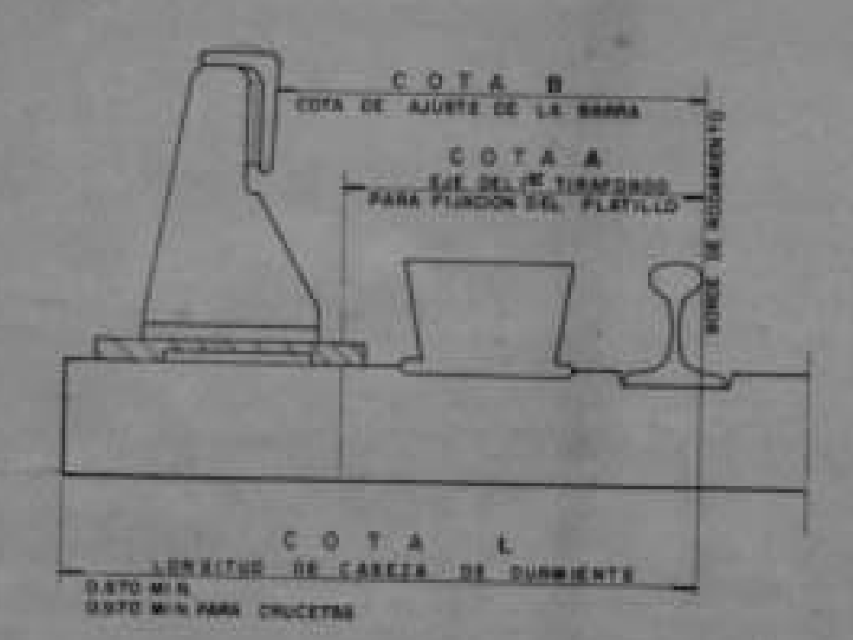
COTA B
COTA DE AJUSTE DE LA BARRA
COTA A
EJE DEL 1er TIRAFONDO PARA FIJACION DEL PLATILLO
BORDE DE RODAMIENTO
COTA L
LONGITUD DE CABEZA DE DURMIENTE
0.870 MIN.
0.970 MIN. PARA CRUCETAS

TIPO DE DURMIENTE	CANTIDAD
100 A	6
100 SA	3

NUMERO DE APARATO	6006	6007	6008	6009	6010
MATERIAL SUPRIMIDO	1 DURMIENTE DE 4.100 (4) 1 DURMIENTE DE 3.600 (6) 8 MONTAJES COMPLETOS DE AISLADOR SOBRE PLATILLO, DURMIENTES (3,6,9,12,15 y 18) LADO F.1 Y DURMIENTES(21 y 24) LADO F.2 2 JUNTAS ORDINARIA DE RIEL DE 100RE Y PISTA	1 DURMIENTE DE 4.100 (3) 1 DURMIENTE DE 4.100 (4) 1 MONTAJE COMPLETO DE AISLADOR SOBRE PLATILLO, DURMIENTE (3) LADO F.3 1 JUNTA ORDINARIA DE RIEL DE 100RE Y PISTA	1 DURMIENTE DE 4.100 (3) 1 DURMIENTE DE 4.100 (4) 1 MONTAJE COMPLETO DE AISLADOR SOBRE PLATILLO, DURMIENTE (3) SOBRE LADO F.4 1 JUNTA ORDINARIO DE RIEL DE 100RE Y PISTA	1 DURMIENTE DE 4.100 (3) 1 DURMIENTE DE 4.100 (4) 1 MONTAJE COMPLETO DE AISLADOR SOBRE PLATILLO, DURMIENTE (3) SOBRE LADO F.5 1 JUNTA ORDINARIA DE RIEL DE 100 RE Y PISTA	1 DURMIENTE DE 4.100 (3) 1 DURMIENTE DE 4.100 (4) 1 MONTAJE COMPLETO DE AISLADOR SOBRE PLATILLO, DURMIENTE (3) SOBRE LADO F.6 1 JUNTA ORDINARIA DE RIEL DE 100 RE Y PISTA
MATERIAL AGREGADO	1 DURMIENTE DE 3.600 (4) 1 DURMIENTE DE 4.400 (6) 4 JUEGOS COMPLETOS DE J.A. DE RIEL DE 100RE Y PISTA	1 DURMIENTE DE 3.600 (3) 1 DURMIENTE DE 2.600 (4) 2 JUEGOS COMPLETOS DE J.A. DE RIEL DE 100RE Y PISTA	1 DURMIENTE DE 3.600 (3) 1 DURMIENTE DE 2.600 (4) 2 JUEGOS COMPLETOS DE J.A. DE RIEL DE 100RE Y PISTA	1 DURMIENTE DE 3.600 (3) 1 DURMIENTE DE 2.600 (4) 2 JUEGOS COMPLETOS DE J.A. DE RIEL DE 100 RE Y PISTA	1 DURMIENTE DE 3.600 (3) 1 DURMIENTE DE 2.600 (4) 2 JUEGOS COMPLETOS DE J.A. DE RIEL DE 100 RE Y PISTA
MATERIAL MODIFICADO	LOS DURMIENTES 1,2 y 3 SERAN CORTADOS A 0.400m DEL BORDE DE RODAMIENTO LADO F.1		LOS DURMIENTES 1,2 y 3 SERAN CORTADOS A 0.400m DEL BORDE DE RODAMIENTO LADO F.4	LOS DURMIENTES 1,2 y 3 SERAN CORTADOS A 0.400m DEL BORDE DE RODAMIENTO LADO F.5	LOS DURMIENTES 1,2 y 3 SERAN CORTADOS A 0.400 m DEL BORDE DE RODAMIENTO LADO F.6

NUMERO DE APARATO	VIA	NUMERO DE DURMIENTES	COTA B (mm)	COTA A (mm)	COTA L (mm)	TIPO DE CRUCETA
6006	DIRECTA	18 15 12	652 590 553 F.2	558 496 462 F.2	970 910 870	DE IZQUIERDA DE 7.500
	DIRECTA	27 30 (DOS ACH.)	652 590 553 F.2	558 496 462 F.2	970 910 870	DE DERECHA DE 7.500
	DESVIADA	21 24 27 30	652 590 553 553 F.1	558 496 462 462 F.1	970 910 870 870	DE IZQUIERDA DE 7.500
6007	DESVIADA	6 9 12 15	652 575 565 553 F.3	558 481 471 462 F.3	970 900 890 870	ESPECIAL DE 12.000 DE DERECHA
6008	DESVIADA	6 9 12 15	652 575 565 553 F.4	558 481 471 462 F.4	970 900 890 870	ESPECIAL DE 12.000 DE DERECHA
6009	DESVIADA	6 9 12 15	652 575 565 553 F.5	558 481 471 462 F.5	970 900 890 870	ESPECIAL DE 12.000 DE DERECHA
6010	DESVIADA	6 9 12 15	652 575 565 553 F.6	558 481 471 462 F.6	970 900 890 870	ESPECIAL DE 12.000 DE DERECHA

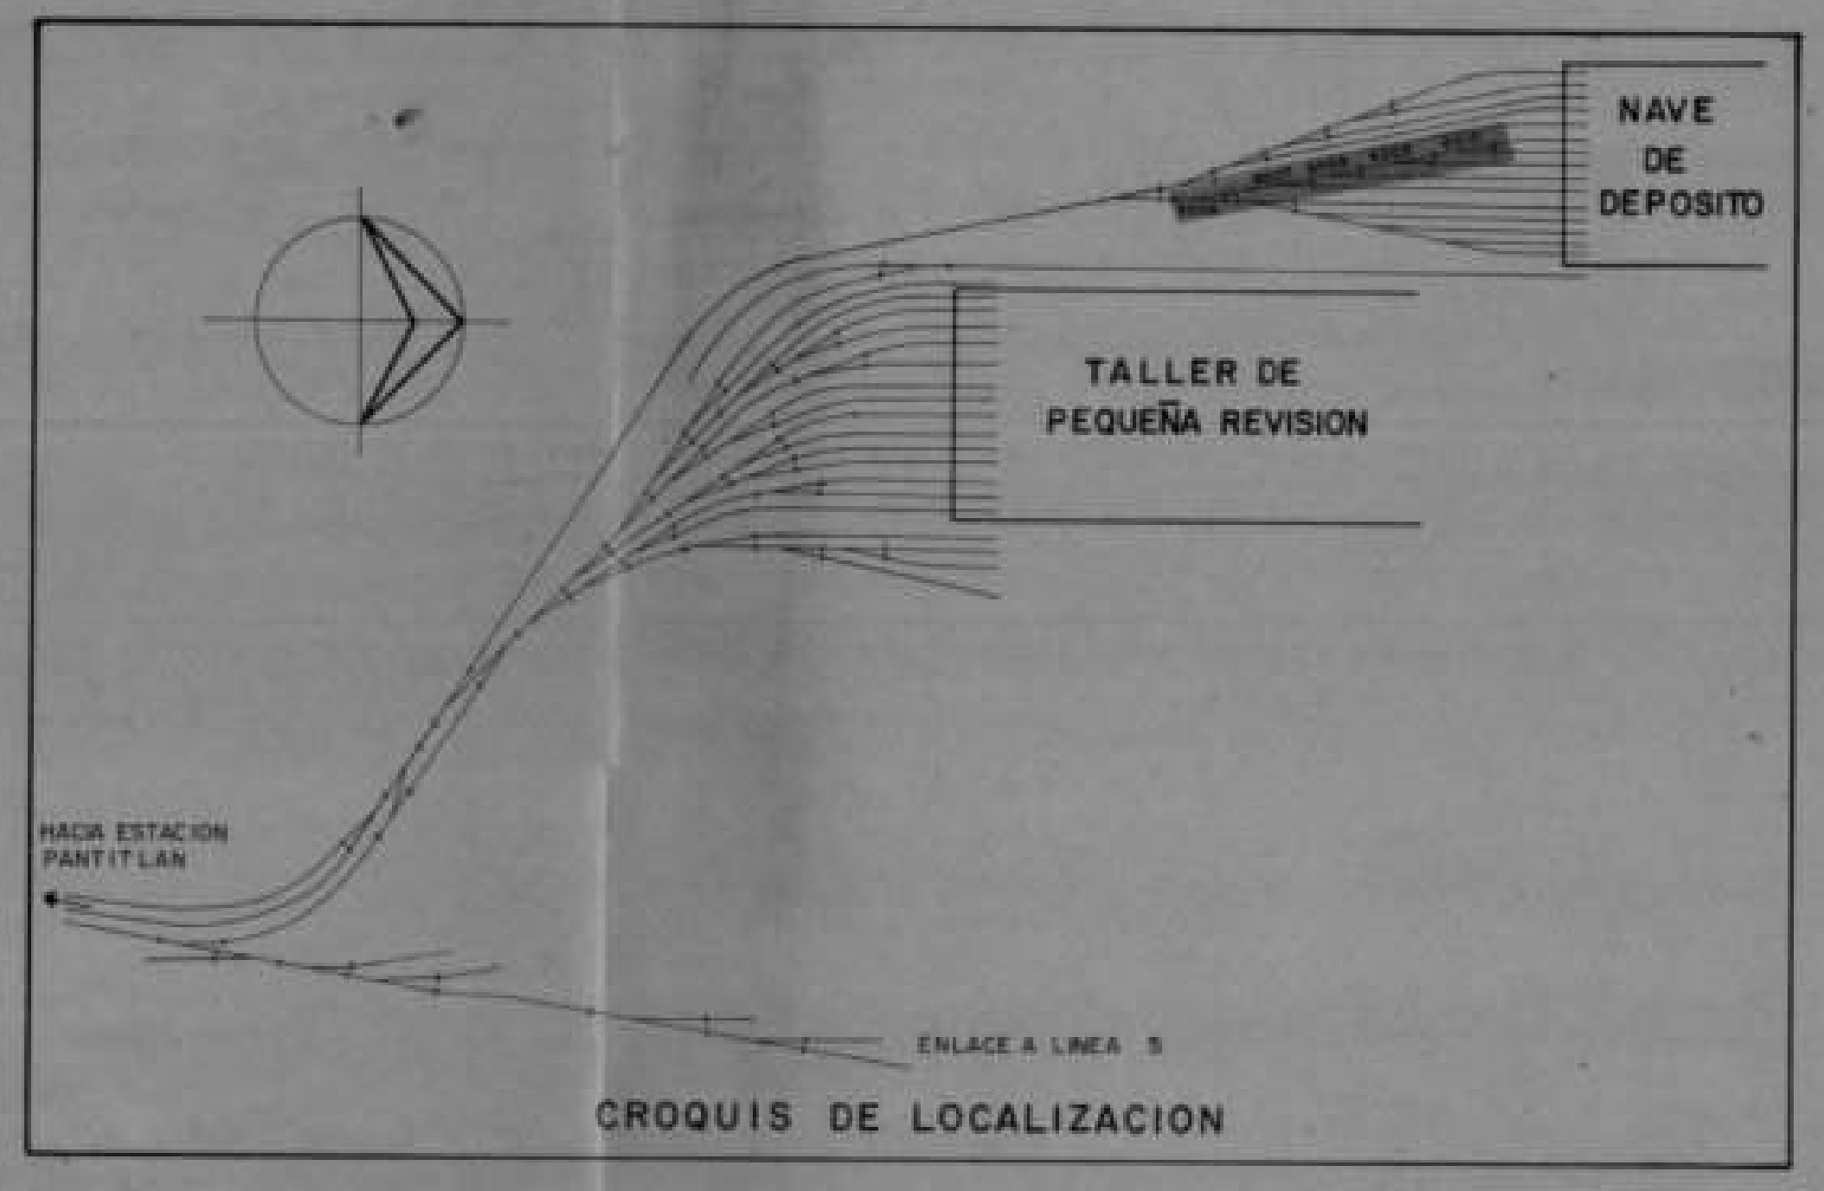
NAVE DE DEPOSITO
TALLER DE PEQUEÑA REVISION
HACIA ESTACION PANTITLAN
ENLACE A LINEA 5

CROQUIS DE LOCALIZACION

NOTAS:

1.- LOS APARATOS ESTAN CONFORME A LOS PLANOS DE CONJUNTO:
80-VI.17-000-III-75-2611-P (ENLACE Tg 0.20 A LA DERECHA)
85-VI.17-81268-III-1-943-P (ENLACE Tg 0.20 A LA IZQUIERDA)
EXCEPTUANDO LAS INDICACIONES MENCIONADAS EN EL PLANO

2.- LA UBICACION DEL PISO DE MANIOBRAS QUE SOPORTAN LOS MOTORES TR-44 ESTA DE ACUERDO AL PLANO 80-VI.17-000-III-76-2612-P

3.- REFERENCIAS

89-VI.13-46012-III-09-P (PROYECTO DE IMPLANTACION DE VIA-TRAZO)

4.- LAS CRUCETAS ESPECIALES DE 12.000m. ESTAN DE ACUERDO AL PLANO 81-VI.17-000-III-128-3784-P

5.- LA POSICION DE LAS CRUCETAS ESTAN CONFORME A LOS CROQUIS PROPORCIONADOS POR EL S.T.C.

6.- LOS MOTORES DE LOS APARATOS SIGUIENTES 6007, 6008, 6009 y 6010 NO SUFRIRAN NINGUN CAMBIO, TANTO EN SU UBICACION COMO EN SU FIJACION

7.- LA COTA A CORRESPONDIENTE A LA COTA B DE 0.553 ES DE 0.462

A ESTACION PANTITLAN
APARATO 6001
CONSULTAR PLANO: 89-VI.17-46012-III-01-P
APARATO 6006
P.de A.=1+595.937 S/T
1+596.169 S/V
T.de A.=1+616.561 S/V
CRUCETA DE 7.500 DE IZQ.
CRUCETA DE 7.500 DE IZQUIERDA
CRUCETA DE 7.500 DE DERECHA
RIEL DE 100 RE DE 7.654
J.A.
MONTAJE No.3 (F.2)
MONTAJE No.2 (F.2)
MONTAJE No.1 (F.1) (F.2)
F.1
F.2
4.500
RIEL DE 100 RE
RIEL DE 80 ASCE VIA ORDINARIA
APARATO 6007
P.de A.=1+623.619 S/T
1+624.215 S/V
MONTAJE No.3 (F.1) (F.3)
MONTAJE No.2 (F.1) (F.3)
MONTAJE No.1 (F.1) (F.3)
VER NOTA No.6
CRUCETA ESPECIAL DE 12.000 DE DERECHA
A NAVE DE DEPOSITO VIA G-6
APARATO 6008
P.de A.=1+644.215 S/T
1+644.611 S/V
MONTAJE No.3 (F.1) (F.4)
MONTAJE No.2 (F.1) (F.4)
MONTAJE No.1 (F.1) (F.4)
A NAVE DE DEPOSITO VIA G-7
APARATO 6009
P.de A.=1+664.626 S/T
1+665.022 S/V
MONTAJE No.3 (F.1) (F.5)
MONTAJE No.2 (F.1) (F.5)
MONTAJE No.1 (F.1) (F.5)
A NAVE DE DEPOSITO VIA G-8
APARATO 6010
P.de A.=1+685.037 S/T
1+685.433 S/V
MONTAJE No.3 (F.1) (F.6)
MONTAJE No.2 (F.1) (F.6)
MONTAJE No.1 (F.1) (F.6)
A NAVE DE DEPOSITO VIA G-9
CONSULTAR PLANO No. 89-VI.17-46012-III-11-R
A NAVE DE DEPOSITO VIA G-10

S I M B O L O G I A

▭	DURMIENTE SOPORTE DE AISLADOR Y DURMIENTE SOPORTE DEL MOTOR DE MANIOBRAS
▬	DURMIENTE NO CONFORME CON EL PLANO DE CONJUNTO
◠	AISLADOR SOBRE PLATILLO PARA LA BARRA DE TOMA DE CORRIENTE
▲	AISLADOR SOBRE PLATILLO PARA CRUCETA
J.A.	JUNTA AISLANTE A SUMINISTRAR CON EL APARATO DEL LADO DEL CORCHETE
▬	AISLADOR SOBRE ZOCLO PARA BARRA DE TOMA DE CORRIENTE

DEPARTAMENTO DEL DISTRITO FEDERAL
STC
SISTEMA DE TRANSPORTE COLECTIVO

ING. GERARDO FERRANDO BRAVO
DIRECTOR GENERAL

ING. FILIBERTO ZEPEDA TIJERINA
DIRECTOR DE OPERACION

ELECTROMETRO S.A.
PROYECTO

PROYECTO:
REALINEACION Y RENIVELACION DE VIAS EN OPERACION
METRO

ING. PABLO GUERRA CARDENAS
ING. ALBERTO GONZALEZ CEMICEROS

LINEA 1
IMPLANTACION DE VIA-FIJACION DE VIA
TRAMO: TALLERES ZARAGOZA
PLANO DE COLOCACION DE LOS APARATOS
6006,6007,6008,6009,6010

ARQ. JOSE LUIS BUENDIA M.
ING. GERARDO MUÑOZ GONZALEZ
ING. SERGIO RUELAS MONCAYO

STC
ARQ. MANUEL MEZA ZATARAIN
STC
ING. SALOMON SOLAY ZYMAN
STC
ING. ROBERTO CASTAÑEDA CHAVEZ
STC
ING. ERASMO CUATECONTZI CASTELLANOS
STC
ING. MARCO A. ROCHA URRINA
STC
ING. ALFREDO NAVARRETE YAÑEZ

ESCALA
1 : 100
ACOTACIONES
EN METROS
FECHA
SEPTIEMBRE / 1989

APROBO
ING. ISMAEL GONZALEZ TECUATL
REVISO
ING. J. BARRIOS R.
PROYECTO
ARQ. J. SILVA Z.
PLANO No.
89-VI.17-46012-III-02-P
INPLAT
ING. FERNANDO CASTRO C.

(0.65 x 1.70)