TABLA DE DATOS COMPLEMENTARIOS

VIA	NUMERO DE CURVA	Δ	Rc	ST	Lc	Lc'	Lc"	I DISTANCIA	II DISTANCIA	III DISTANCIA	IV DISTANCIA	LONGITUD TOTAL *
G15	a	22° 34' 22.89"	60.000	11.974	23.638	23.921	24.031	16.296	19.830			60.157
G14	b	11° 15' 50.70"	60.000	5.917	11.796	11.937	11.992	40.800	5.486			58.278
G13	c	11° 12' 29.90"	60.000	5.887	11.737	11.878	11.932	60.048	5.494			77.474
G12	d	11° 19' 26.30"	60.000	5.949	11.858	12.000	12.055	79.933	4.696			96.684
G11	e	11° 17' 25.80"	60.000	5.931	11.823	11.965	12.020	99.480	4.387			115.887

S I M B O L O G I A

Δ = DEFLEXION
Rc = RADIO
ST = SUBTANGENTE
Lc = LONGITUD DE CURVA SOBRE EJE DE VIA
Lc' = LONGITUD DE CURVA SOBRE RIEL DE MAYOR DESARROLLO
Lc" = LONGITUD DE CURVA SOBRE PISTA DE MAYOR DESARROLLO
I = DISTANCIA PC AL TALON DEL APARATO.
II = DISTANCIA PT A LA ZONA DE TRANSICION, CONCRETO/BALASTO.
III = DISTANCIA DEL TALON DE APARATO A LA ZONA DE TRANSICION, CONCRETO/BALASTO
IV = DISTANCIA DEL TALON DE APARATO A LA PUNTA DE APARATO.
* = LONGITUD TOTAL: Lc" + I + II + III + IV

RESUMEN GENERAL DE LA DISTRIBUCION DE DURMIENTES

TIPO DE DURMIENTES

VIA	O	100 SA	GA	100 A	GC	100 T	SACR 1	SACR 2	SACR 3	SCCR 1	SCCR 2	SCCR 3	100SACR	SA	SC	A
G15	53	2		4			1	1	1					8	8	4
G14	40	1	1	5			1	1	1	2	2	2		14	5	4
G13	61	1	1	5	1		1	1	1	2	2	2		20	3	4
G12	79	1	1	5	1		1	1	1	2	2	2		27	3	4
G11	96	2	2	4	1		1	1	1	2	2	2		35	2	5
TOTAL	329	7	5	23	3		5	5	5	8	8	8		104	21	21

S I M B O L O G I A

▬ AISLADOR SOBRE ZOCLO
EJE DE VIA.
J.A. EJE DE JUNTA AISLANTE.
100SA DURMIENTE SOPORTE CON AISLADOR SIN GUIADO PARA RIEL DE 100RE EN TAN. ó EN CURVA DE R ≥ a 500.000 M
100SC DURMIENTE SOPORTE CON AISLADOR SIN GUIADO PARA RIEL DE 100RE CON CURVA DE R < a 500.000 M
100A DURMIENTE ORDINARIO PARA RIEL DE 100RE EN TAN. ó EN CURVA DE R ≥ a 500.000 M
100O DURMIENTE ORDINARIO PARA RIEL DE 100RE CON CURVA DE R < a 500.000 M.
100T DURMIENTE DE TRANSICION DE RIEL DE 100RE, **A—C, C—A**.
SACR DURMIENTE SOPORTE DE AISLADOR PARA CRUCETA EN TAN. ó EN CURVA DE R ≥ a 500.000 M
SCCR DURMIENTE SOPORTE DE AISLADOR PARA CRUCETA CON CURVA DE R < a 500.000 M.
J.M. EJE DE JUNTA MECANICA.
100SACR DURMIENTE SOPORTE CON AISLADOR PARA CRUCETA EN RIEL DE 100RE EN TAN. ó EN CURVA CON R ≥ a 500.000 M
O DURMIENTE DE CONCRETO ORDINARIO
SA DURMIENTE SOPORTE DE AISLADOR SIN GUIADO PARA RIEL 80 ASCE EN TAN. ó EN CURVA DE R ≥ a 500.000 M
SC DURMIENTE SOPORTE DE AISLADOR SIN GUIADO PARA RIEL 80 ASCE EN CURVA DE R < a 500.000 M.
GA DURMIENTE SOPORTE DE AISLADOR (AMBOS LADOS) SIN GUIADO PARA RIEL DE 80ASCE EN TAN. ó EN CURVA DE R ≥ a 500.000 M
GC DURMIENTE SOPORTE DE AISLADOR (AMBOS LADOS) SIN GUIADO PARA RIEL DE 80ASCE EN CURVA DE R < a 500.000 M
A DURMIENTE ORDINARIO, DE MADERA.

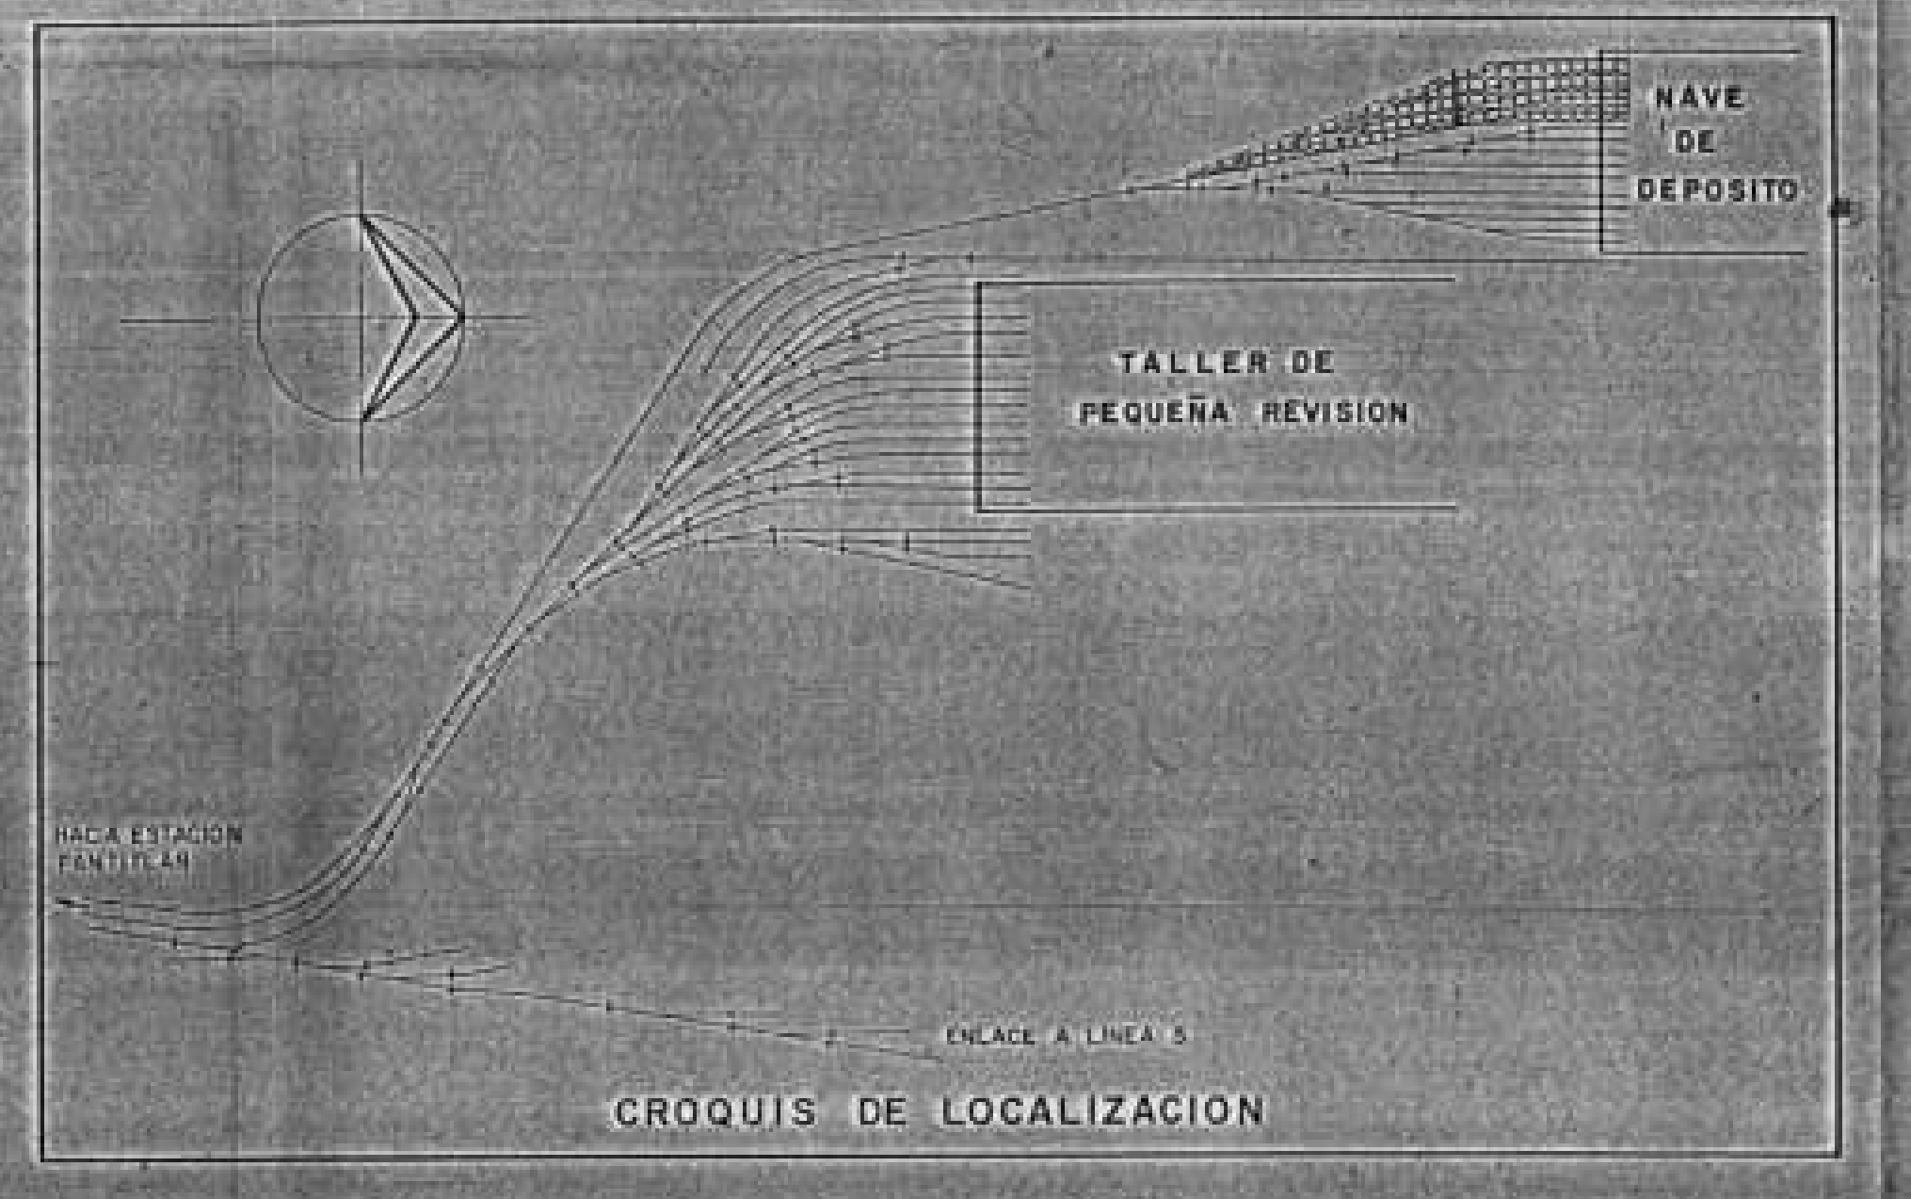

CROQUIS DE LOCALIZACION

COLOCACION DE LA VIA SOBRE DURMIENTE DE MADERA EN ZONA DE BALASTO

SIN ESCALA

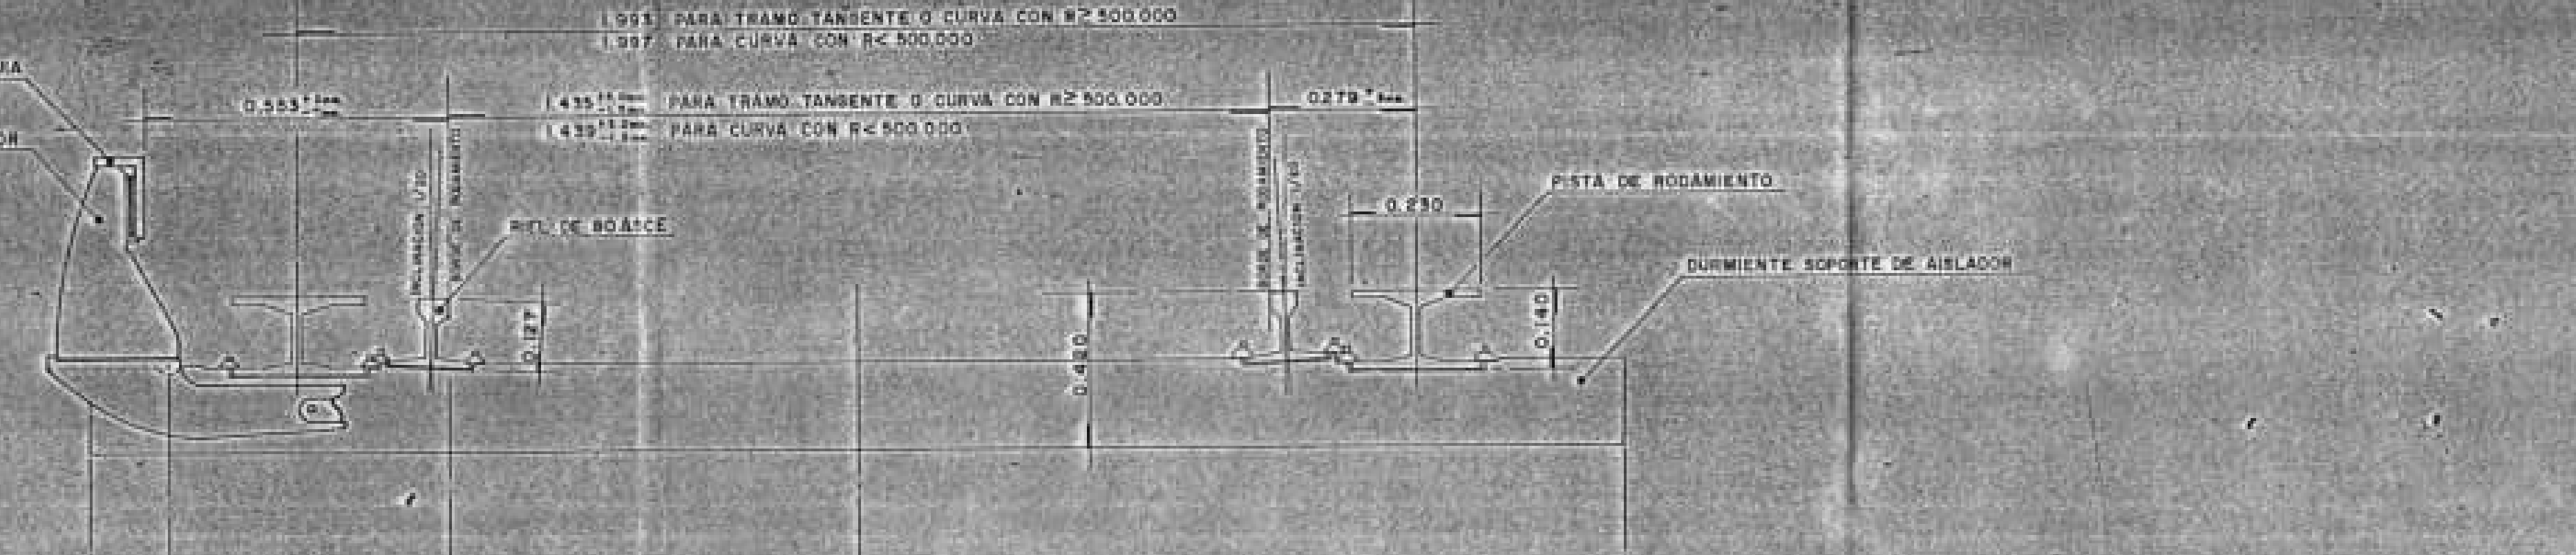
1.993 PARA TRAMO TANGENTE O CURVA CON R ≥ 500.000
1.997 PARA CURVA CON R < 500.000
BARRA GUIA
AISLADOR
0.553
1.435 PARA TRAMO TANGENTE O CURVA CON R ≥ 500.000
1.439 PARA CURVA CON R < 500.000
0.279
RIEL DE 80 ASCE
PISTA DE RODAMIENTO
DURMIENTE SOPORTE DE AISLADOR
0.230
0.127
0.420
0.140
0.520
1.350
1.350
2.700

COLOCACION DE LA VIA SOBRE DURMIENTE DE CONCRETO EN ZONA DE BALASTO (TIPO "O")

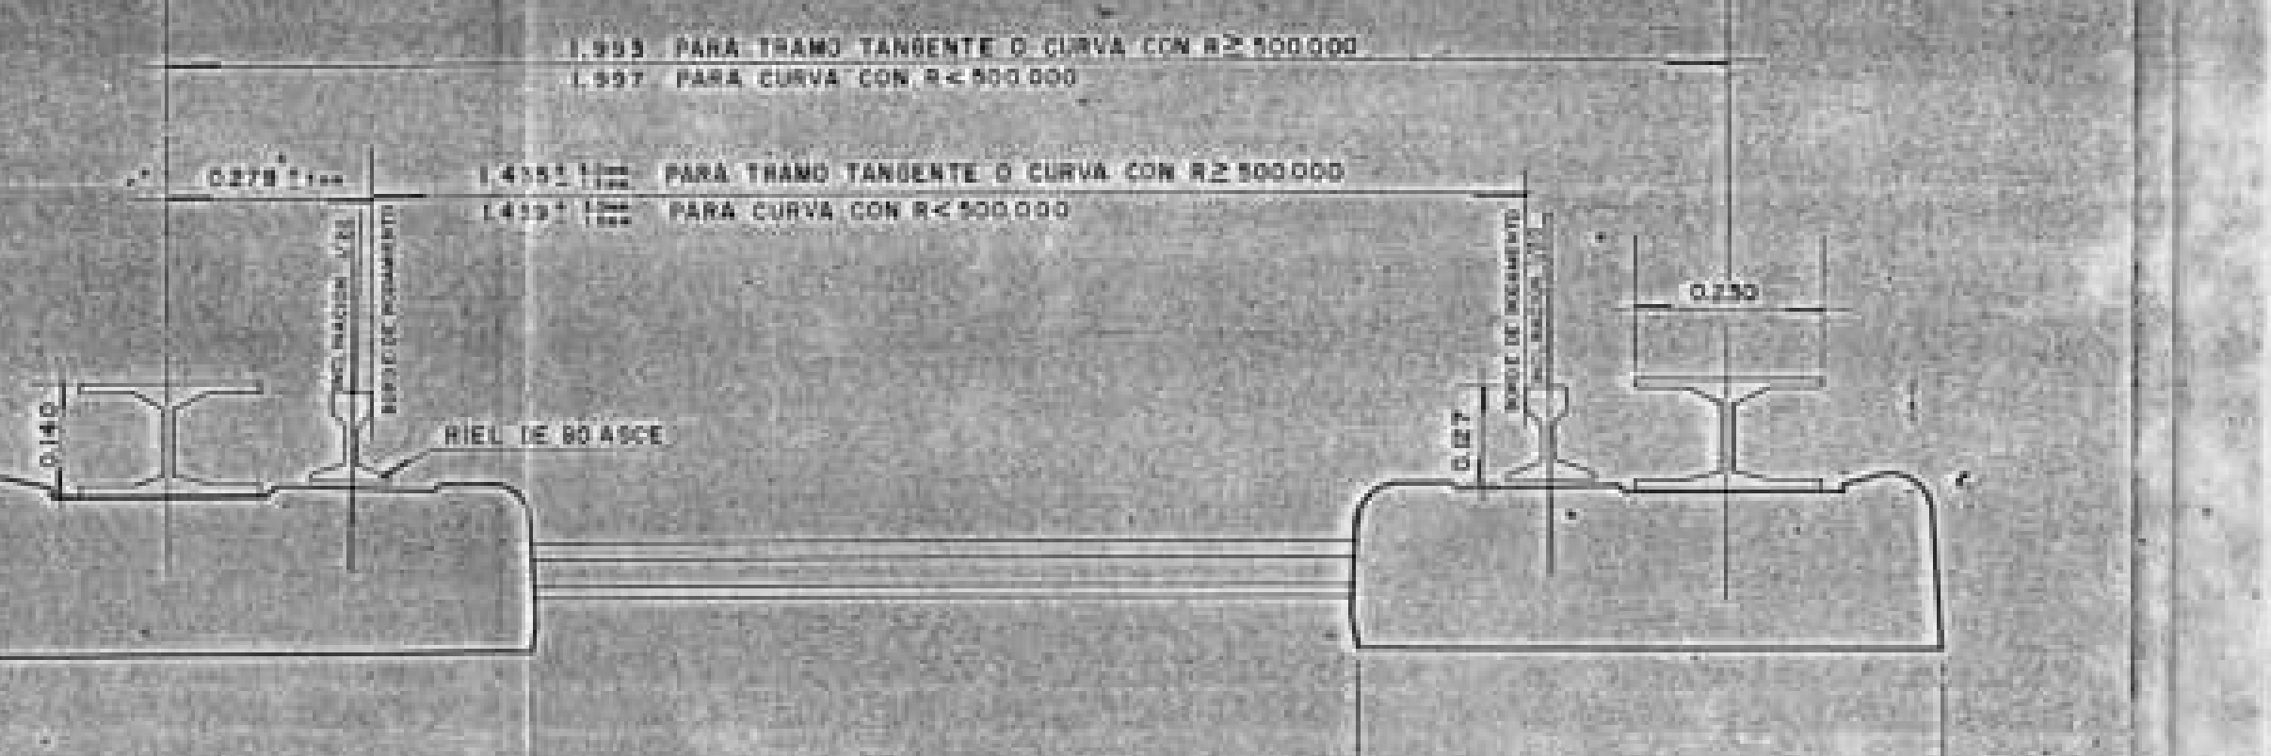
1.993 PARA TRAMO TANGENTE O CURVA CON R ≥ 500.000
1.997 PARA CURVA CON R < 500.000
0.278
1.435 PARA TRAMO TANGENTE O CURVA CON R ≥ 500.000
1.439 PARA CURVA CON R < 500.000
0.230
0.140
0.127
RIEL DE 80 ASCE
0.750
1.053
0.750
2.553

NOTAS:

1.- ESTE PLANO SE EJECUTO CON LAS "ESPECIFICACIONES PARA EL PROYECTO Y CONSTRUCCION DE LAS LINEAS DEL METRO DE LA CIUDAD DE MEXICO", EDITADAS POR COVITUR.

VOLUMEN	1
LIBRO	2
PARTE	2.02
SECCION	2.02.03
CAPITULO	2.02.03.002
CLAUSULA	2.02.03.002.F.

2.- SE COMPLEMENTA CON LOS PLANOS:
No. 89-VI.17-46012-III-01-P. (APARATOS 6002, 6003, 6004, 6005)
No. 89-VI.13-46012-III-09-P. (IMPLANTACION DE VIA–TRAZO)
No. 89-VI.16-46012-III-14-P. (RECTIFICACION DE NIVELES DE RASANTE)

3.- LA LONGITUD DE LAS VIAS SE CALCULO SOBRE LA PISTA DE MAYOR DESARROLLO Y LA DISTRIBUCION DE DURMIENTES SOBRE EL RIEL DE MAYOR DESARROLLO.

4.- LOS CADENAMIENTOS ESTAN REFERIDOS AL EJE DE VIA–TRAZO.

5.- EN CASO DE UTILIZAR DURMIENTES DE CONCRETO EN ZONA DE J.A., LA SEPARACION ENTRE LOS EJES DE DURMIENTES SERA DE 0.484 M

6.- LOS DURMIENTES CON AISLADOR CONSERVAN SU POSICION ORIGINAL.

3

DEPARTAMENTO DEL DISTRITO FEDERAL
STC
SISTEMA DE TRANSPORTE COLECTIVO

ING. GERARDO FERRANDO BRAVO
DIRECTOR GENERAL

ING. FILIBERTO ZEPEDA TIJERINA
DIRECTOR DE OPERACION

ELECTRO METRO S.A.
PROYECTO

PROYECTO:
REALINEACION Y RENIVELACION DE VIAS EN OPERACION
M E T R O

ING. PABLO GUERRA CARDENAS
ING. ALBERTO GONZALEZ CENICEROS

LINEA 1
IMPLANTACION DE VIA-FIJACION DE VIA
TRAMO: TALLERES ZARAGOZA
DISTRIBUCION DE DURMIENTES, LOCALIZACION DE J.A. EN VIAS DE ACCESO A NAVE DE DEPOSITO.
VIAS G11 A G15

ARQ. JOSE LUIS BUENDIA MARTINEZ
ARQ. GERARDO MUÑOZ GONZALEZ
ING. SERGIO HUELLAS MONCAYO

S.T.C.
ARQ. MANUEL MEZA ZATARAIN
S.T.C.
ING. SALOMON SOLAY ZYMAN
S.T.C.
ING. ROBERTO CASTAÑEDA CHAVEZ
S.T.C.
ING. ERASMO CUATECONTZI CASTELLANOS
S.T.C.
ING. MARCO A. ROCHA URBINA
S.T.C.
ING. ALFREDO NAVARRETE YAÑEZ

ESCALA: INDICADAS
ACOTACIONES: EN METROS
FECHA: SEPTIEMBRE/89

APROBO: ING. ISMAEL GONZALEZ TECUATL
REVISO: ING. J. RUBIOS R.
PROYECTO: ARQ. J. SEAN I.
PLANO No. 89-VI.17-46012-III-12-P
INPLAT: ING. FERNANDO CASTRO CARRANZA

0.65 X 2.00 mts.