M. Carbajal T.
V. González D.
J. Bautista T.
A. Martínez

NUMERO DE APARATO	9301	8301
MATERIAL SUPRIMIDO	10 MONTAJES COMPLETOS DE AISLADOR SOBRE PLATILLO DURMIENTES 3,6,9,12,15,18,21,24,27,30(LADO VIA DESVIADA). 1 DURMIENTE DE 2.800 mts. (7) 1 DURMIENTE DE 4.100 mts. (4)	10 MONTAJES COMPLETOS DE AISLADOR SOBRE PLATILLO DURMIENTES 3,6,9,12,15,18,21,24,27,30(LADO VIA DIRECTA) 1 DURMIENTE DE 2.800 mts. (7) 1 DURMIENTE DE 4.100 mts. (4)
MATERIAL AGREGADO	1 DURMIENTE DE 4.100 mts. (7) 1 DURMIENTE DE 2.800 mts. (4)	1 DURMIENTE DE 4.100 mts. (7) 1 DURMIENTE DE 2.800 mts. (4)
MATERIAL MODIFICADO		

DETALLE DE LAS CABEZAS DE LOS DURMIENTES

(AISLADOR SOBRE PLATILLO)

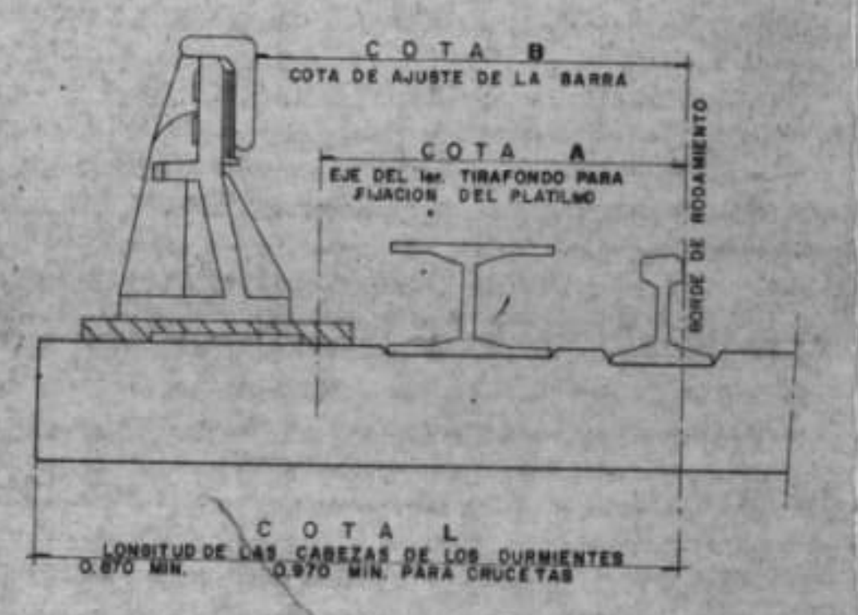
COTA B
COTA DE AJUSTE DE LA BARRA
COTA A
EJE DEL 1er. TIRAFONDO PARA FIJACION DEL PLATILLO
BORDE DE RODAMIENTO
COTA L
LONGITUD DE LAS CABEZAS DE LOS DURMIENTES
0.870 MIN. 0.970 MIN. PARA CRUCETAS

DETALLE DE LAS CABEZAS DE LOS DURMIENTES

(AISLADOR SOBRE ZOCLO)

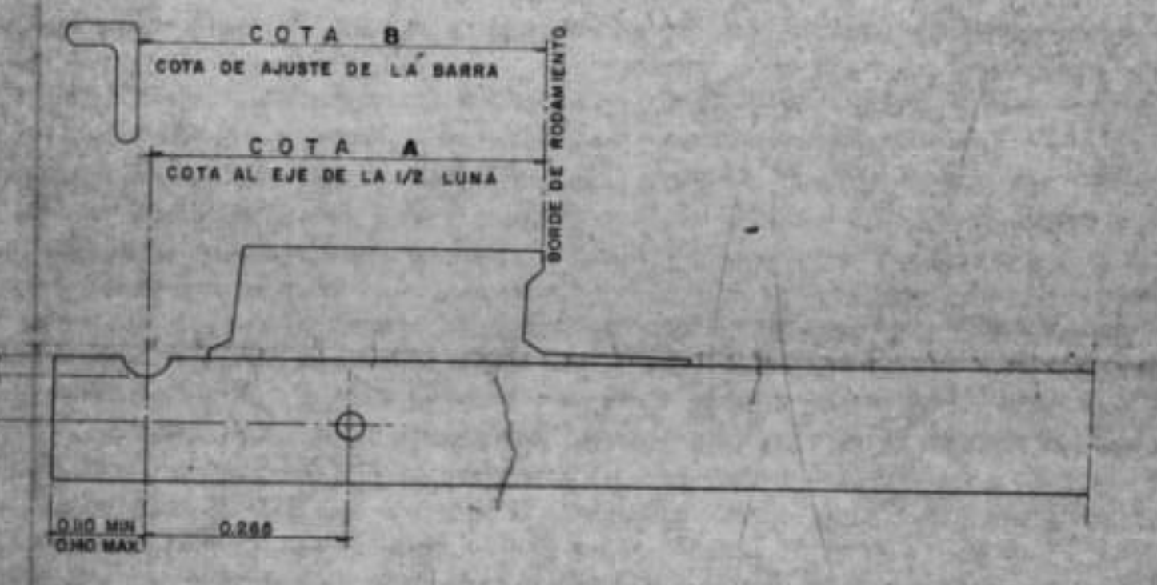

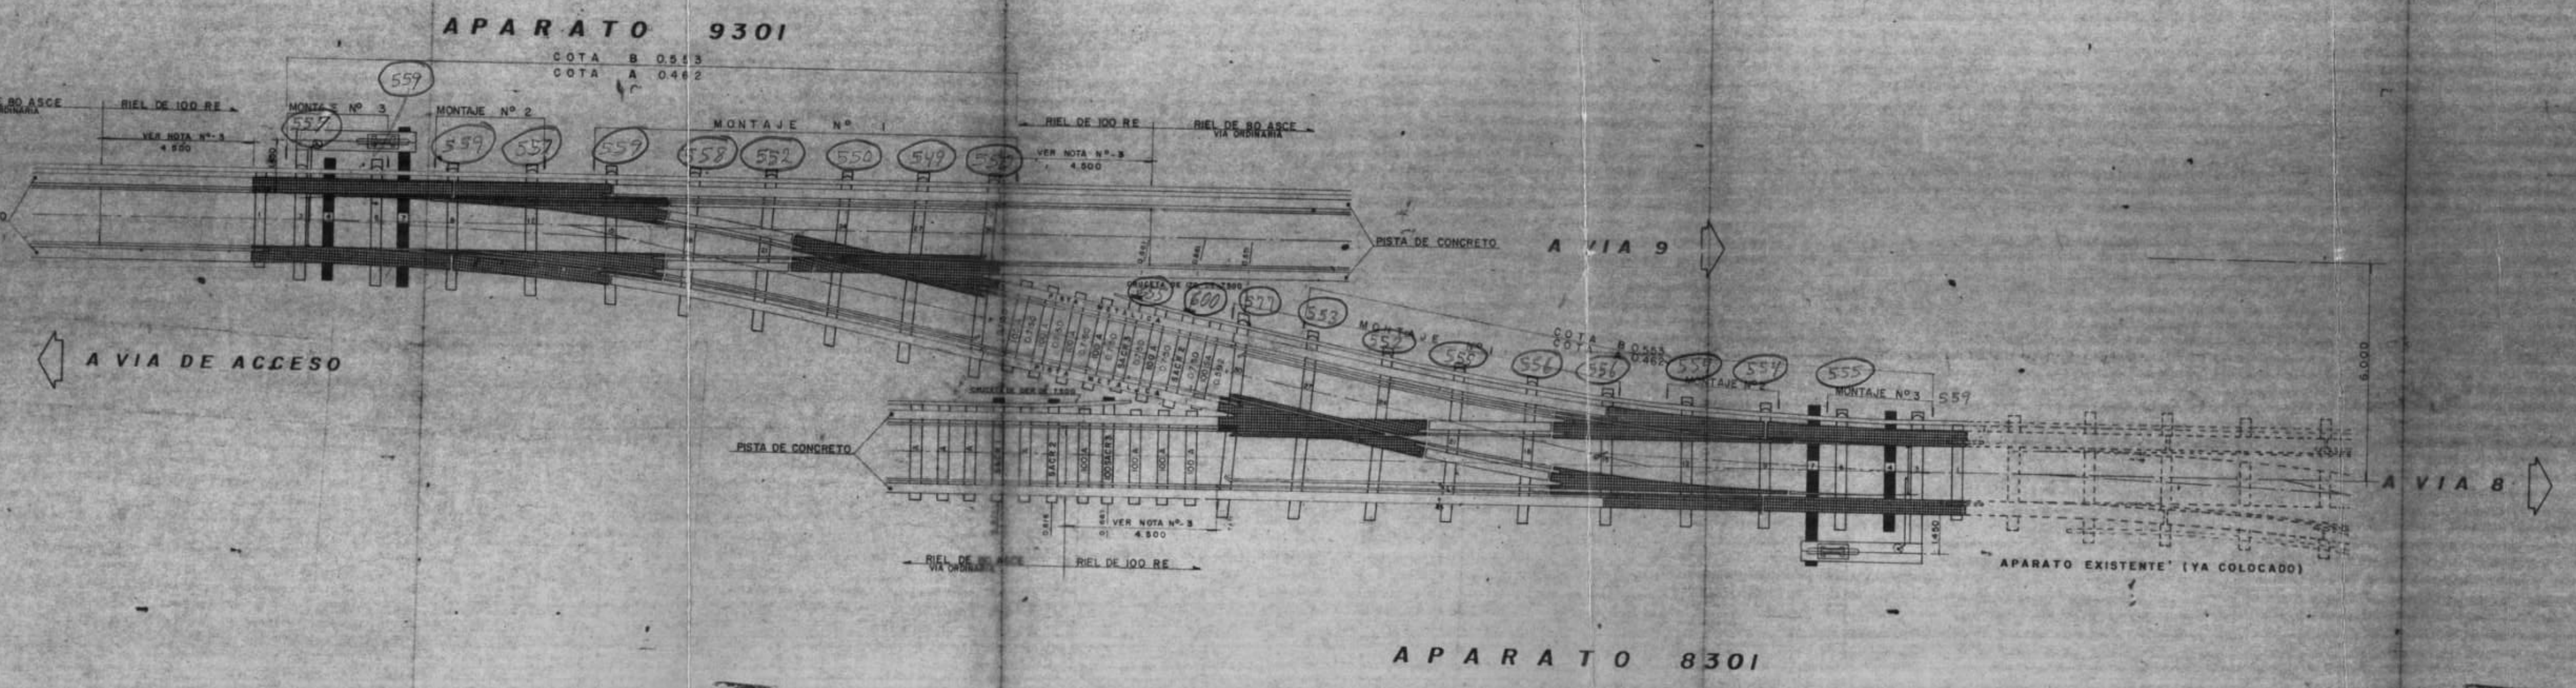

NOTAS:

1.- LOS APARATOS ESTAN DE ACUERDO AL PLANO 80-VI.17-000-III-76-2611-P. (ENLACE Tg 0.20 A LA DER.) EXCLUYENDO LAS INDICACIONES MENCIONADAS EN ESTE PLANO.

2.- LA PALANCA TALONABLE Y REVERSIBLE ESTA DE ACUERDO AL PLANO No. 80-VI.17-000-III-78-2614-P.

3.- LAS PISTAS METALICAS A COLOCAR DEBERAN TENER UNA LONGITUD MINIMA DE 6.000 m. HASTA LLEGAR A UNA PISTA DE CONCRETO.

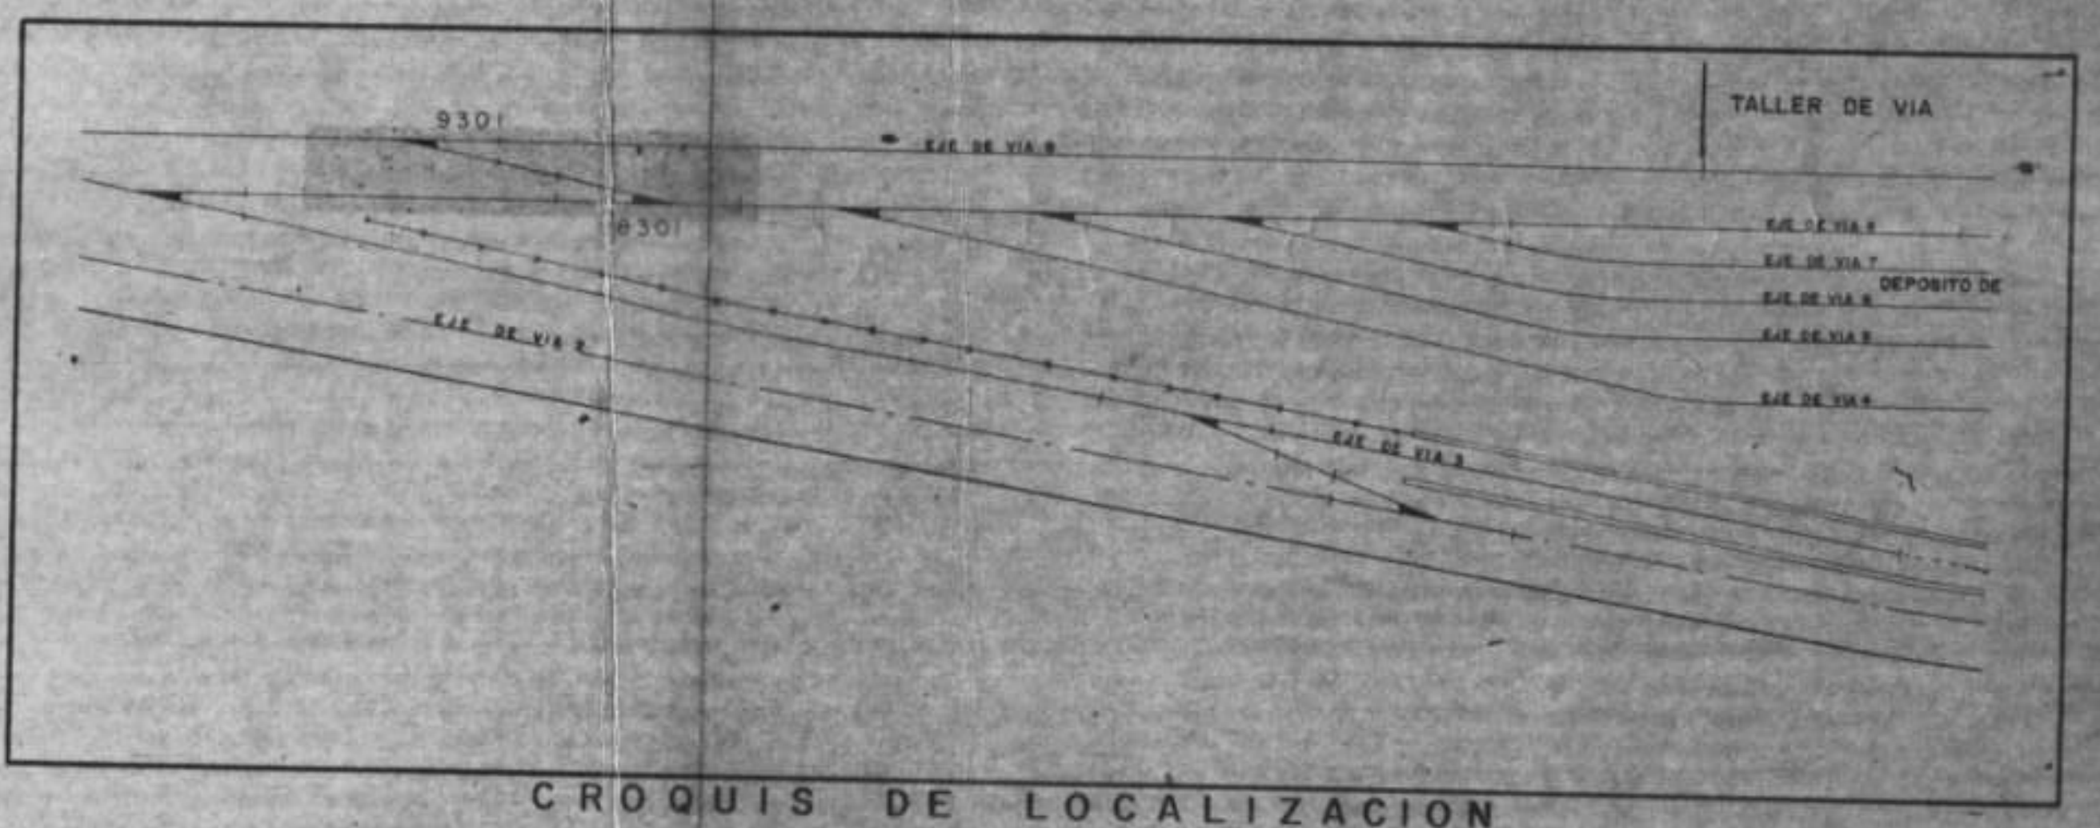

CROQUIS DE LOCALIZACION

DEPARTAMENTO DEL DISTRITO FEDERAL
COMISION DE VIALIDAD Y TRANSPORTE URBANO
covitur

ING. FRANCISCO NOREÑA CASADO
VOCAL EJECUTIVO

ISTME
PROYECTO

PROYECTO:
SISTEMA DE TRANSPORTE COLECTIVO
METRO

ARQ. ANGEL BORJA NAVARRETE	ING. MANUEL DIAZ CANALES	ARQ. JOSE LUIS BUENDIA M.

TALLERES ZARAGOZA
IMPLANTACION DE VIA-FIJACION DE VIA
VIAS 8-9
PLANO DE COLOCACION DE LOS APTS. Tg. 0.20 No. 8301 Y 9301

ING. ALEJANDRO VAZQUEZ V.
APROBO
ING. RAMON CUESTA L.
REVISO
ING. ISMAEL GONZALEZ T.

SOFRETU ING. D. HEURTEUX	COVITUR GCIA. O.E. ING D. LUCE V. COORDINACION	ESCALA 1:100	REVISO ING. J. ARRIAGA C.	PROYECTO ING. M. ALAMO P.
		ACOTACIONES METROS	PLANO No. 81-VI.17-553-III-10-3905-P	
		FECHA 7-SEPTIEMBRE-1981	MODIFICACION No.	