## DIAGRAMA DE LAS LÍNEAS DIRECTRICES

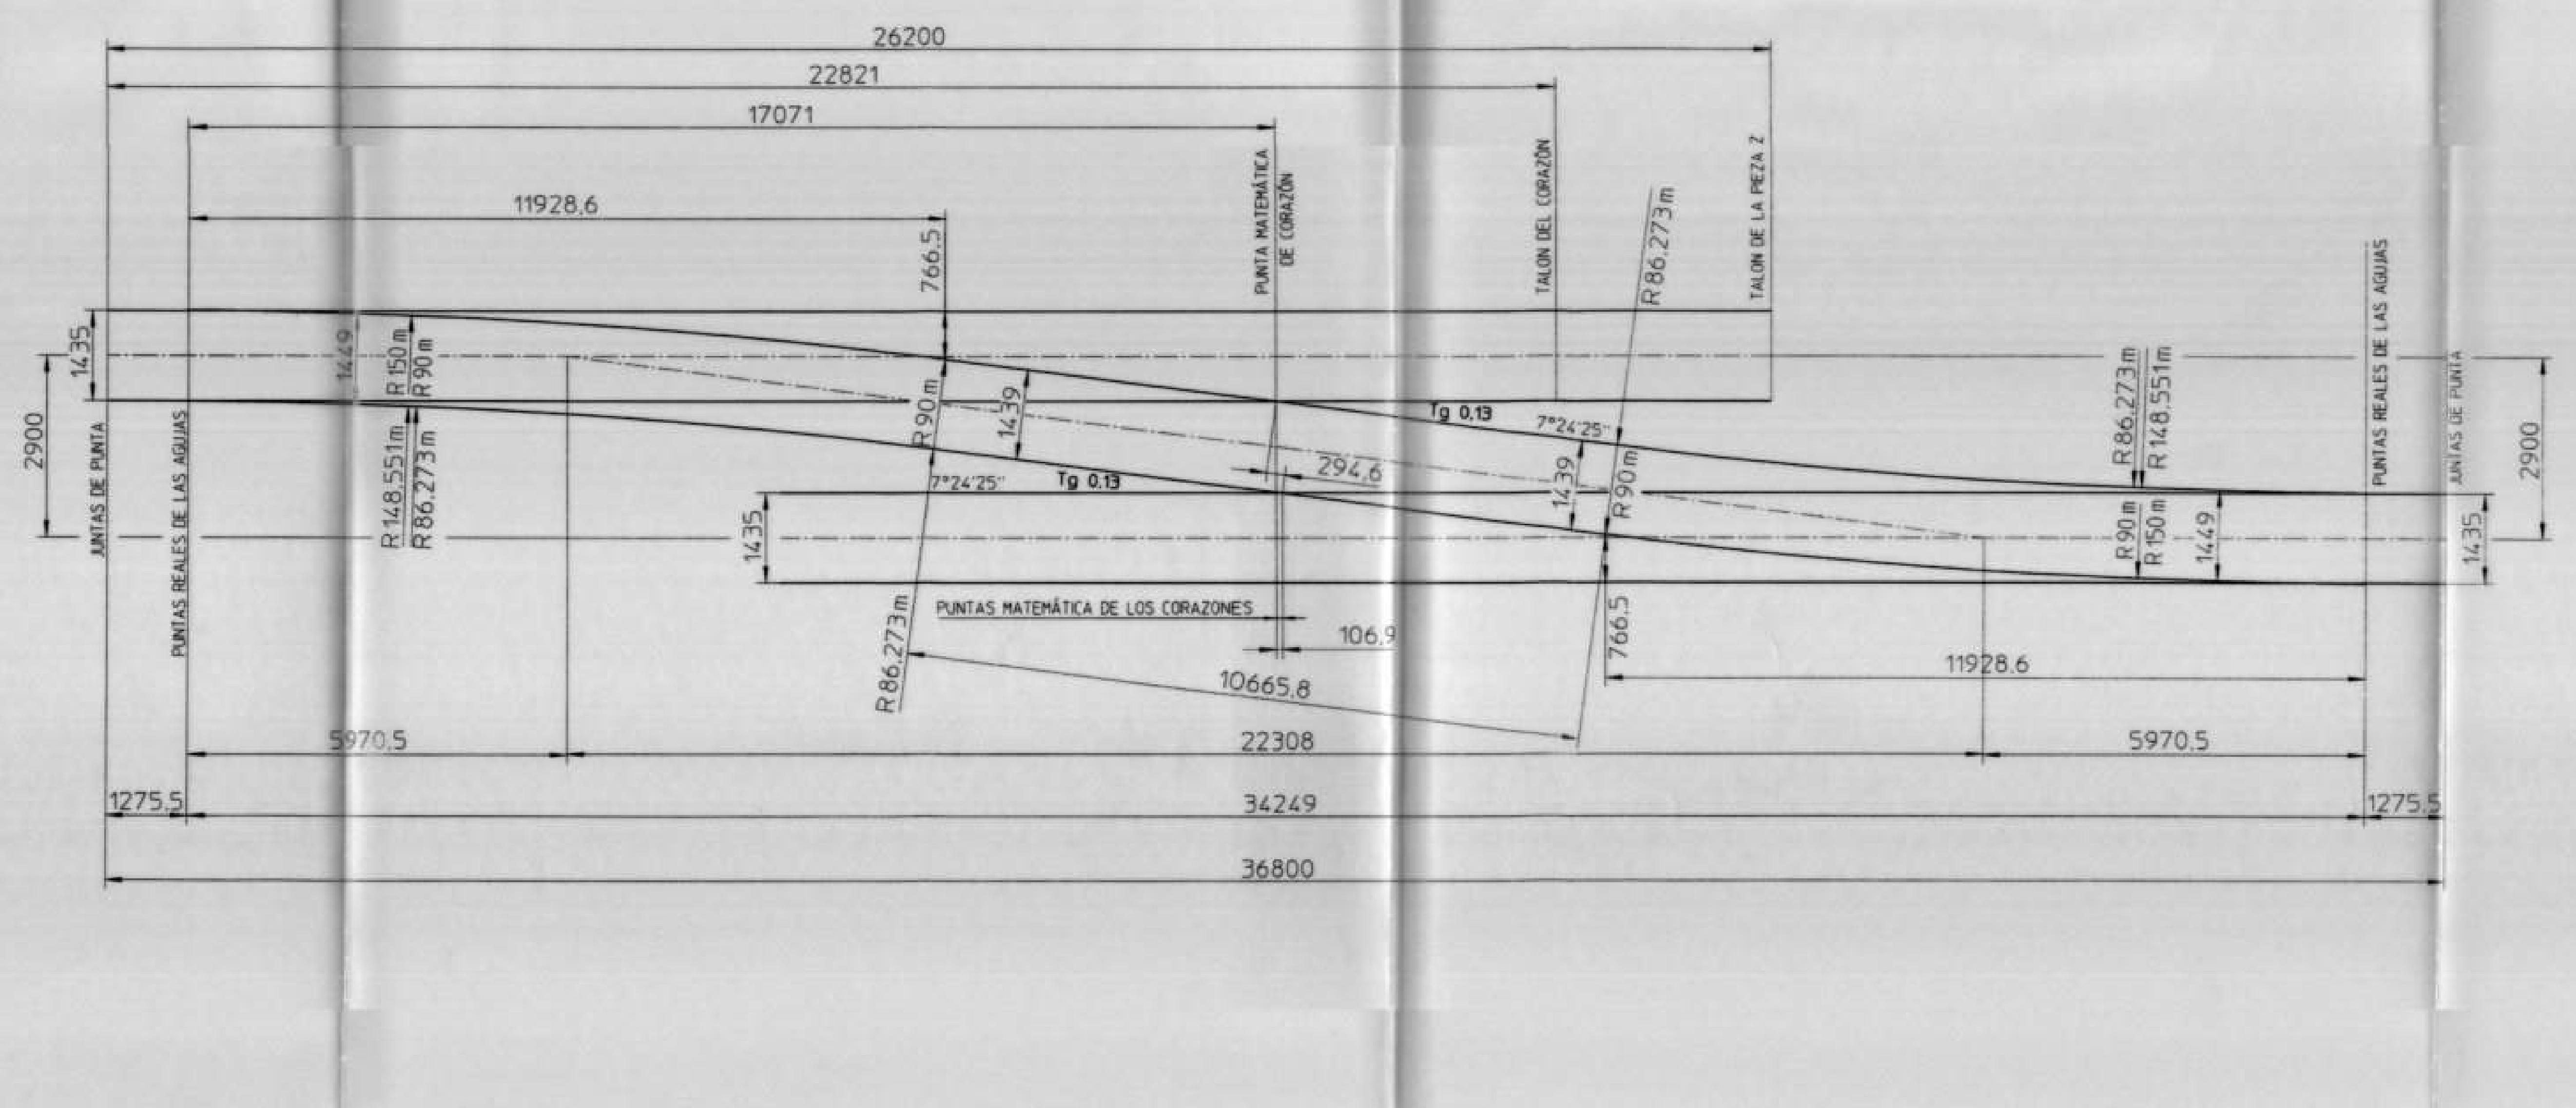

## DIAGRAMA DE LAS AGUJAS

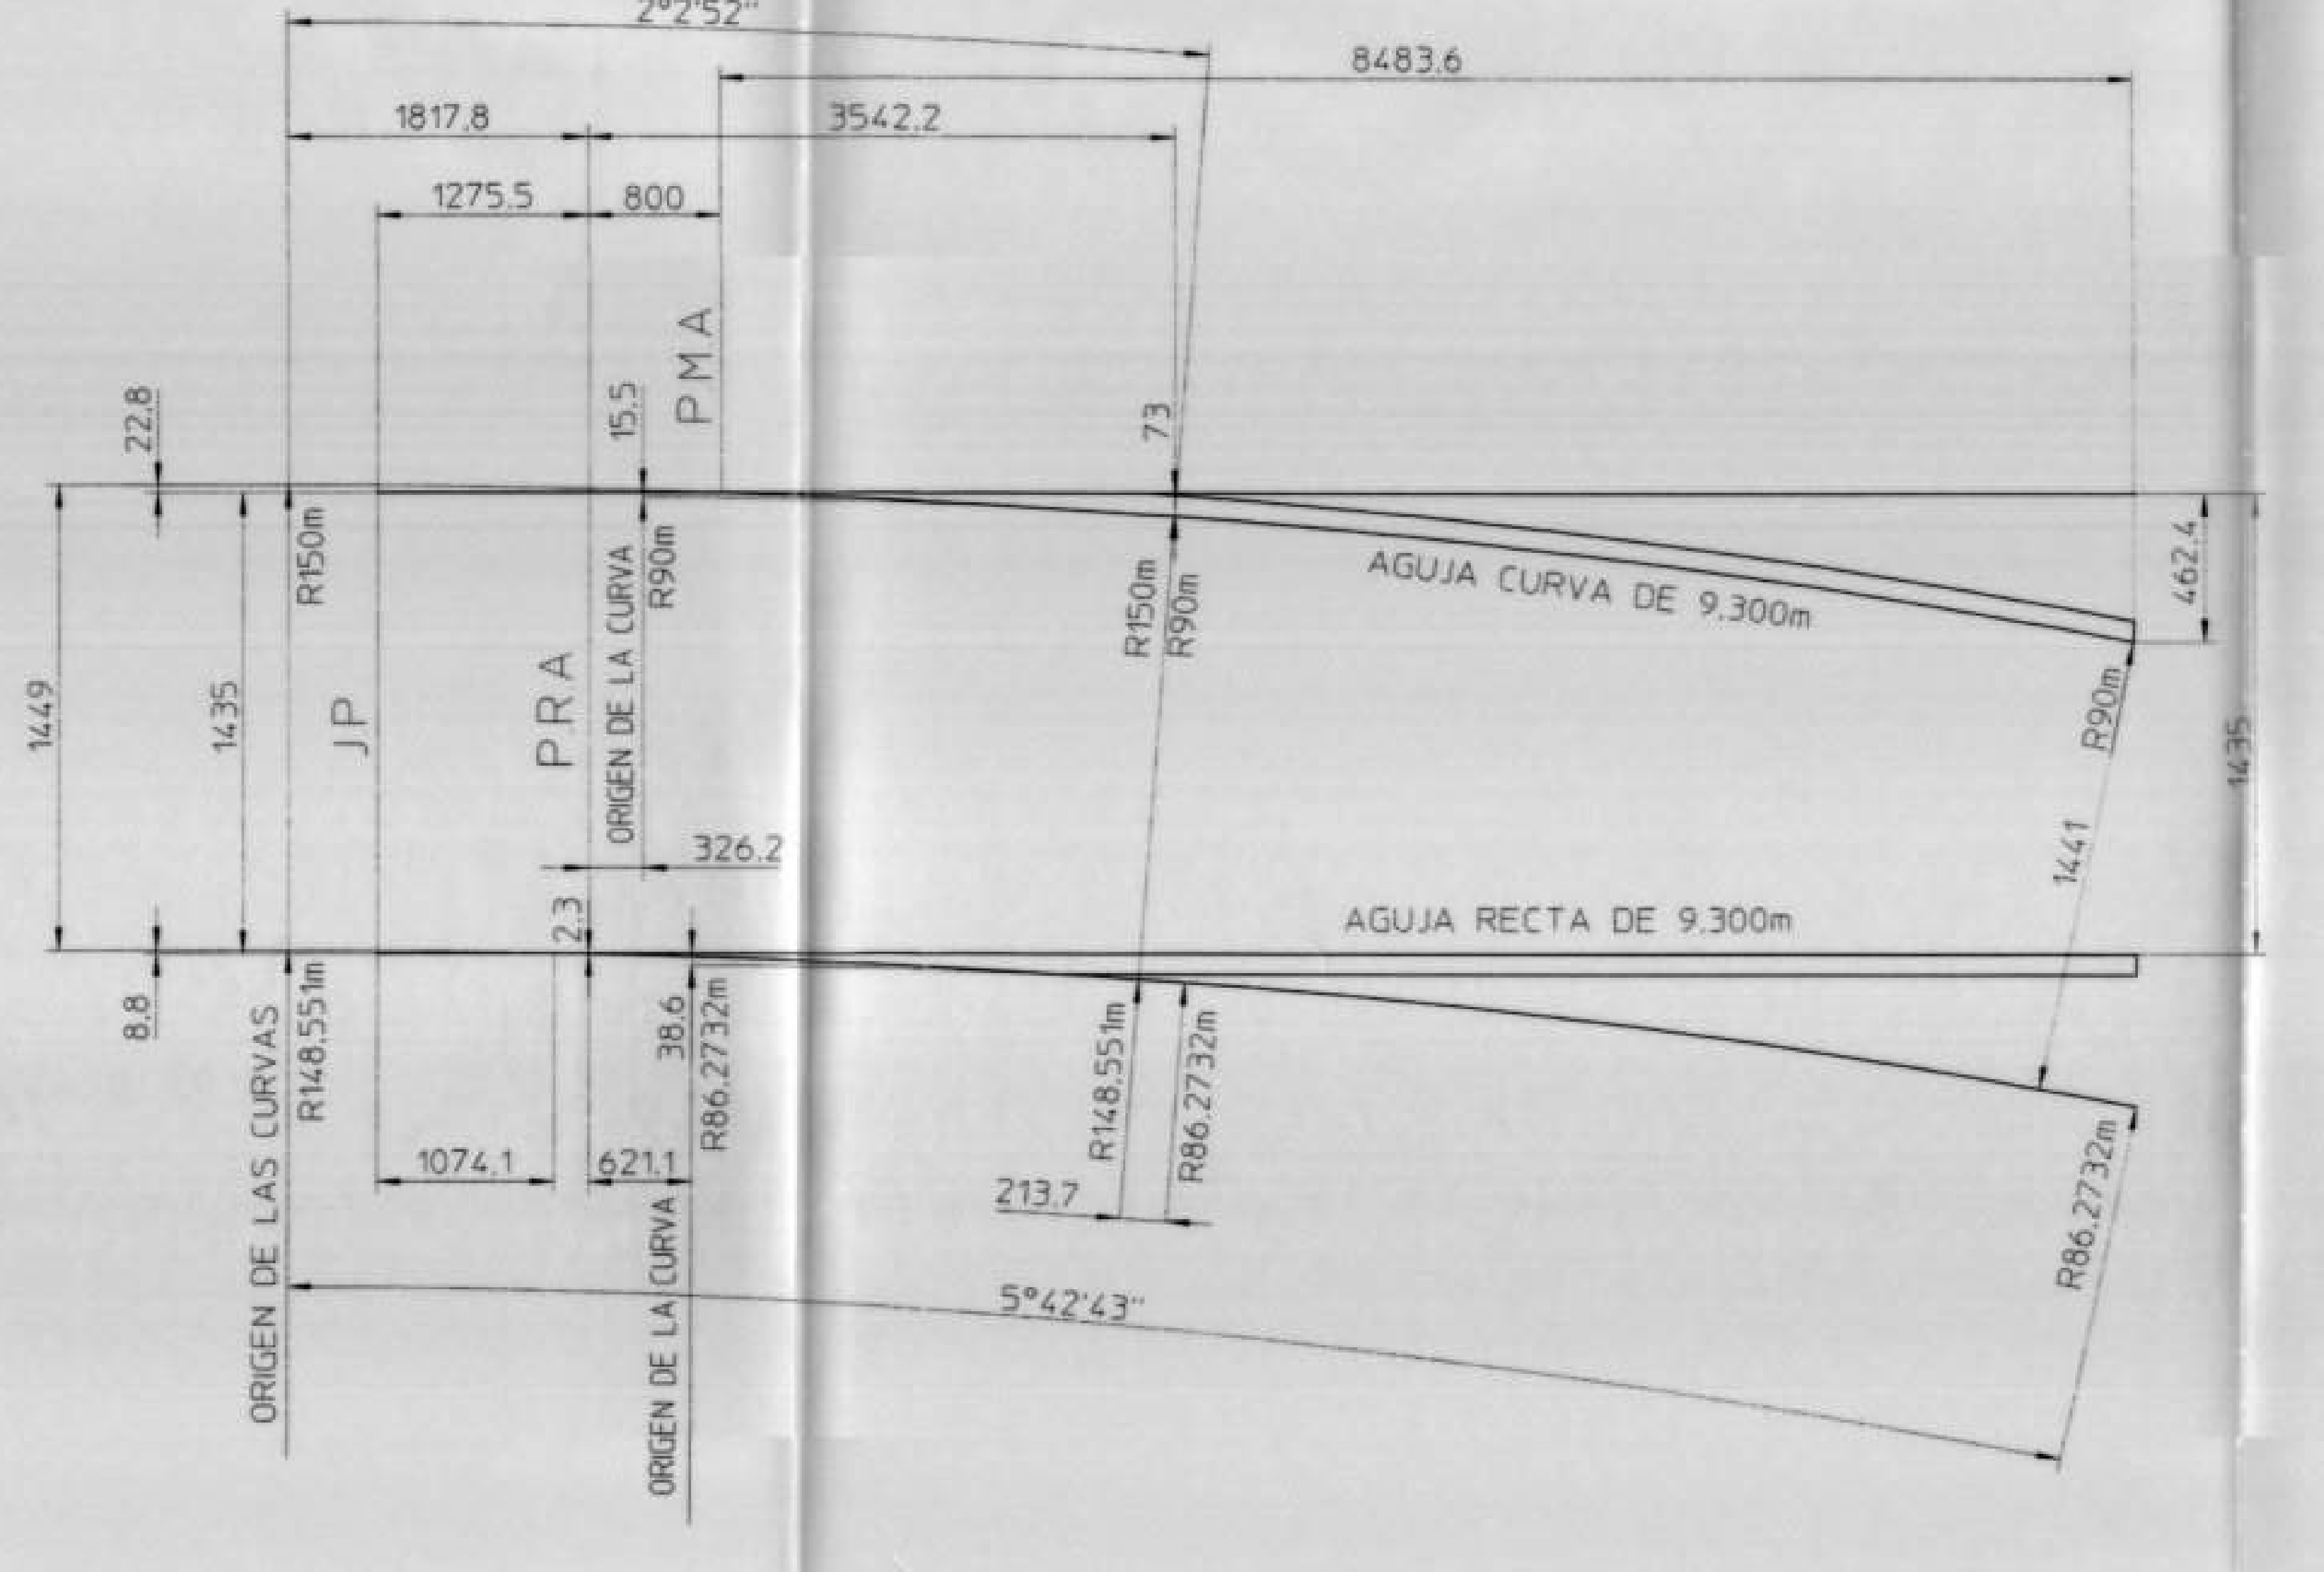

### DETALLE DE LAS CABEZAS DE LOS DURMIENTES
AISLADOR SOBRE PLATILLO
Consultar plano N°6.000.0008

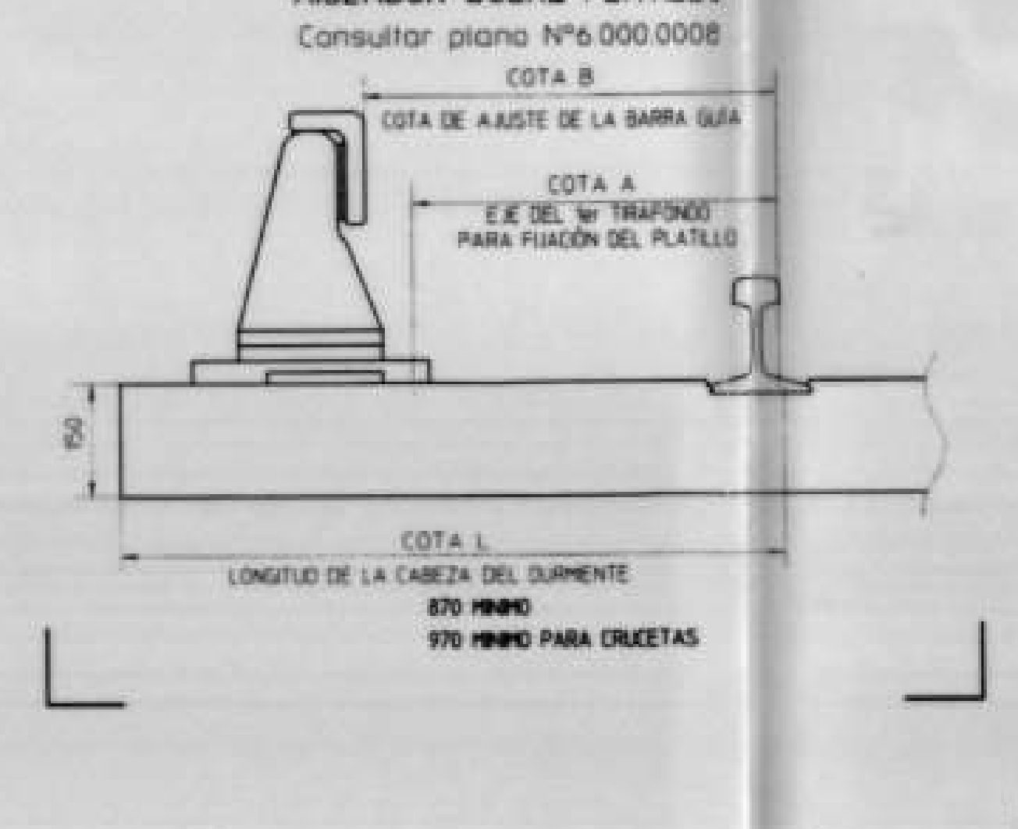
COTA B
COTA DE AJUSTE DE LA BARRA GUÍA
COTA A
E.E. DEL 1er TIRAFONDO PARA FIJACIÓN DEL PLATILLO
COTA L
LONGITUD DE LA CABEZA DEL DURMIENTE
870 MÍNIMO
970 MÍNIMO PARA CRUCETAS

### DETALLE DE LAS CABEZAS DE LOS DURMIENTES
AISLADOR SOBRE ZOCLO
Consultar plano N°6.000.0007

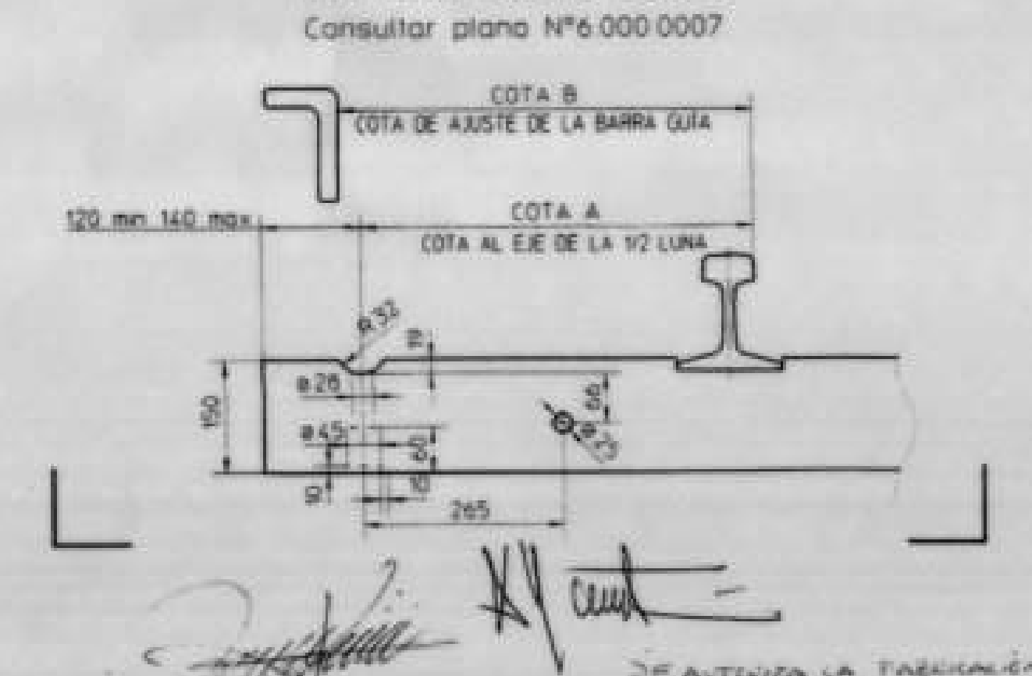

Ing. A. K. Perea M.
S.T.C.
08/Febrero/2007

SE AUTORIZA LA FABRICACIÓN DE LA COMUNICACIÓN DE VÍA COMPLETA CON PIEZAS [illegible], JUEGO DE DURMIENTES Y [illegible] CON LA ENTREVÍA Y RAMIFICACIÓN INDICADAS EN ESTE DOCUMENTO

NOTA : Las piezas indicadas con líneas mixtas no forman parte del suministro.

| AUTORIZO DGCOSTC | APROBO DGCOSTC | REVISO DGCOSTC |
|---|---|---|

IMPLANTACIÓN DE VÍA - FIJACIÓN DE VÍA
**COMUNICACIÓN TG.0,13 A LA DERECHA CON ENTREVIA 2,9**
APARATO 13-23 - BALBUENA-PUERTO AERO - Linea 1

| | |
|---|---|
| Date | 30-01-07 |
| Dess. Drawn | KOCHER |
| Vérif. Checked | |

| Echelle Scale | Type de rail Type of rail | Poids total Total weight | Symbole Symbol |
|---|---|---|---|
| 150 | AREA 100RE<br>PISTE 68kg | | |

Vossloh Switch Systems
**Vossloh Cogifer**

6 217 4342

CE PLAN EST NOTRE PROPRIETE EXCLUSIVE
THIS DRAWING IS CONFIDENTIAL AND THE COPYRIGHT OF Vossloh Cogifer