DIAGRAMA DE LAS LÍNEAS DIRECTRICES

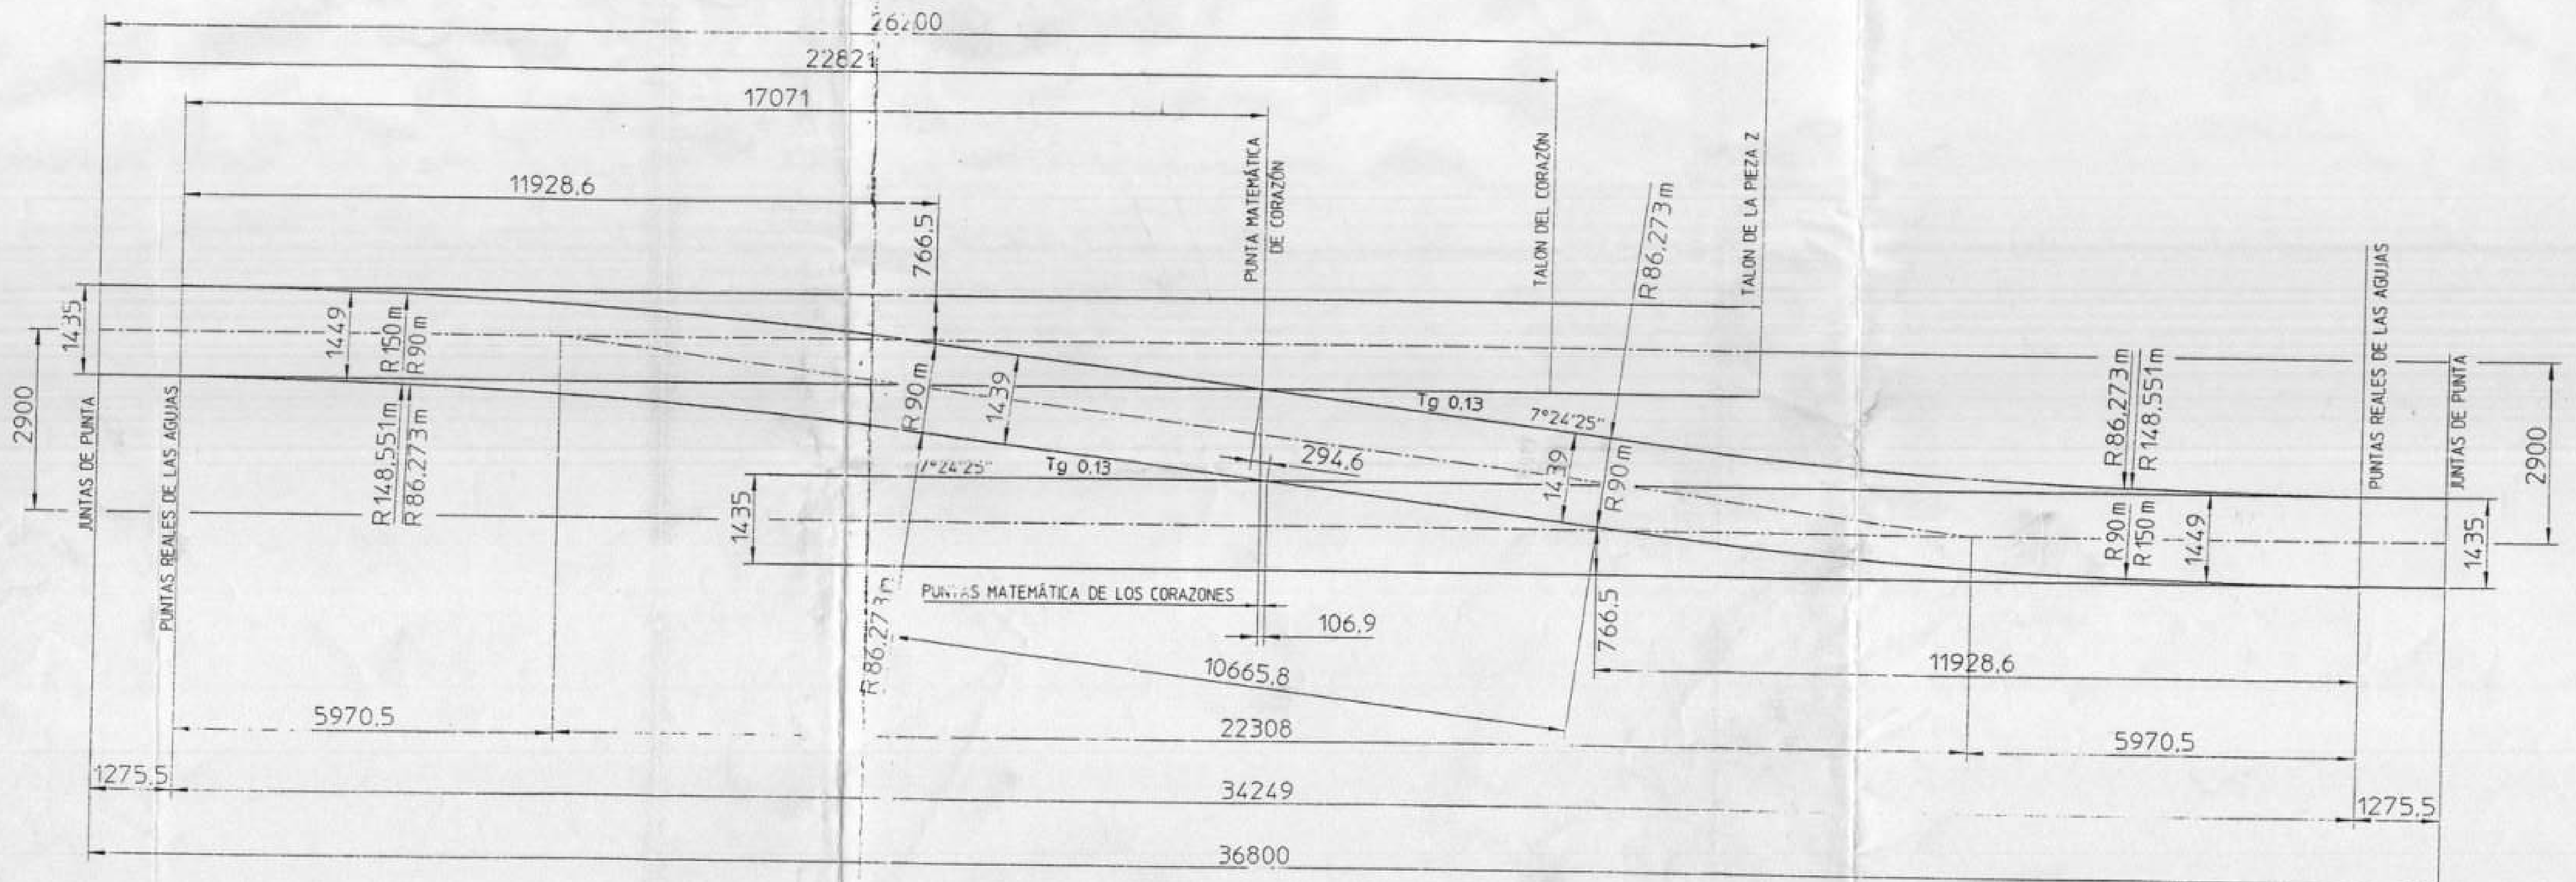

DIAGRAMA DE LAS AGUJAS

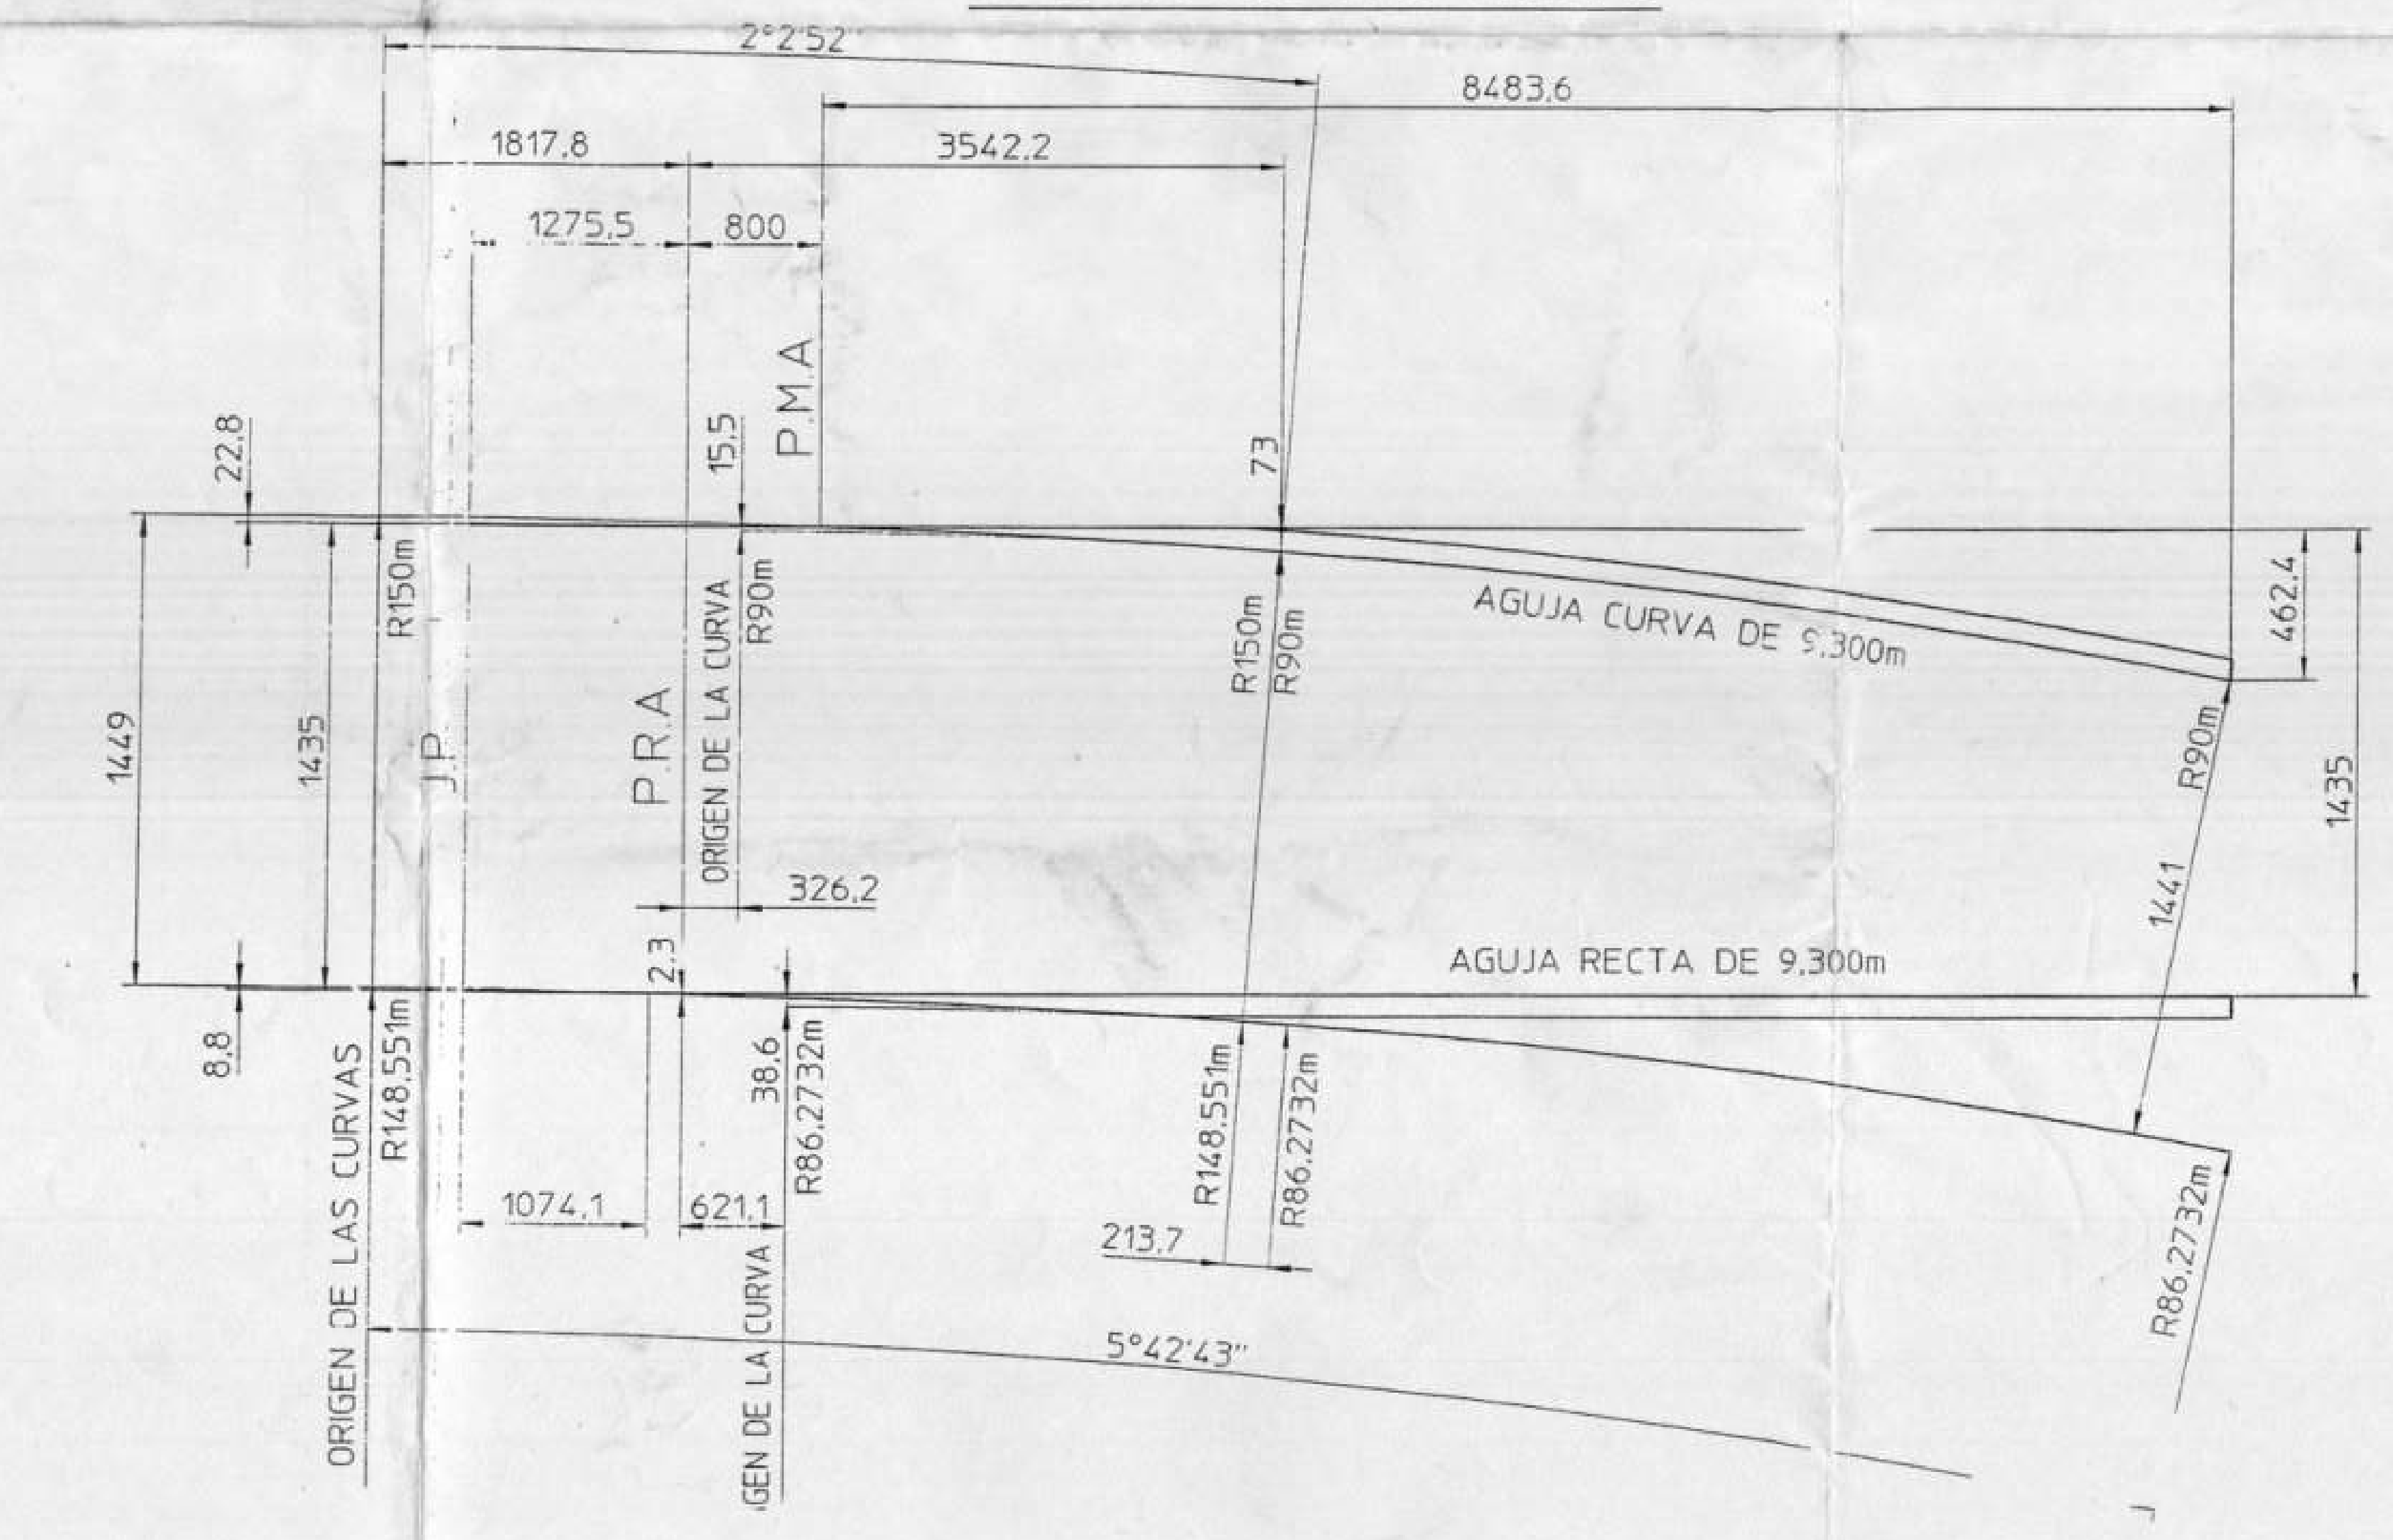

DETALLE DE LAS CABEZAS DE LOS DURMIENTES
AISLADOR SOBRE PLATILLO
Consultar plano N°6.000.0008 Mod.0

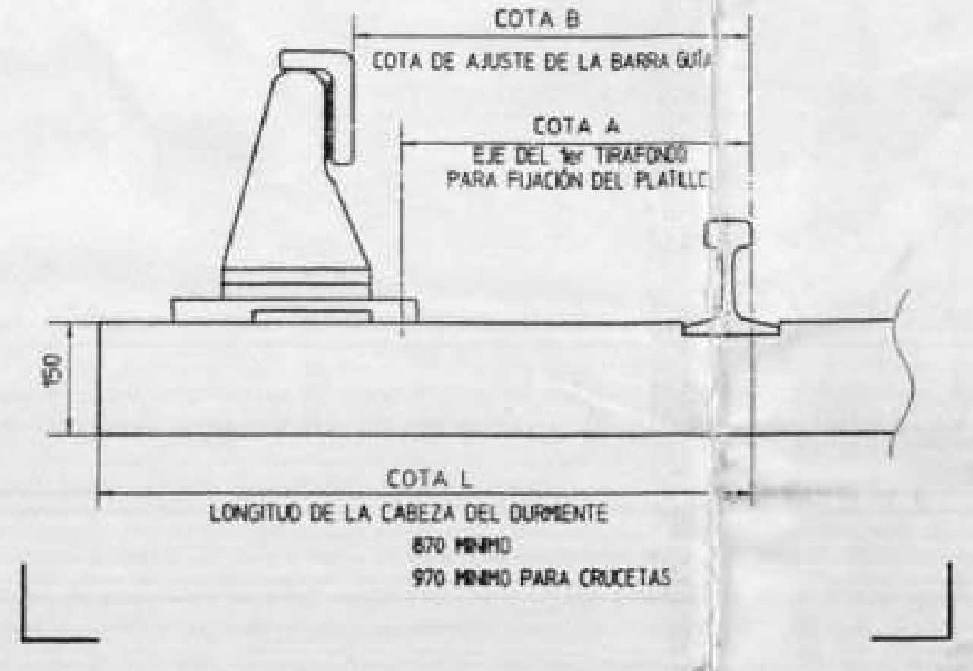
COTA B
COTA DE AJUSTE DE LA BARRA GUÍA
COTA A
EJE DEL 1er TIRAFONDO PARA FIJACIÓN DEL PLATILLO
150
COTA L
LONGITUD DE LA CABEZA DEL DURMIENTE
870 MINIMO
970 MINIMO PARA CRUCETAS

DETALLE DE LAS CABEZAS DE LOS DURMIENTES
AISLADOR SOBRE ZOCLO
Consultar plano N° 6.000.0007 Mod.2

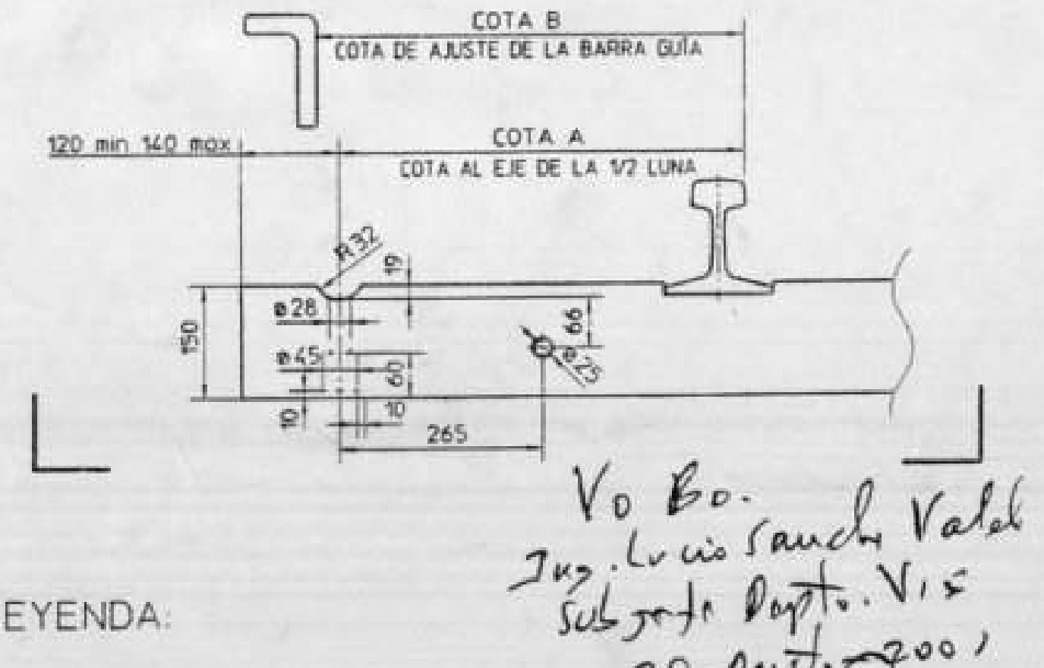

Vo Bo.
Ing. Lucio Sanchez Valdez
Subjefe Depto. Vis
28-Abril-2001

LEYENDA:

- ▬ Aislador sobre platillo
- — Aislador sobre zoclo (1/2 luna)

NOTA : Las piezas indicadas con líneas mixtas no forman parte del suministro.

0	27.06.01 BC0371	
Revisó	MODIFICACION	Aprobó COGIFER
COGIFER COGIFER DEPARTEMENT INDUSTRIE 40, quai de l'Ecluse 78290 Croissy-sur-Seine France	IMPLANTACIÓN DE VÍA - FIJACIÓN DE VÍA COMUNICACIÓN TG0,13 A LA DER. CON ENTREVÍA 2,90 APARATO 11-21 - CHAPULTEPEC -	SISTEMA DE TRANSPORTE COLECTIVO Delicias No. 67 C.P. 06070 México D.F.

Escala: 1:50	No. de Plano Cogifer:	No. de Plano S.T.C.:	Fecha de aprobación S.T
Revisó S.T.C.: Ing. Lucio Sanchez V.	6 217 4038	Contrato No. 001/2000	Dibujó DAAB
Aprobó S.T.C.: Ing. Erasmo Cuatecontzi C.	Vo. Bo. S.T.C.: Ing. Alfredo Navarrete Y.	Autorizó S.T.C.:	Revisó
			Fecha 27-06-0

L K J I H G F E D C B A