DETALLE DE LAS CABEZAS DE LOS DURMIENTES
AISLADOR SOBRE ZOCLO
Consultar plano N°6.000.0007 Mod.2

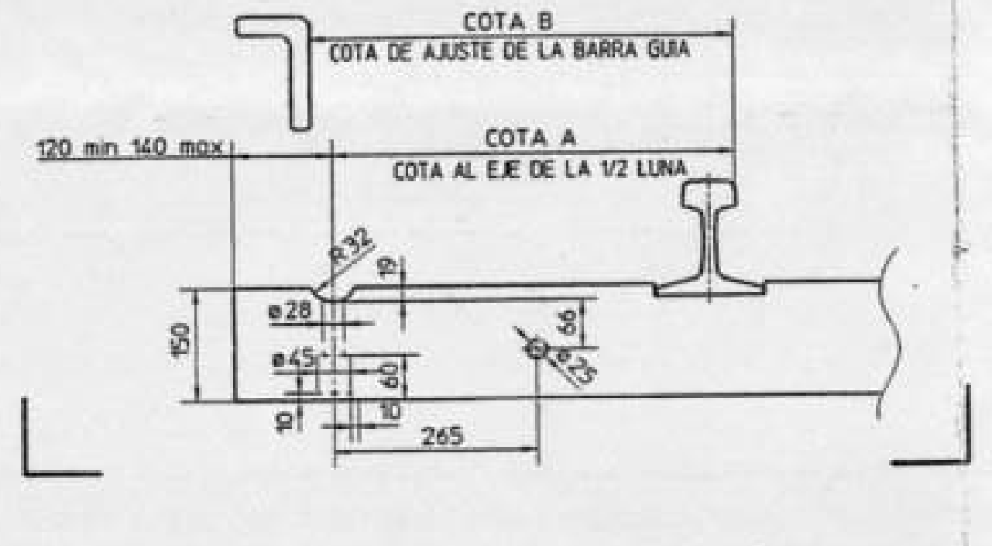

DIAGRAMA DE LAS LÍNEAS DIRECTRICES

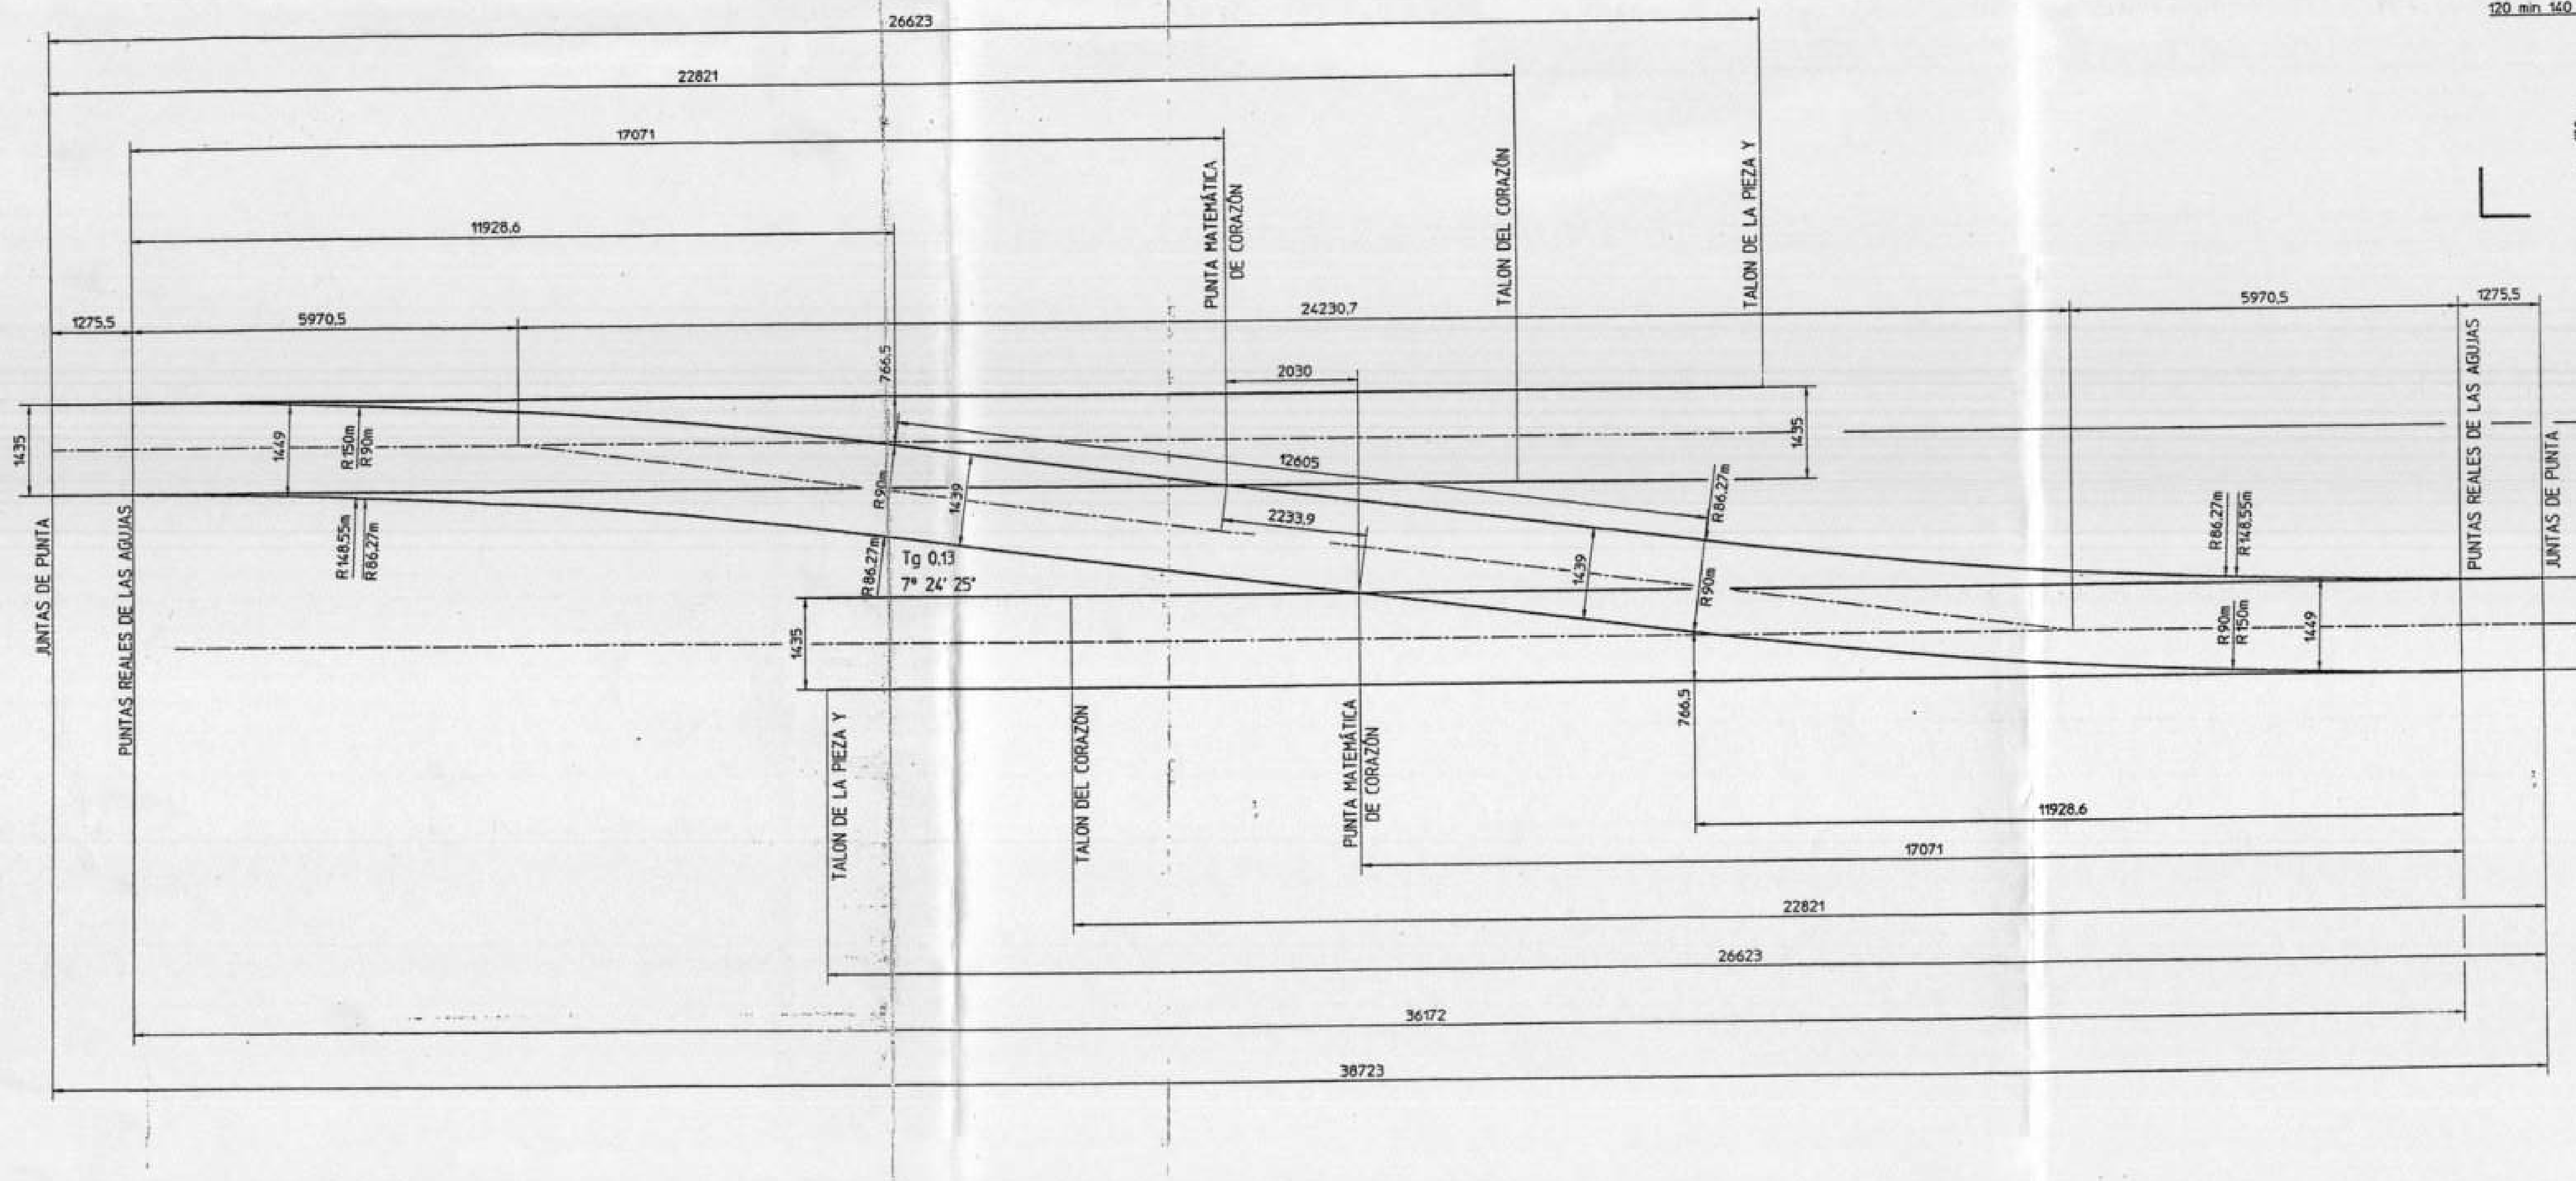

DIAGRAMA DE LAS AGUJAS

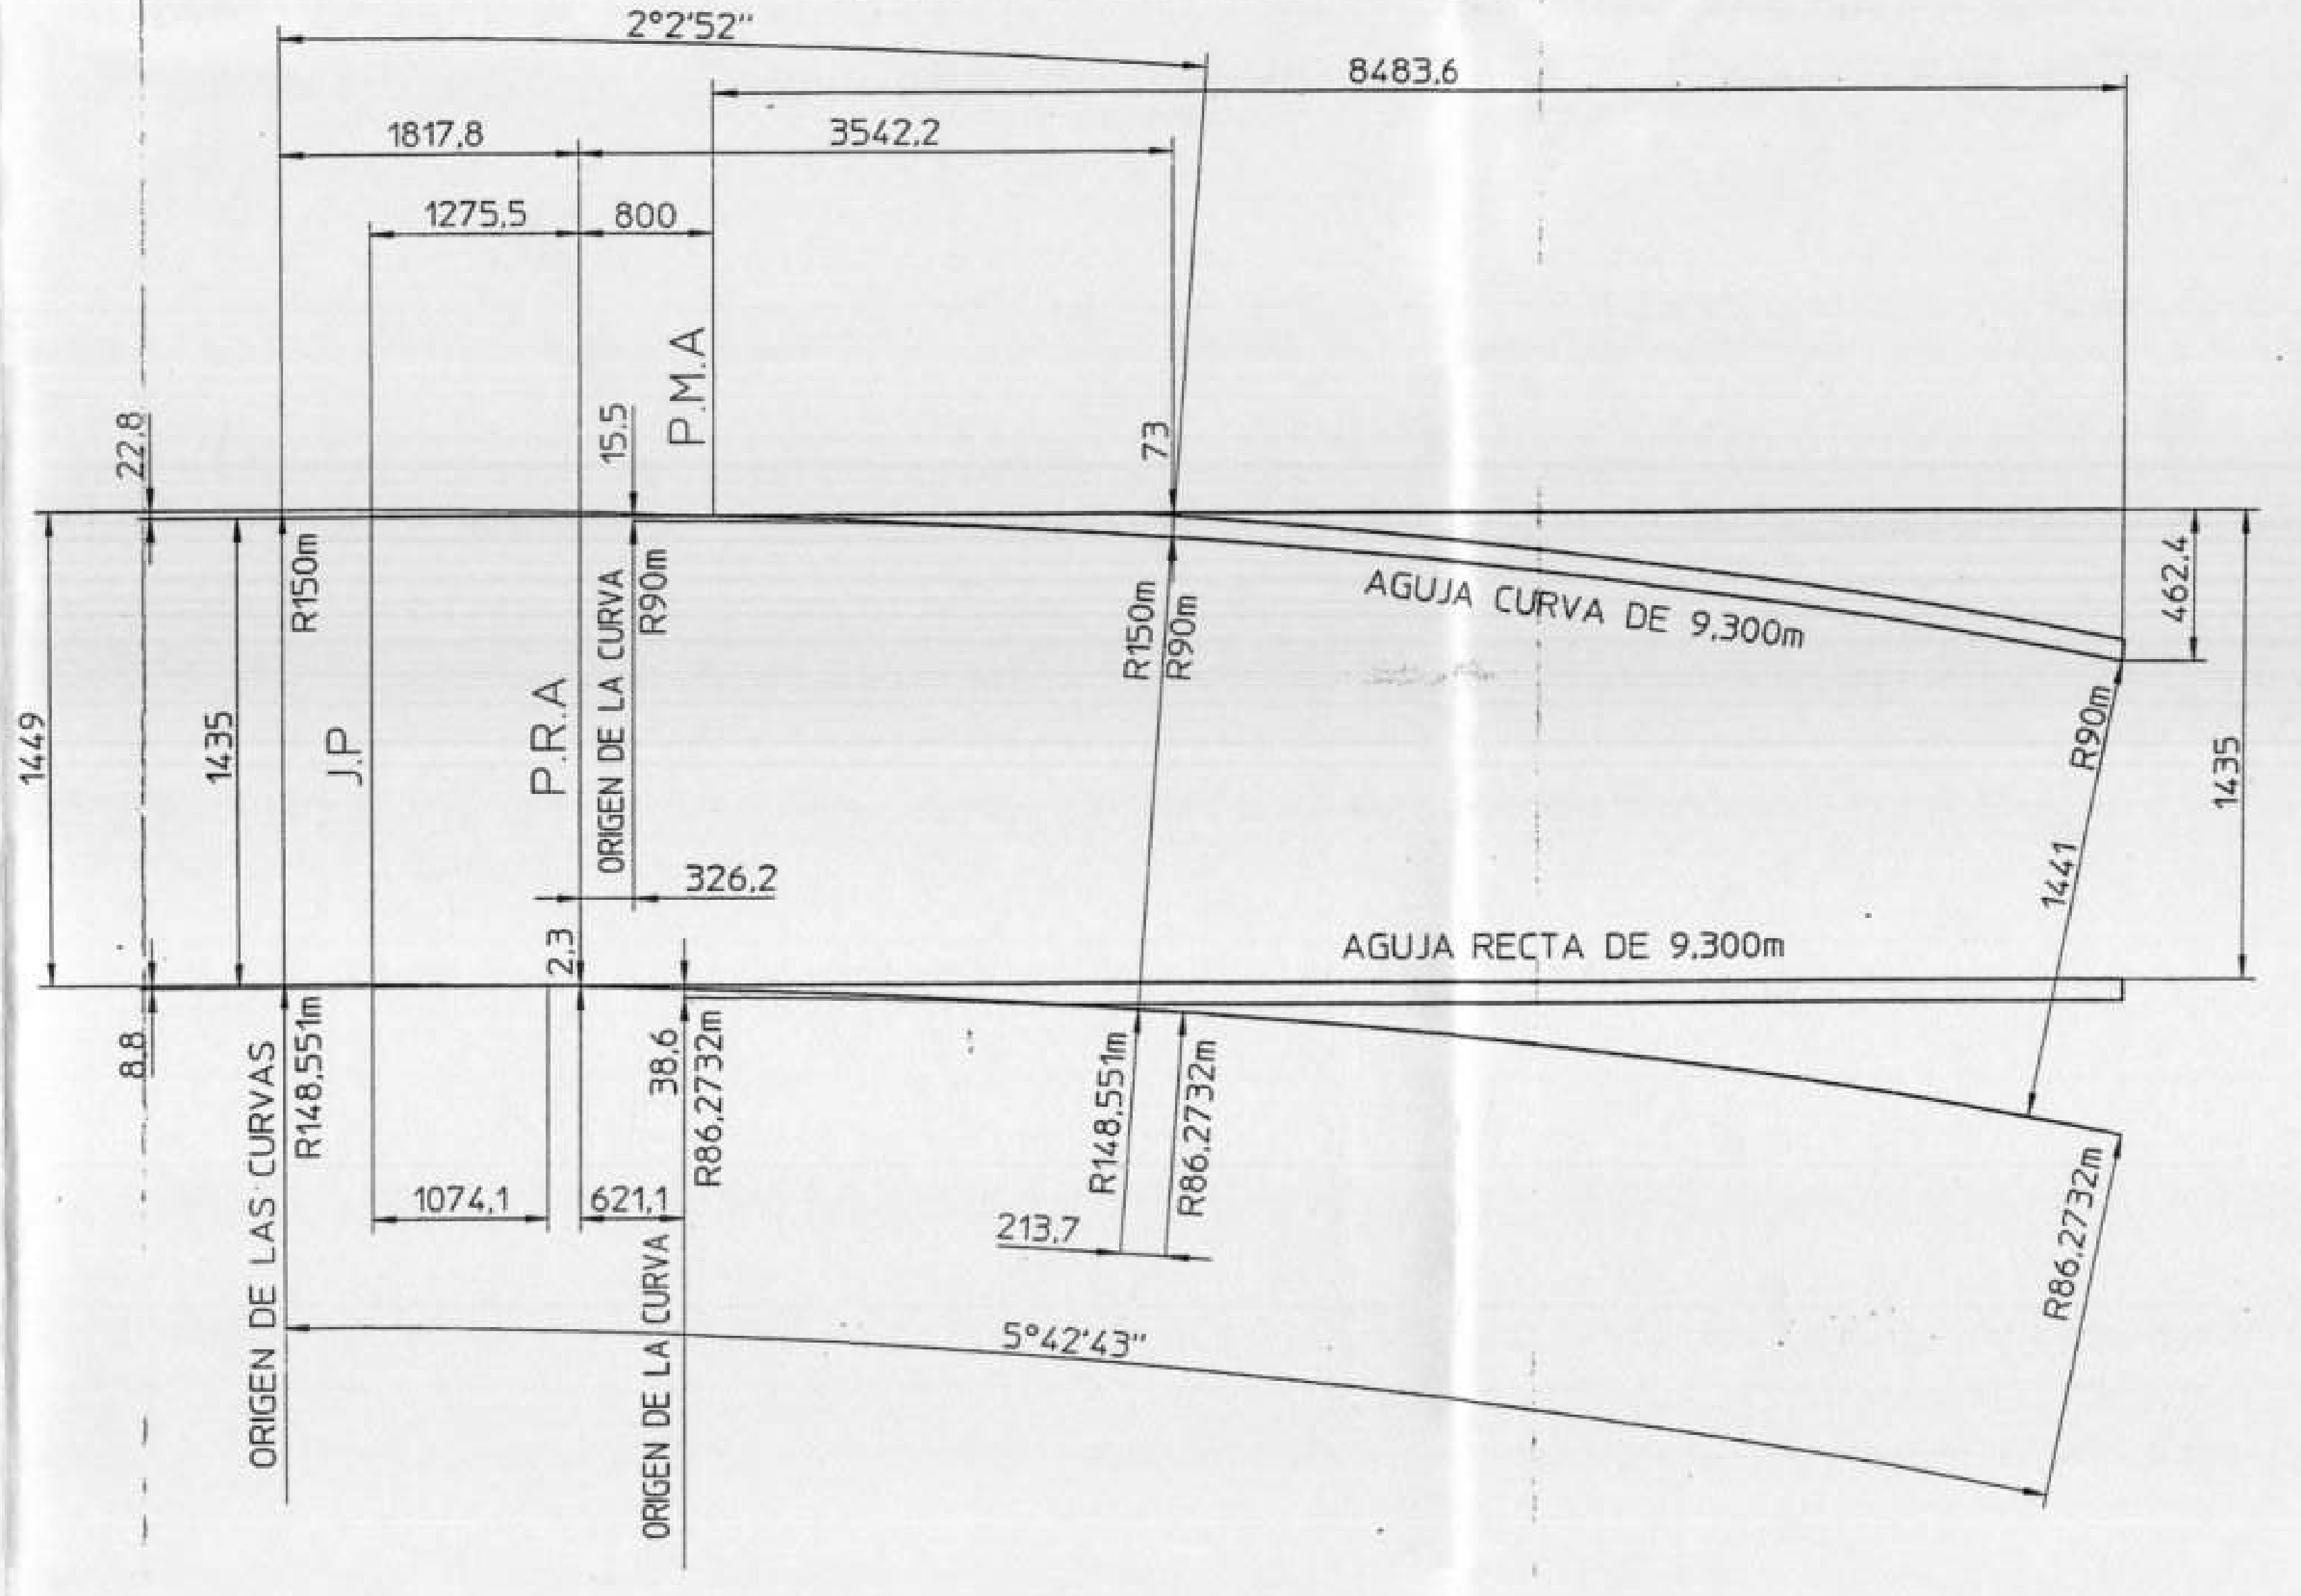

DETALLE DE LAS CABEZAS DE LOS DURMIENTES
AISLADOR SOBRE PLATILLO
Consultar plano N°6.000.0008 Mod.0

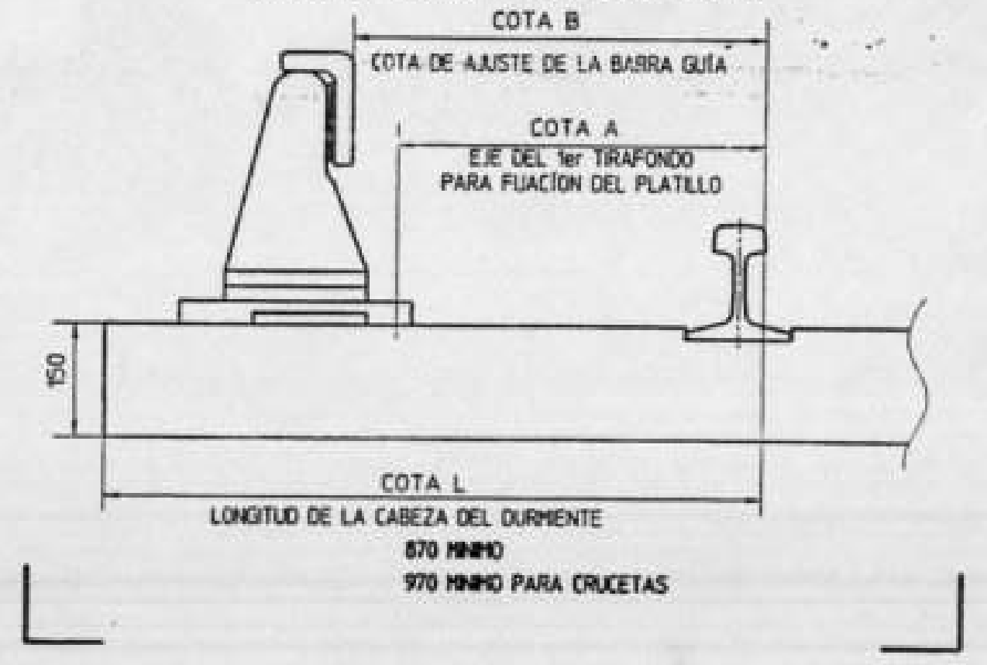
COTA B
COTA DE AJUSTE DE LA BARRA GUÍA
COTA A
EJE DEL 1er TIRAFONDO
PARA FIJACIÓN DEL PLATILLO
150
COTA L
LONGITUD DE LA CABEZA DEL DURMIENTE
870 MINIMO
970 MINIMO PARA CRUCETAS

NOTA : Las piezas indicadas con líneas mixtas no forman parte del suministro.

0	8.01.01 BC0371	
Revisó	MODIFICACION	Aprobó COGIFER

COGIFER
DEPARTEMENT INDUSTRIE
40, quai de l'Ecluse
78290 Croissy-sur-Seine
France

IMPLANTACIÓN DE VÍA - FIJACIÓN DE VÍA
COMUNICACIÓN TG0,13 A LA DER. CON ENTREVÍA 3,15
APARATO 75-ZA2 - BALDERAS - SALTO DEL AGUA

SISTEMA DE TRANSPORTE COLECTIVO
Delicias No. 67 C.P. 06070
México,D.F.

Escala: 1:50	No. de Plano Cogifer:	No. de Plano S.T.C.:	Fecha de aprobación S.T.C.:
Revisó S.T.C.: ING. SERGIO ARENAS MEJIA	6 217 4027	Contrato No. 001/2000	Dibujó: DAAB