

ZB2

ZB1

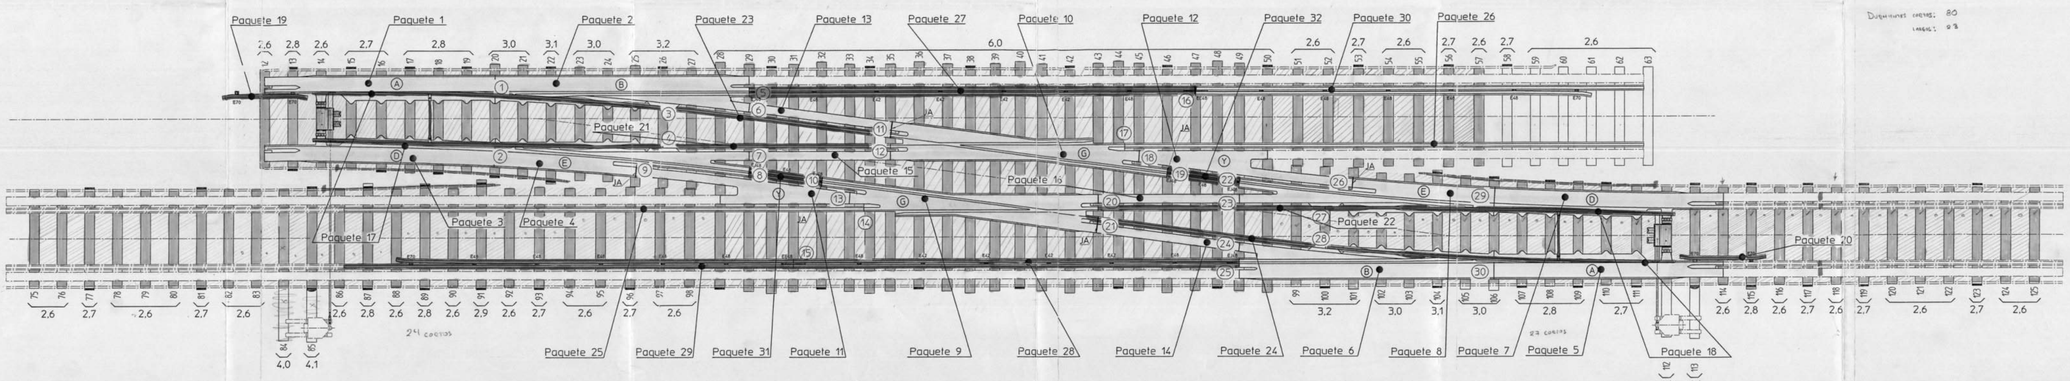

EMPAQUE DE LOS DURMIENTES

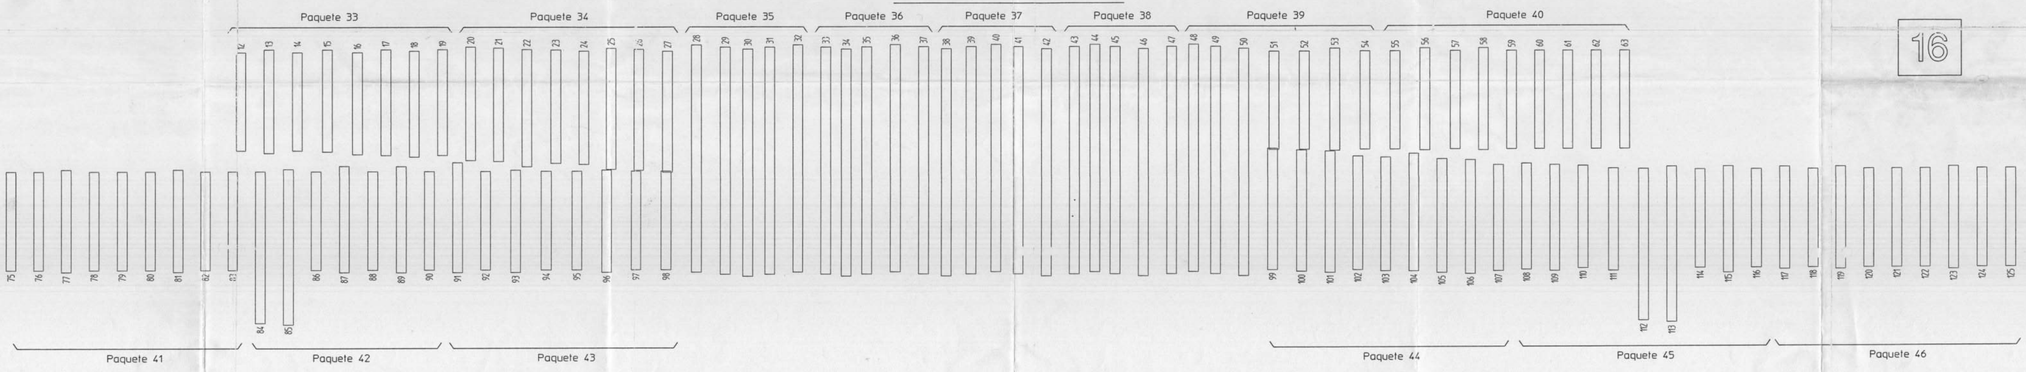

16

PLANO DE EMPAQUE

0	18.0101 BC0371		Aprobó COGIFER
Revisó	MODIFICACION		
COGIFER	IMPLANTACIÓN DE VÍA - FIJACIÓN DE VÍA COMUNICACIÓN TG.01.03 A LA DER. CON ENTREVÍA 3.15 APARATO ZB2-16 - BALDERAS - SALTO DEL AGUA		SISTEMA DE TRANSPORTE COLECTIVO Decreto No. 67 C.P. 06070
Escala: 1:50	No. de Plano Cogifer: 6 217 4030 Folio 2	No. de Plano S.T.C.:	Fecha de aprobación S.T.C.:
Revisó S.T.C.:		Contrato No. 001/2000	Dibujó: GENTY
Aprobó S.T.C.:	Vo. Bo S.T.C.:	Autorizó S.T.C.:	Revisó: Fecha: 24-04-01