14
Controladores de posición de puntas de aguja tipo " Paulve ".

DIAGRAMA DE LAS LÍNEAS DIRECTRICES

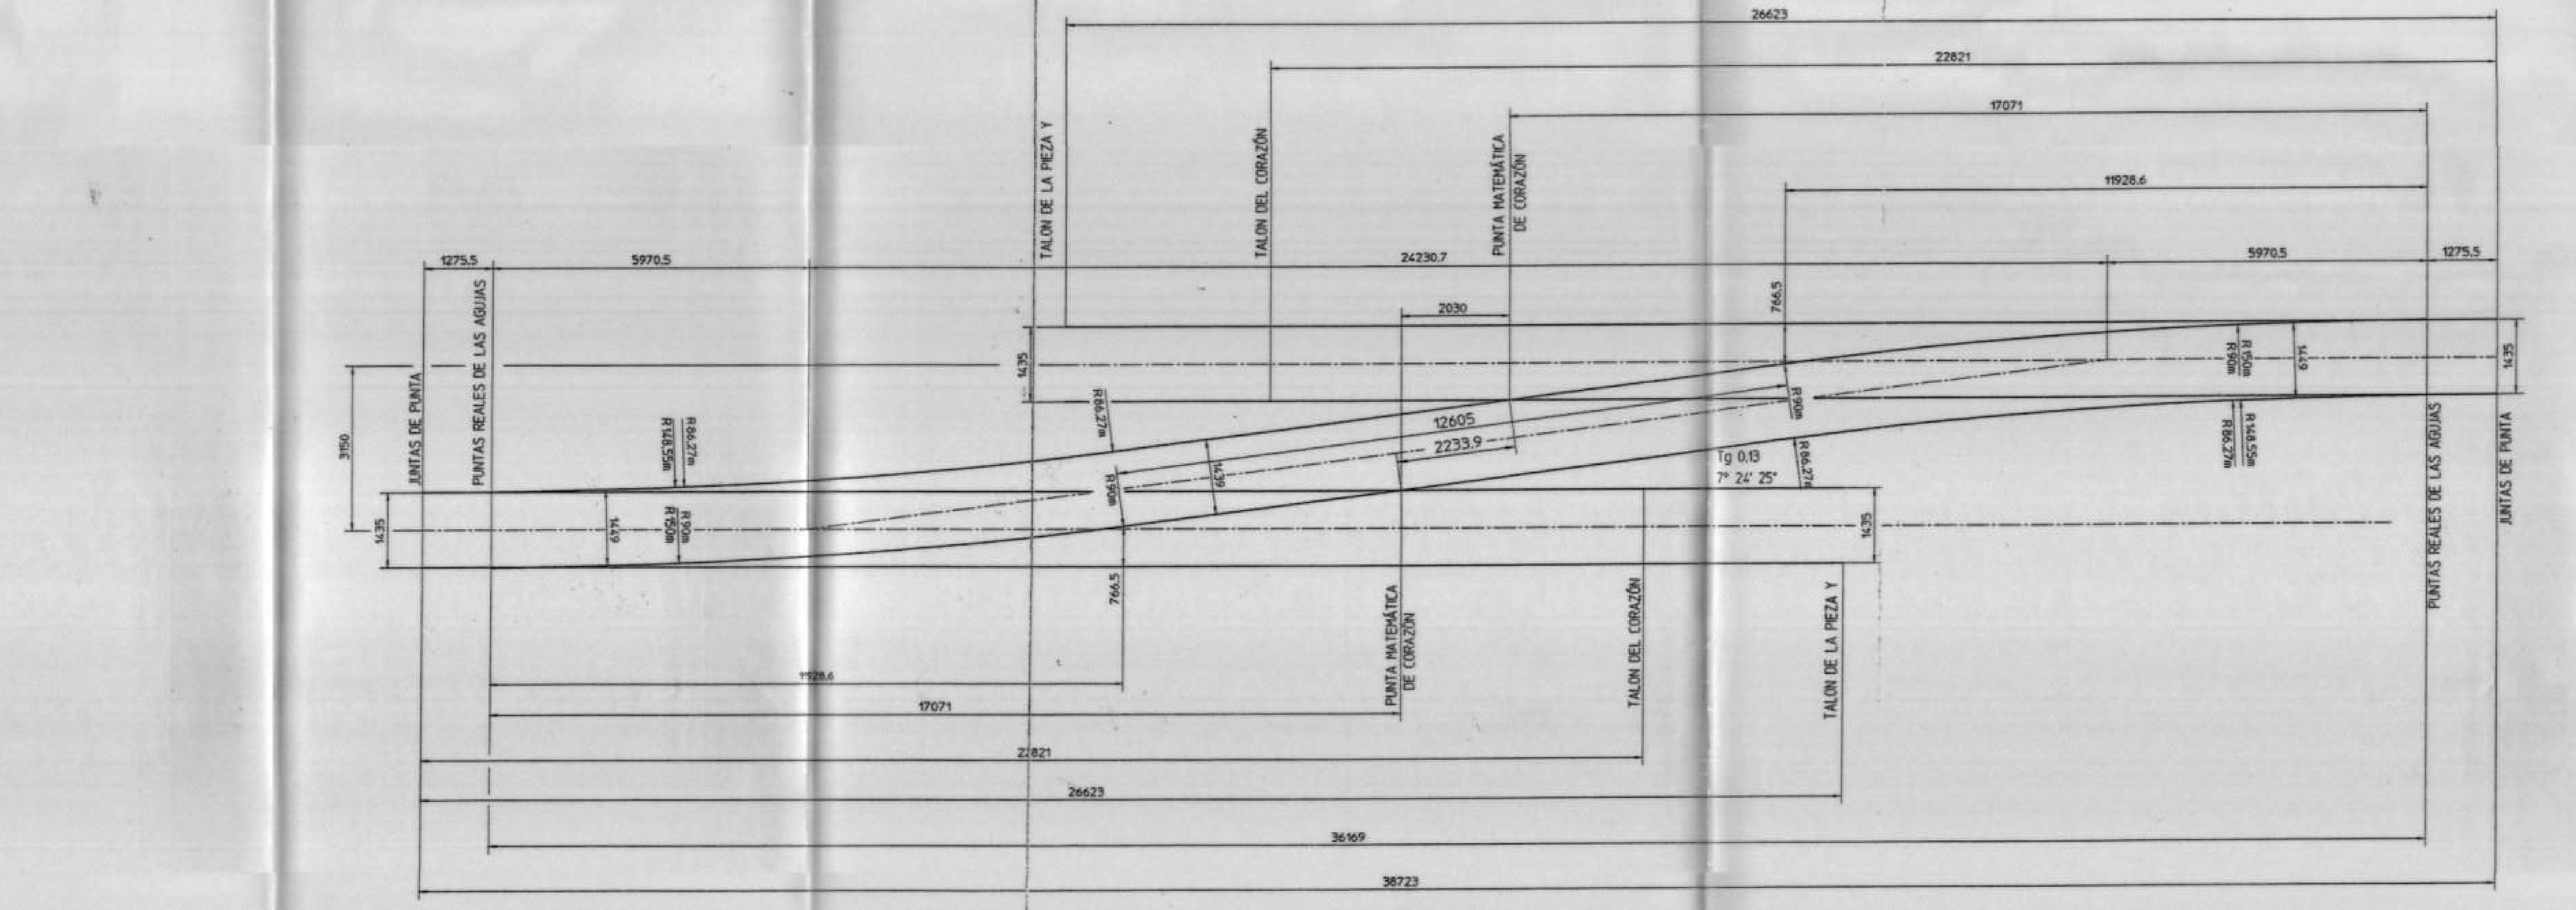

DIAGRAMA DE LAS AGUJAS

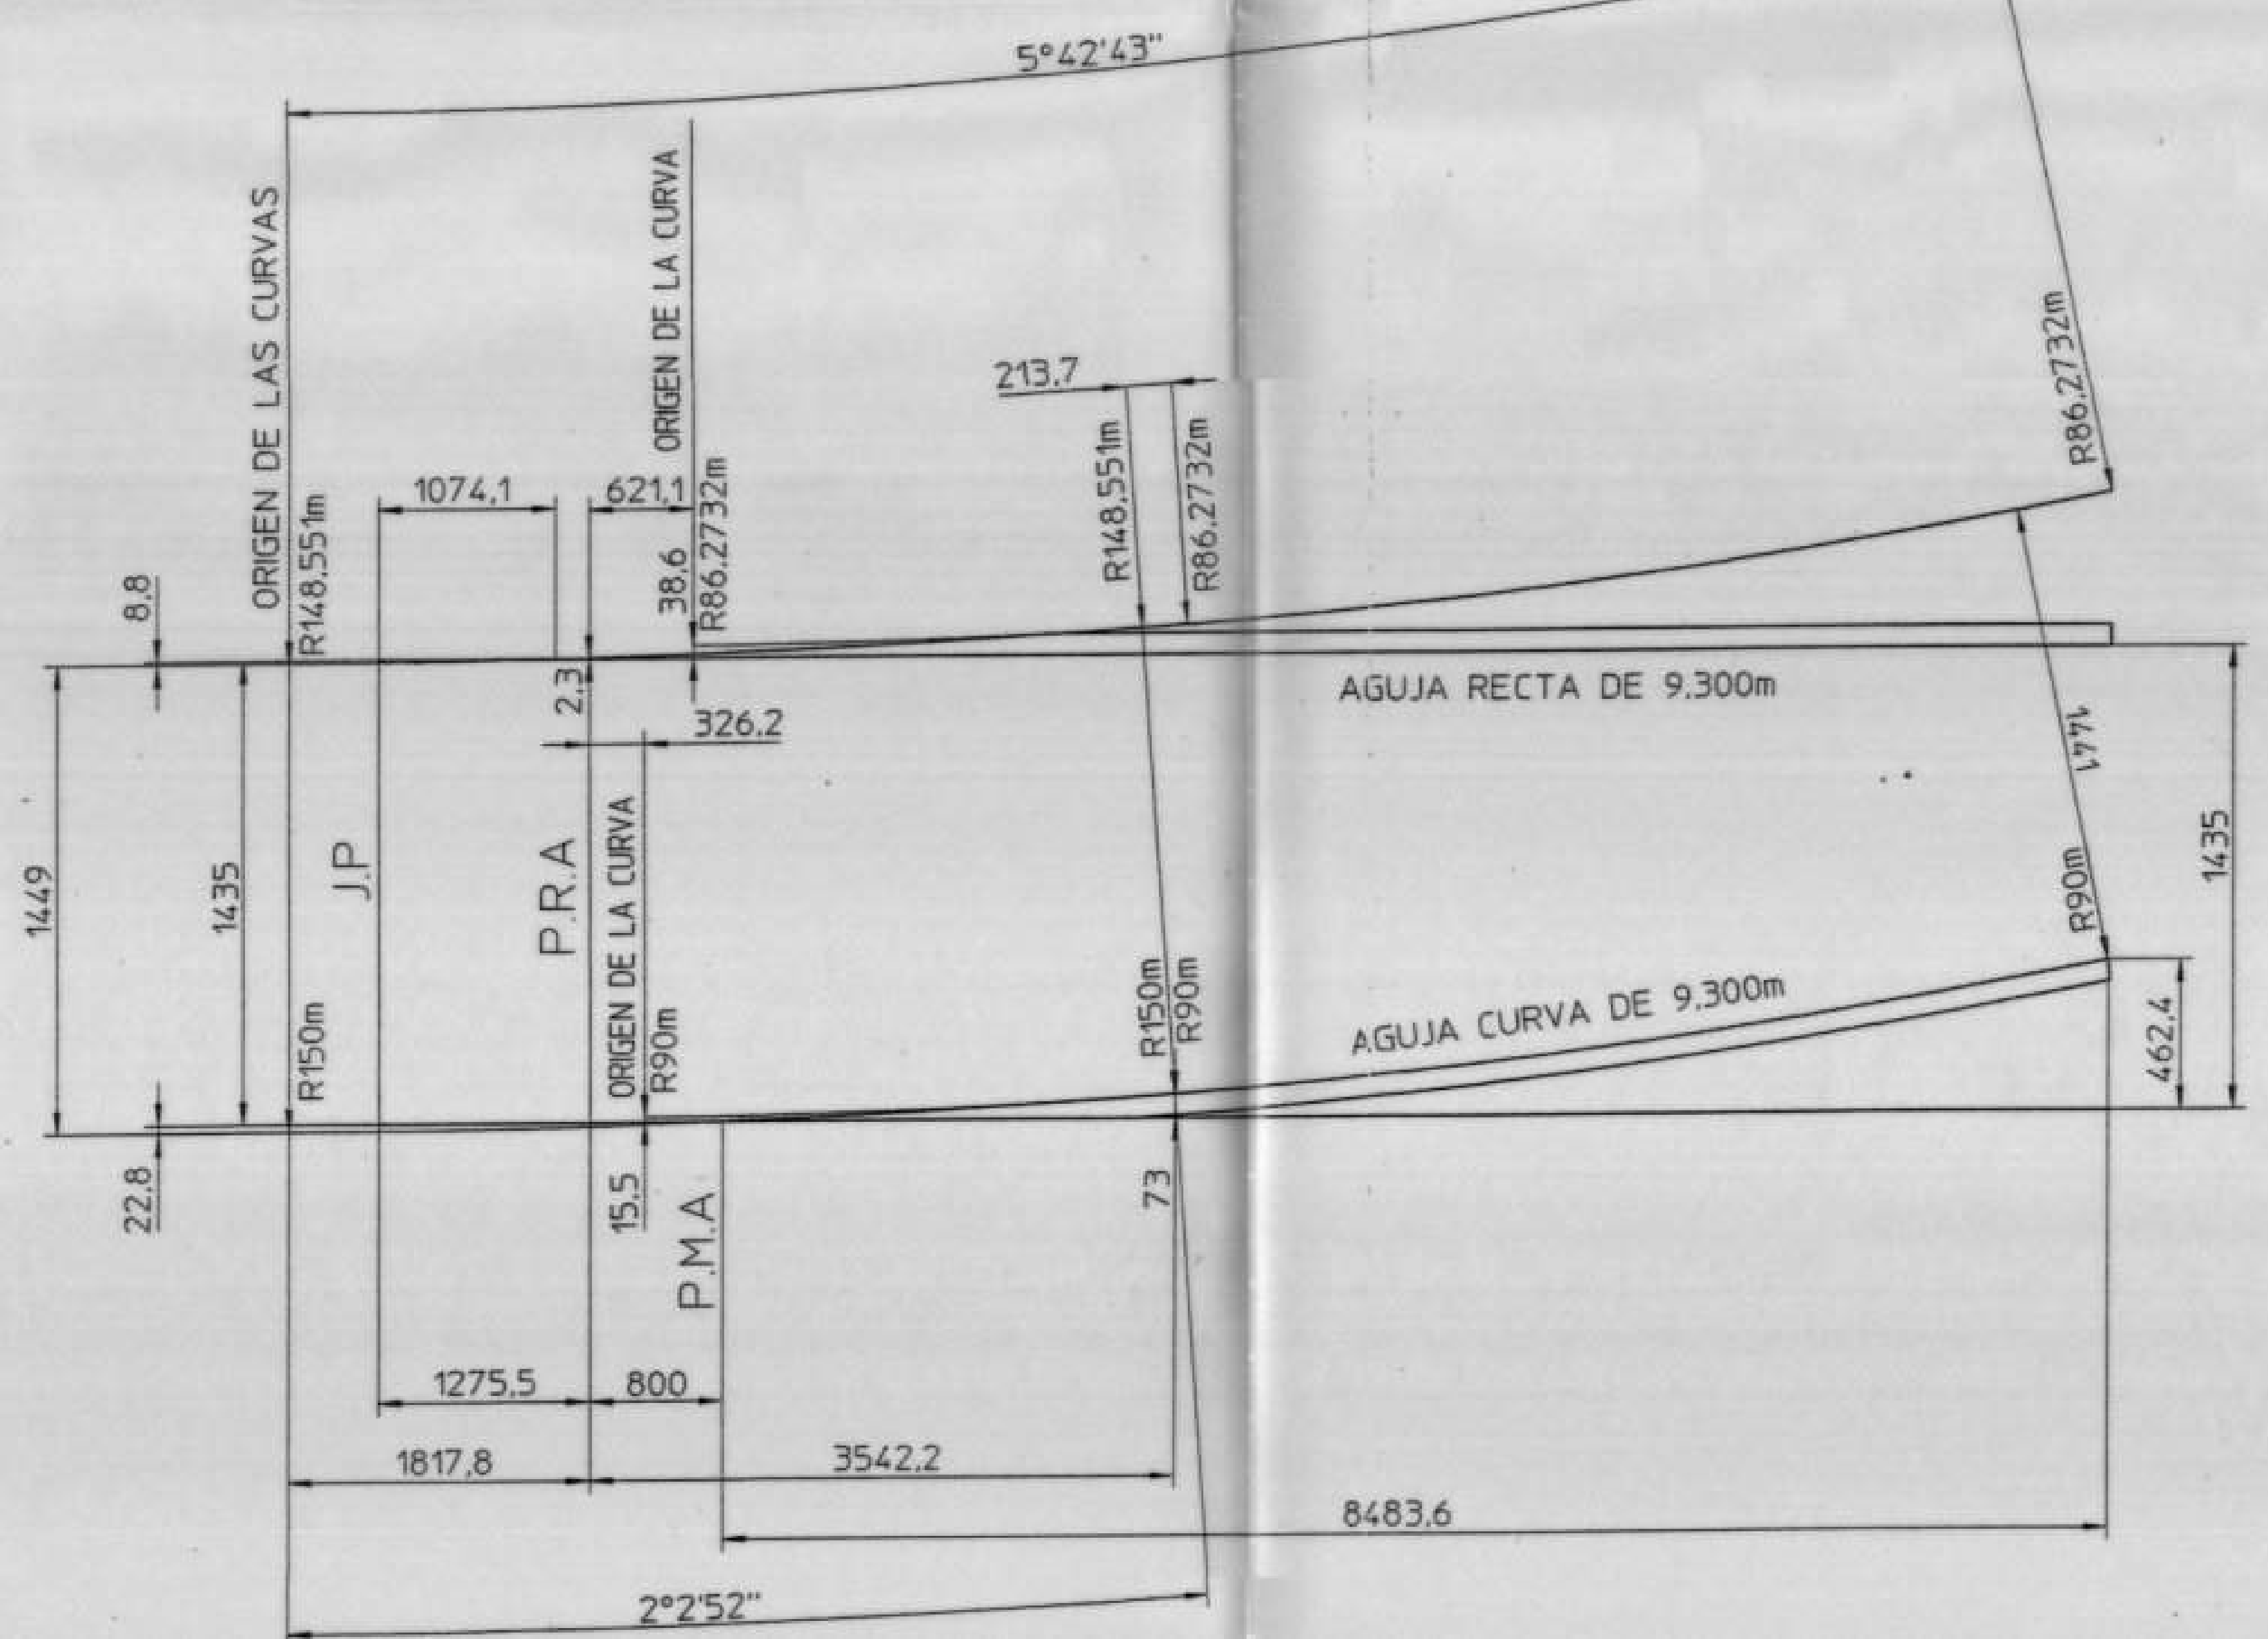

DETALLE DE LAS CABEZAS DE LOS DURMIENTES
AISLADOR SOBRE PLATILLO
Consultar plano N°6.000.0008 Mod.0

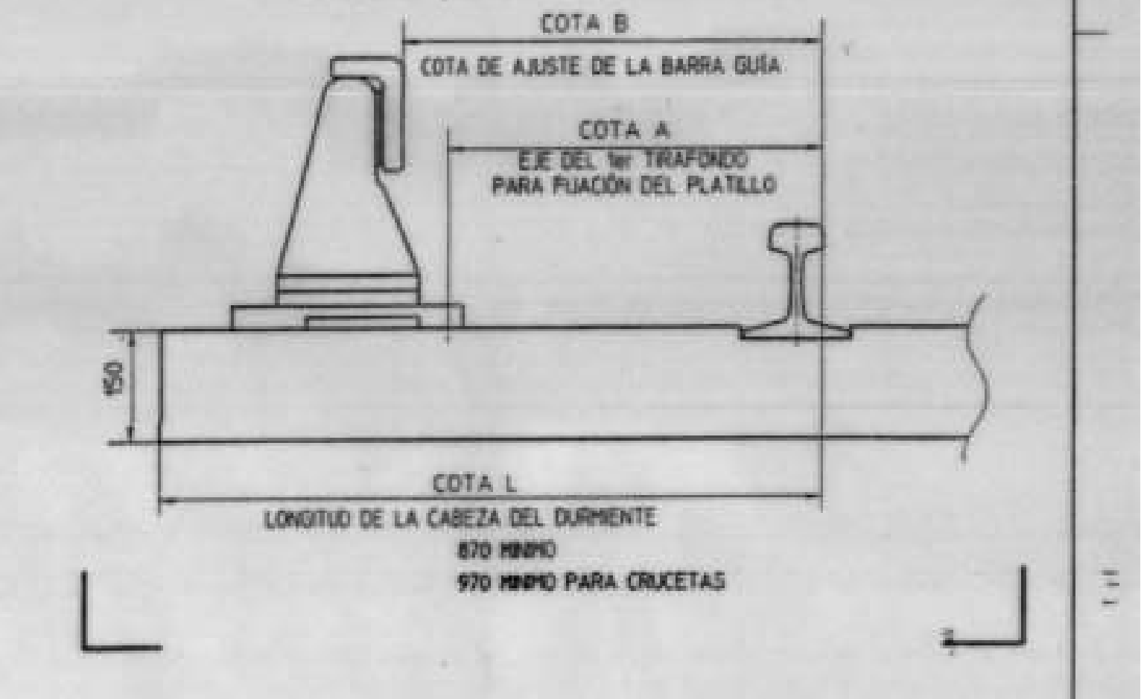
COTA B
COTA DE AJUSTE DE LA BARRA GUÍA
COTA A
EJE DEL 1er TIRAFONDO PARA FIJACIÓN DEL PLATILLO
150
COTA L
LONGITUD DE LA CABEZA DEL DURMIENTE
870 MINIMO
970 MINIMO PARA CRUCETAS

DETALLE DE LAS CABEZAS DE LOS DURMIENTES
AISLADOR SOBRE ZOCLO
Consultar plano N°6.000.0007 Mod.2

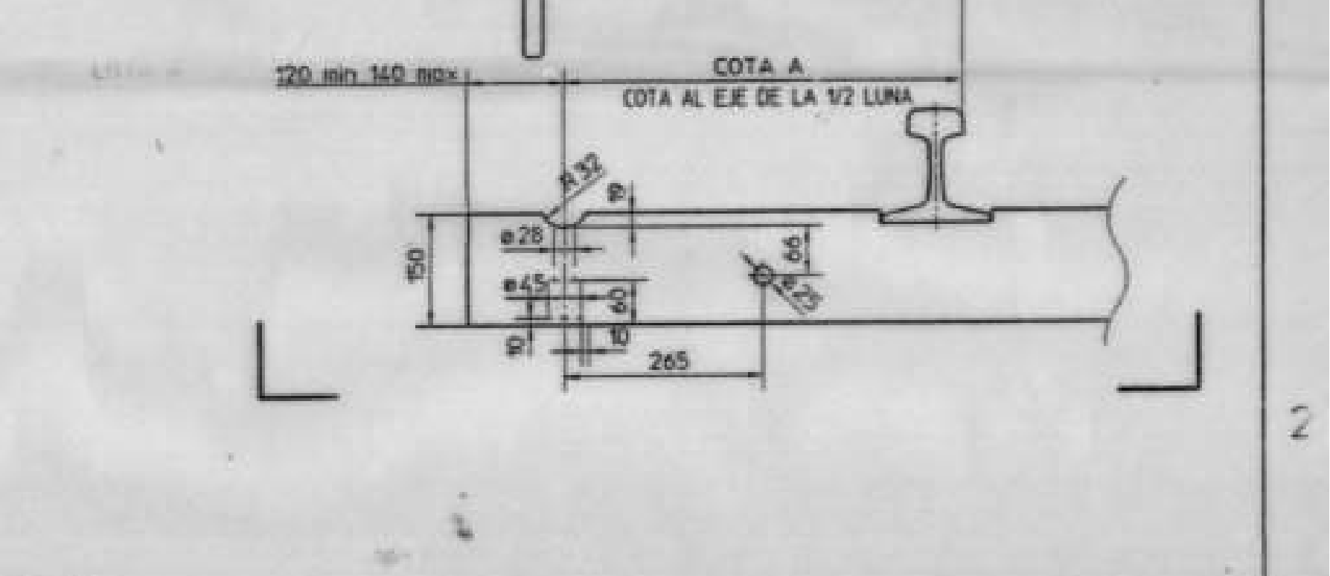

LEYENDA:
- Aislador sobre platillo
- Aislador sobre zoclo (1/2 luna)

NOTA : Las piezas indicadas con lineas mixtas no forman parte del suministro.

0	29.01.01 BC0371		
Revisó	MODIFICACION		Aprobó COGIFER
COGIFER COGIFER DEPARTEMENT INDUSTRIE 40, quai de l'Ecluse 78290 Croissy-sur-Seine France	IMPLANTACIÓN DE VÍA - FIJACIÓN DE VÍA COMUNICACIÓN TG0,13 A LA IZQ. CON ENTREVÍA 3,15 APARATO ZA1-14 - BALDERAS - SALTO DEL AGUA		SISTEMA DE TRANSPORTE COLECTIVO Delicias No. 67 C.P. 06070 México,D.F.
Escala: 1:50	No. de Plano Cogifer: 6 117 3705	No. de Plano S.T.C.:	Fecha de aprobación S.T.C.:
Revisó S.T.C.:		Contrato No. 001/2000	Dibujó: DAAB
Aprobó S.T.C.:	Vo. Bo. S.T.C.:	Autorizó S.T.C.:	Revisó:
			Fecha: 29-01-01